
FIND YOURSELF v22 / A館 B1 / 詳細配置・検証図

ゲーム用寸法 / 床レベル Y=-5.350m / 建築申請図・構造安全証明ではありません

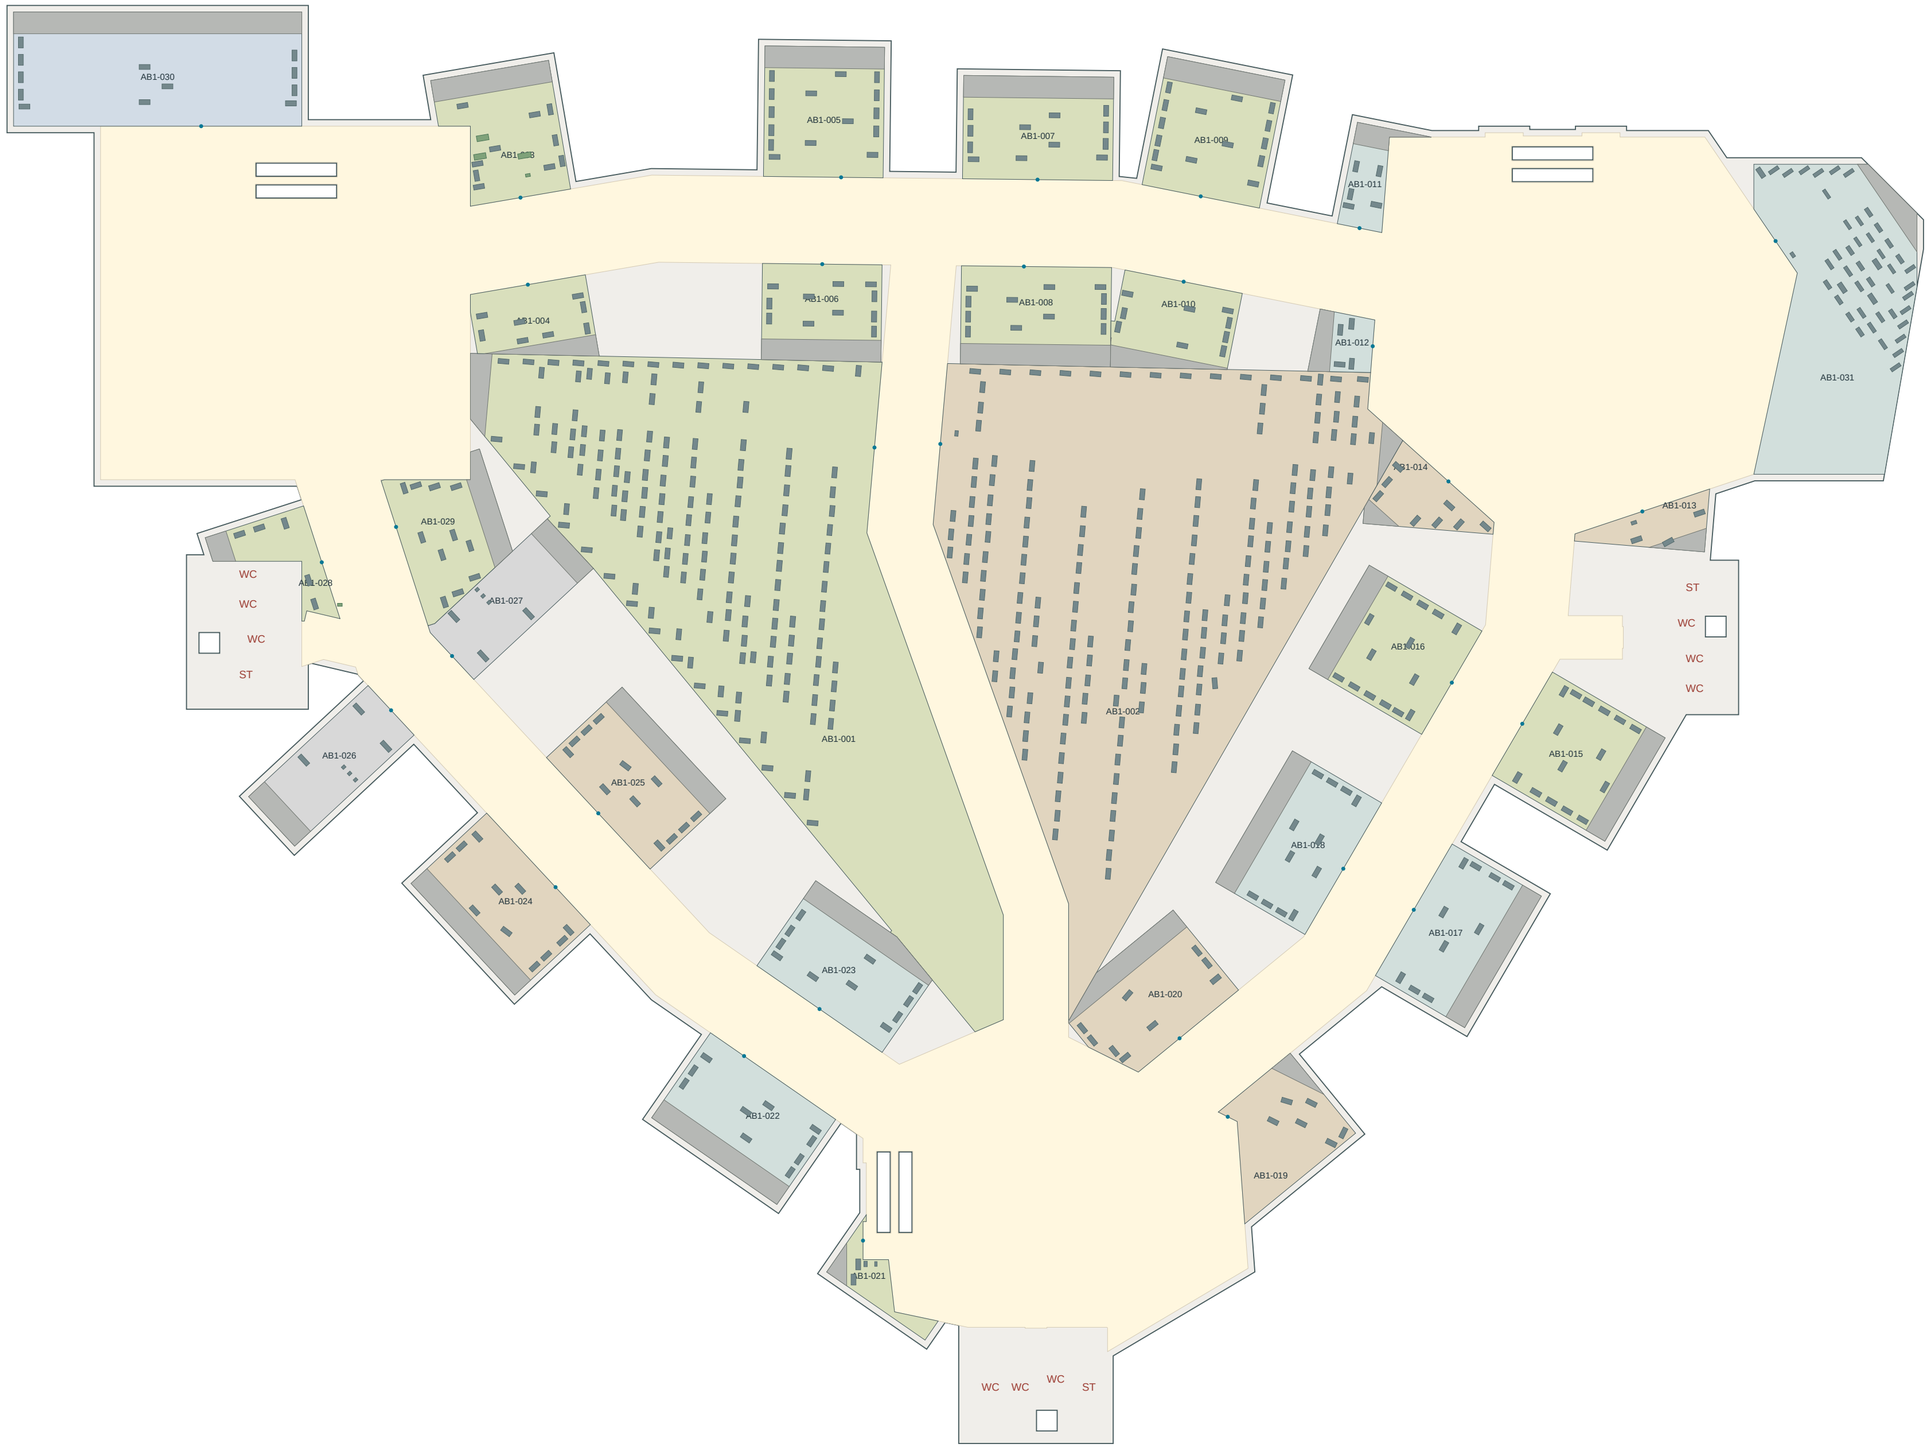


X方向 352.40 m

青丸：実効入口 / 灰：バックヤード / 青灰：什器外接輪郭 / 緑：共用設備 / 橙線：約7.53m連続ES乗継候補

図面の整合性・カプセル検査・自動歩行・人間による実操作は別評価。支持力・基礎・防水・排水・避難容量は未検証。

FIND YOURSELF v22 / A館 1F / 詳細配置・検証図

ゲーム用寸法 / 床レベル Y=0.000m / 建築申請図・構造安全証明ではありません

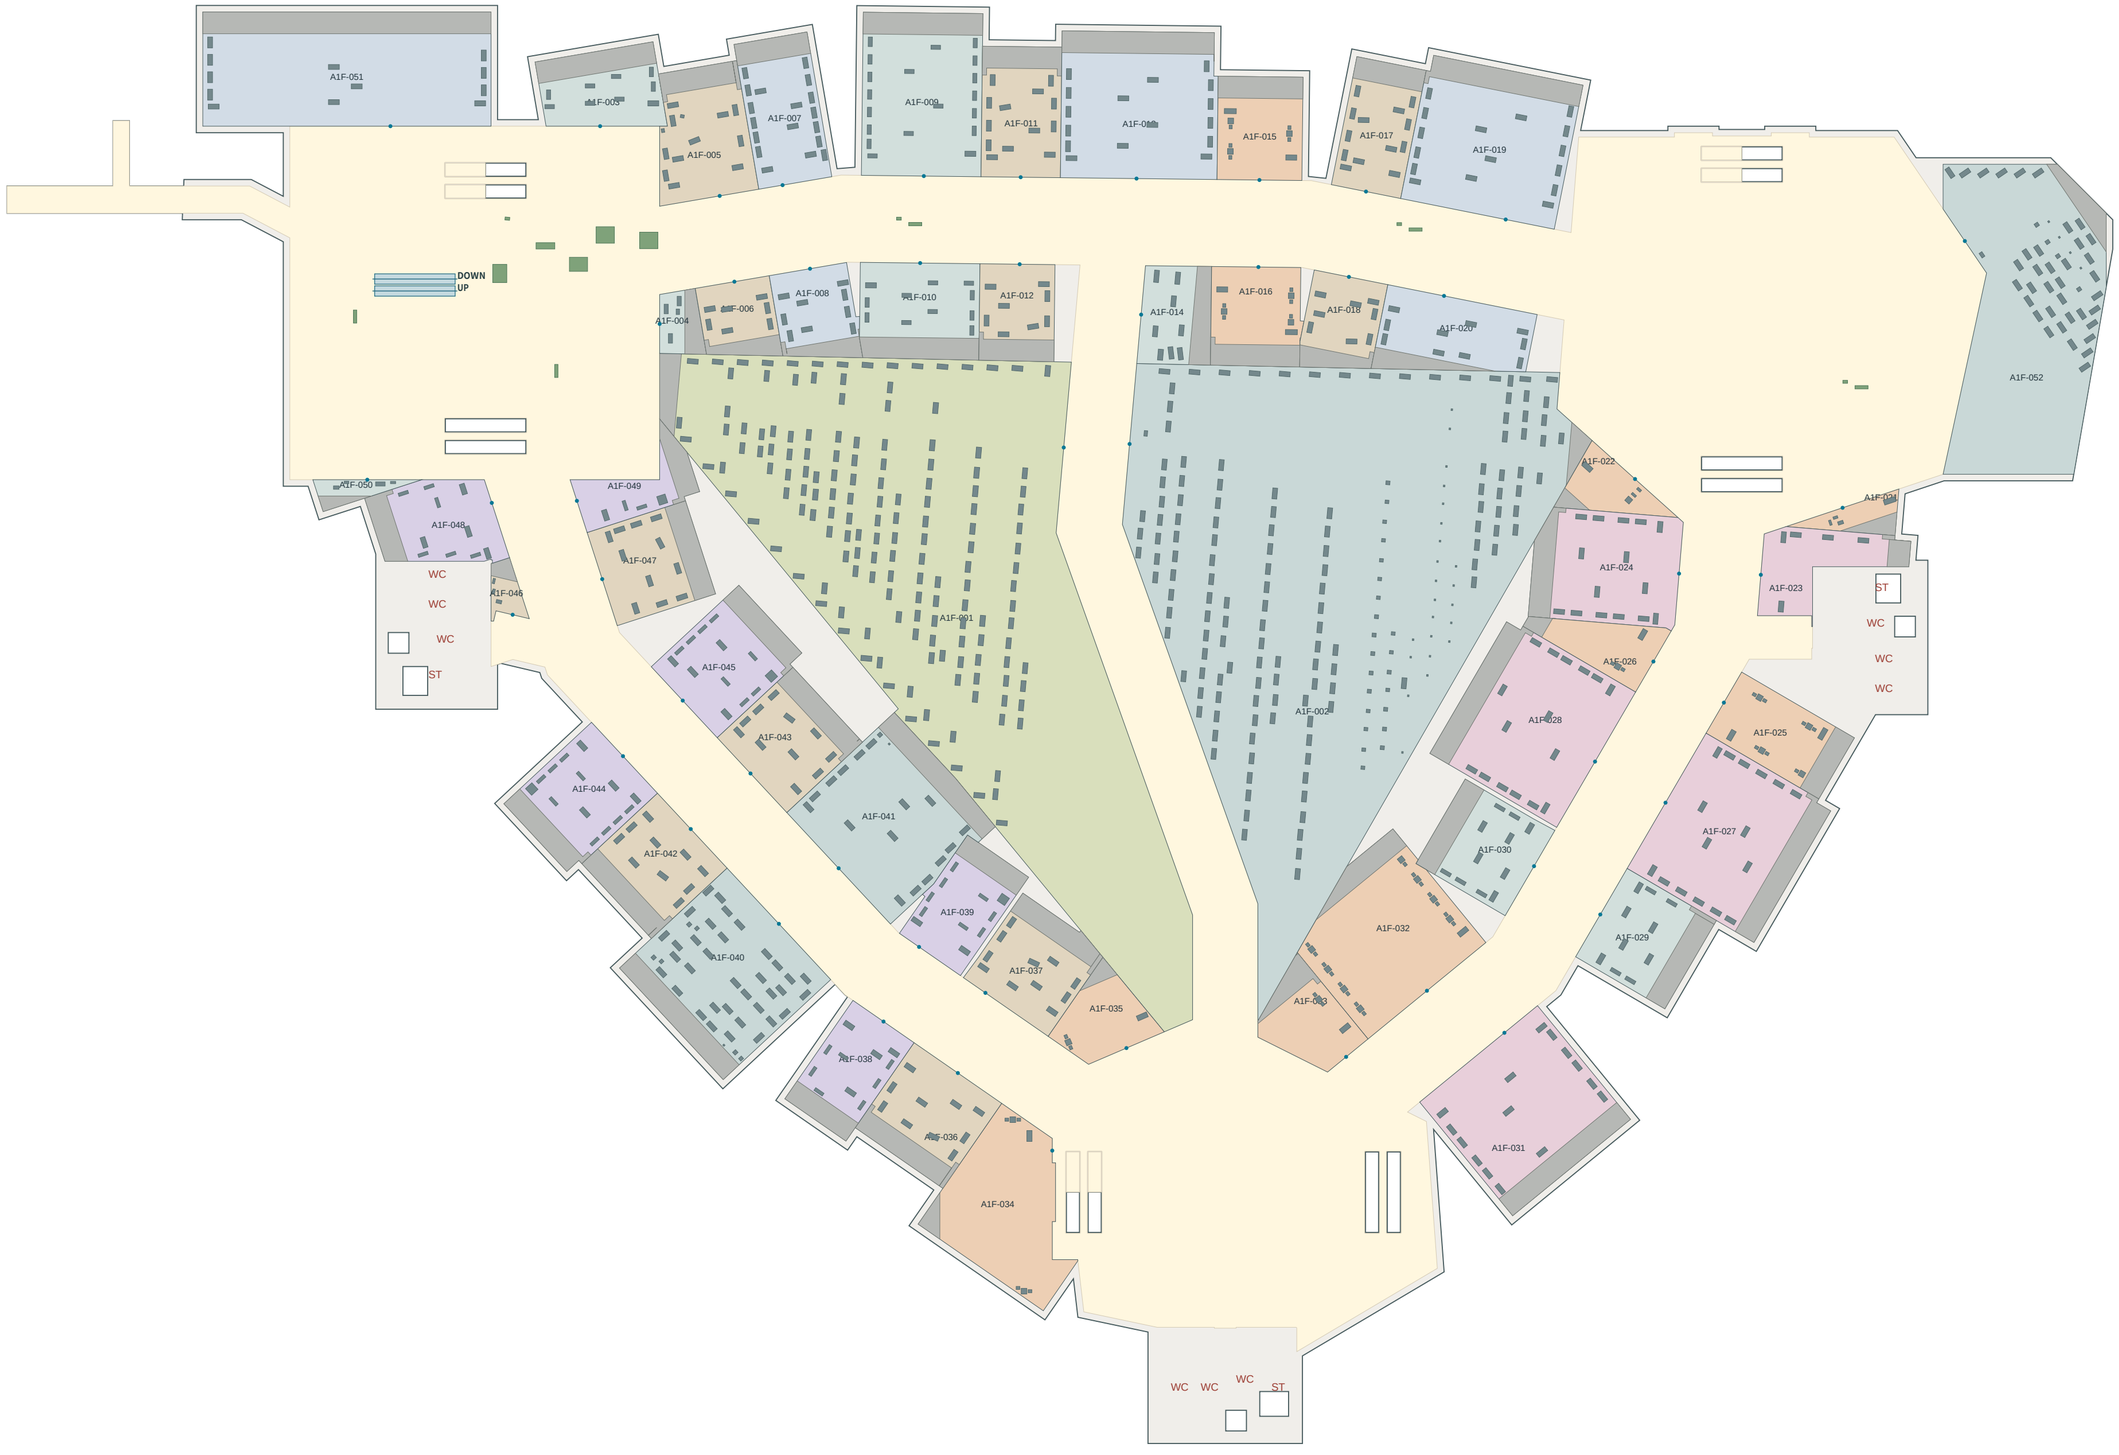


X方向 387.20 m

青丸：実効入口 / 灰：バックヤード / 青灰：什器外接輪郭 / 緑：共用設備 / 橙線：約7.53m連続ES乗継候補

図面の整合性・カプセル検査・自動歩行・人間による実操作は別評価。支持力・基礎・防水・排水・避難容量は未検証。

FIND YOURSELF v22 / A館 2F / 詳細配置・検証図

ゲーム用寸法 / 床レベル Y=5.525m / 建築申請図・構造安全証明ではありません

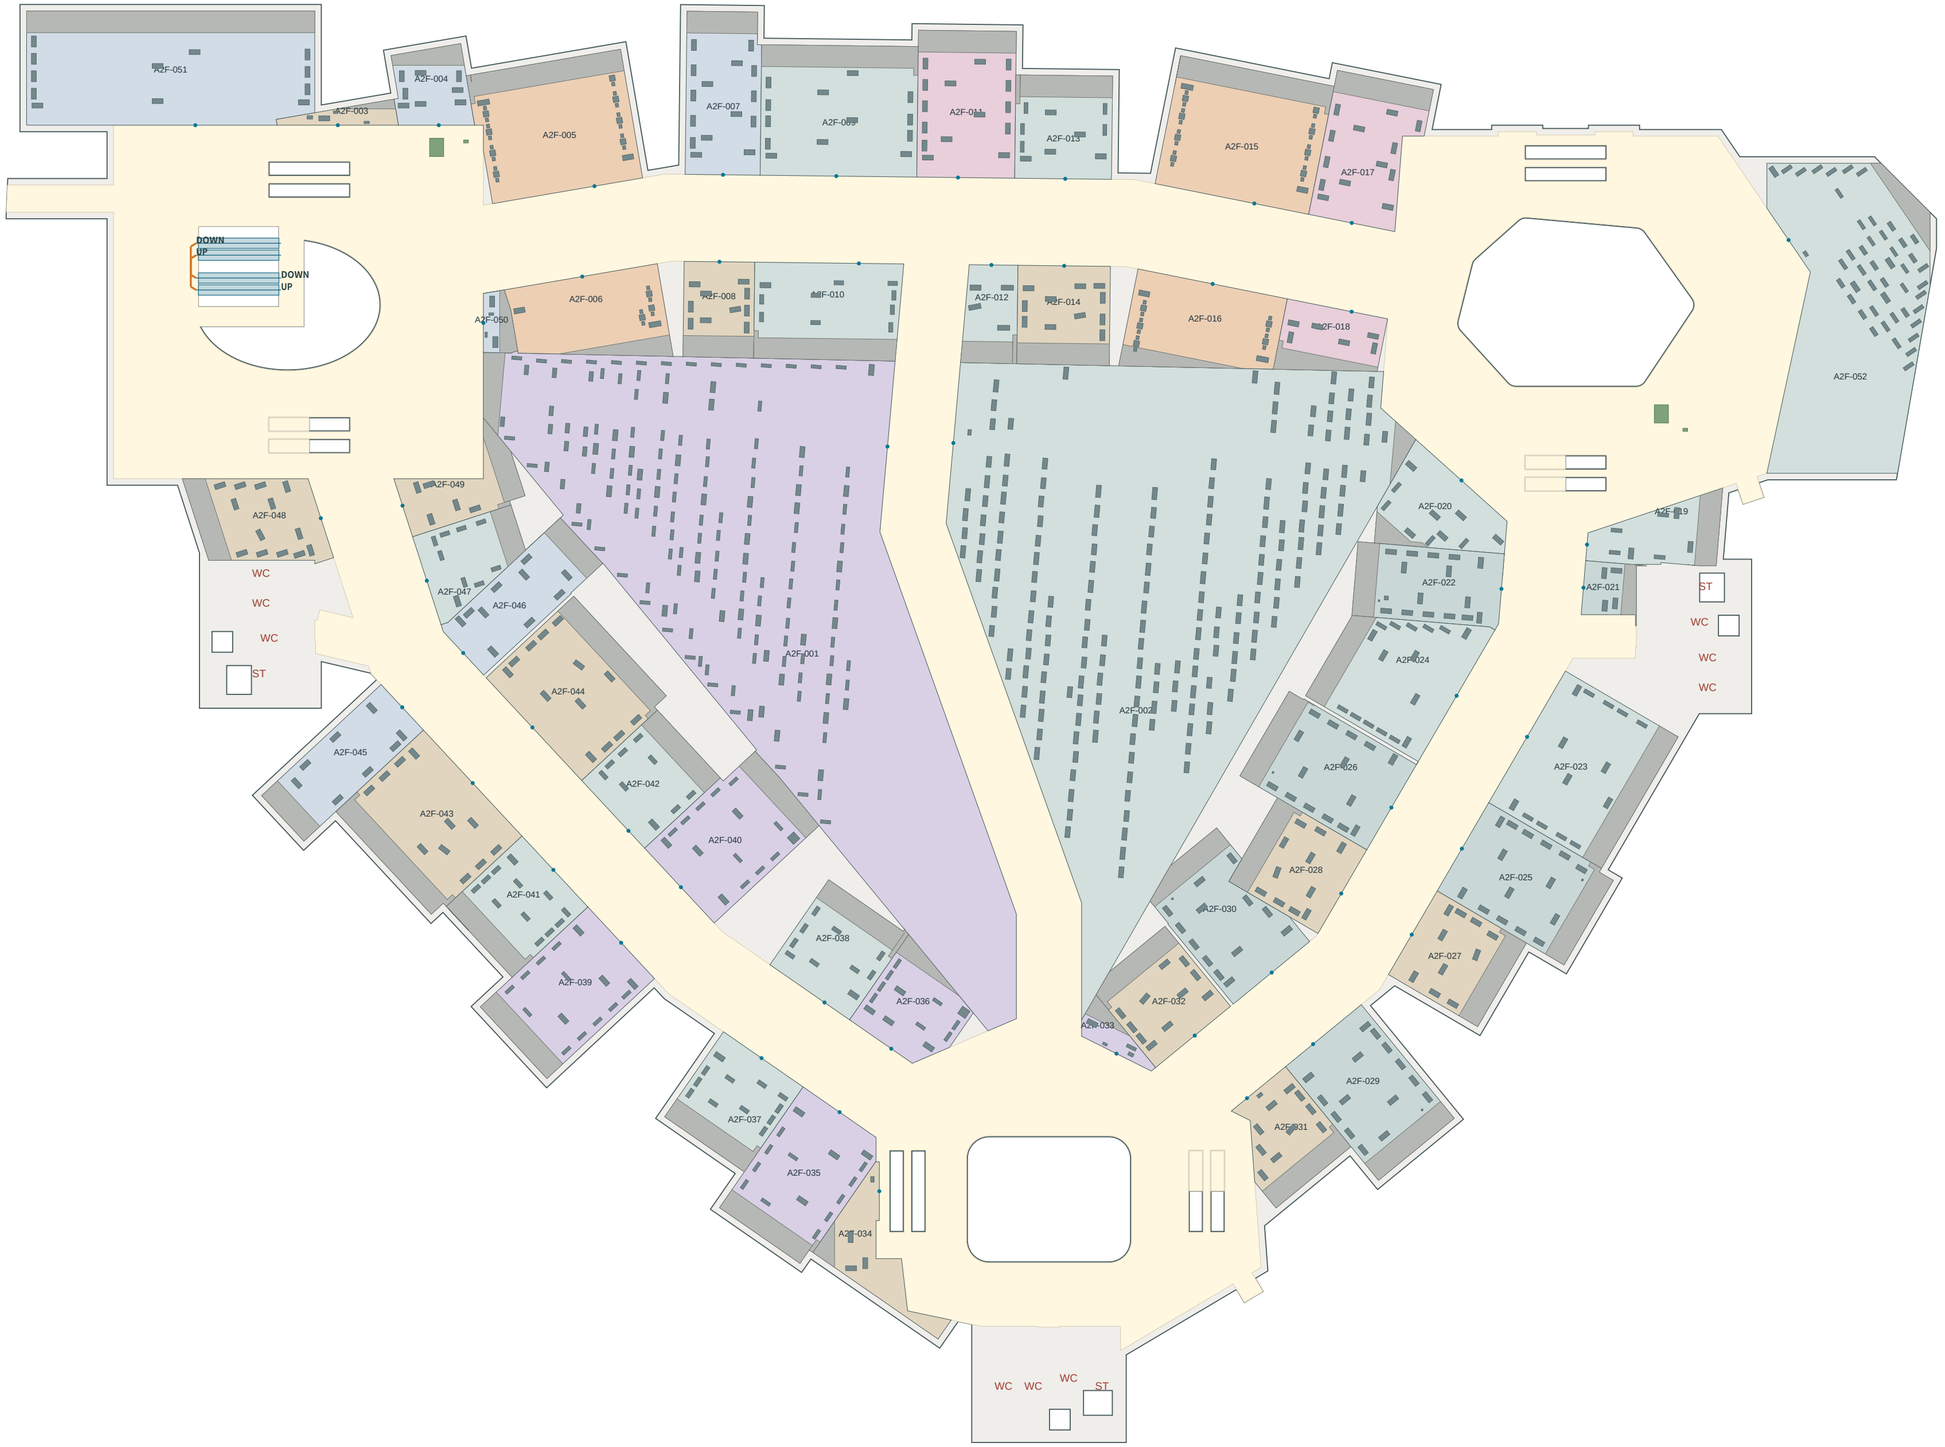


X方向 354.98 m

青丸：実効入口 / 灰：バックヤード / 青灰：什器外接輪郭 / 緑：共用設備 / 橙線：約7.53m連続ES乗継候補

図面の整合性・カプセル検査・自動歩行・人間による実操作は別評価。支持力・基礎・防水・排水・避難容量は未検証。

FIND YOURSELF v22 / A館 3F / 詳細配置・検証図

ゲーム用寸法 / 床レベル Y=10.875m / 建築申請図・構造安全証明ではありません

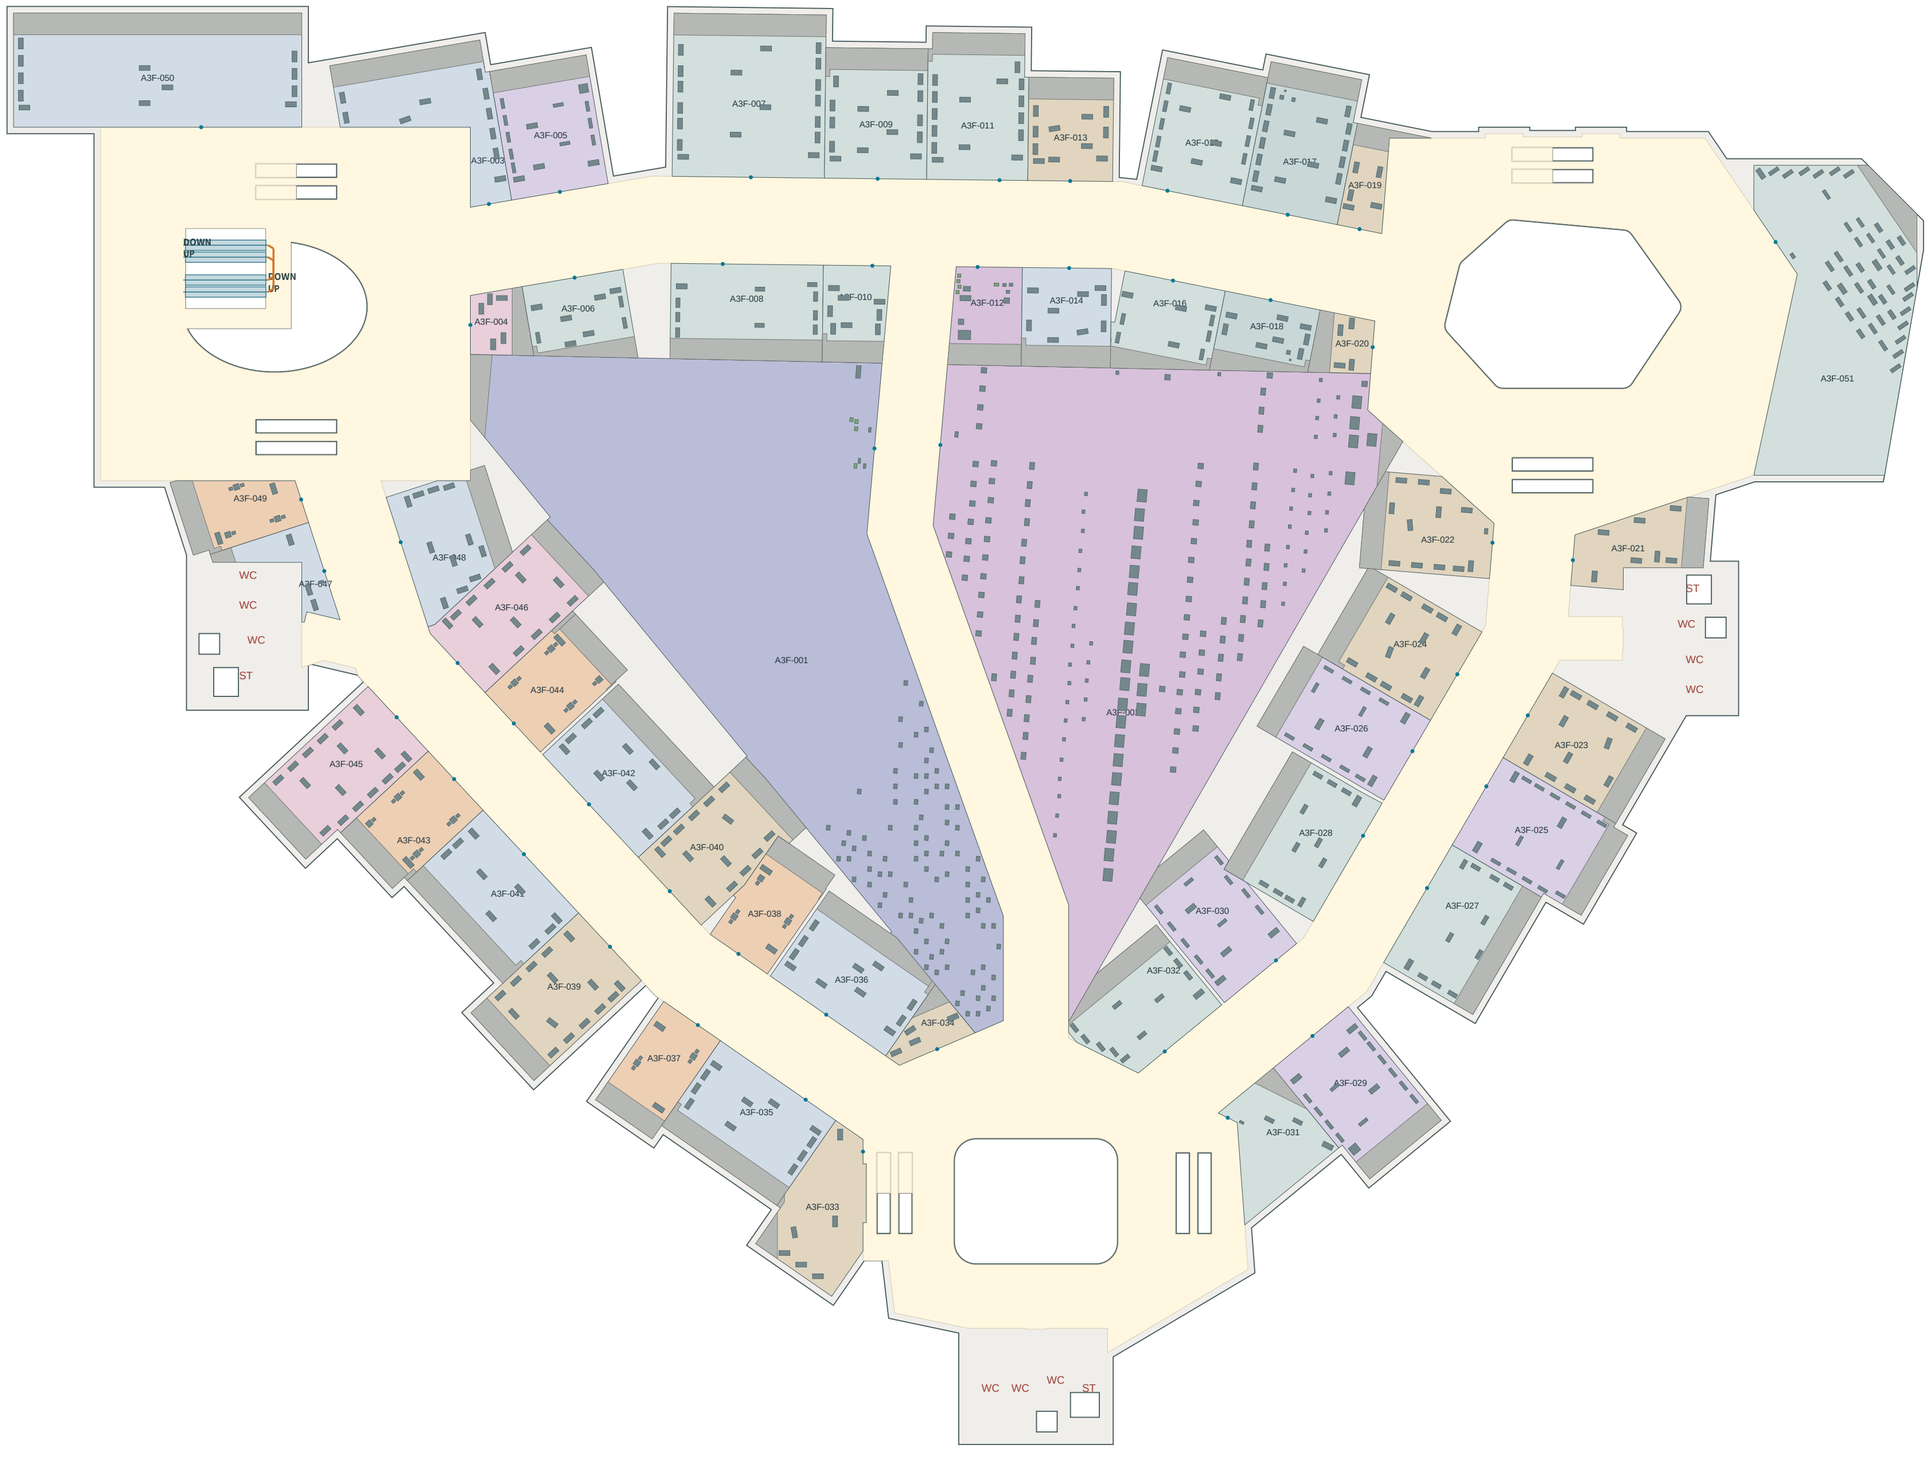


X方向 352.40 m

青丸：実効入口 / 灰：バックヤード / 青灰：什器外接輪郭 / 緑：共用設備 / 橙線：約7.53m連続ES乗継候補

図面の整合性・カプセル検査・自動歩行・人間による実操作は別評価。支持力・基礎・防水・排水・避難容量は未検証。

FIND YOURSELF v22 / A館 RF / 詳細配置・検証図

ゲーム用寸法 / 床レベル Y=16.400m / 建築申請図・構造安全証明ではありません

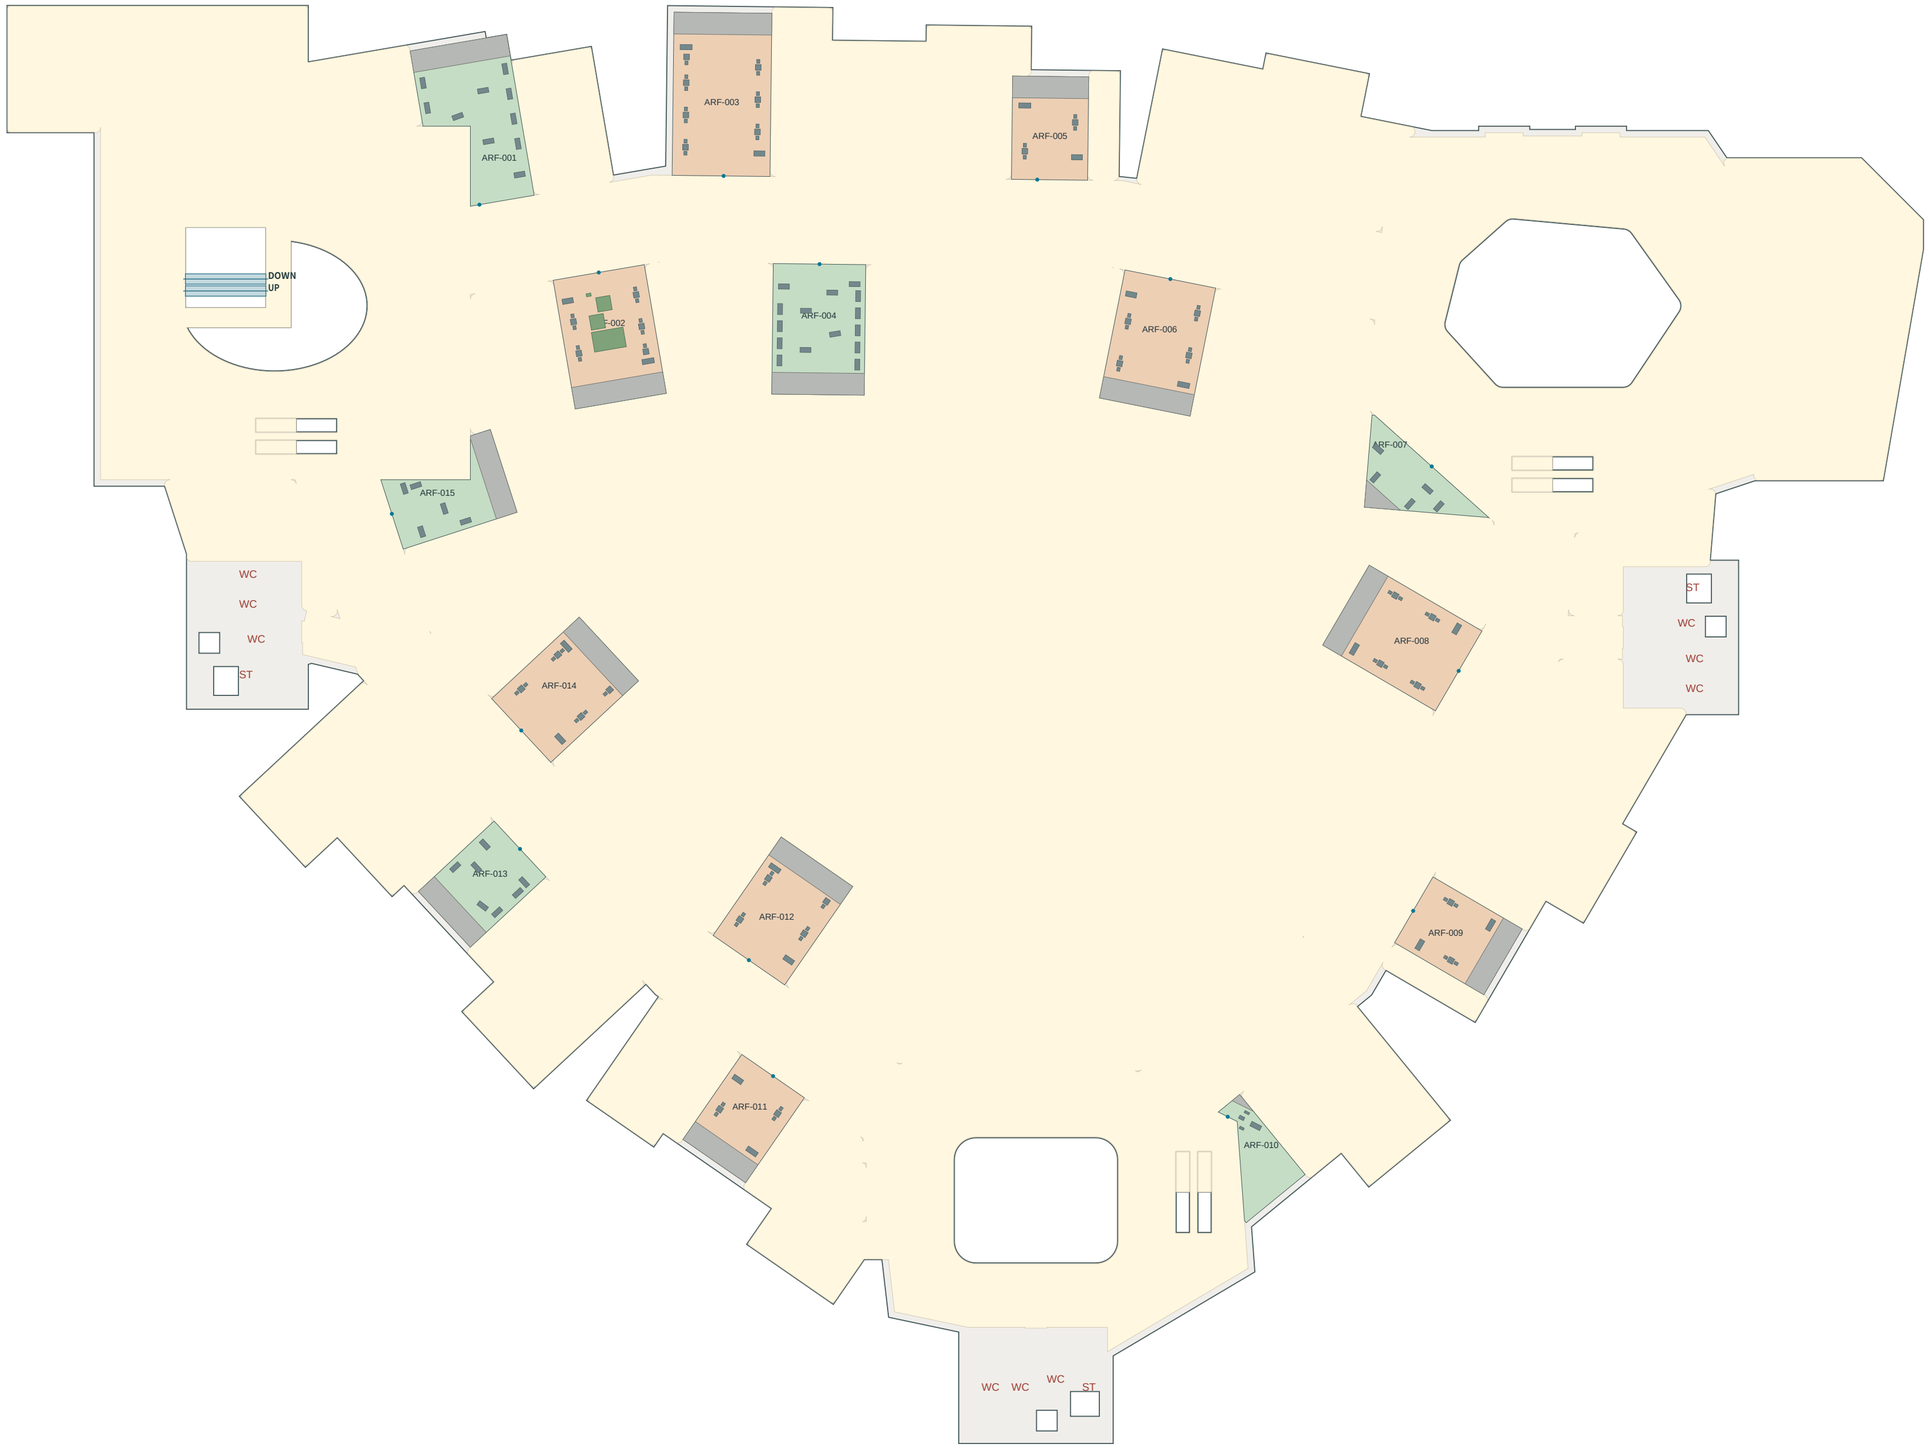


X方向 352.40 m

青丸：実効入口 / 灰：バックヤード / 青灰：什器外接輪郭 / 緑：共用設備 / 橙線：約7.53m連続ES乗継候補

図面の整合性・カプセル検査・自動歩行・人間による実操作は別評価。支持力・基礎・防水・排水・避難容量は未検証。

FIND YOURSELF v22 / B館 B1 / 詳細配置・検証図

ゲーム用寸法 / 床レベル Y=-5.350m / 建築申請図・構造安全証明ではありません

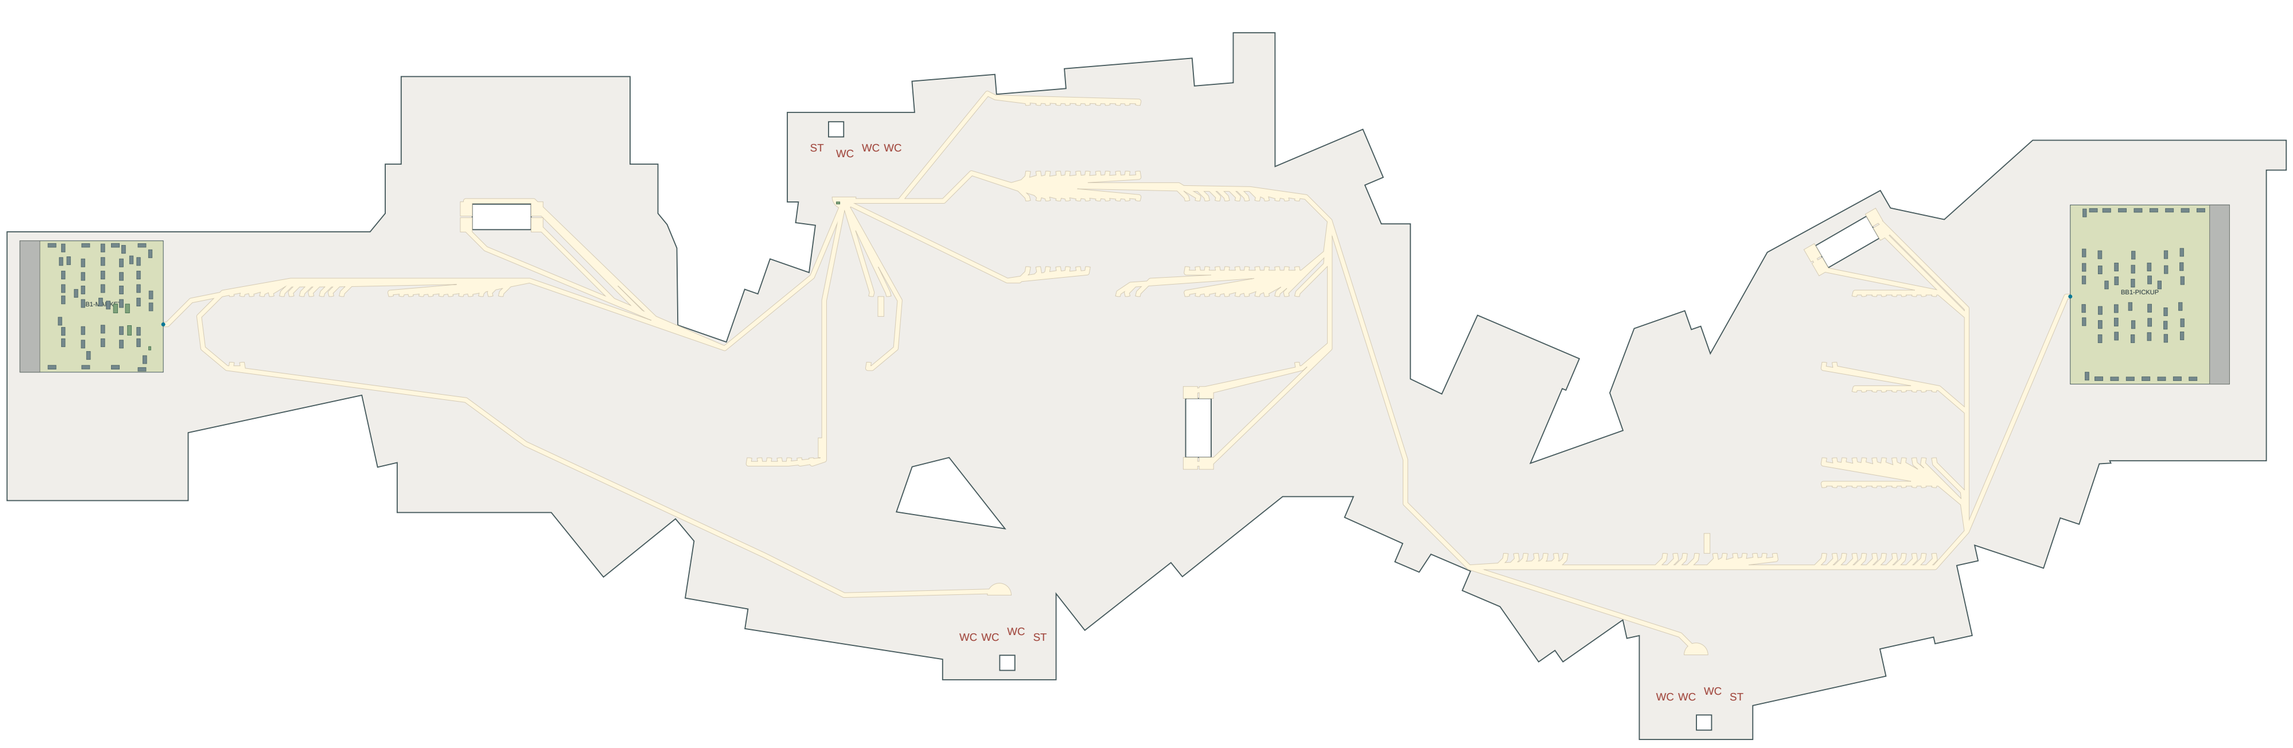


X方向 572.50 m

青丸：実効入口 / 灰：バックヤード / 青灰：什器外接輪郭 / 緑：共用設備 / 橙線：約7.53m連続ES乗継候補

図面の整合性・カプセル検査・自動歩行・人間による実操作は別評価。支持力・基礎・防水・排水・避難容量は未検証。

FIND YOURSELF v22 / B館 1F / 詳細配置・検証図

ゲーム用寸法 / 床レベル Y=0.000m / 建築申請図・構造安全証明ではありません

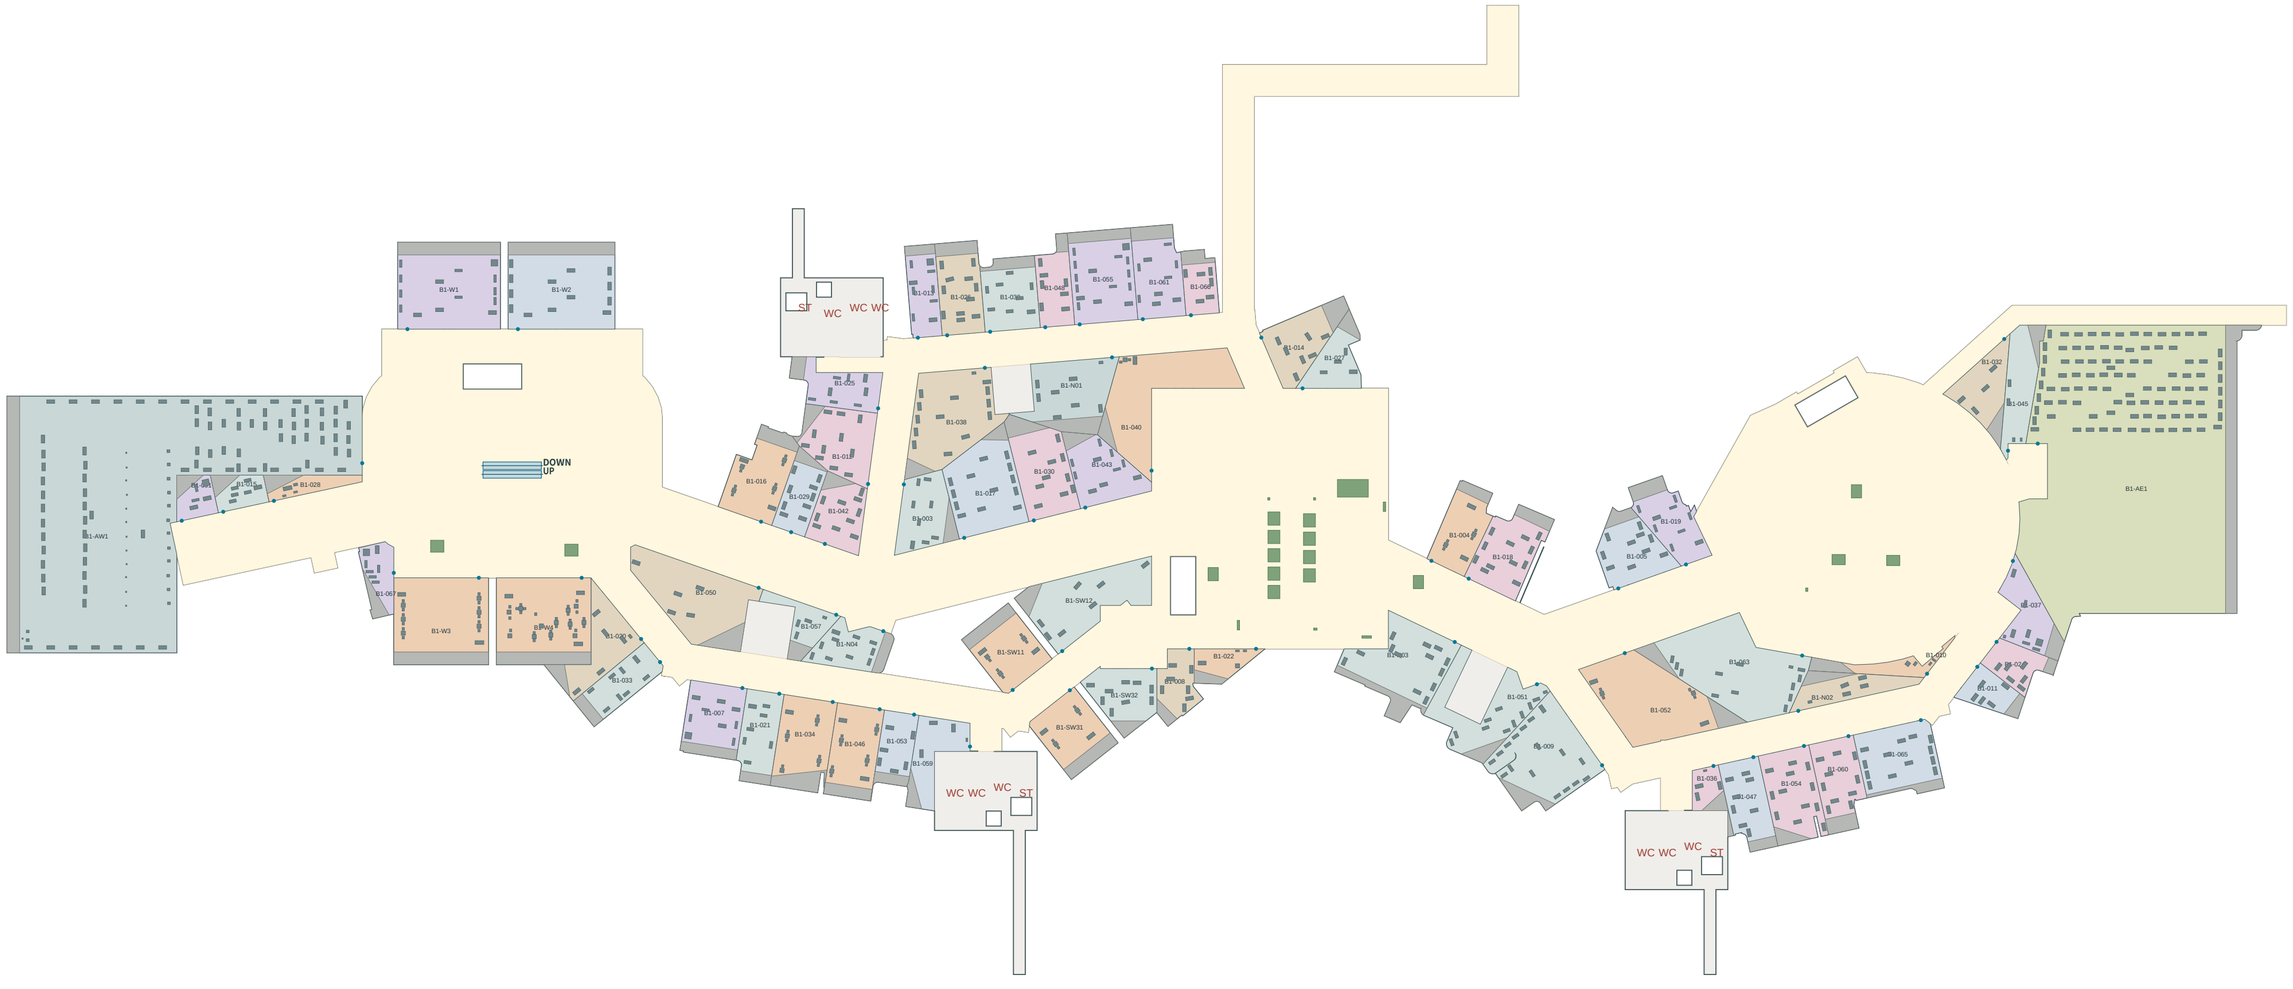


X方向 577.50 m

青丸：実効入口 / 灰：バックヤード / 青灰：什器外接輪郭 / 緑：共用設備 / 橙線：約7.53m連続ES乗継候補

図面の整合性・カプセル検査・自動歩行・人間による実操作は別評価。支持力・基礎・防水・排水・避難容量は未検証。

FIND YOURSELF v22 / B館 2F / 詳細配置・検証図

ゲーム用寸法 / 床レベル Y=5.525m / 建築申請図・構造安全証明ではありません

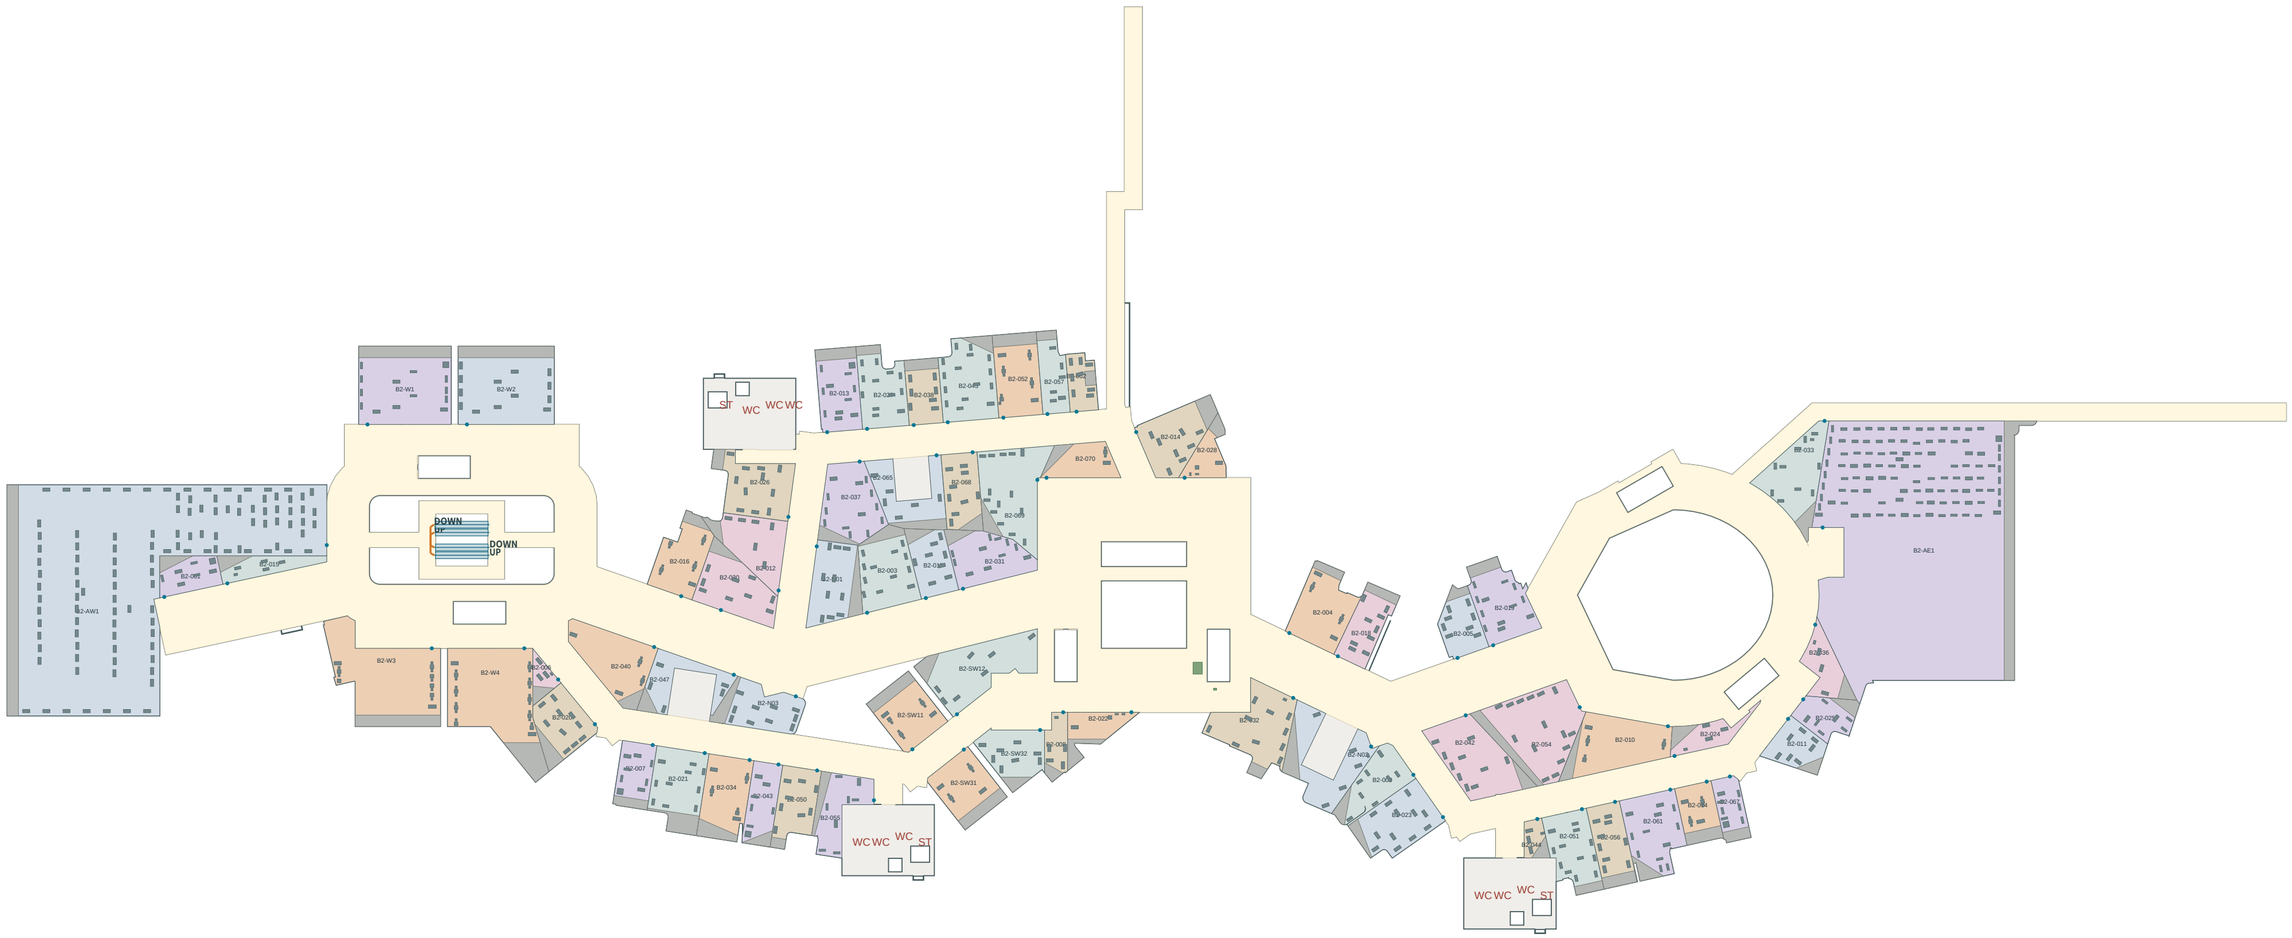


X方向 641.50 m

青丸：実効入口 / 灰：バックヤード / 青灰：什器外接輪郭 / 緑：共用設備 / 橙線：約7.53m連続ES乗継候補

図面の整合性・カプセル検査・自動歩行・人間による実操作は別評価。支持力・基礎・防水・排水・避難容量は未検証。

FIND YOURSELF v22 / B館 3F / 詳細配置・検証図

ゲーム用寸法 / 床レベル Y=10.875m / 建築申請図・構造安全証明ではありません

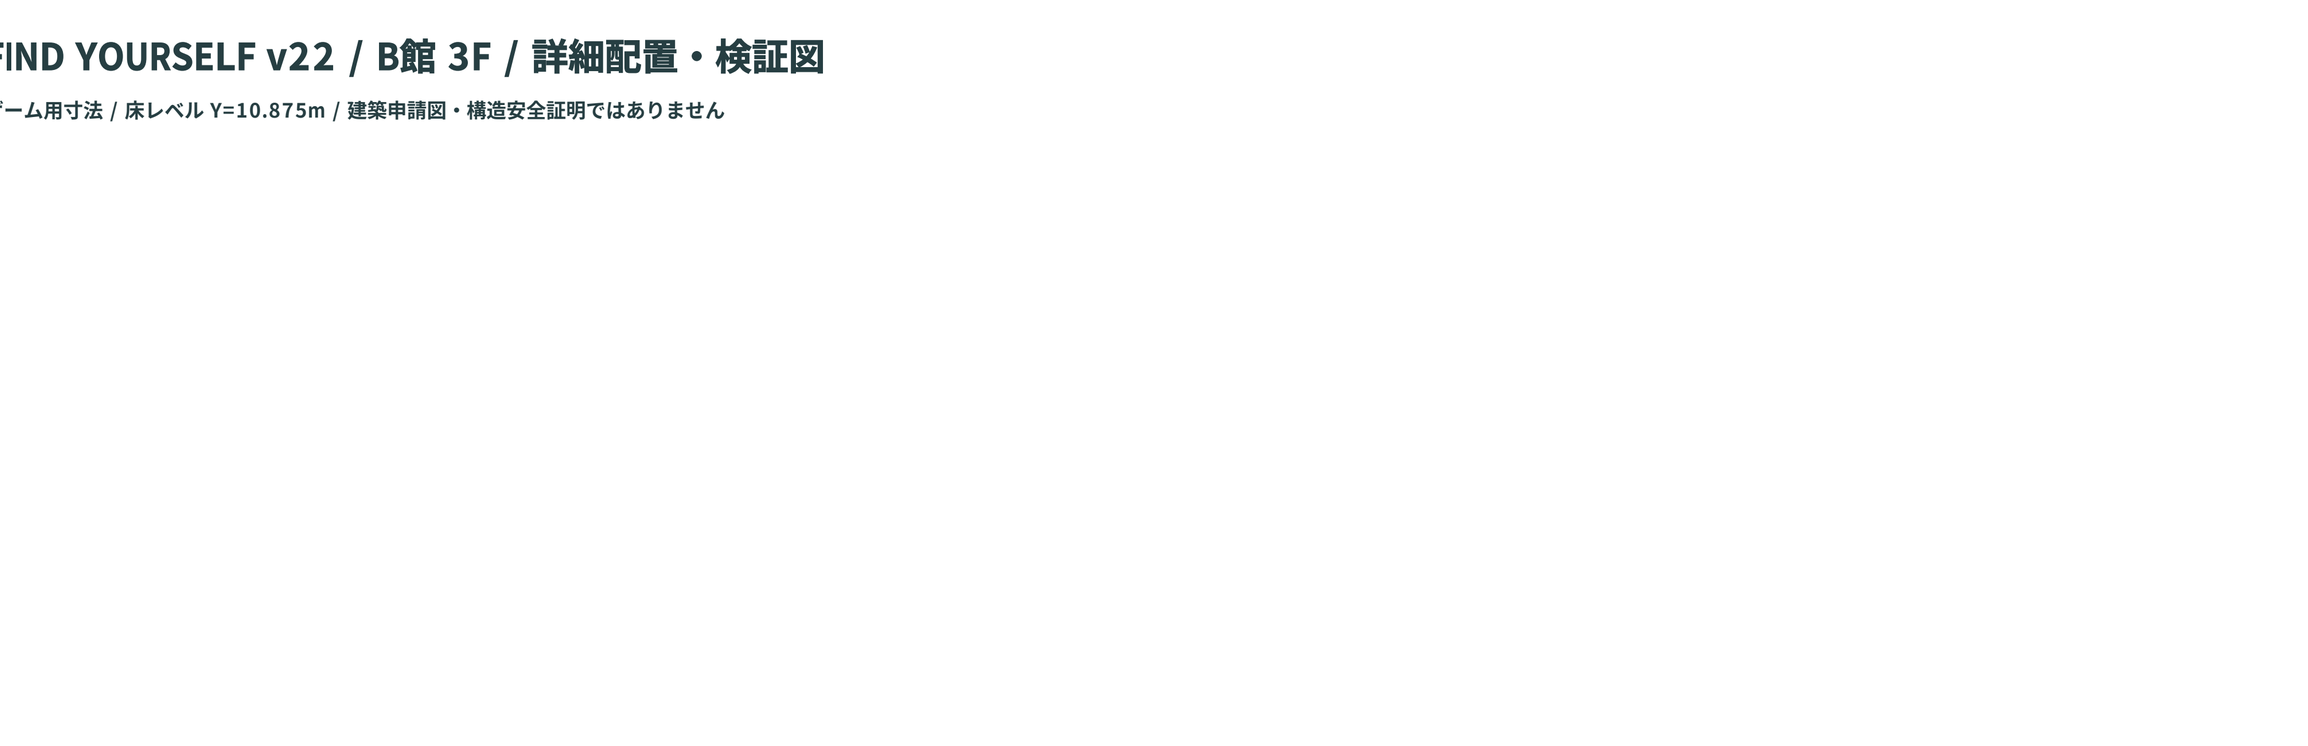


X方向 571.25 m

青丸：実効入口 / 灰：バックヤード / 青灰：什器外接輪郭 / 緑：共用設備 / 橙線：約7.53m連続ES乗継候補

図面の整合性・カプセル検査・自動歩行・人間による実操作は別評価。支持力・基礎・防水・排水・避難容量は未検証。

FIND YOURSELF v22 / B館 RF / 詳細配置・検証図

ゲーム用寸法 / 床レベル Y=16.400m / 建築申請図・構造安全証明ではありません

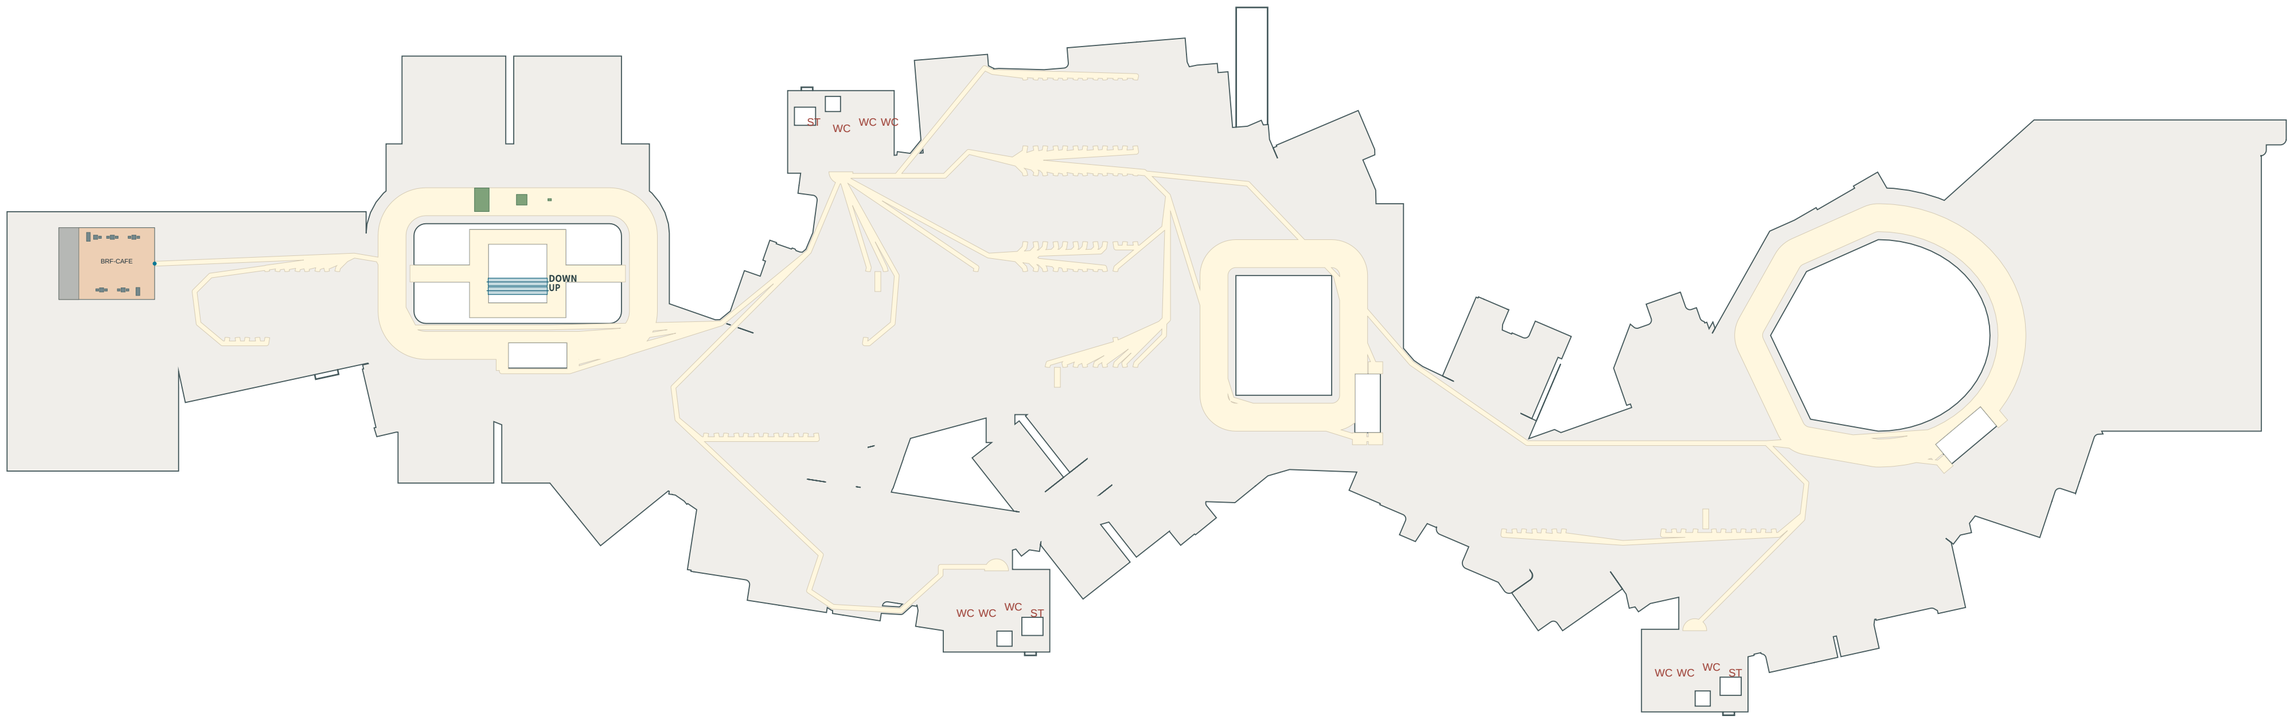


X方向 571.25 m

青丸：実効入口 / 灰：バックヤード / 青灰：什器外接輪郭 / 緑：共用設備 / 橙線：約7.53m連続ES乗継候補

図面の整合性・カプセル検査・自動歩行・人間による実操作は別評価。支持力・基礎・防水・排水・避難容量は未検証。

FIND YOURSELF v22 / C館 B1 / 詳細配置・検証図

ゲーム用寸法 / 床レベル Y=-5.350m / 建築申請図・構造安全証明ではありません

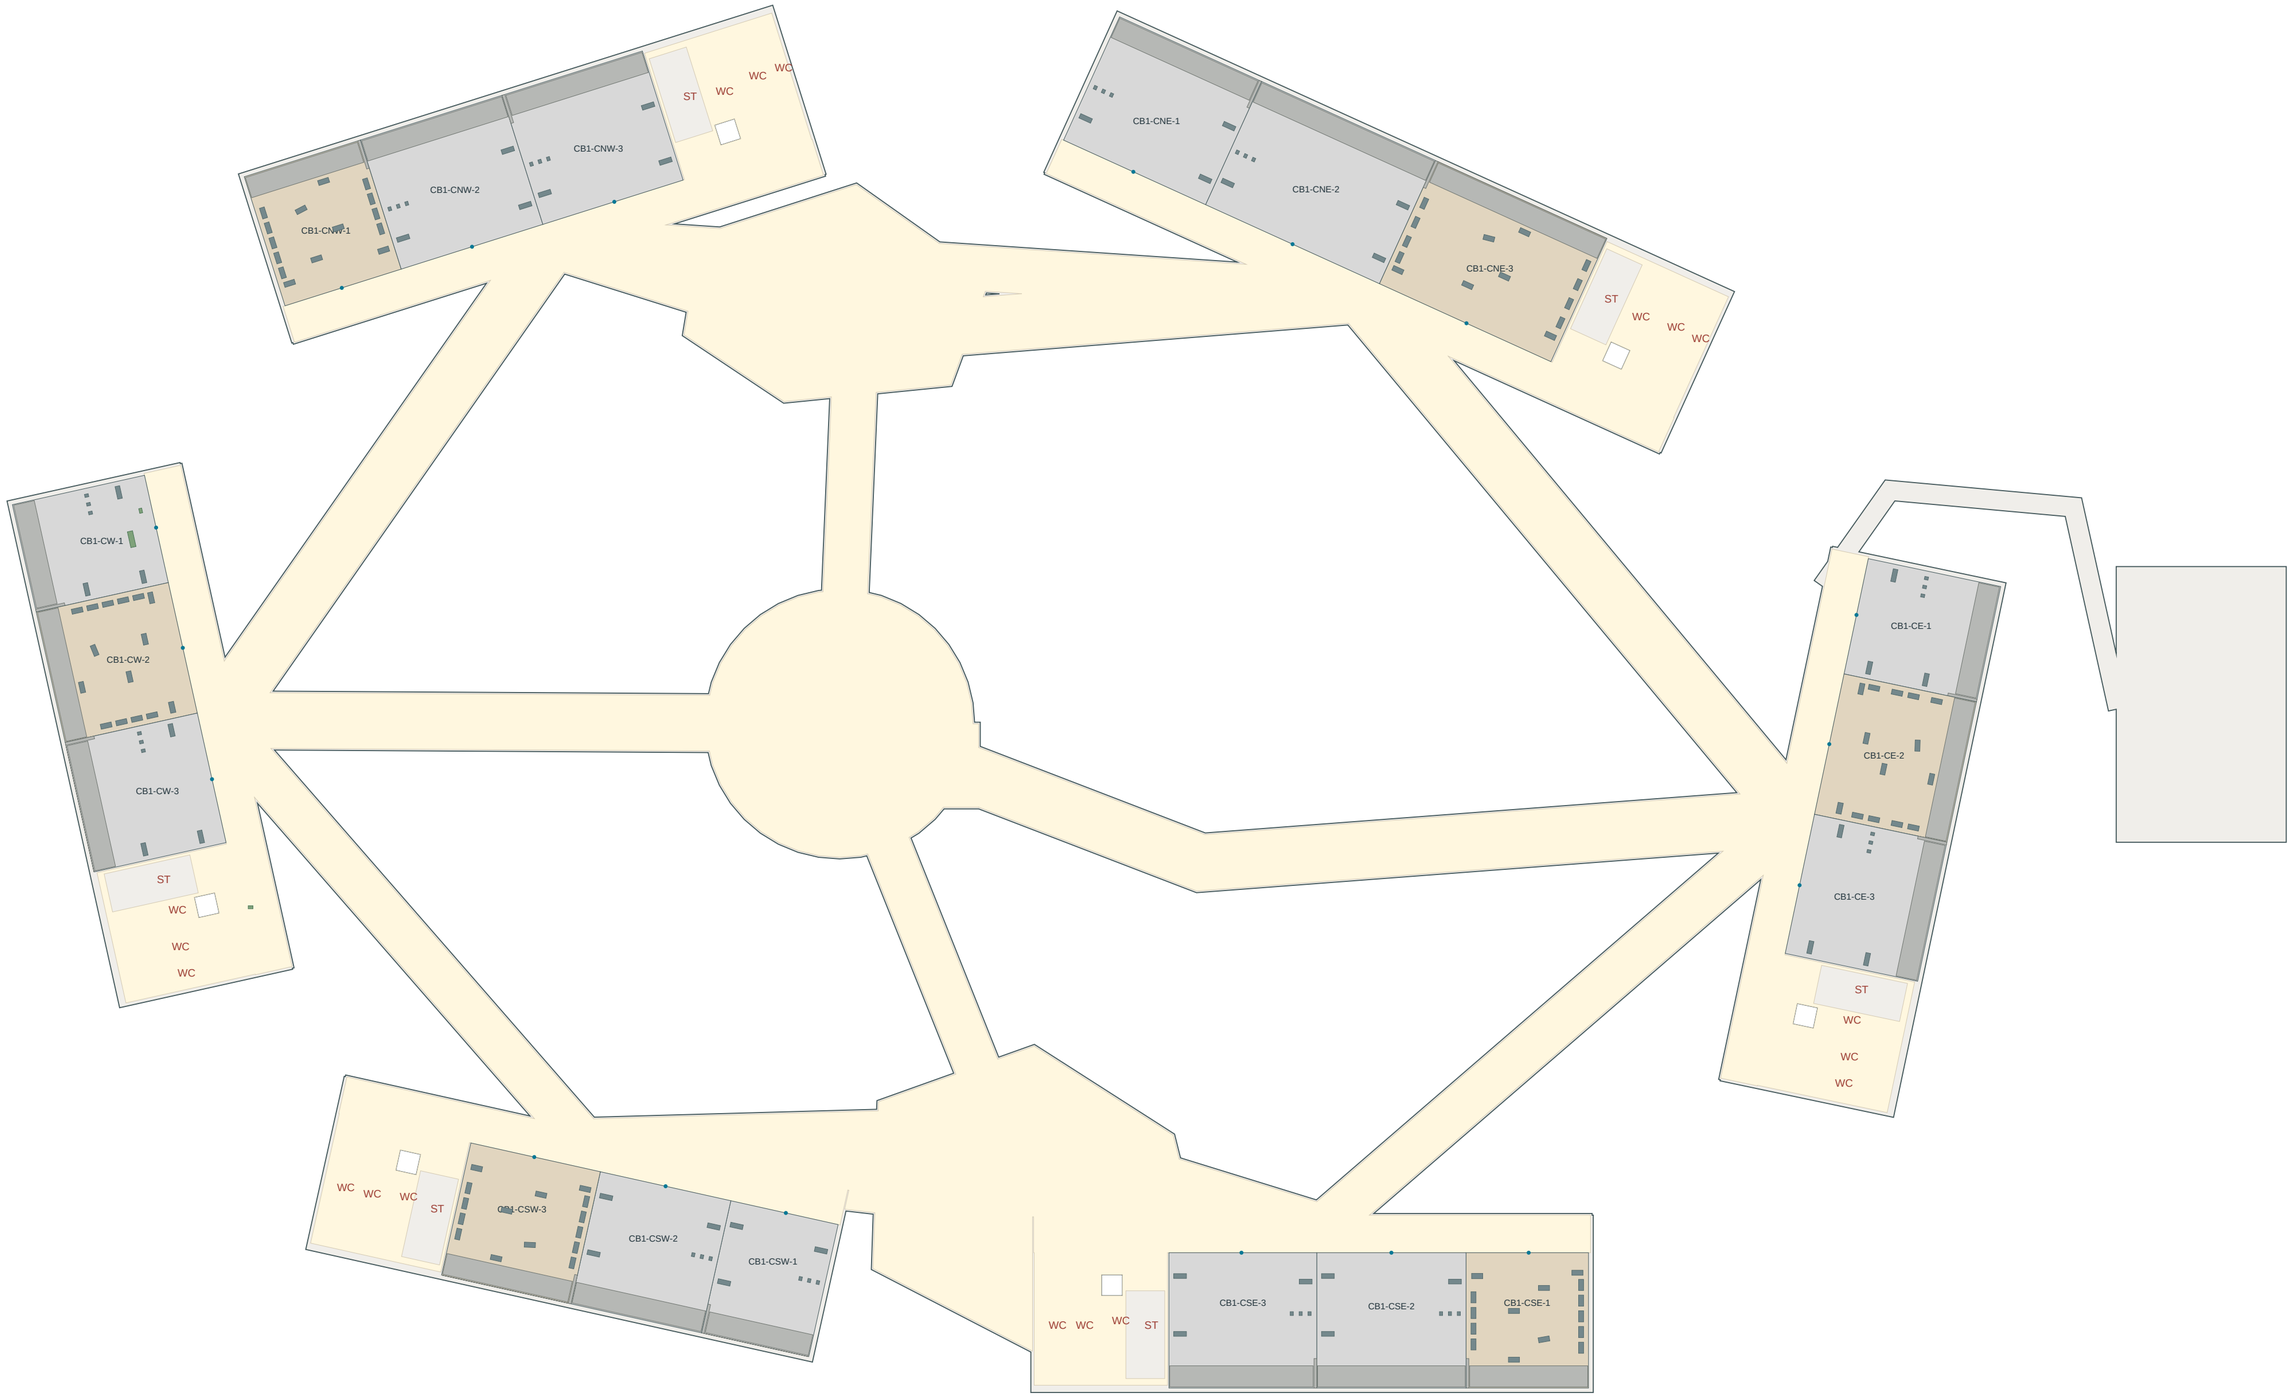


X方向 410.13 m

青丸：実効入口 / 灰：バックヤード / 青灰：什器外接輪郭 / 緑：共用設備 / 橙線：約7.53m連続ES乗継候補

図面の整合性・カプセル検査・自動歩行・人間による実操作は別評価。支持力・基礎・防水・排水・避難容量は未検証。

FIND YOURSELF v22 / C館 1F / 詳細配置・検証図

ゲーム用寸法 / 床レベル Y=0.000m / 建築申請図・構造安全証明ではありません

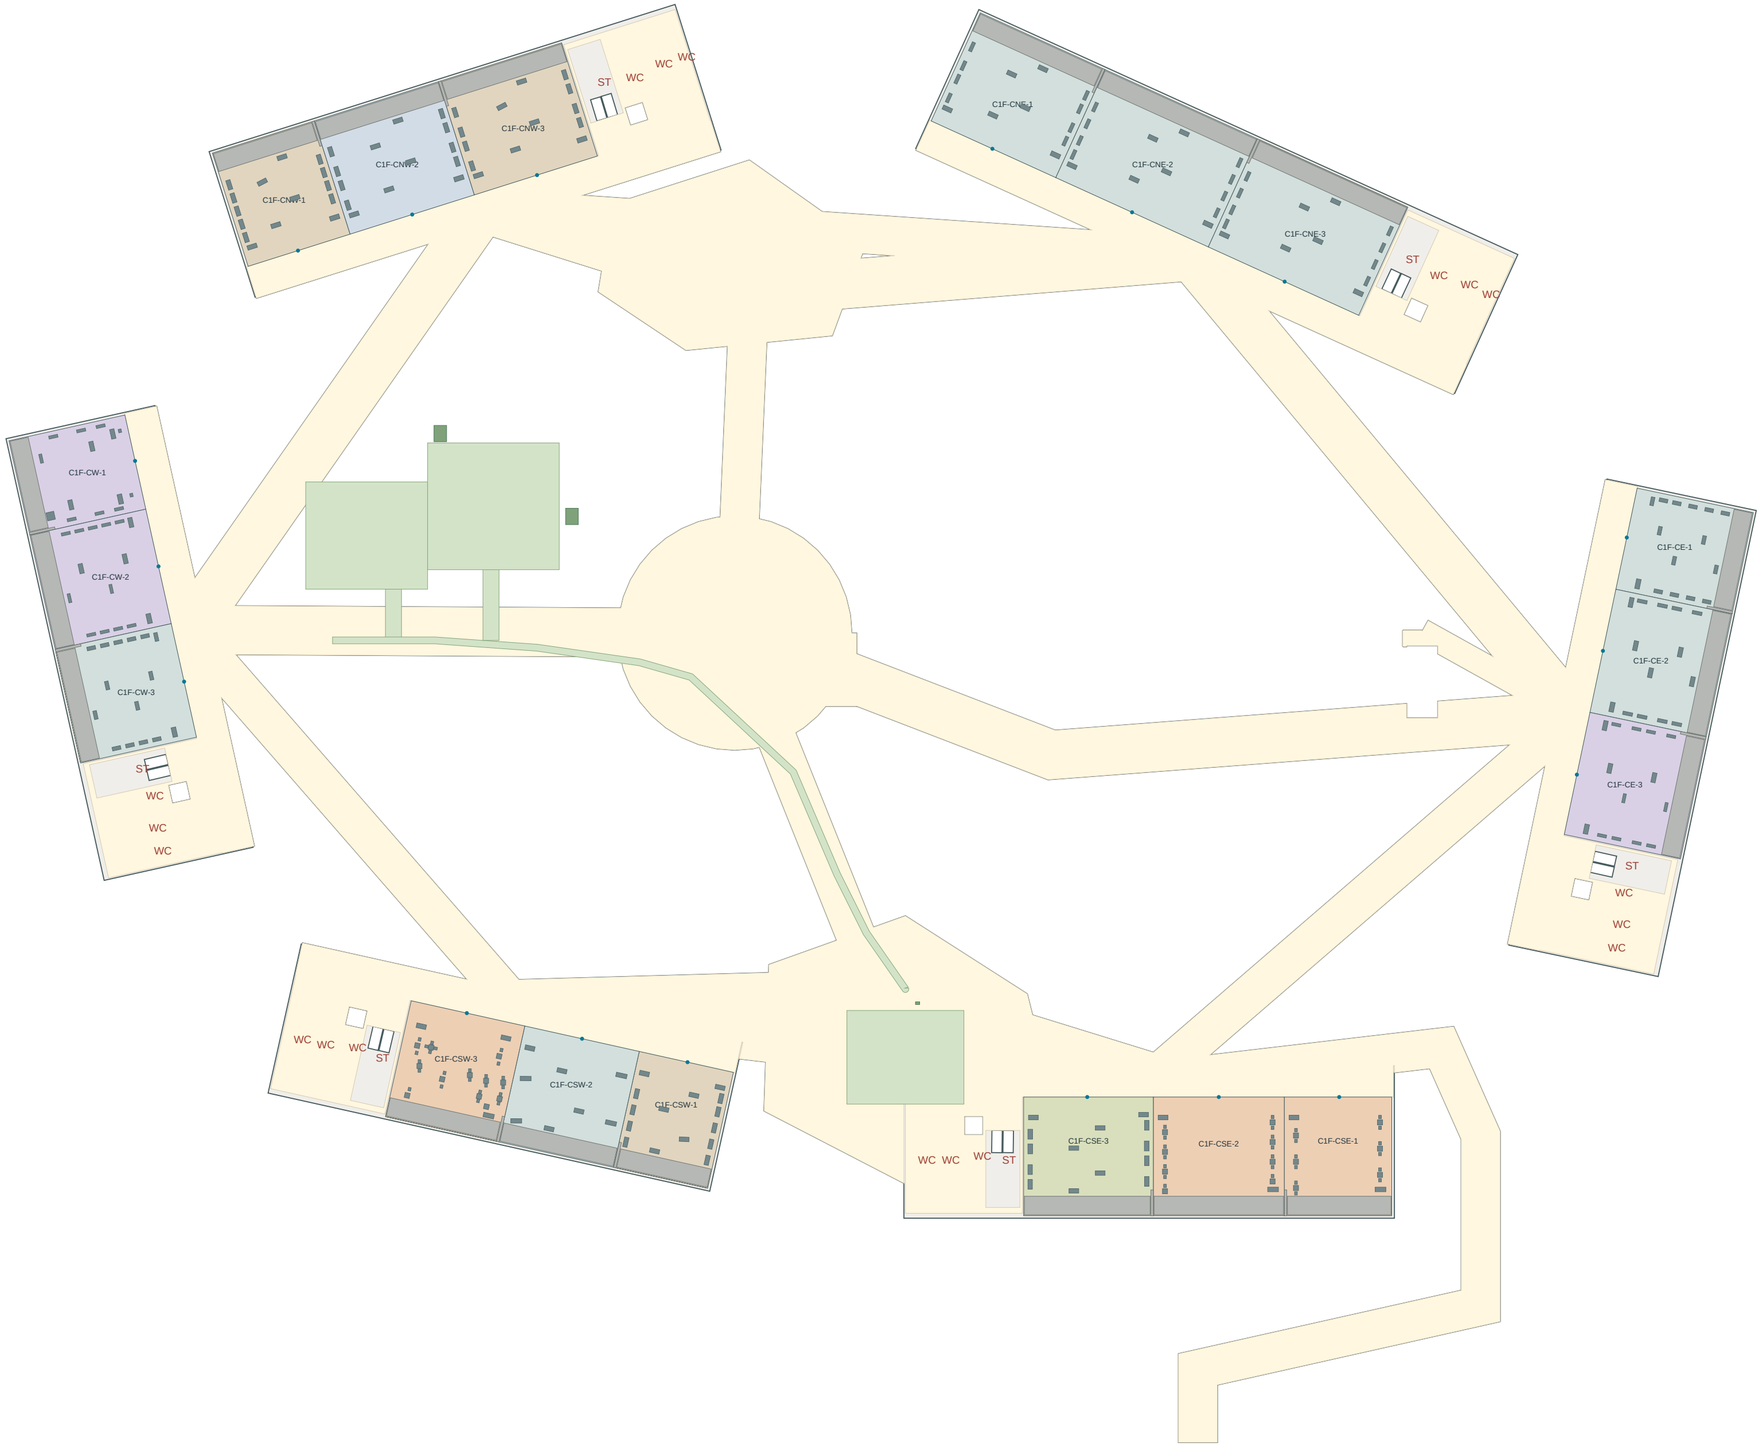


X方向 359.00 m

青丸：実効入口 / 灰：バックヤード / 青灰：什器外接輪郭 / 緑：共用設備 / 橙線：約7.53m連続ES乗継候補

図面の整合性・カプセル検査・自動歩行・人間による実操作は別評価。支持力・基礎・防水・排水・避難容量は未検証。

FIND YOURSELF v22 / C館 2F / 詳細配置・検証図

ゲーム用寸法 / 床レベル Y=5.525m / 建築申請図・構造安全証明ではありません

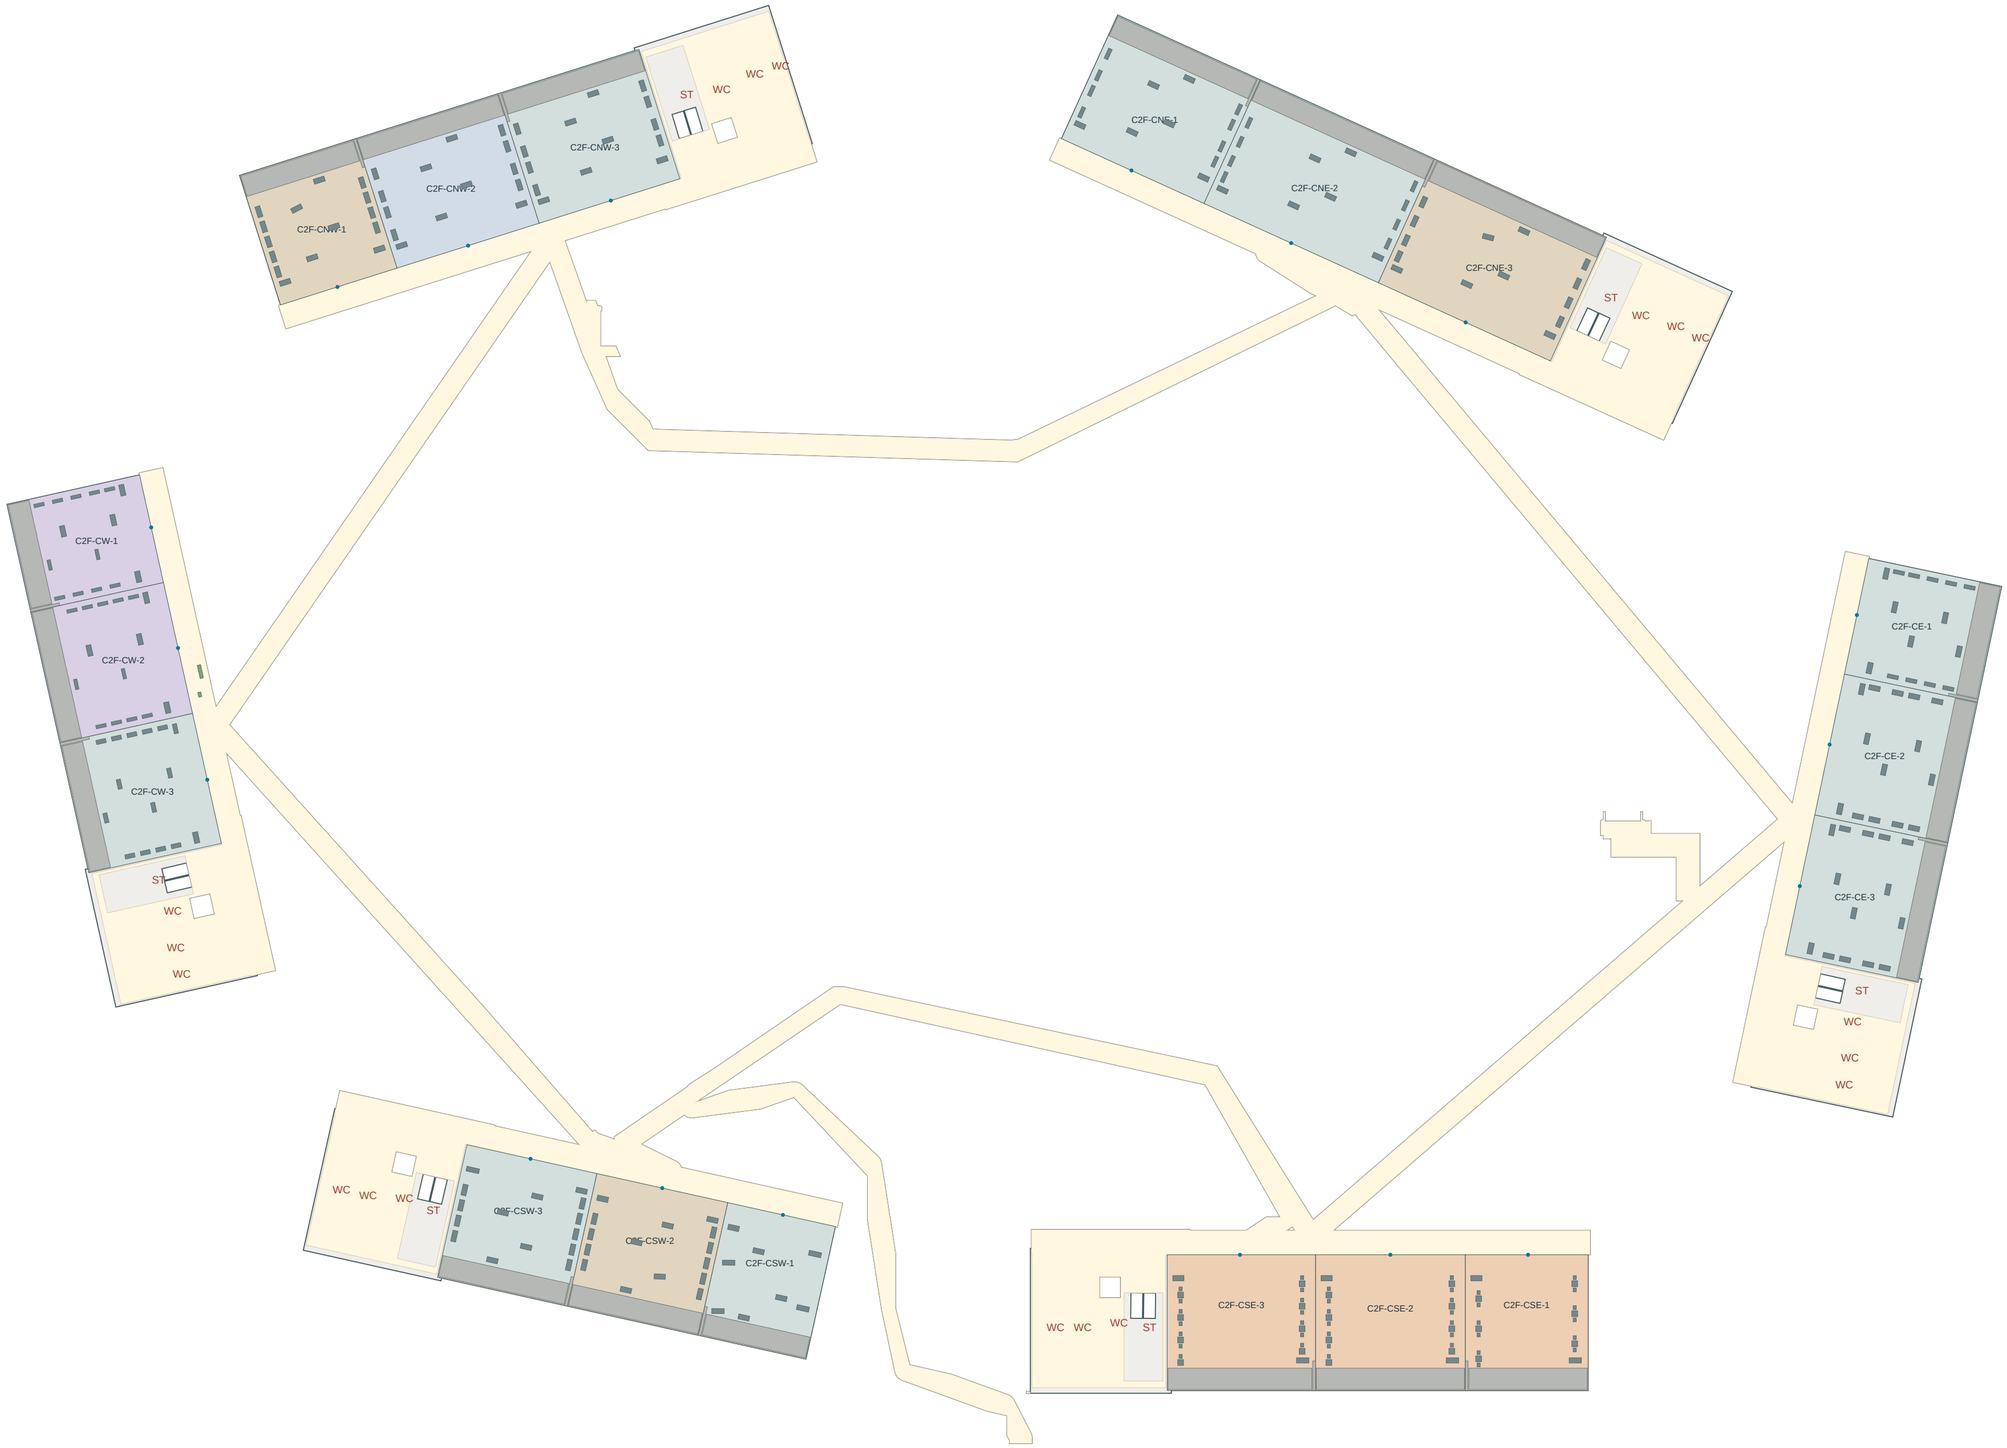


X方向 357.79 m


青丸：実効入口 / 灰：バックヤード / 青灰：什器外接輪郭 / 緑：共用設備 / 橙線：約7.53m連続ES乗継候補


図面の整合性・カプセル検査・自動歩行・人間による実操作は別評価。支持力・基礎・防水・排水・避難容量は未検証。


FIND YOURSELF v22 / C館 3F / 詳細配置・検証図


ゲーム用寸法 / 床レベル Y=10.875m / 建築申請図・構造安全証明ではありません

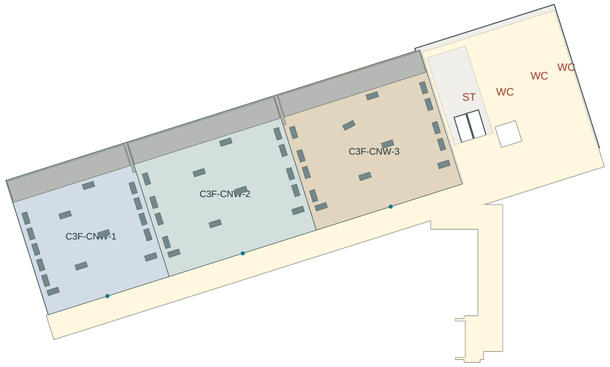


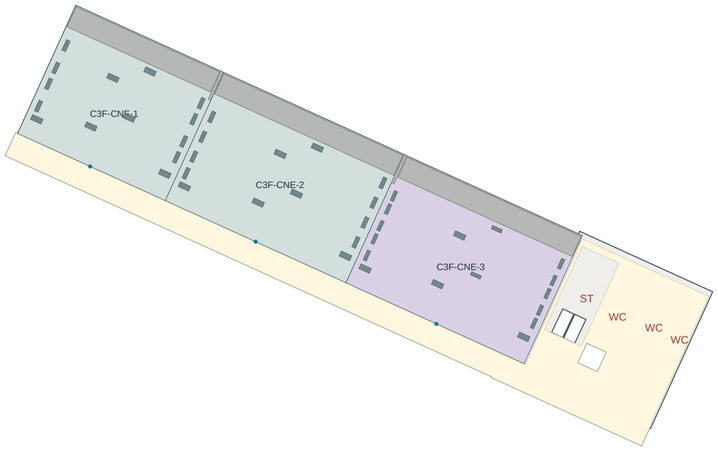

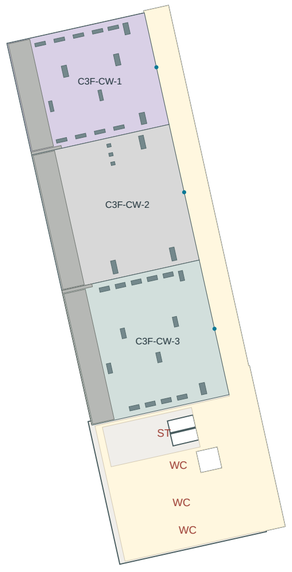

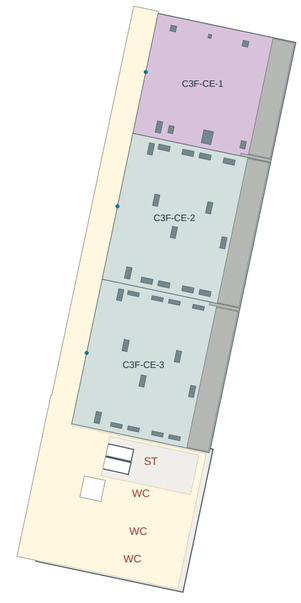

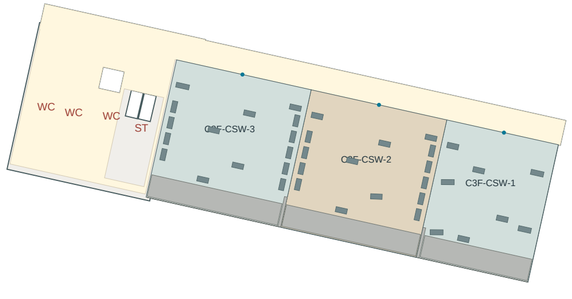

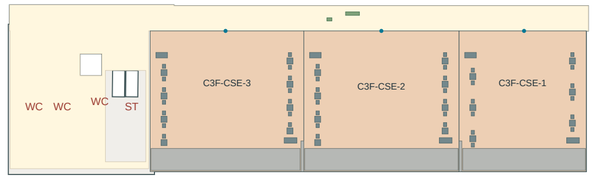


X方向 357.79 m

青丸：実効入口 / 灰：バックヤード / 青灰：什器外接輪郭 / 緑：共用設備 / 橙線：約7.53m連続ES乗継候補

図面の整合性・カプセル検査・自動歩行・人間による実操作は別評価。支持力・基礎・防水・排水・避難容量は未検証。

FIND YOURSELF v22 / C館 RF / 詳細配置・検証図

ゲーム用寸法 / 床レベル Y=16.400m / 建築申請図・構造安全証明ではありません

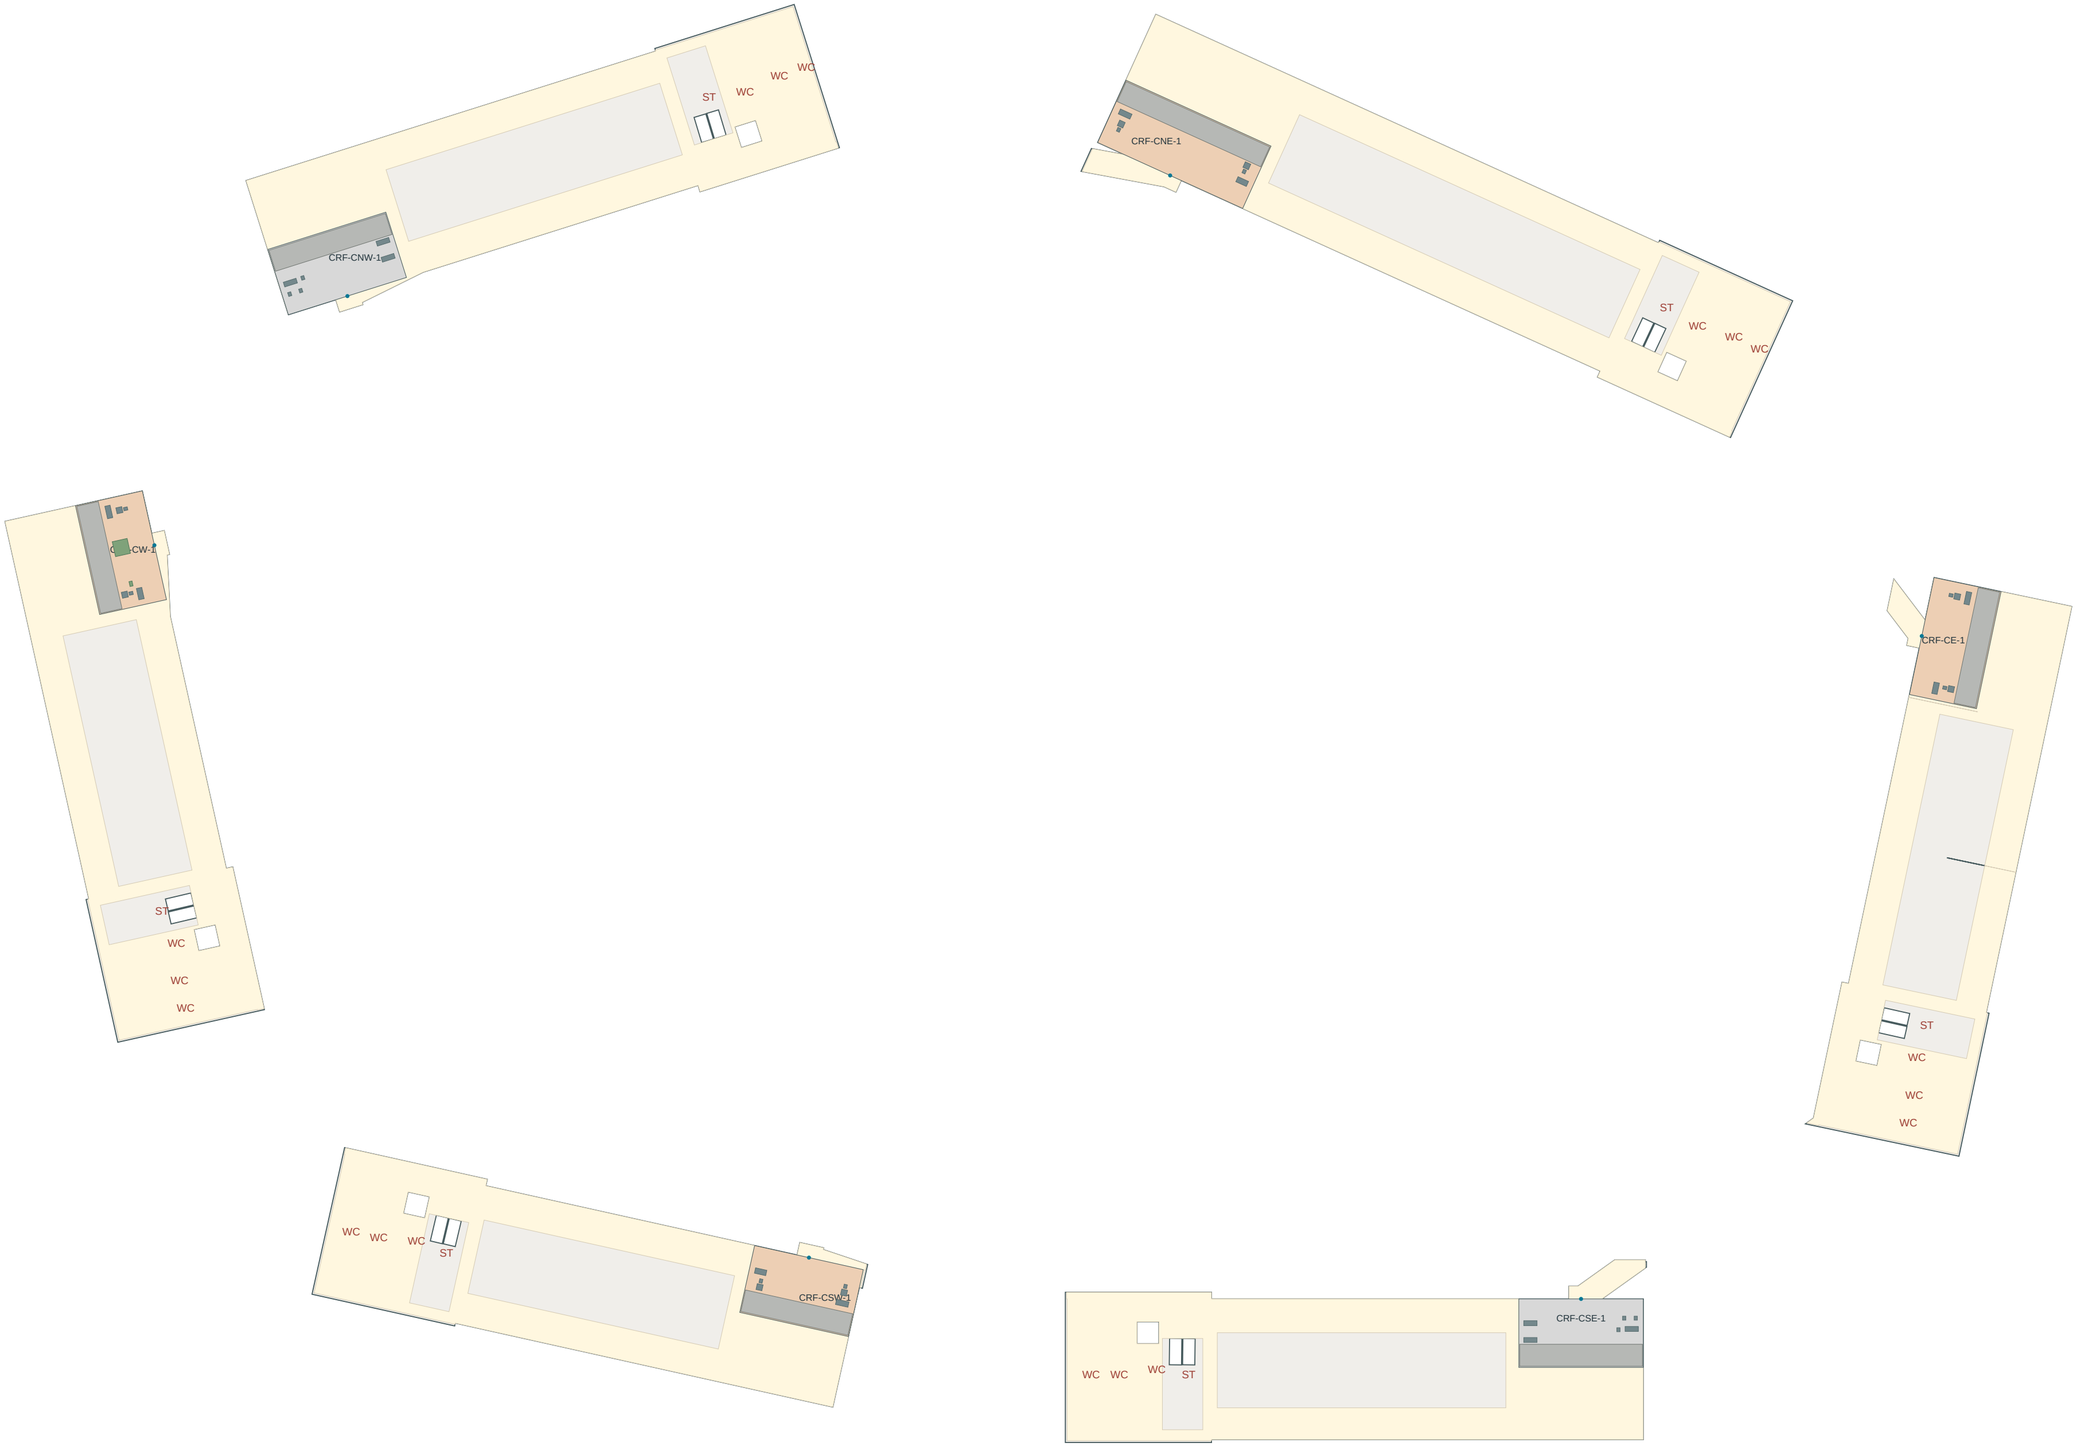


青丸：実効入口 / 灰：バックヤード / 青灰：什器外接輪郭 / 緑：共用設備 / 橙線：約7.53m連続ES乗継候補

図面の整合性・カプセル検査・自動歩行・人間による実操作は別評価。支持力・基礎・防水・排水・避難容量は未検証。

A館 連続エスカレーター / 投影断面

1F〜RF / 機材の奥行き位置は平面図参照 / 移動処理は既存の連続斜面方式を維持

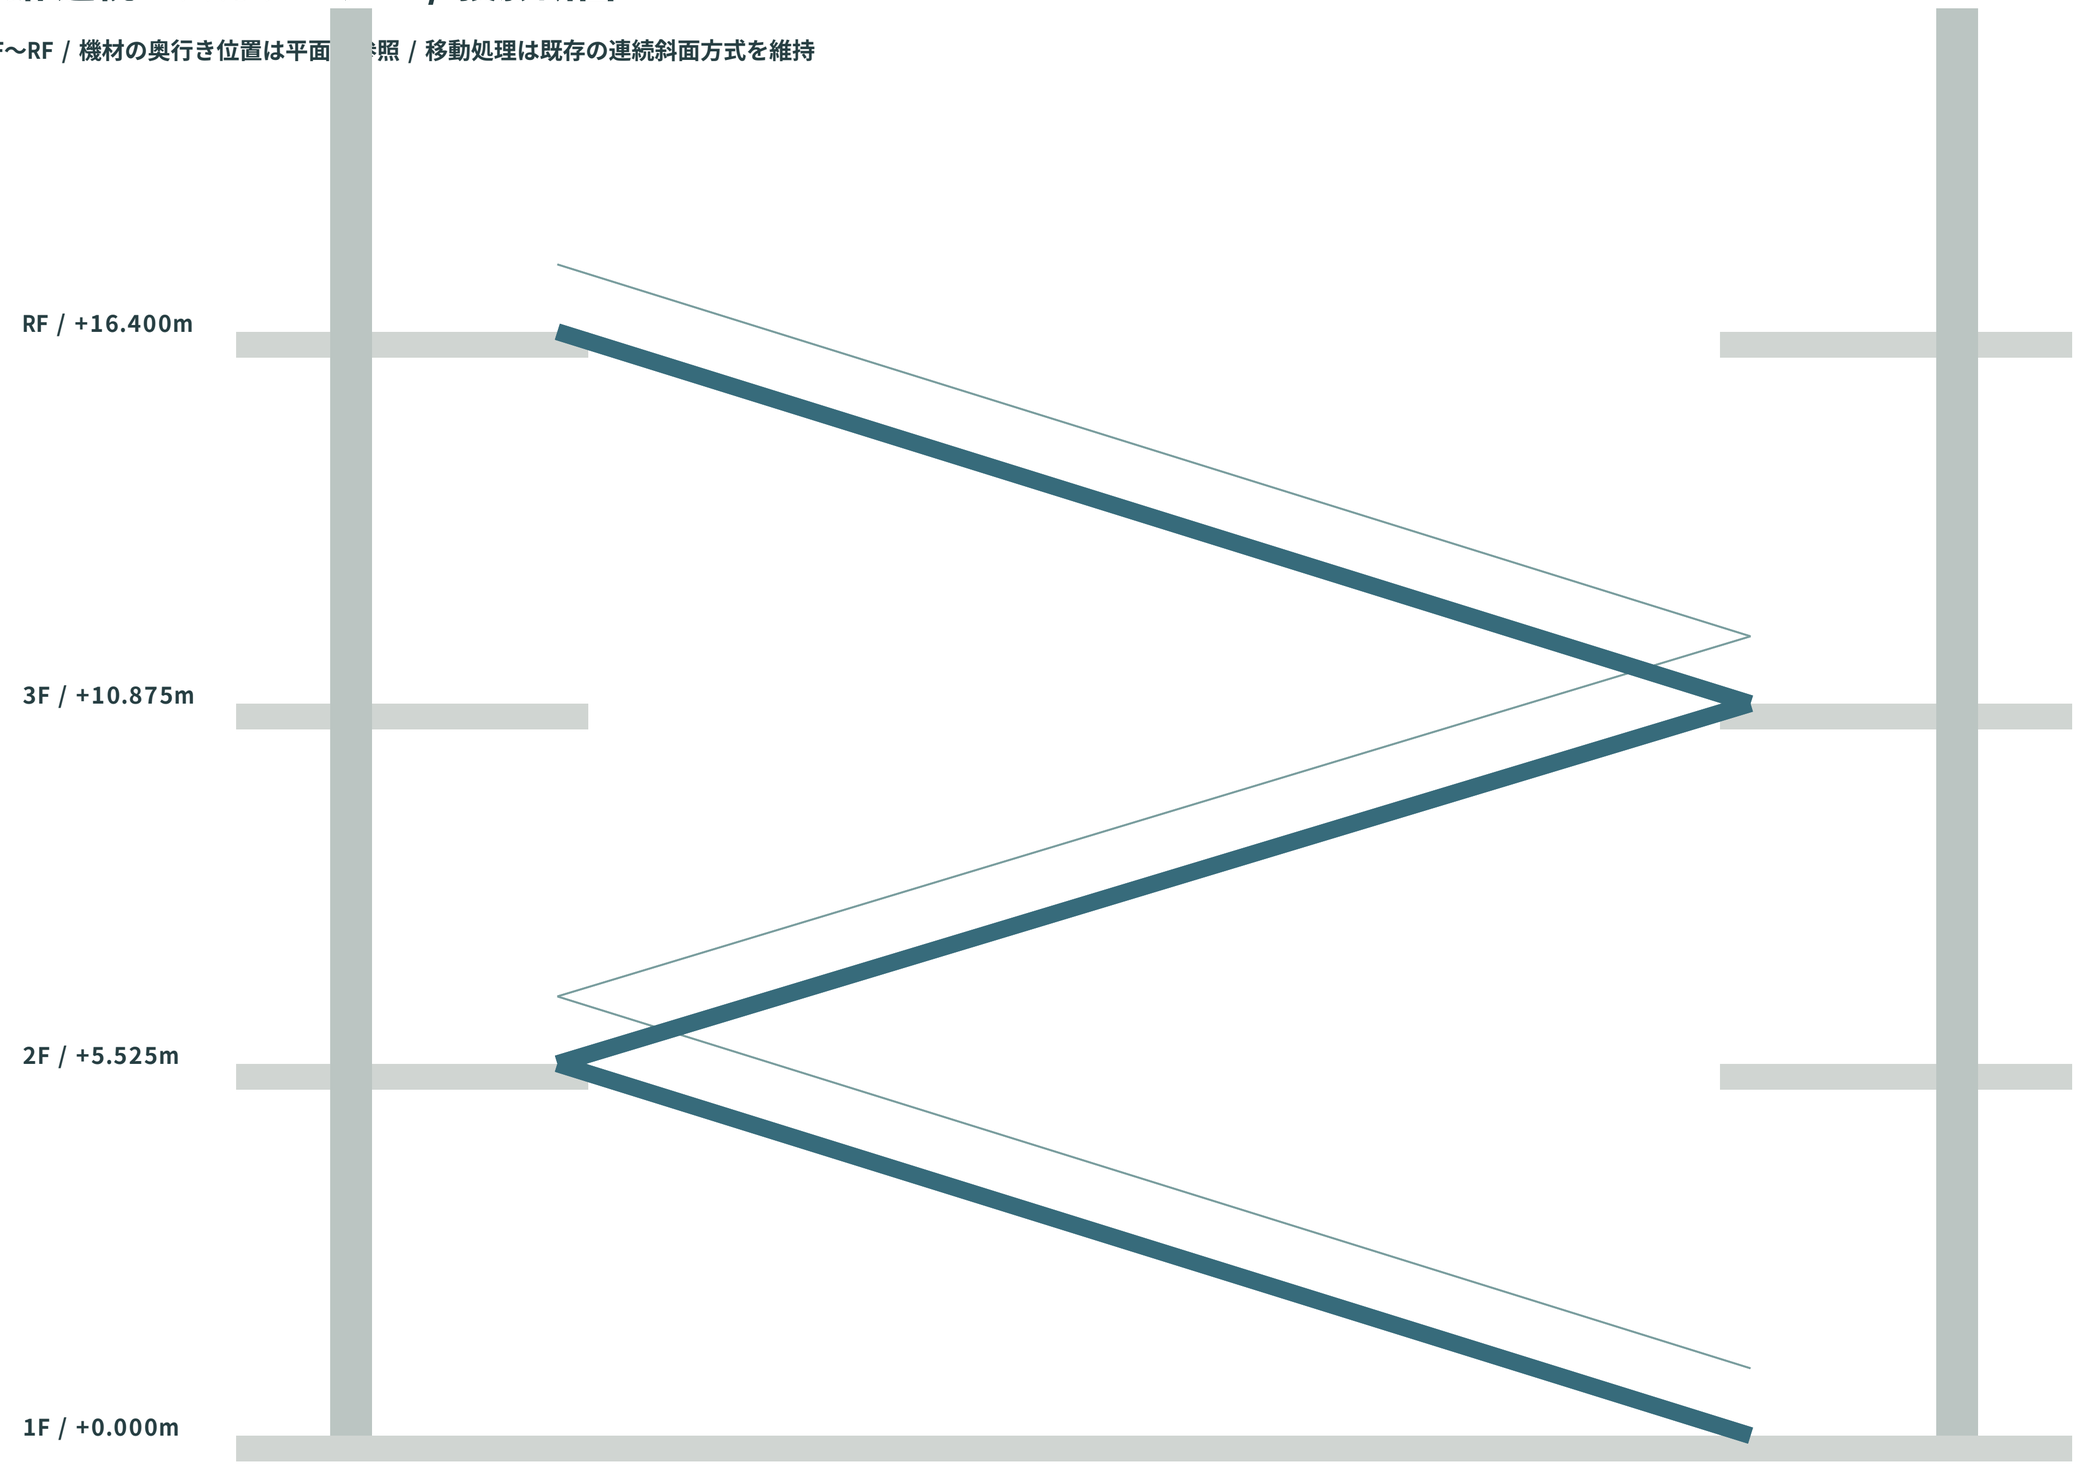


新設地下延伸なし。既存B1の車路・駐車区画は変更していません。

構造計算・基礎・荷重・避難の承認ではありません。RF-SUPPORT-16は未承認を維持。

B館 連続エスカレーター / 投影断面

1F〜RF / 機材の奥行き位置は平面図参照 / 移動処理は既存の連続斜面方式を維持

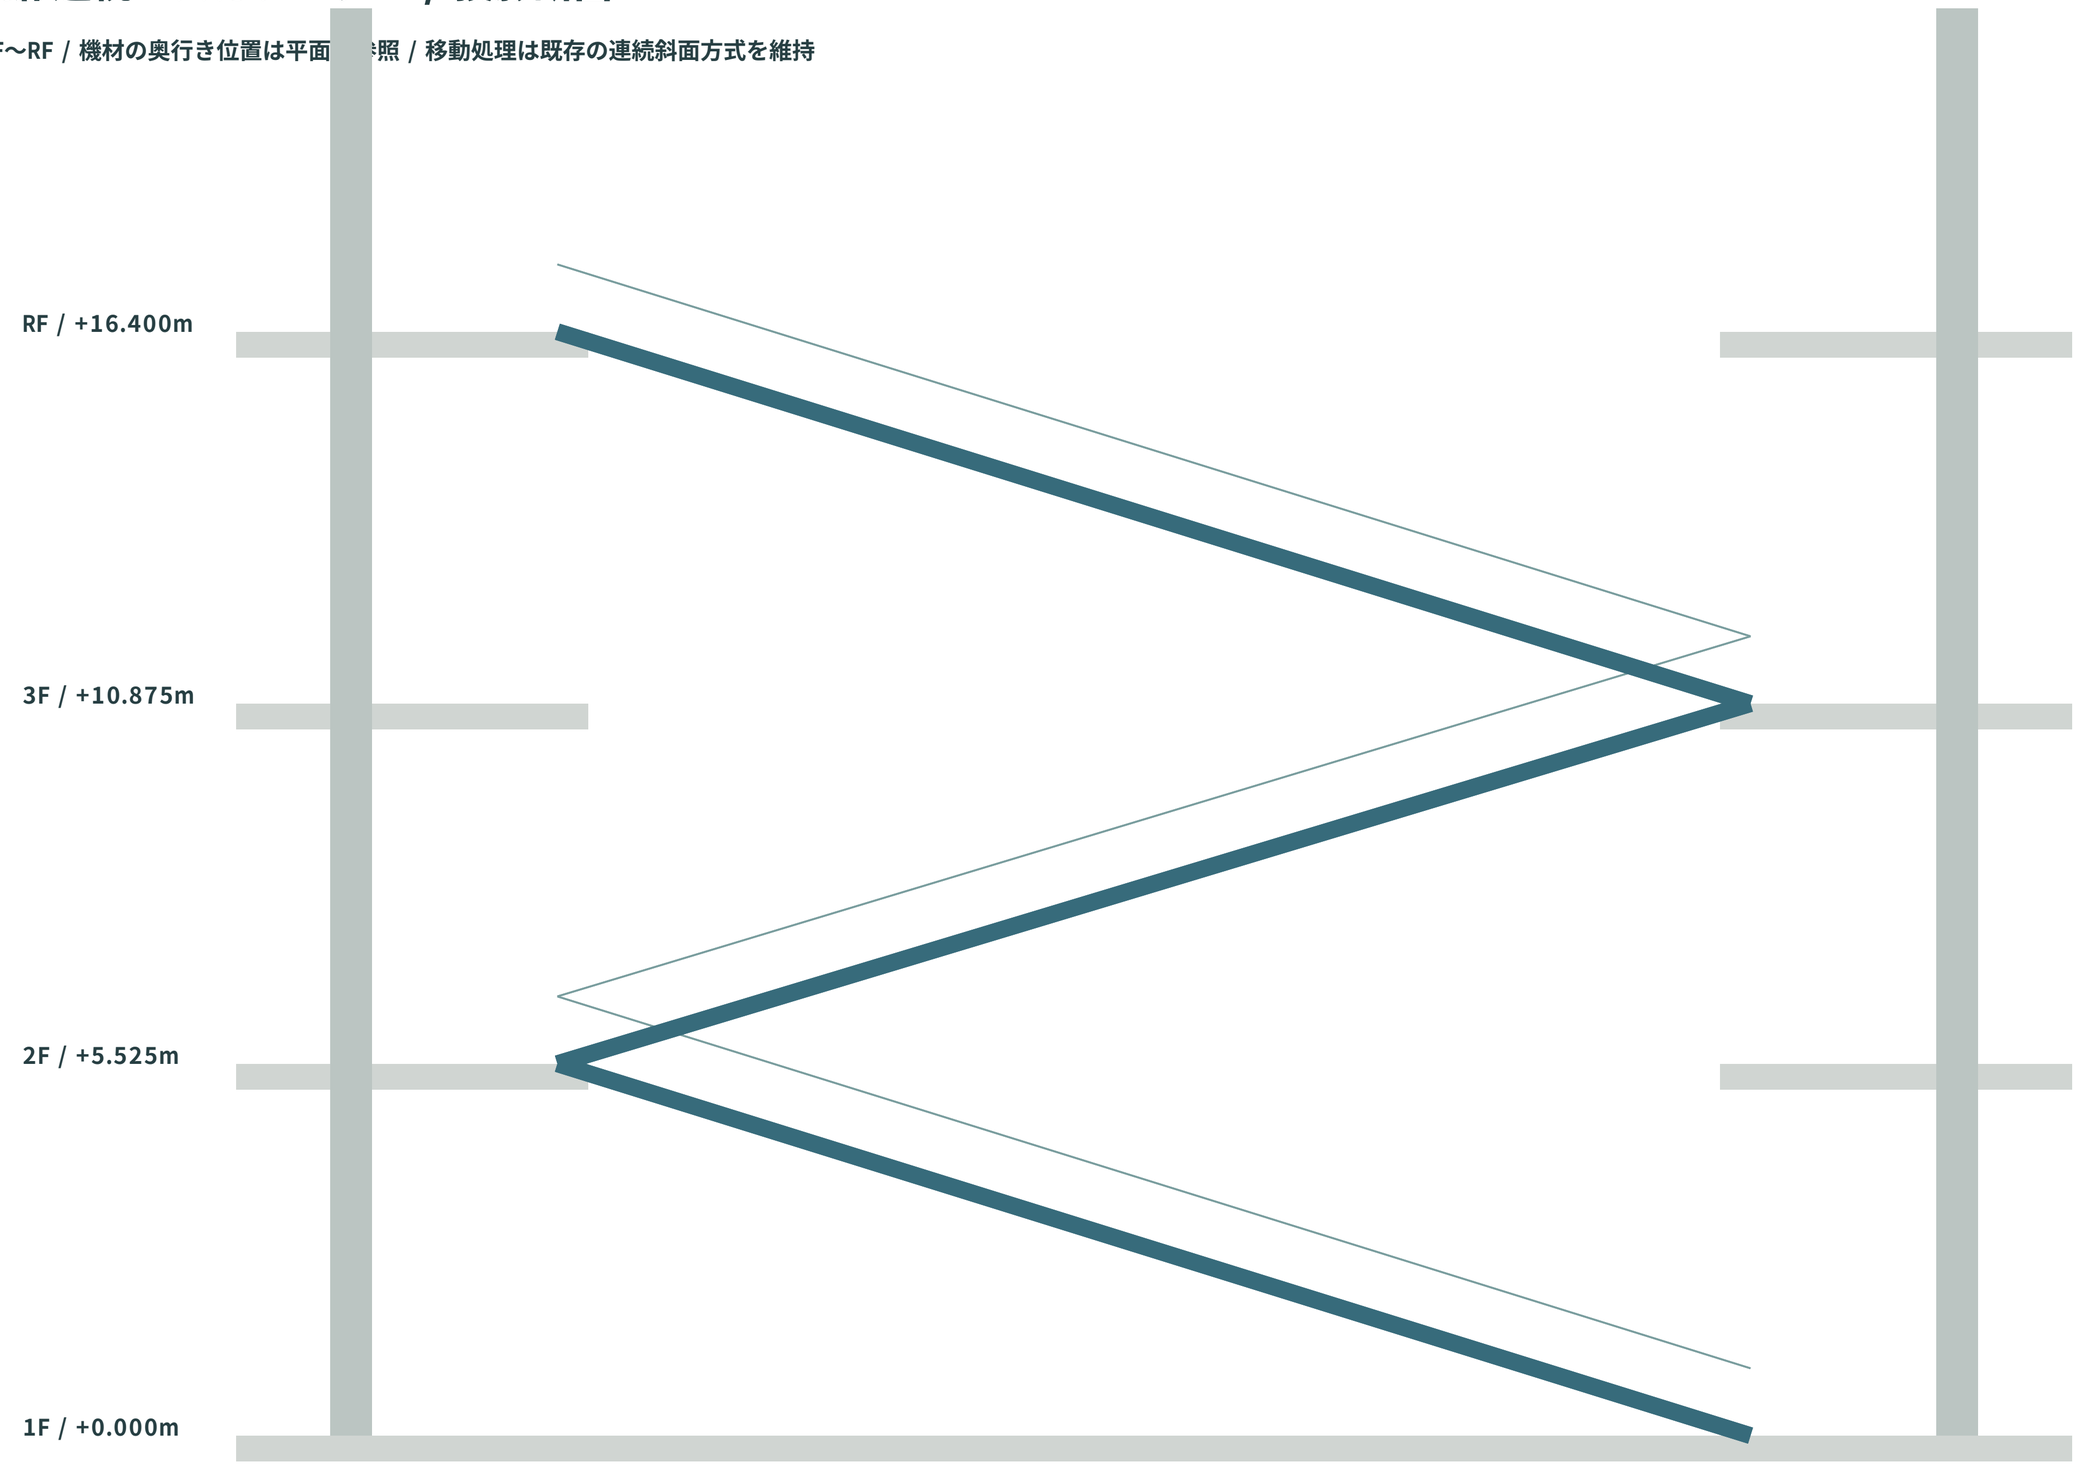

新設地下延伸なし。既存B1の車路・駐車区画は変更していません。

構造計算・基礎・荷重・避難の承認ではありません。RF-SUPPORT-16は未承認を維持。