B館 1F–3F 詳細設計レビュー：改訂3

承認対象はゲーム用の空間設計。実施設計・施工許可図ではありません。

対象：添付13ページPDF・区画JSON・店舗台帳・仮座標変換を独立検査し、図面データを改訂。

維持：屈曲する主軸、局所的な回遊路、3つの吹き抜け。旧SVGの楕円リングは採用しない。

修正：B1-068入口、歩行域と吹き抜け・設備の重複、エスカレーター軸、館間接続、設備内訳。

座標案：World X = Local X − 714、World Z = Local Z − 30。縮尺1:1・回転なし。

計画区画数：1F 70、2F 72、3F 62（各階に大型核2を含む）。

平面幾何検査：9,508件、失敗 0件。多くは区画間重複の組合せ検査。

実歩行・Godot衝突・NPC経路・宝箱・猫・ソナー・ファストトラベルは改修後の試験。今回は未実施。

図中の棚は通路を確保する内装計画帯。完成した商品モデル・店舗装飾ではない。

全店に裏の専用搬入回廊を通した計画ではない。搬入は店内主路を営業時間外に共用する。


構造柱・耐火区画・避難計画・梁と設備配管の確定は範囲外。実建築の適法性は保証しない。

確認してほしい点：通路の屈曲・店舗配置・吹き抜け規模・A/C接続案・搬入方式。

ゲームシーン／ロジック／保存済みワールド／配布ゲームは変更していない。承認後に段階施工。

B館 1F / 全体平面図

床高 +0.000m / 通常区画 68＋大型核 2 / Local XZ m / 茶＝専用バックルーム・灰＝共用設備・外壁サービス帯

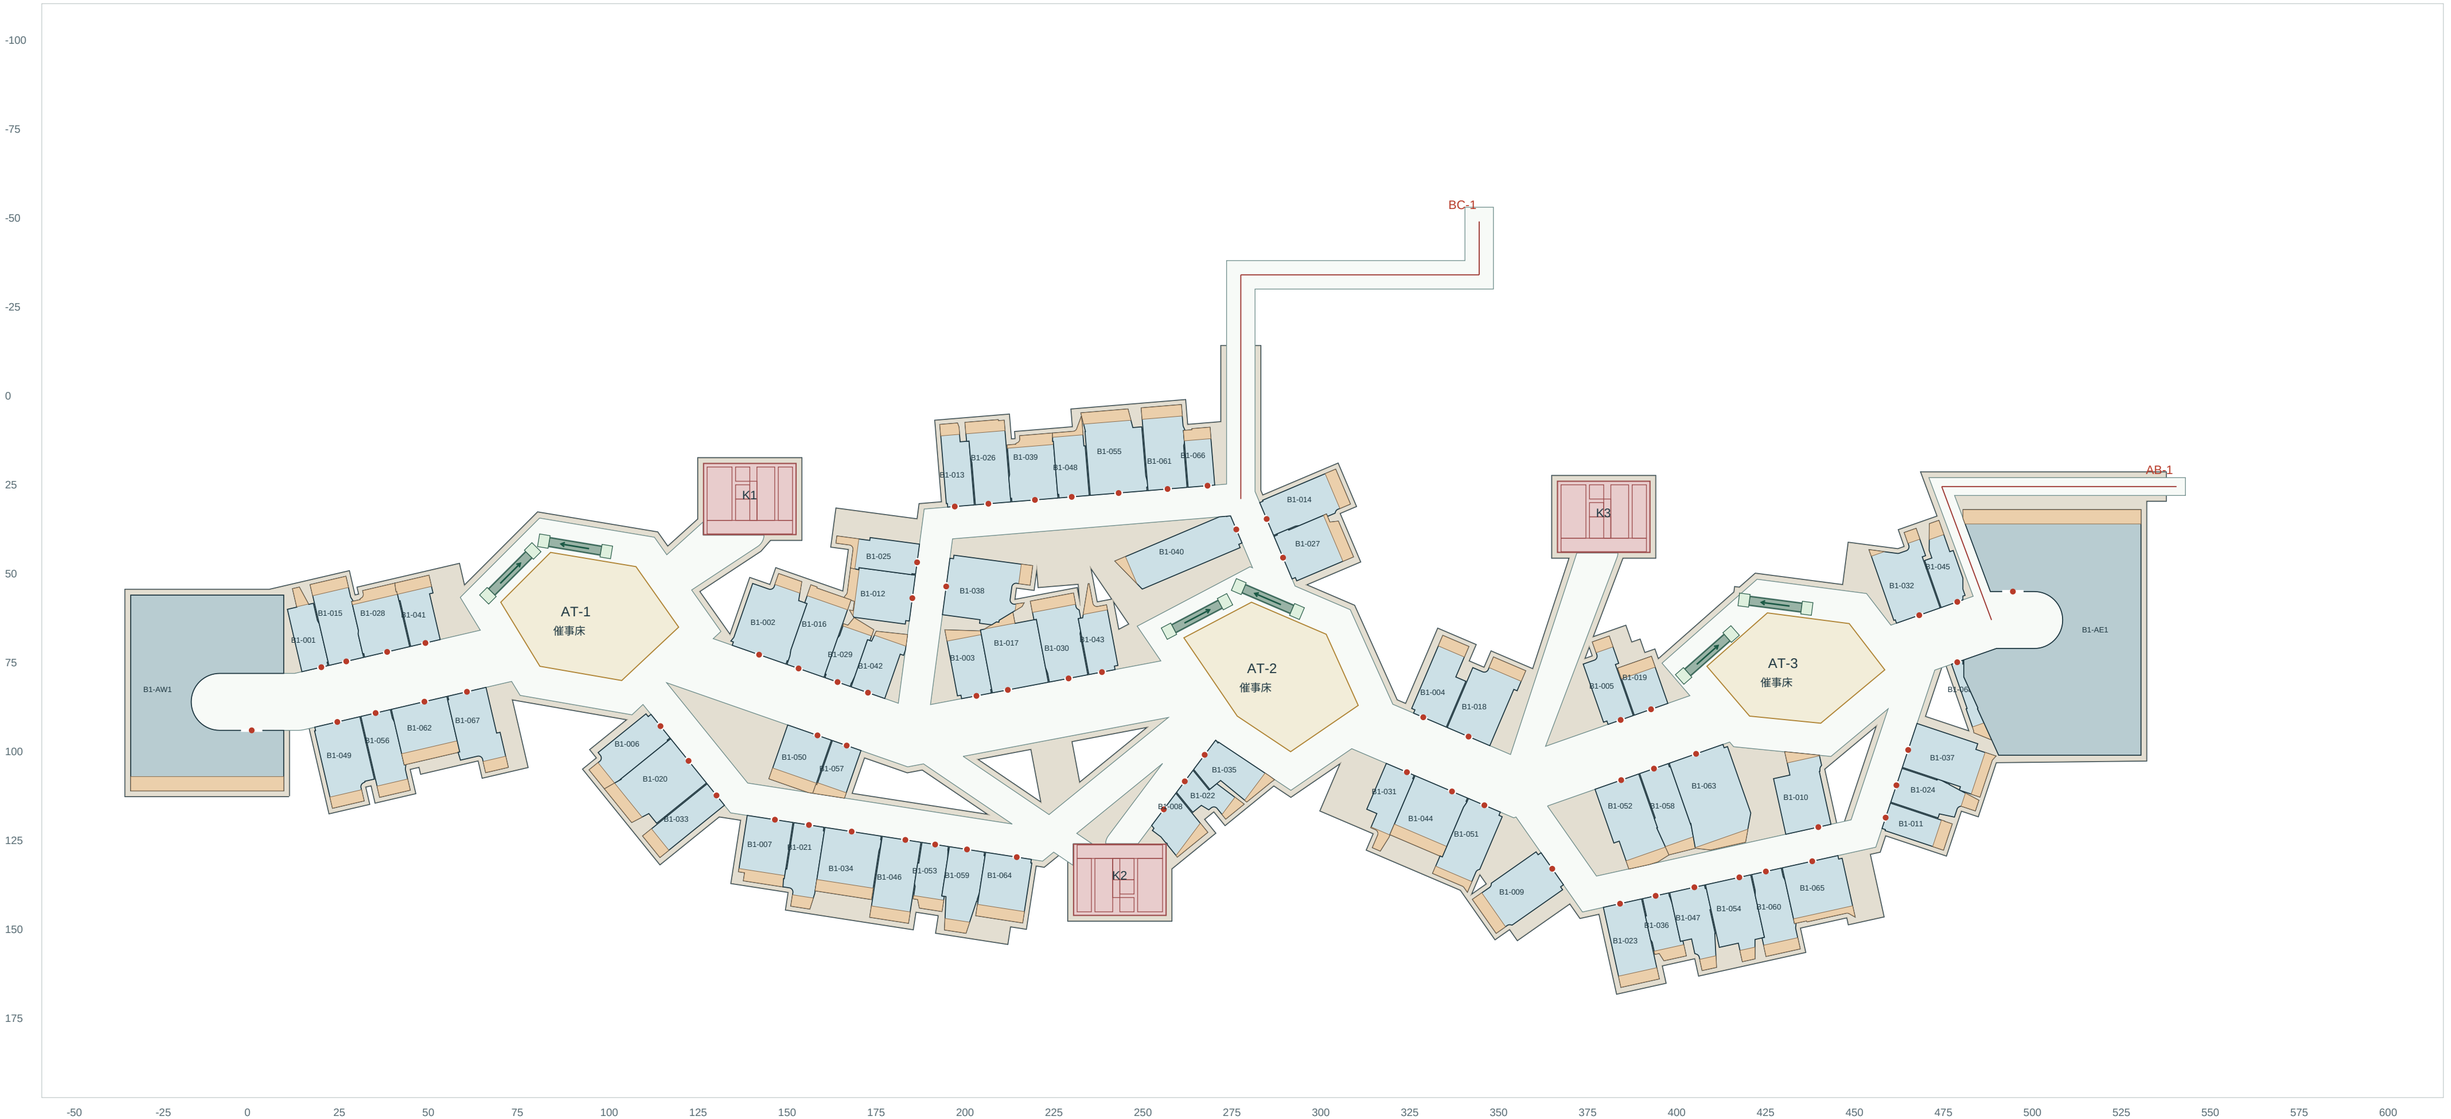


共用主軸16m・枝道9m・設備アクセス8m。赤点＝入口。入口幅は台帳参照。

上階の黄土色＝共通吹き抜け、緑＝昇降機と乗降床。断面・拡大図で方向と高さを確認。

灰色の余剰部分は非公開の設備・躯体帯。探索可能な空白としてNPCや宝箱を置かない。

B館 1F / 区画拡大 1


店舗ID・入口開口・売場主路/横断路・棚配置帯・専用バックルーム。実線壁厚0.25m。棚帯は内装計画。

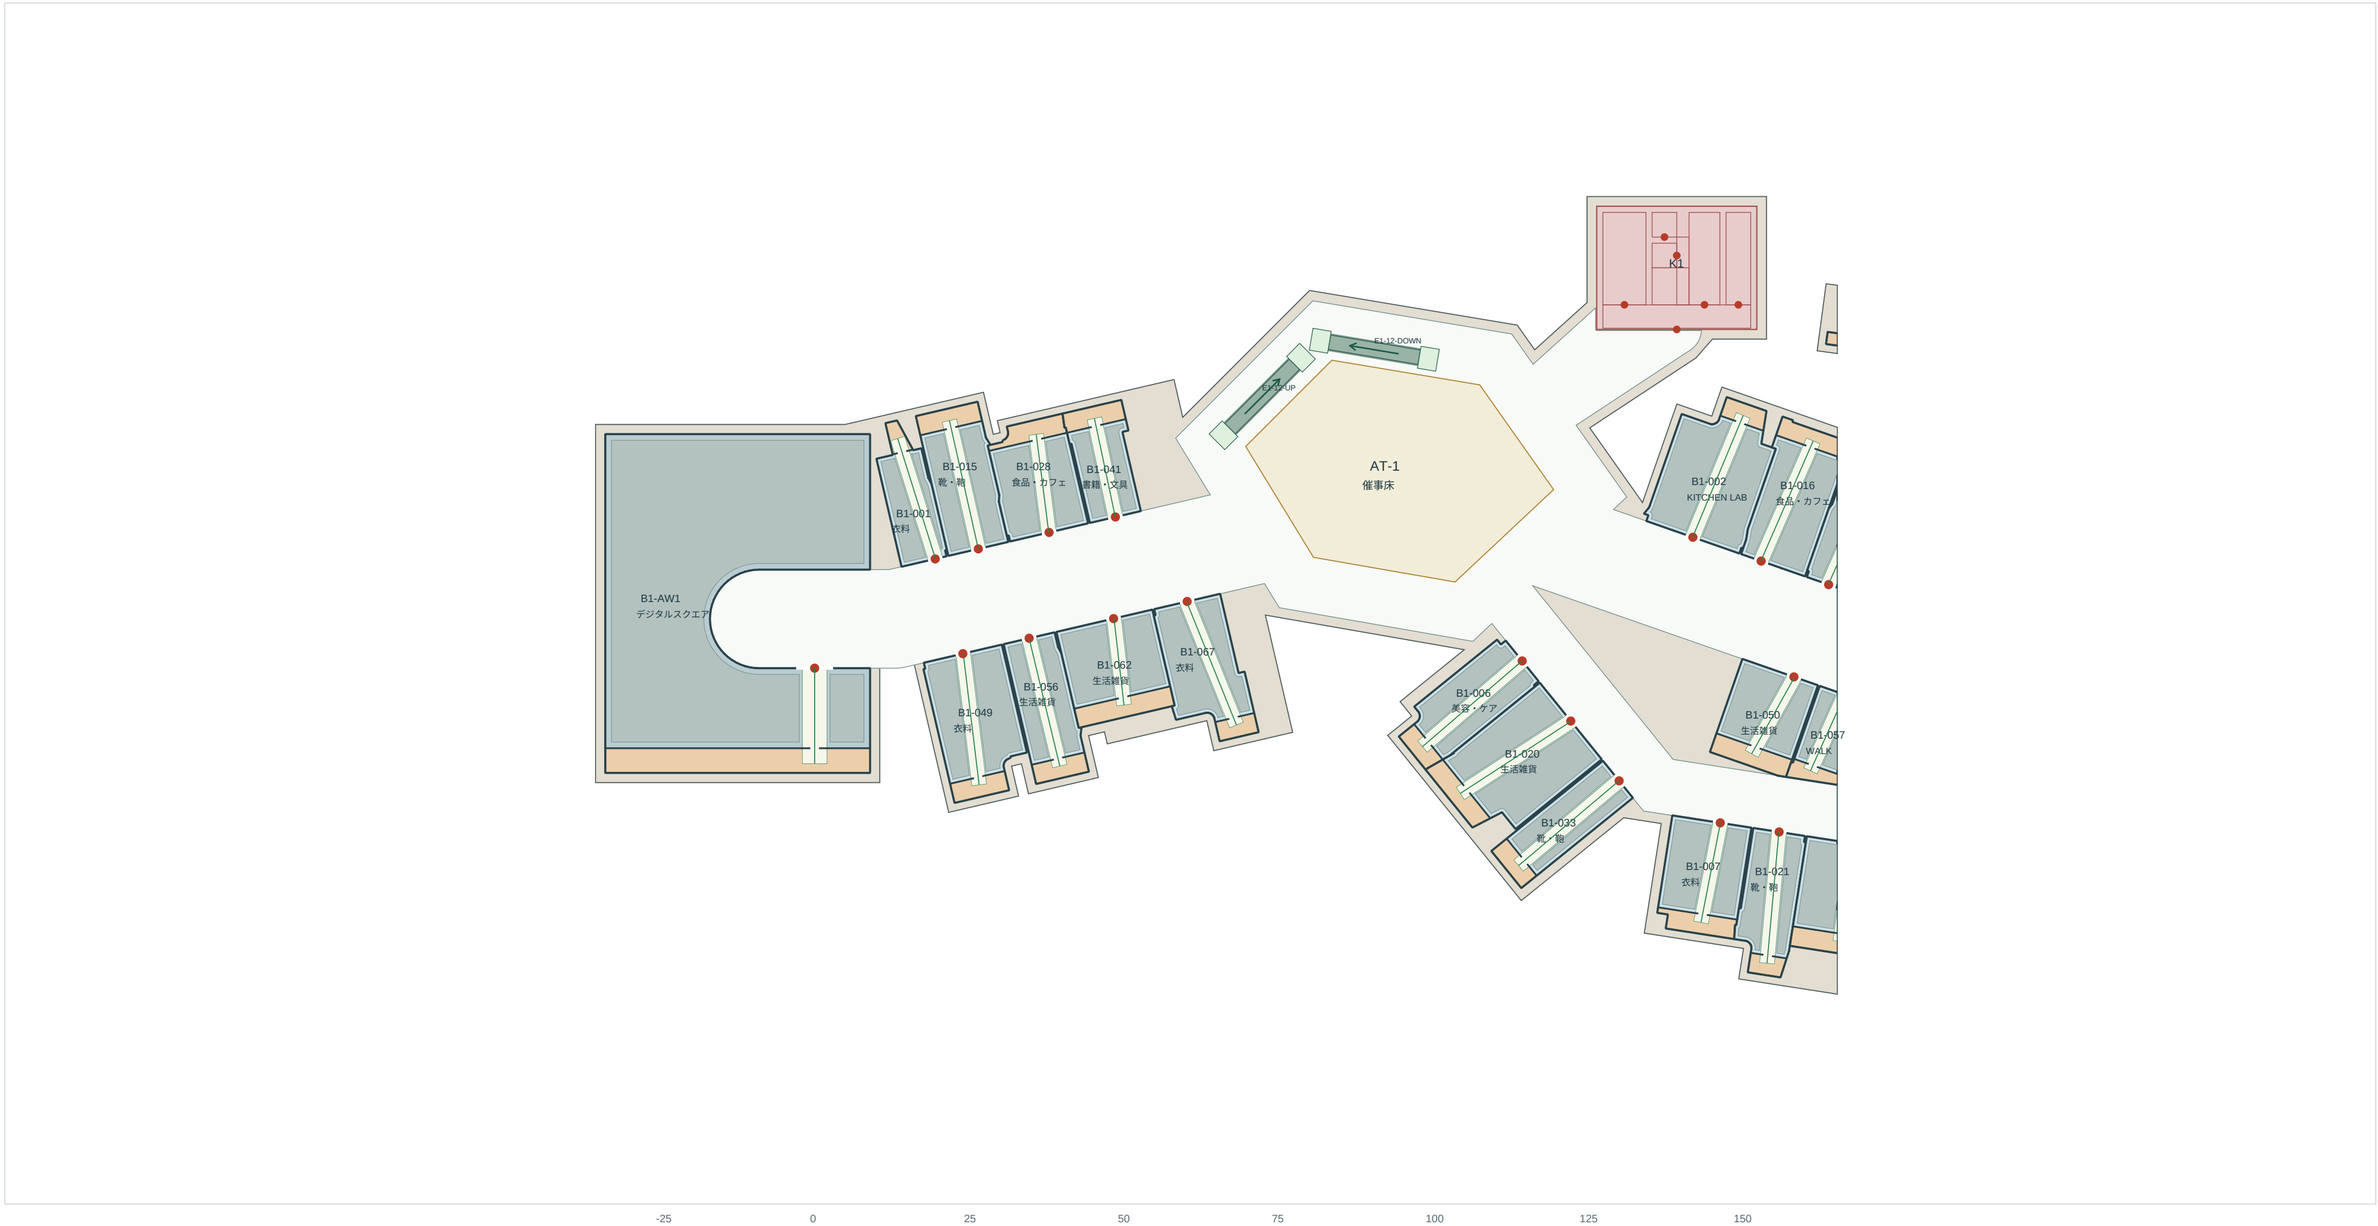

図示の局所座標と機械可読geometry.jsonは共通。入口は2.4m、大型核は6m（有効開口の詳細は改修時検証）。

B館 1F / 区画拡大 2


店舗ID・入口開口・売場主路/横断路・棚配置帯・専用バックルーム。実線壁厚0.25m。棚帯は内装計画。

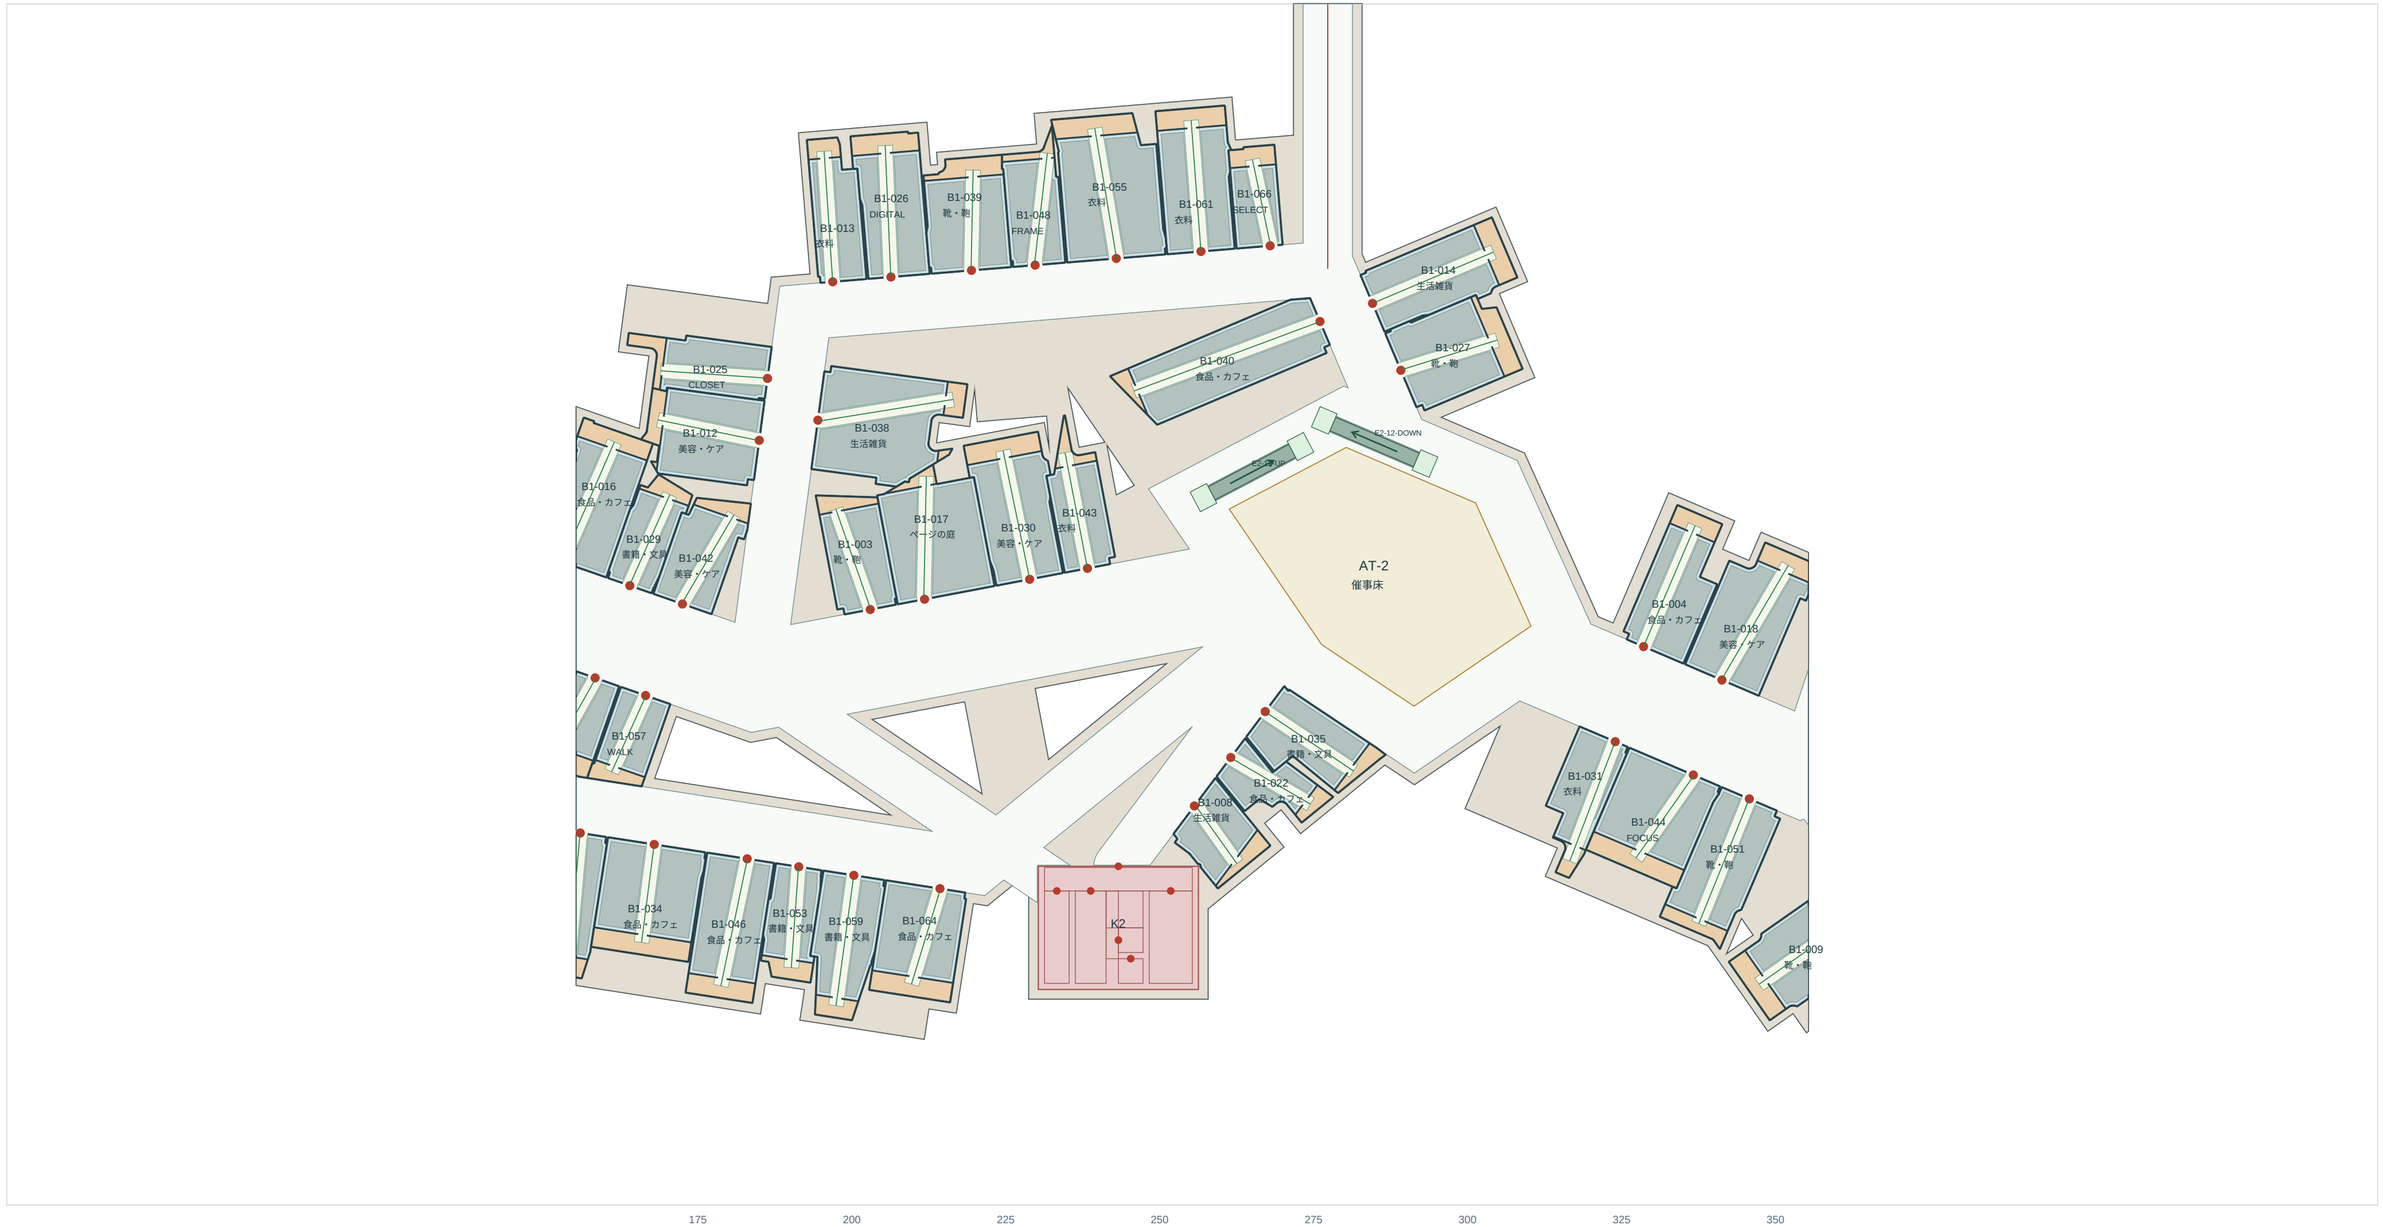

図示の局所座標と機械可読geometry.jsonは共通。入口は2.4m、大型核は6m（有効開口の詳細は改修時検証）。

B館 1F / 区画拡大 3


店舗ID・入口開口・売場主路/横断路・棚配置帯・専用バックルーム。実線壁厚0.25m。棚帯は内装計画。

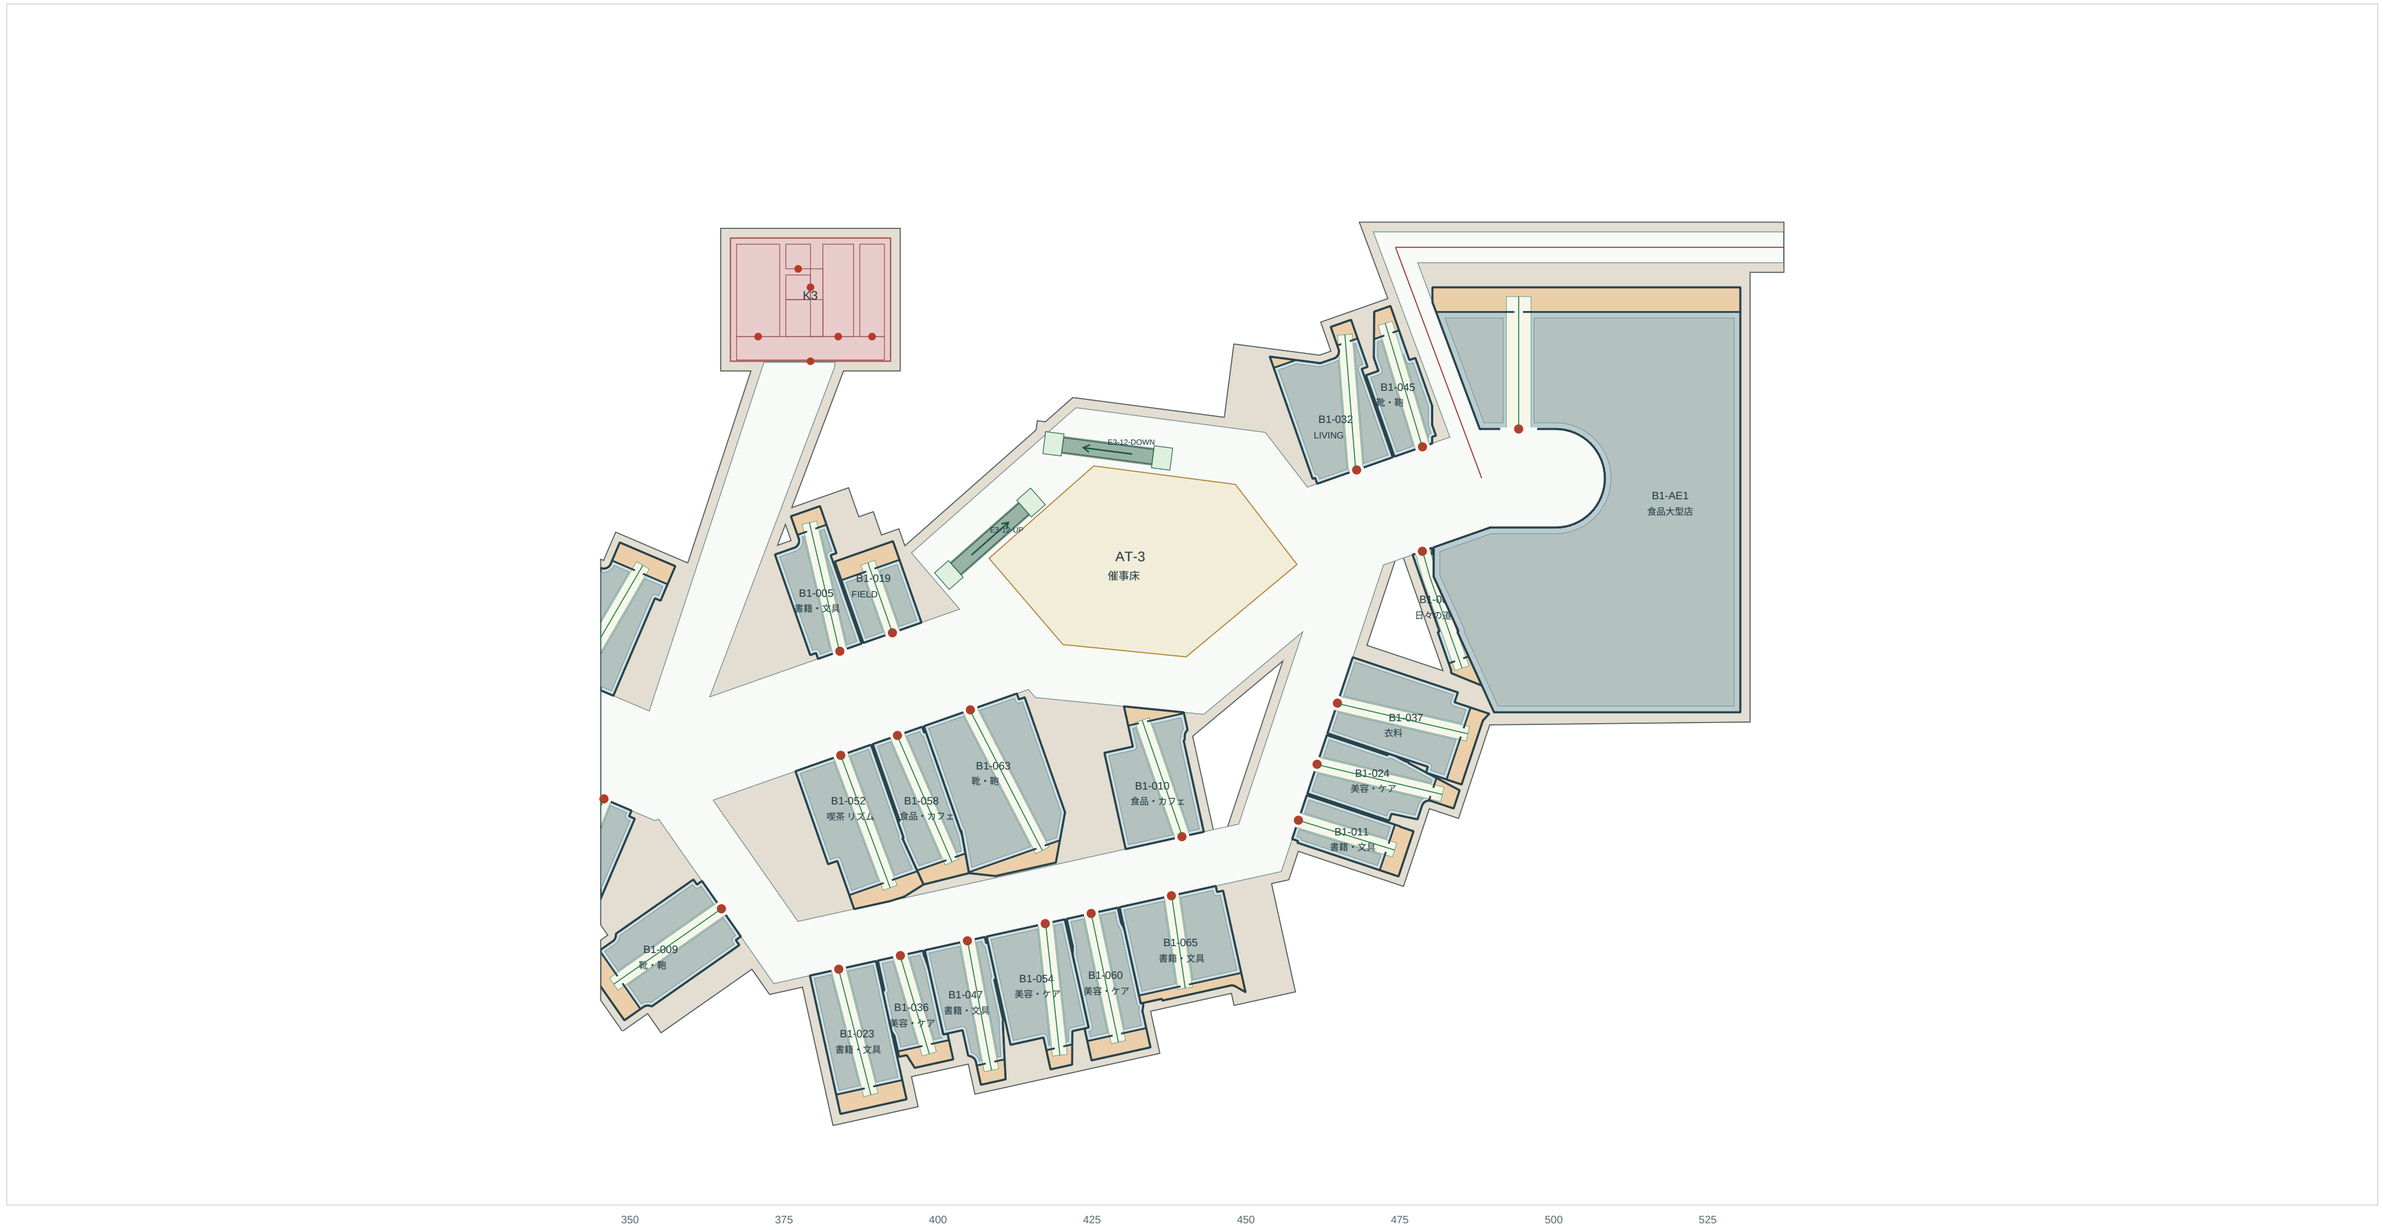

図示の局所座標と機械可読geometry.jsonは共通。入口は2.4m、大型核は6m（有効開口の詳細は改修時検証）。

B館 2F / 全体平面図

床高 +5.525m / 通常区画 70＋大型核 2 / Local XZ m / 茶＝専用バックルーム・灰＝共用設備・外壁サービス帯

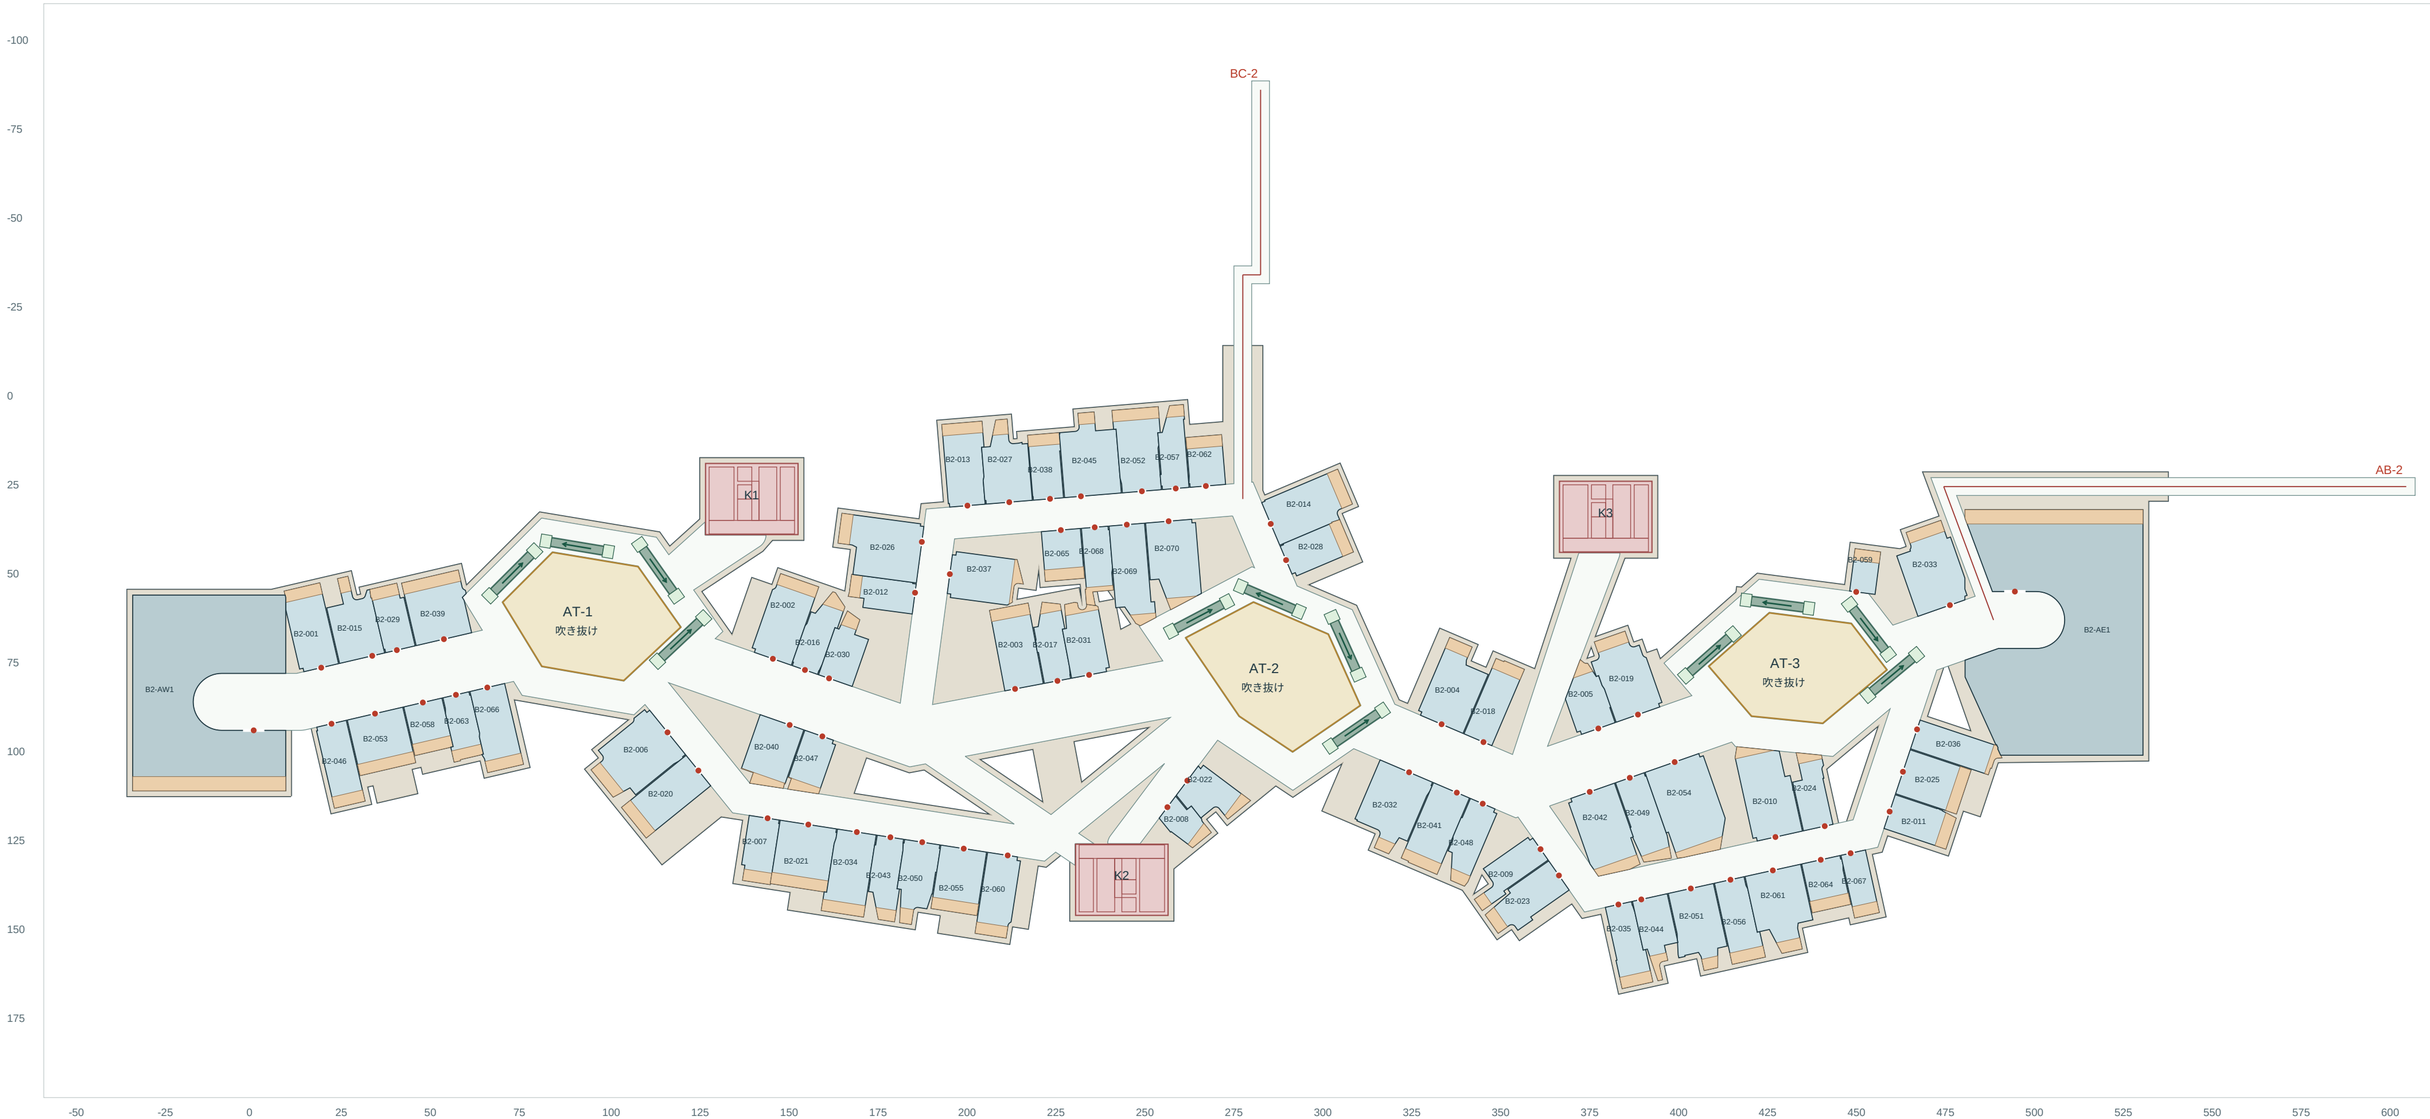


共用主軸16m・枝道9m・設備アクセス8m。赤点＝入口。入口幅は台帳参照。

上階の黄土色＝共通吹き抜け、緑＝昇降機と乗降床。断面・拡大図で方向と高さを確認。

灰色の余剰部分は非公開の設備・躯体帯。探索可能な空白としてNPCや宝箱を置かない。

B館 2F / 区画拡大 1


店舗ID・入口開口・売場主路/横断路・棚配置帯・専用バックルーム。実線壁厚0.25m。棚帯は内装計画。

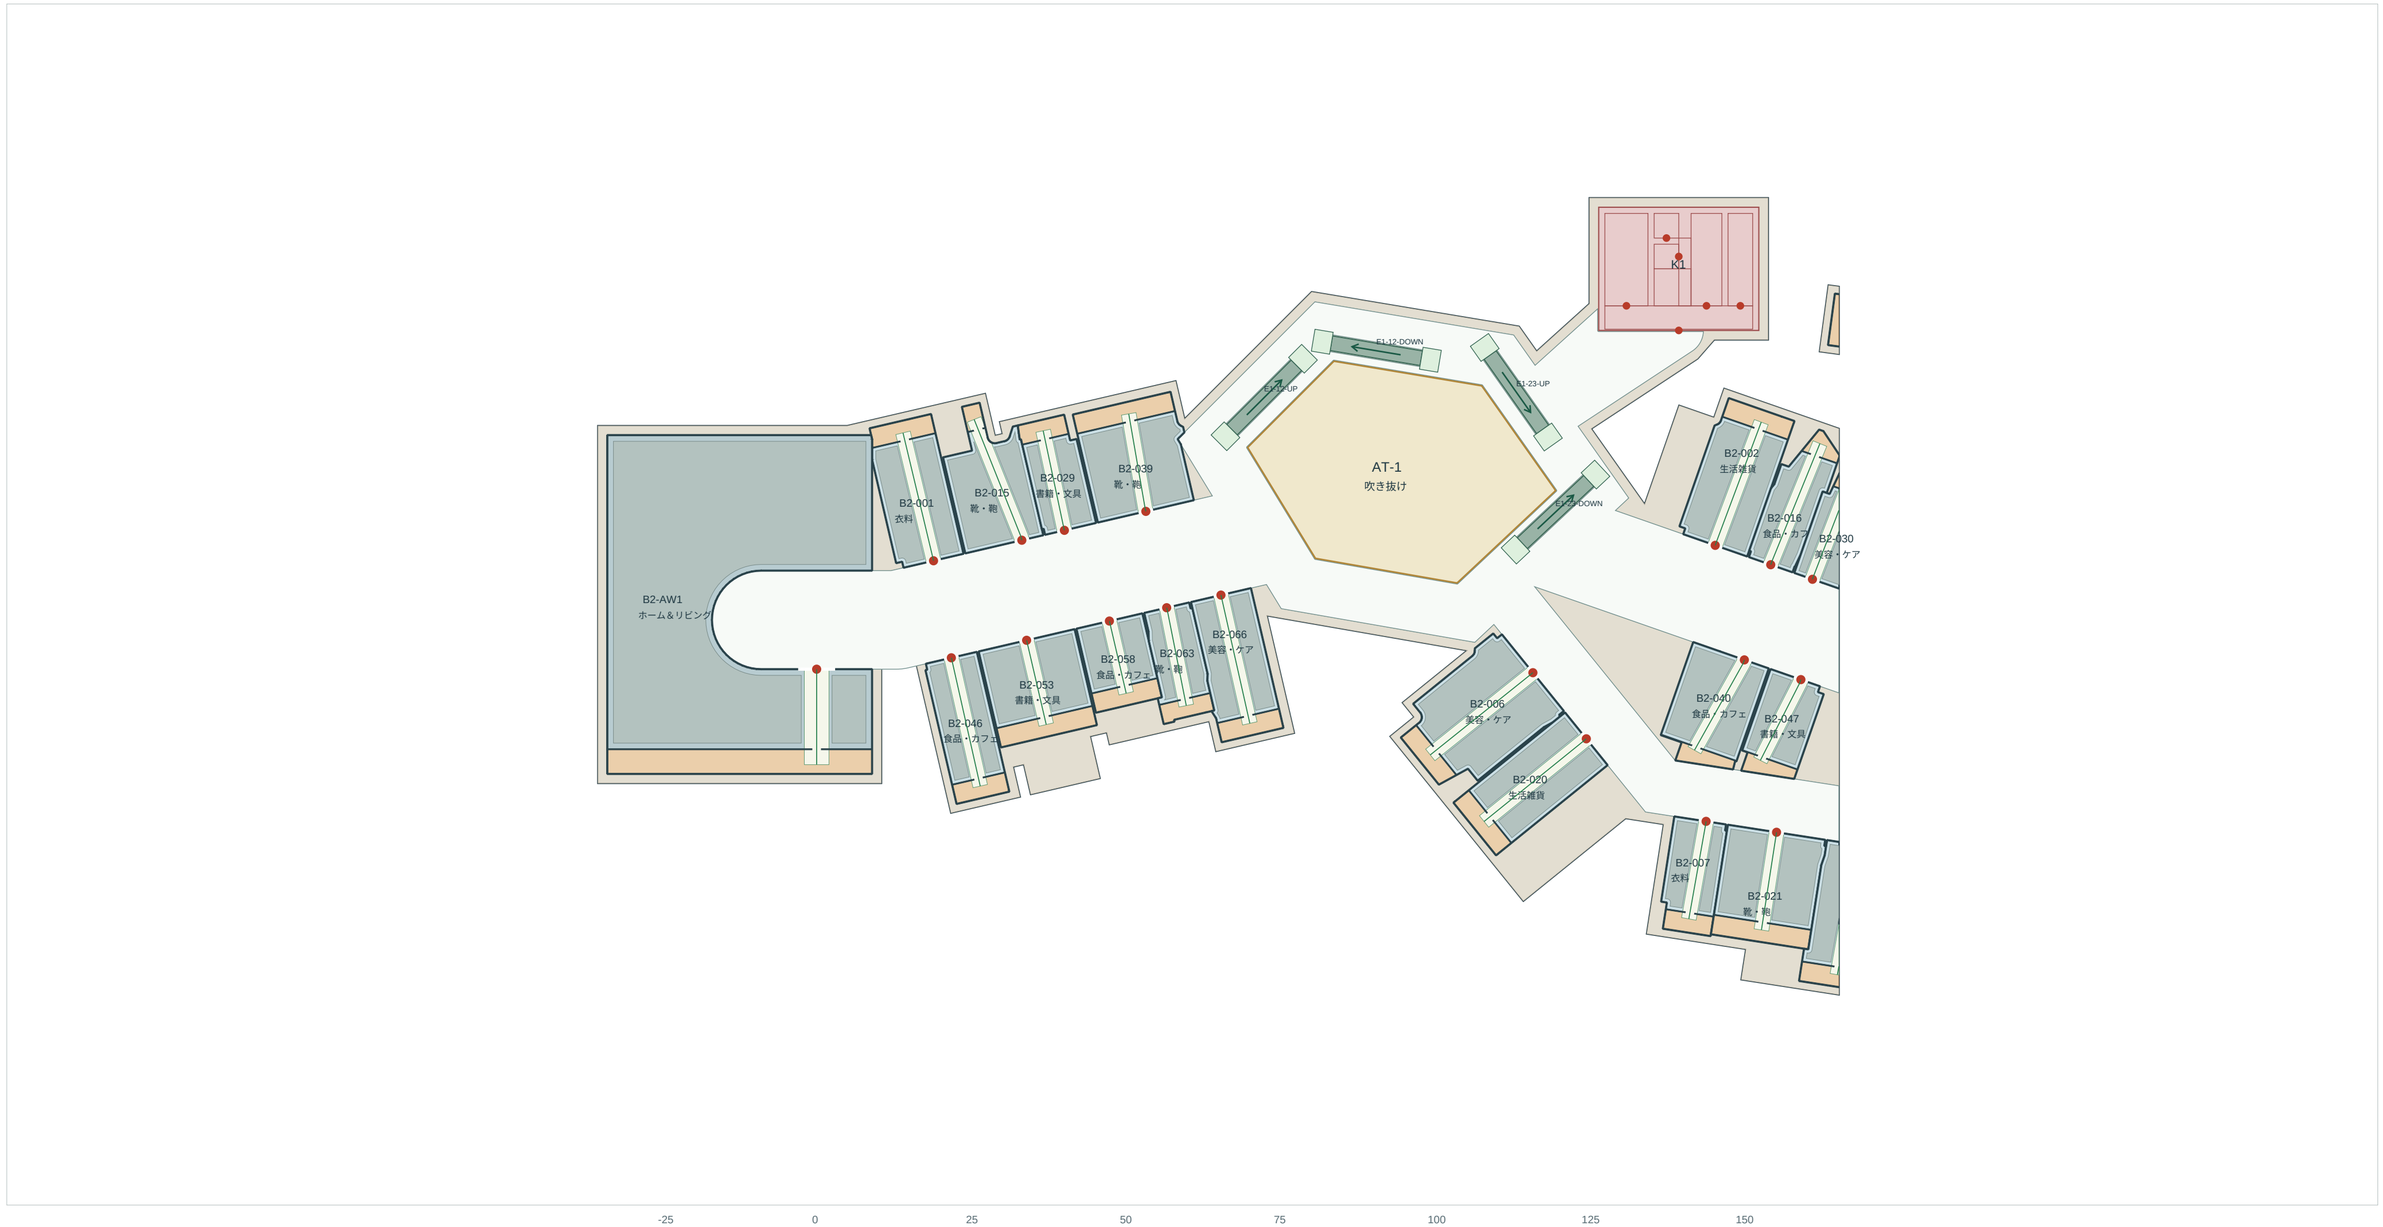

図示の局所座標と機械可読geometry.jsonは共通。入口は2.4m、大型核は6m（有効開口の詳細は改修時検証）。

B館 2F / 区画拡大 2


店舗ID・入口開口・売場主路/横断路・棚配置帯・専用バックルーム。実線壁厚0.25m。棚帯は内装計画。

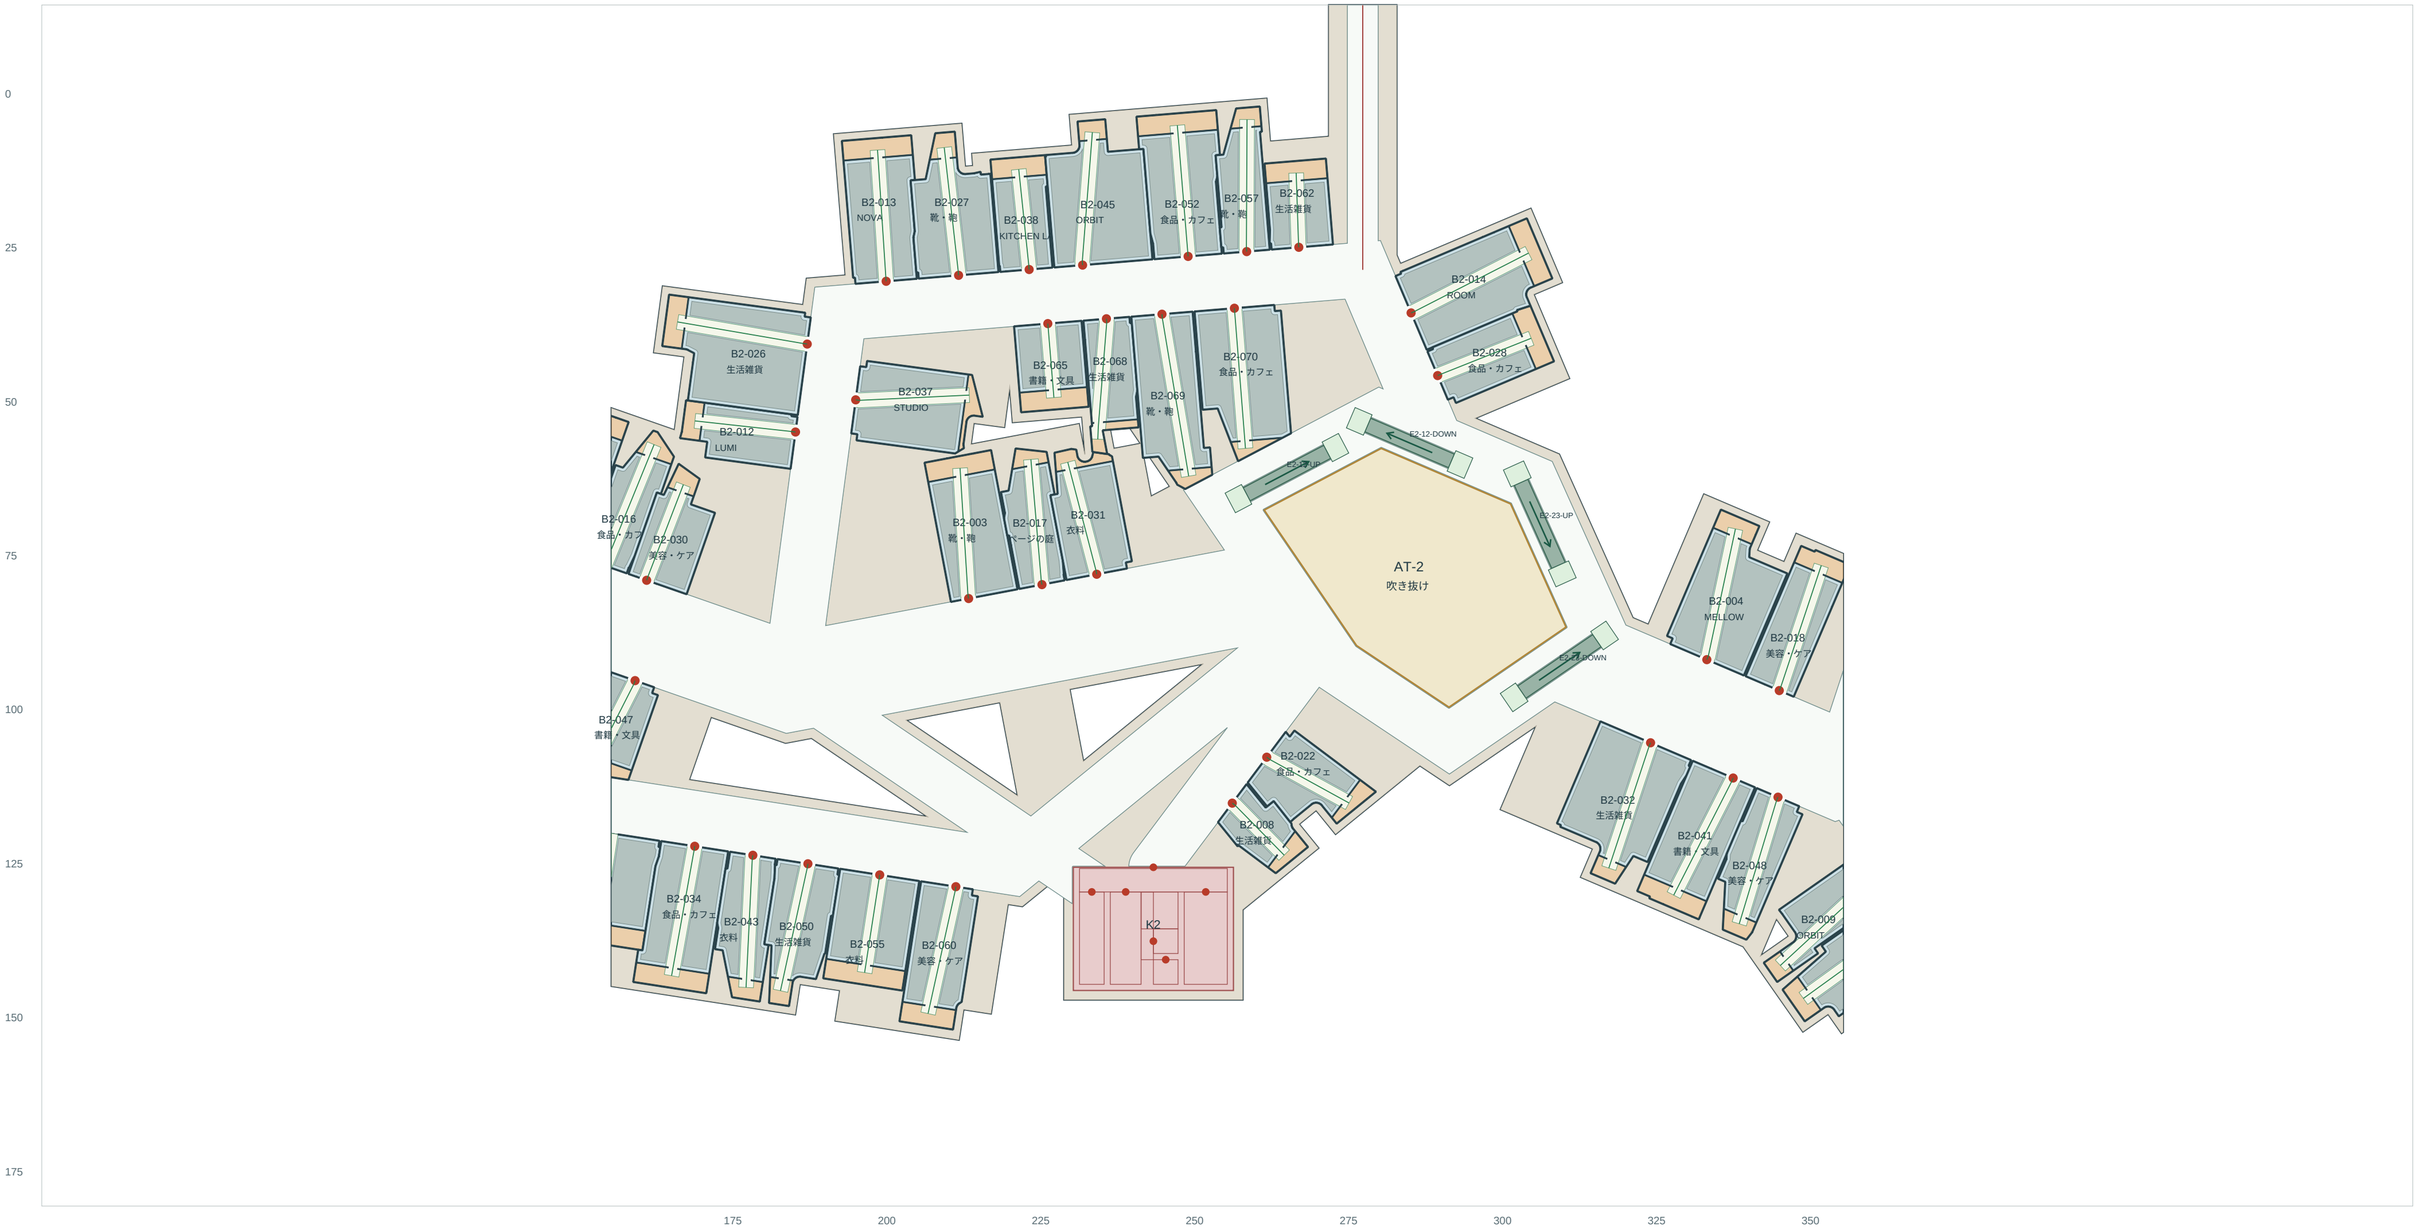

図示の局所座標と機械可読geometry.jsonは共通。入口は2.4m、大型核は6m（有効開口の詳細は改修時検証）。

B館 2F / 区画拡大 3

店舗ID・入口開口・売場主路/横断路・棚配置帯・専用バックルーム。実線壁厚0.25m。棚帯は内装計画。

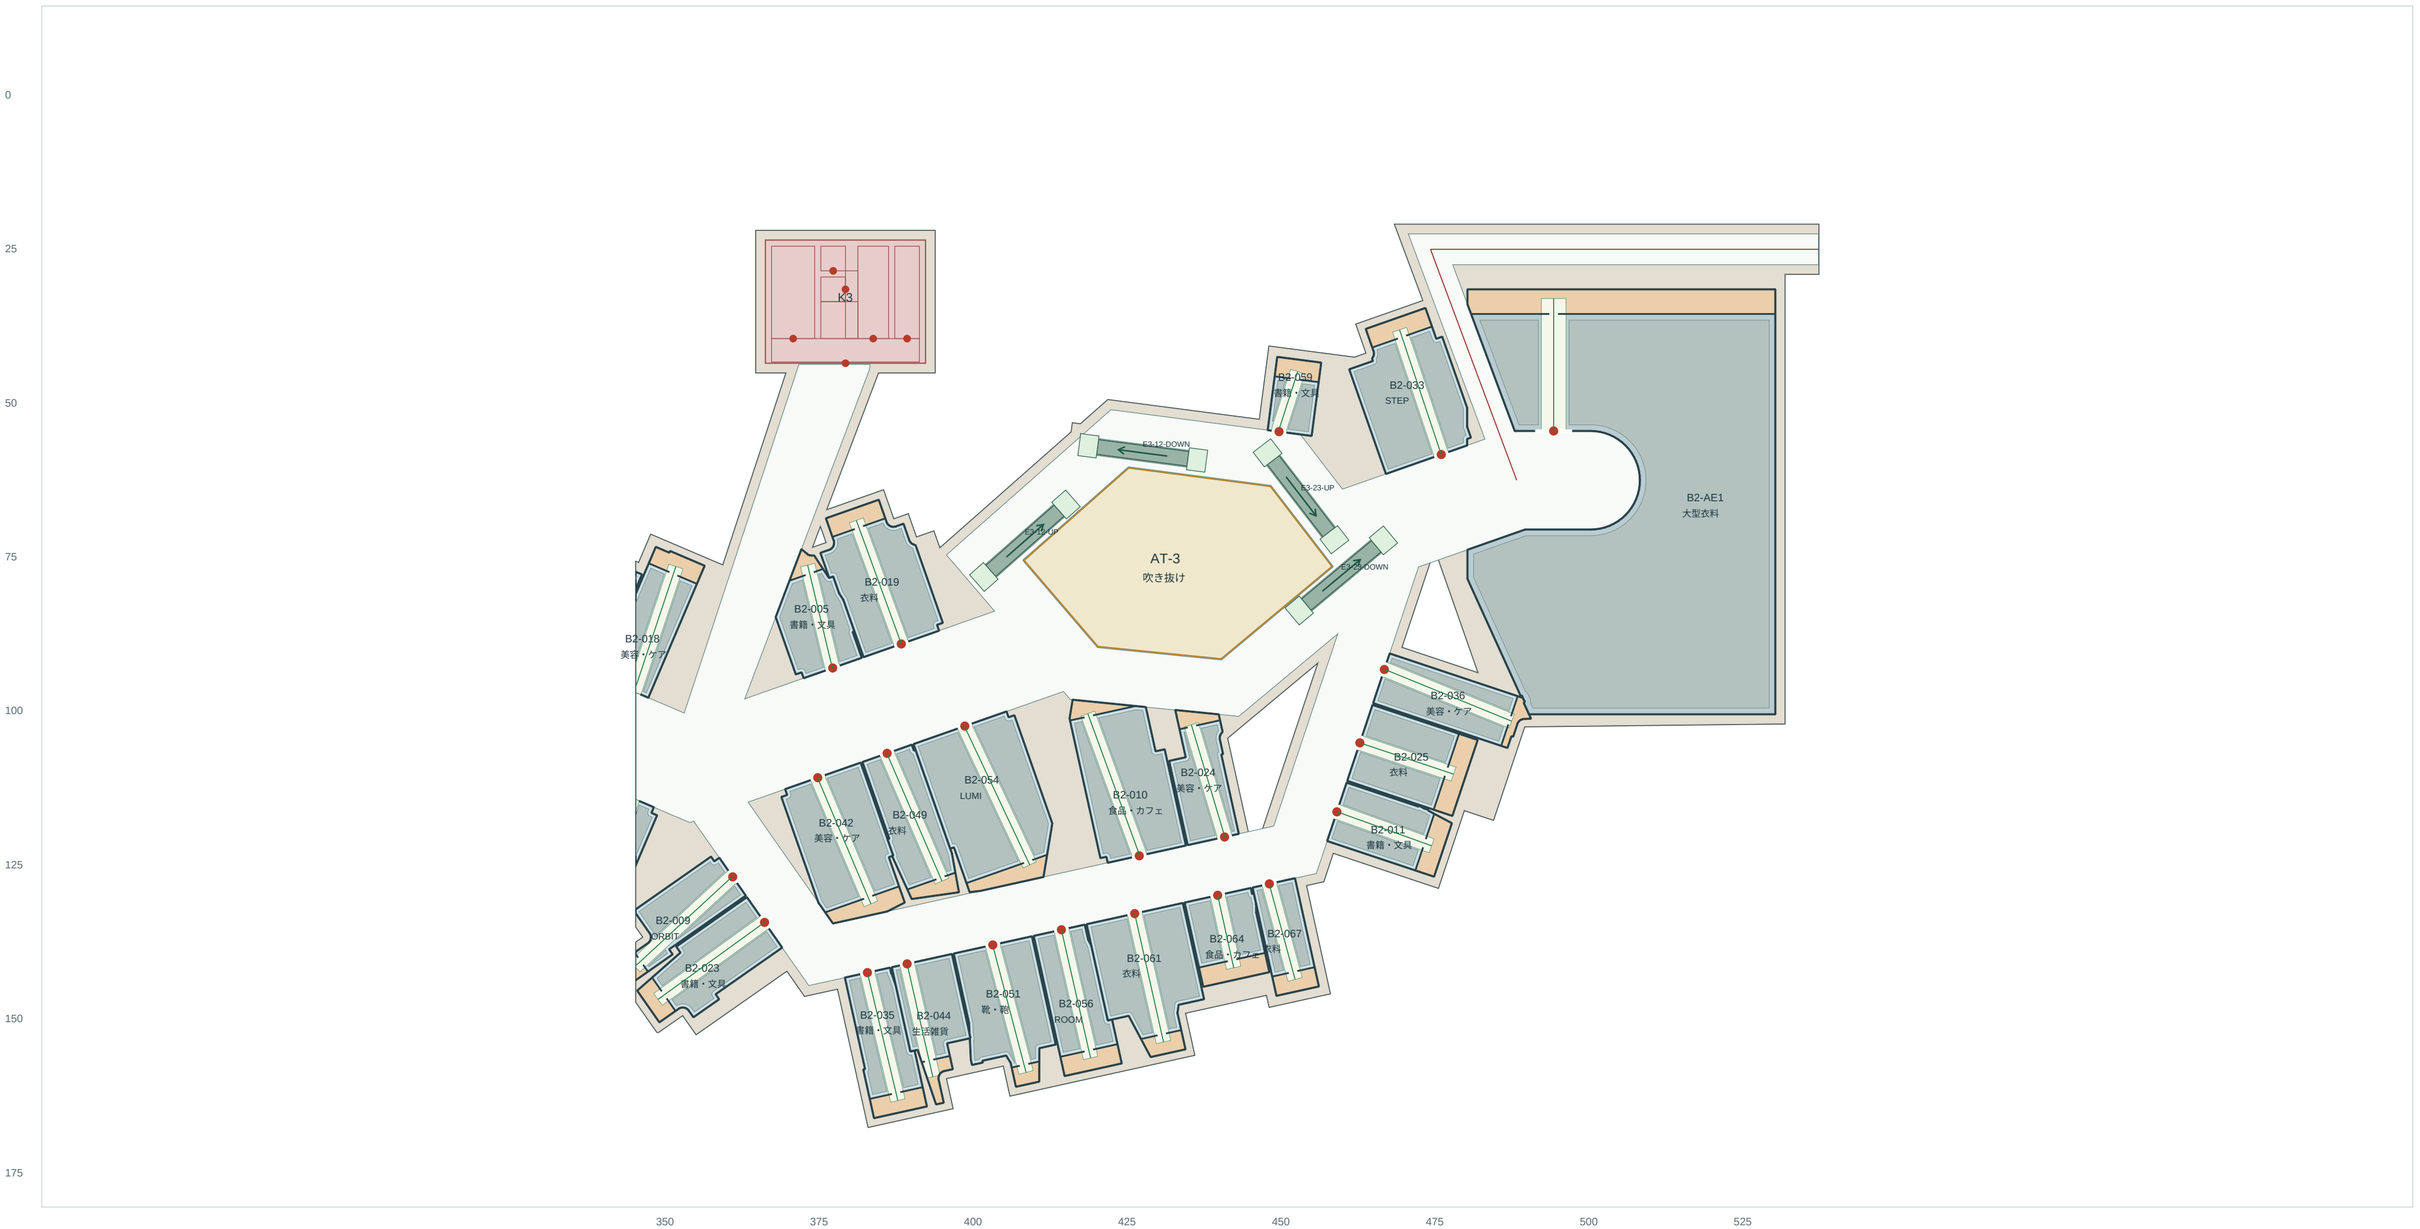

図示の局所座標と機械可読geometry.jsonは共通。入口は2.4m、大型核は6m（有効開口の詳細は改修時検証）。

B館 3F / 全体平面図

床高 +10.875m / 通常区画 60＋大型核 2 / Local XZ m / 茶＝専用バックルーム・灰＝共用設備・外壁サービス帯




共用主軸16m・枝道9m・設備アクセス8m。赤点＝入口。入口幅は台帳参照。

上階の黄土色＝共通吹き抜け、緑＝昇降機と乗降床。断面・拡大図で方向と高さを確認。

灰色の余剰部分は非公開の設備・躯体帯。探索可能な空白としてNPCや宝箱を置かない。

B館 3F / 区画拡大 1


店舗ID・入口開口・売場主路/横断路・棚配置帯・専用バックルーム。実線壁厚0.25m。棚帯は内装計画。

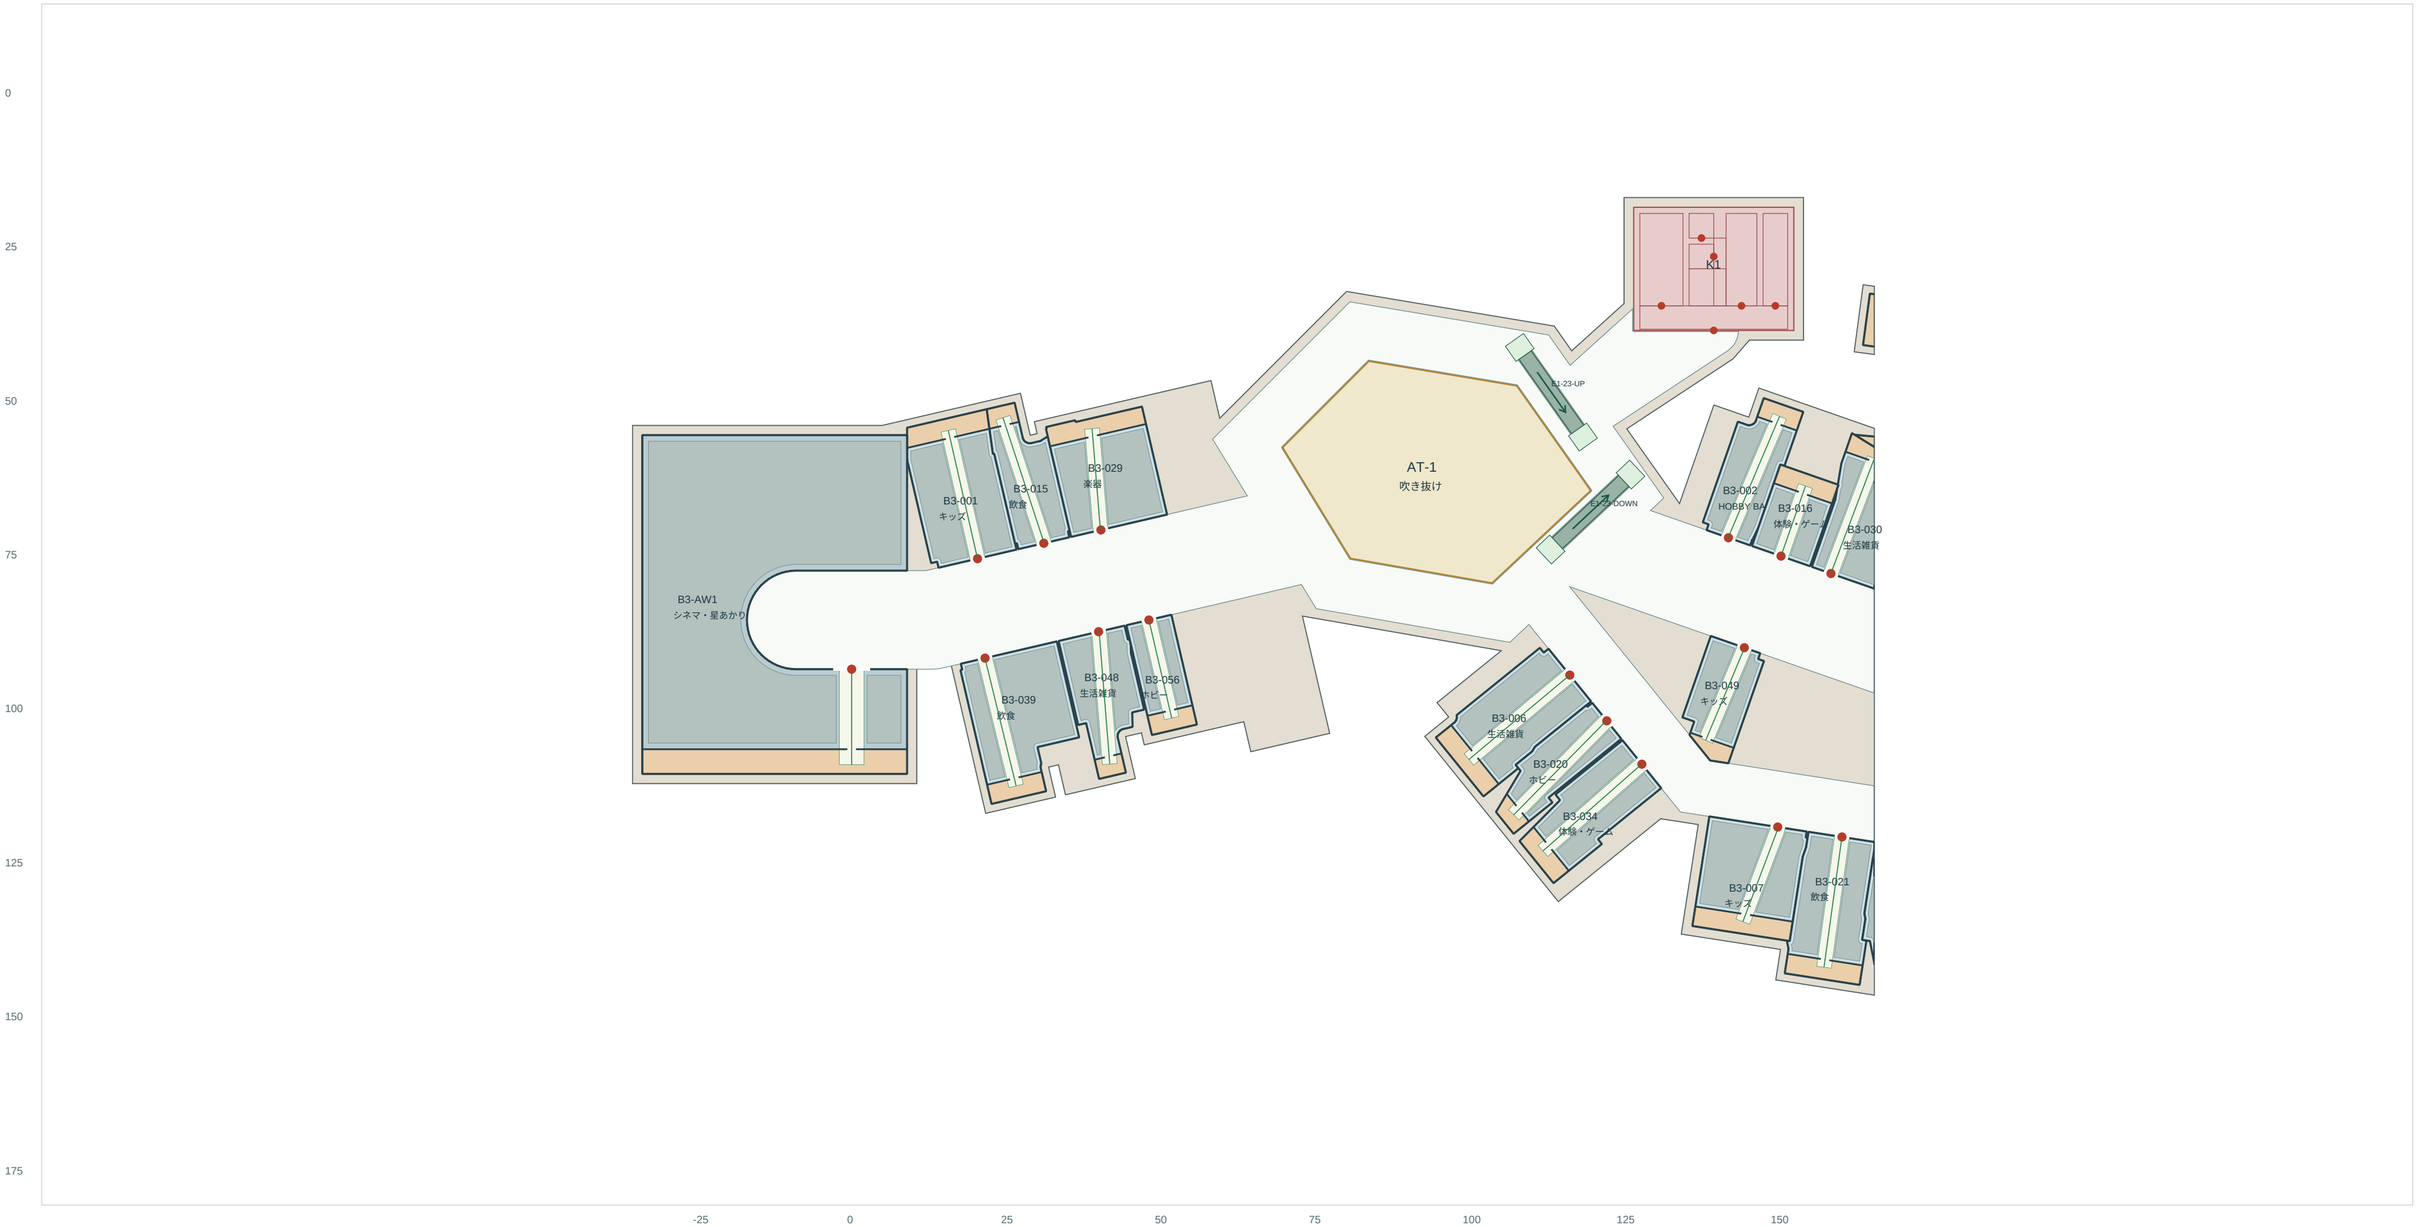

図示の局所座標と機械可読geometry.jsonは共通。入口は2.4m、大型核は6m（有効開口の詳細は改修時検証）。

B館 3F / 区画拡大 2


店舗ID・入口開口・売場主路/横断路・棚配置帯・専用バックルーム。実線壁厚0.25m。棚帯は内装計画。

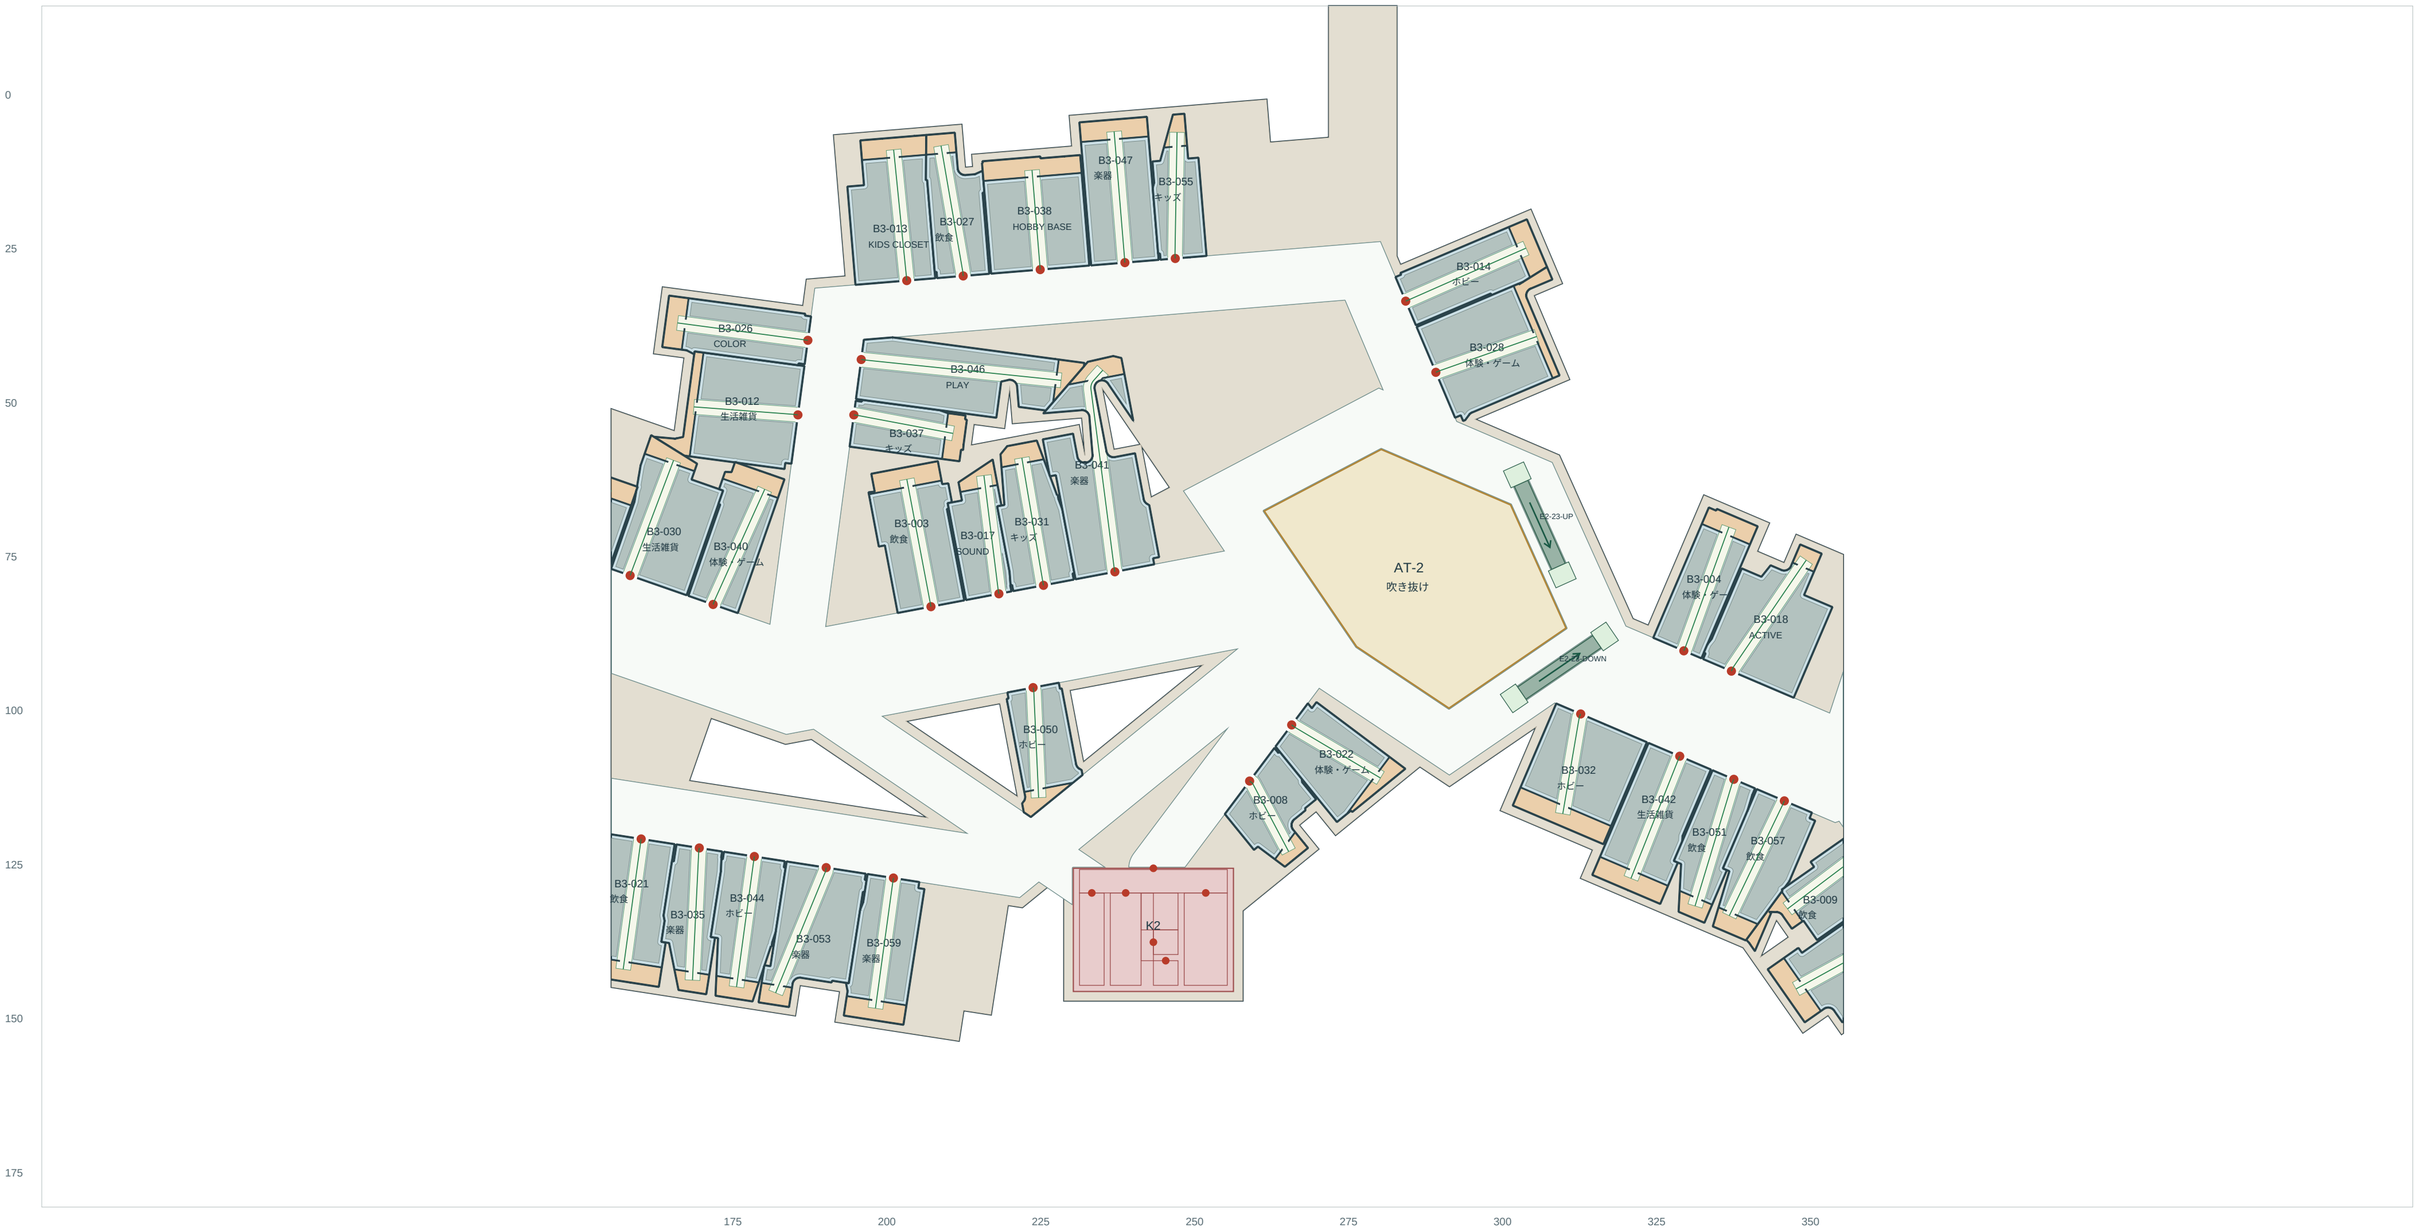

図示の局所座標と機械可読geometry.jsonは共通。入口は2.4m、大型核は6m（有効開口の詳細は改修時検証）。

B館 3F / 区画拡大 3

店舗ID・入口開口・売場主路/横断路・棚配置帯・専用バックルーム。実線壁厚0.25m。棚帯は内装計画。

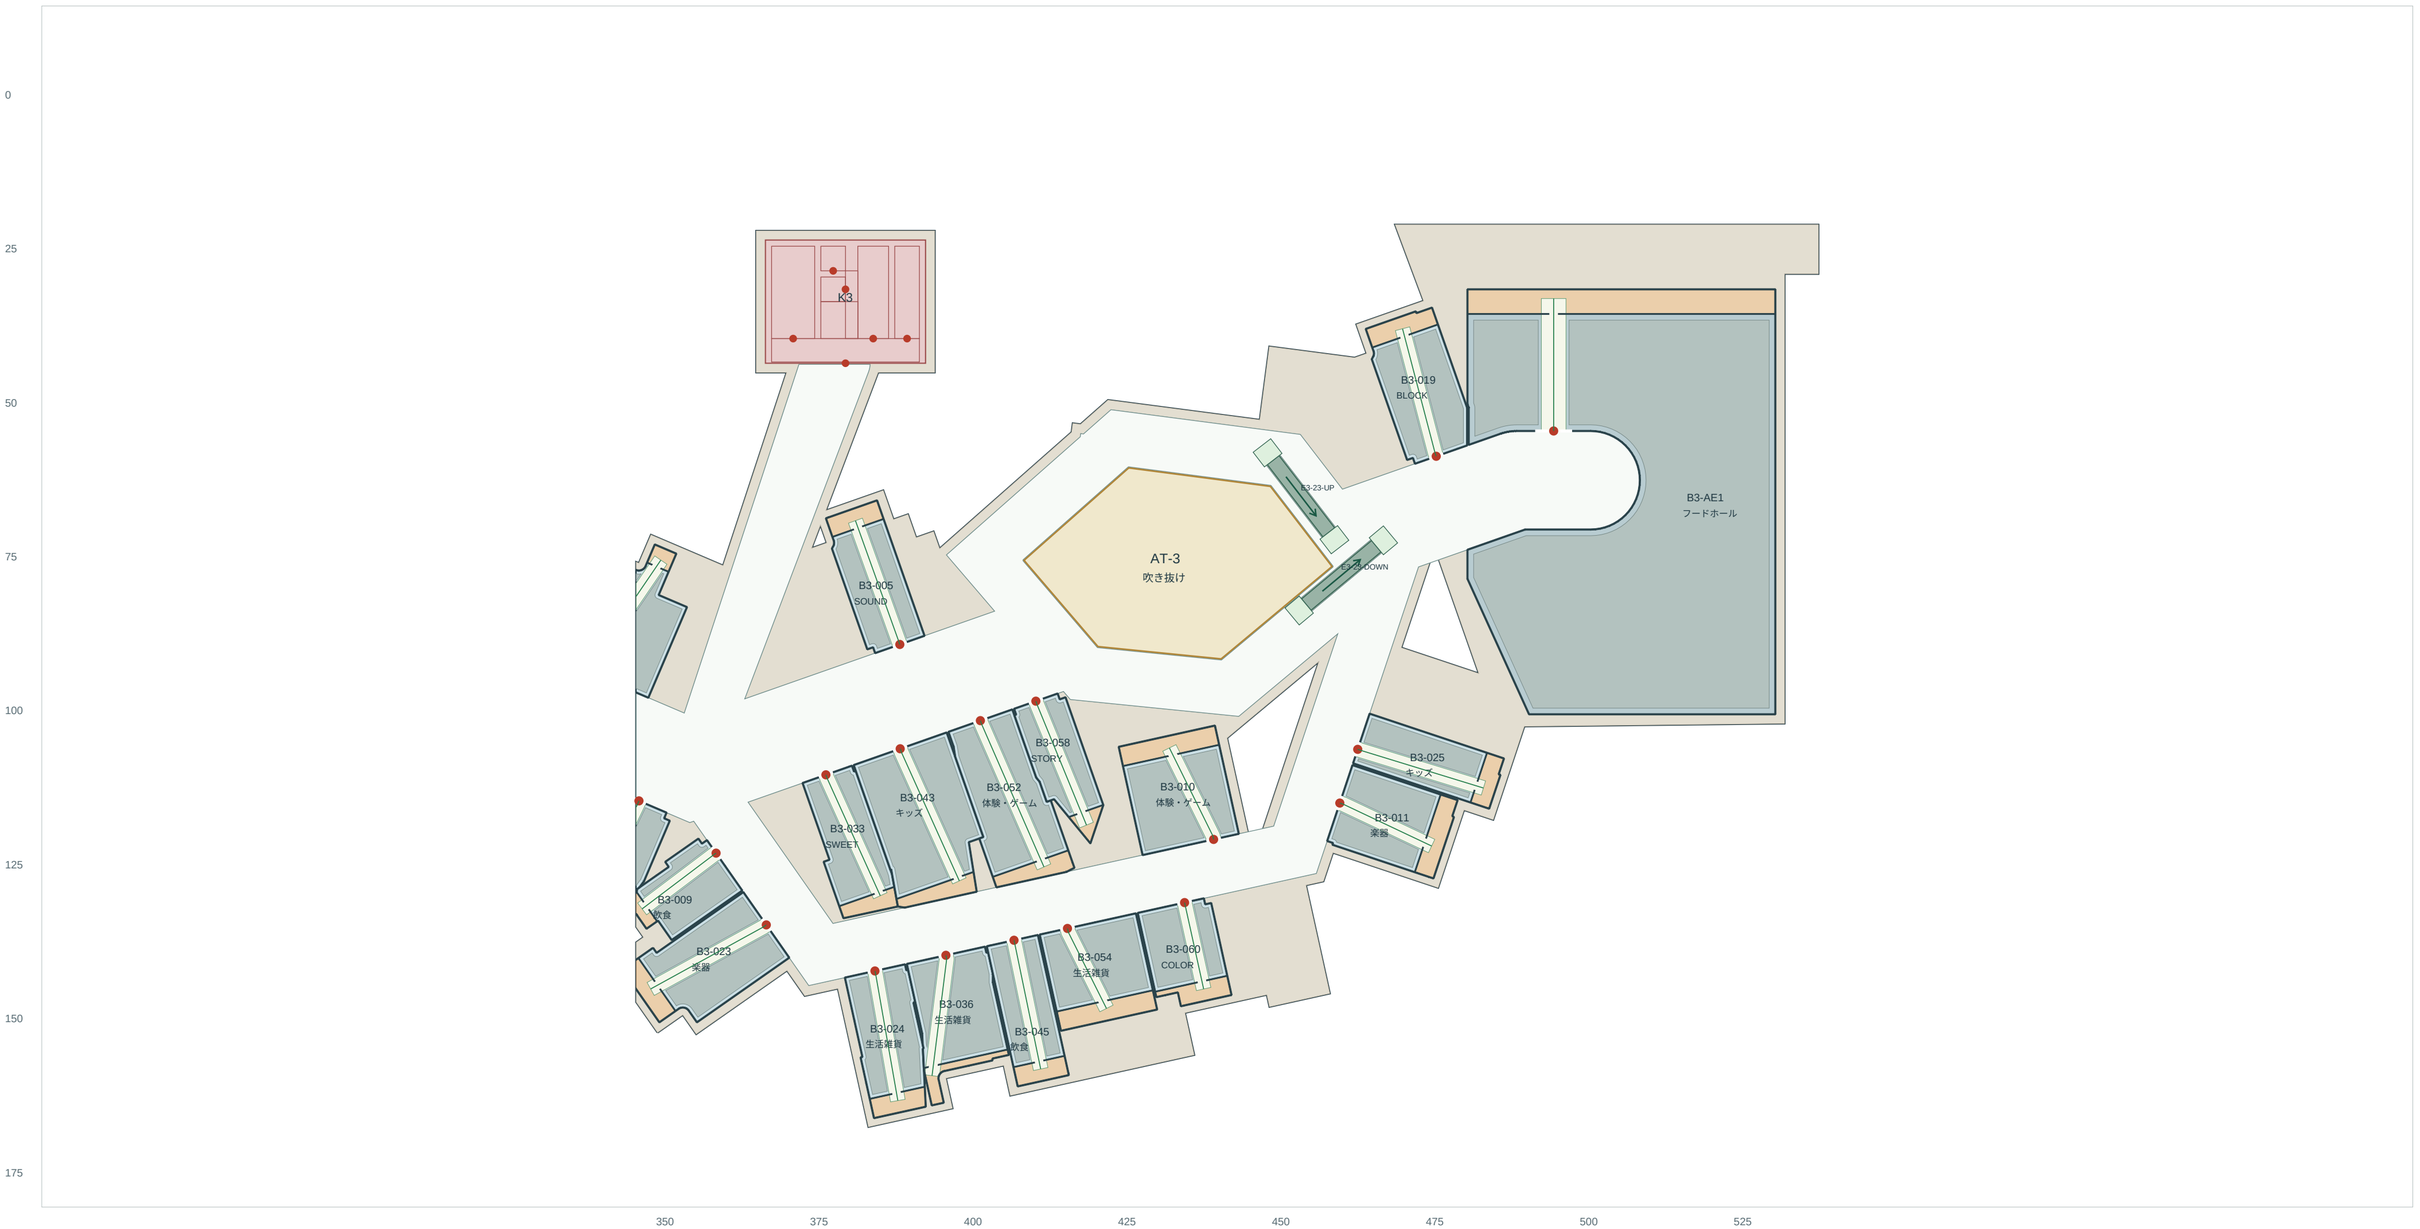


図示の局所座標と機械可読geometry.jsonは共通。入口は2.4m、大型核は6m（有効開口の詳細は改修時検証）。


AT-1 / 吹き抜け・エスカレーター配置と断面

共通開口を上下階で固定。12＝1F↔2F、23＝2F↔3F。上り/下りは矢印方向。


1F +0.000m

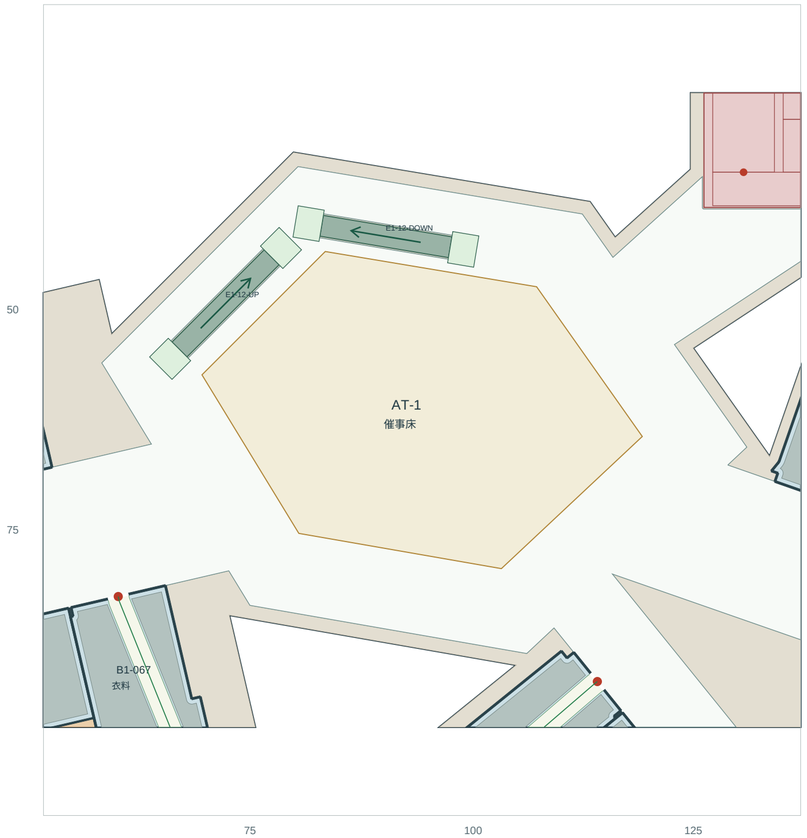


2F +5.525m

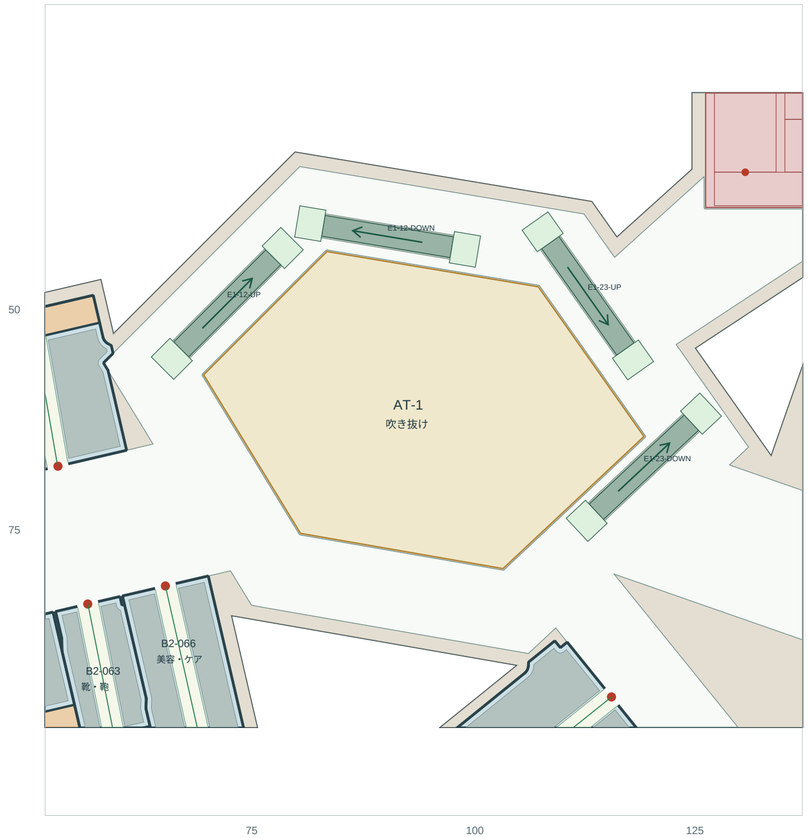


3F +10.875m

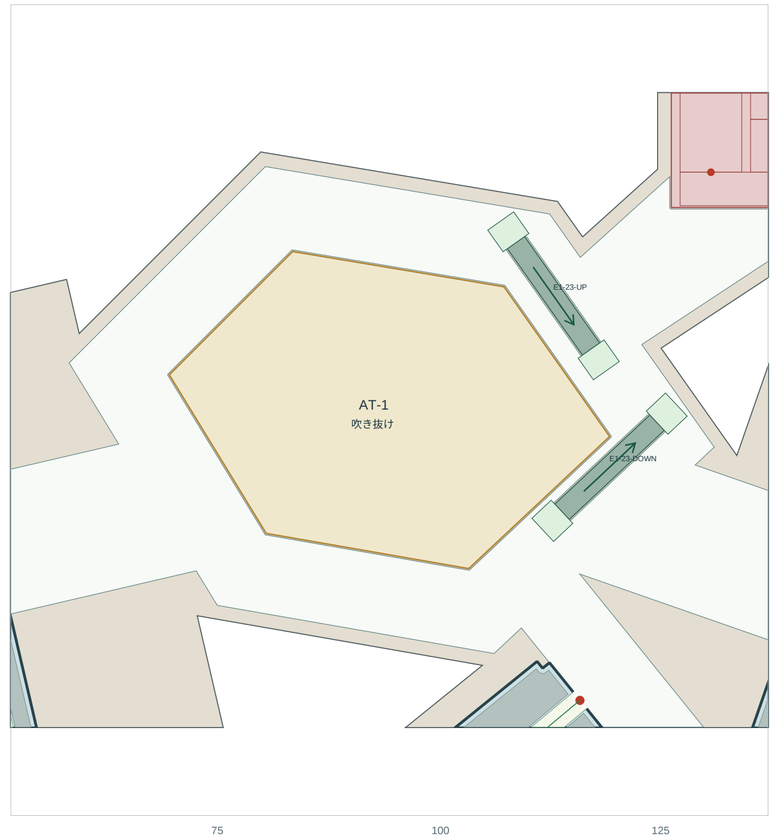

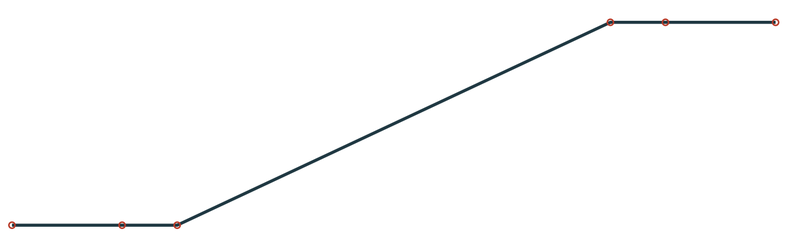

1F → 2F 高差 5.525m / 勾配 25.1°

有効乗降床3.0m ＋ 水平部1.5m ＋ 傾斜走行11.8m ＋ 水平部1.5m ＋ 乗降床3.0m

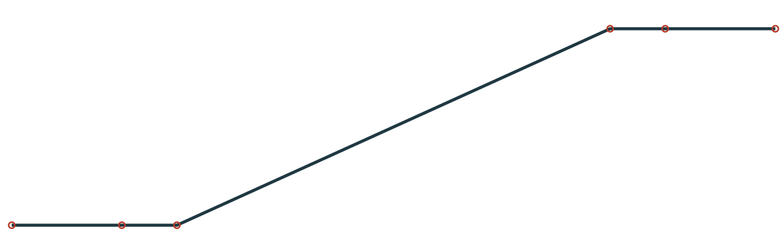

2F → 3F 高差 5.350m / 勾配 24.4°


有効乗降床3.0m ＋ 水平部1.5m ＋ 傾斜走行11.8m ＋ 水平部1.5m ＋ 乗降床3.0m

上階手すり：吹き抜け・床開口周囲 高1.2m、厚0.10mを計画。乗降床への開口を塞がない。頭上有効2.4mは3D施工後に確認。


AT-2 / 吹き抜け・エスカレーター配置と断面

共通開口を上下階で固定。12＝1F↔2F、23＝2F↔3F。上り/下りは矢印方向。


1F +0.000m

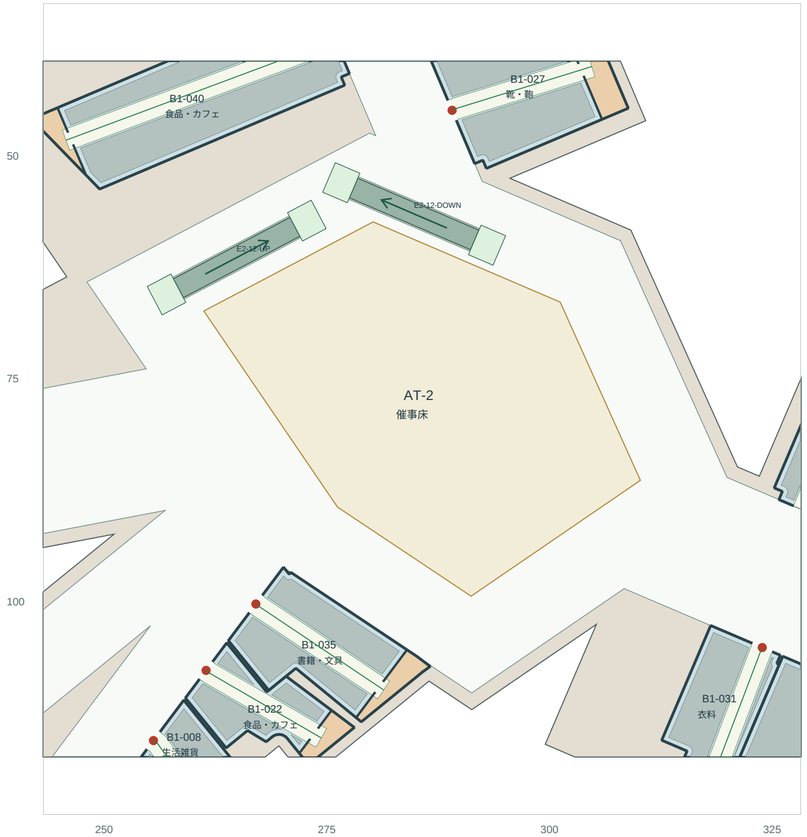


2F +5.525m

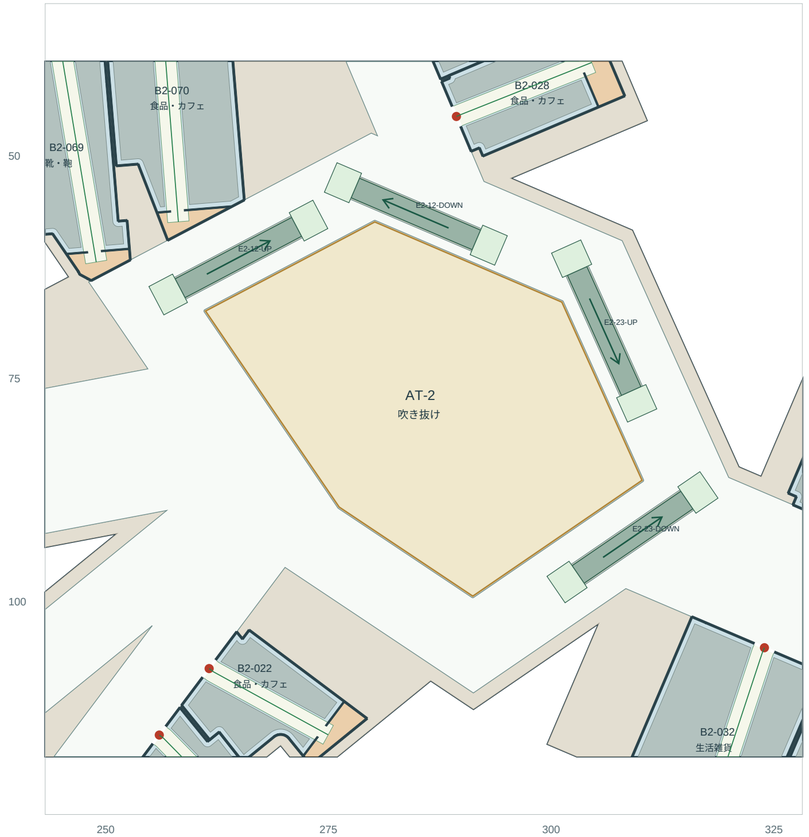


3F +10.875m

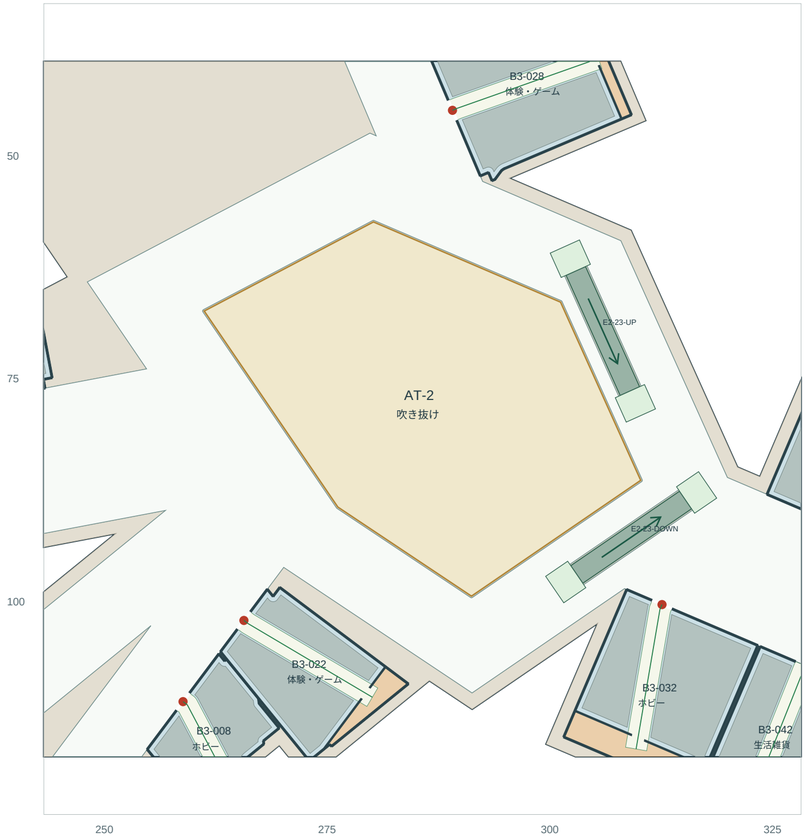

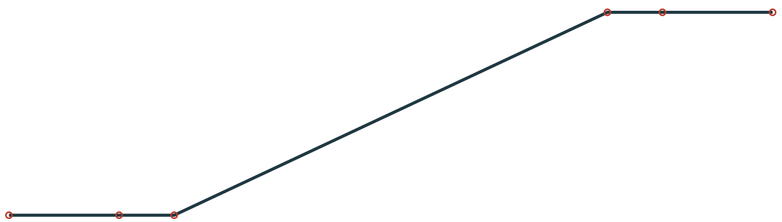

1F → 2F 高差 5.525m / 勾配 25.1°

有効乗降床3.0m ＋ 水平部1.5m ＋ 傾斜走行11.8m ＋ 水平部1.5m ＋ 乗降床3.0m

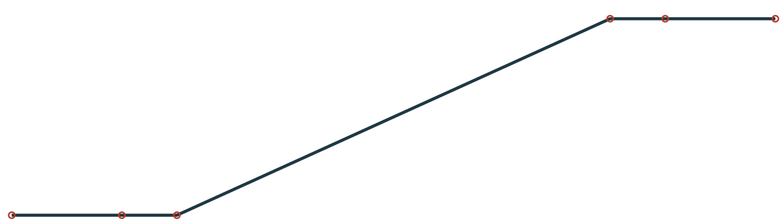

2F → 3F 高差 5.350m / 勾配 24.4°


有効乗降床3.0m ＋ 水平部1.5m ＋ 傾斜走行11.8m ＋ 水平部1.5m ＋ 乗降床3.0m

上階手すり：吹き抜け・床開口周囲 高1.2m、厚0.10mを計画。乗降床への開口を塞がない。頭上有効2.4mは3D施工後に確認。


AT-3 / 吹き抜け・エスカレーター配置と断面

共通開口を上下階で固定。12＝1F↔2F、23＝2F↔3F。上り/下りは矢印方向。


1F +0.000m

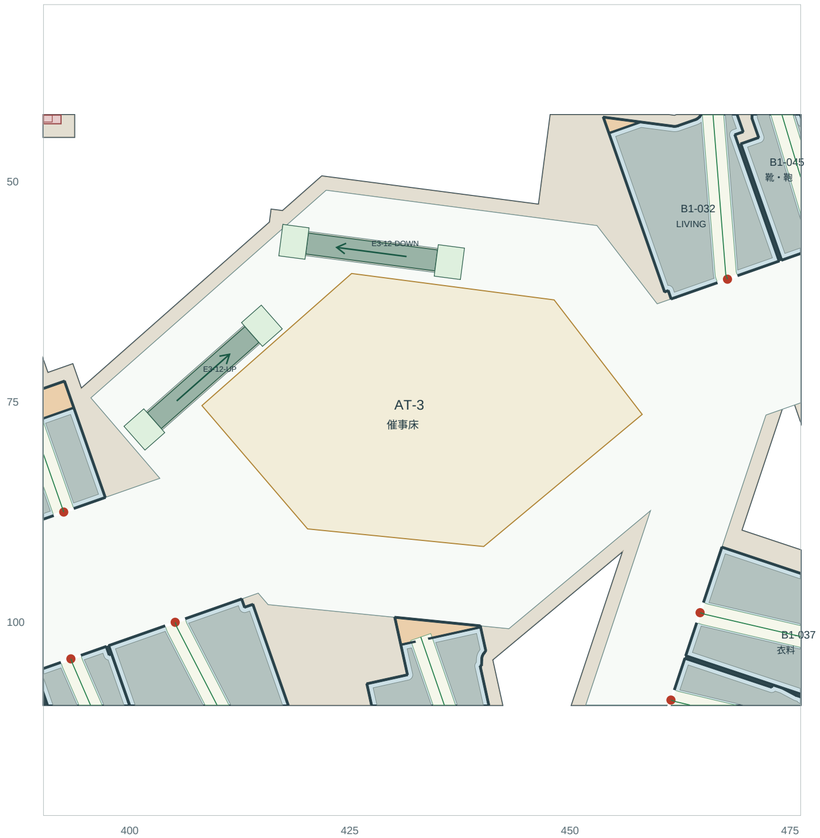


2F +5.525m

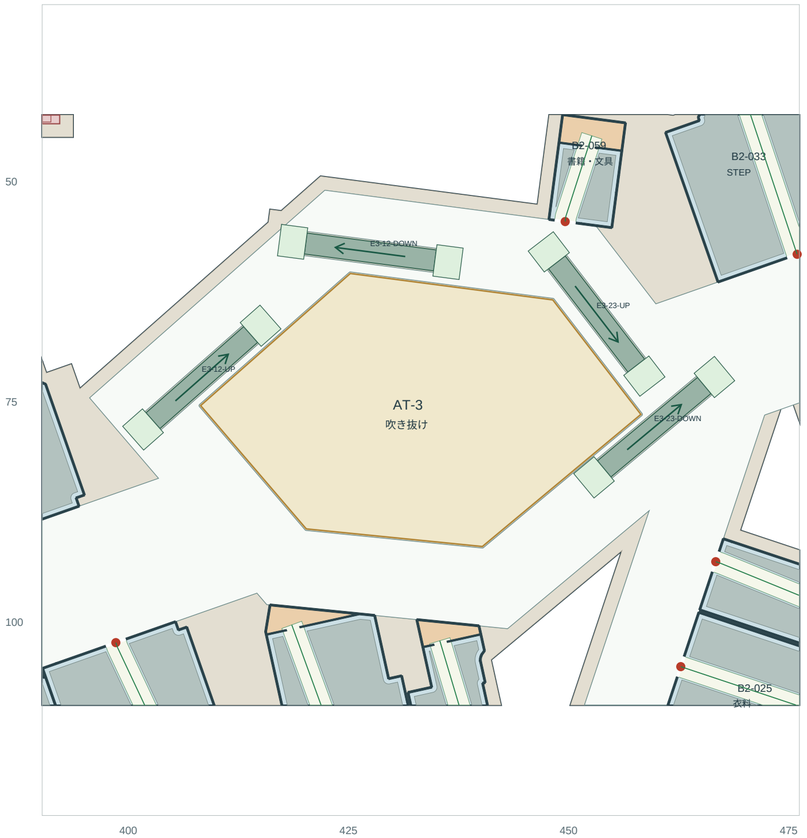


3F +10.875m

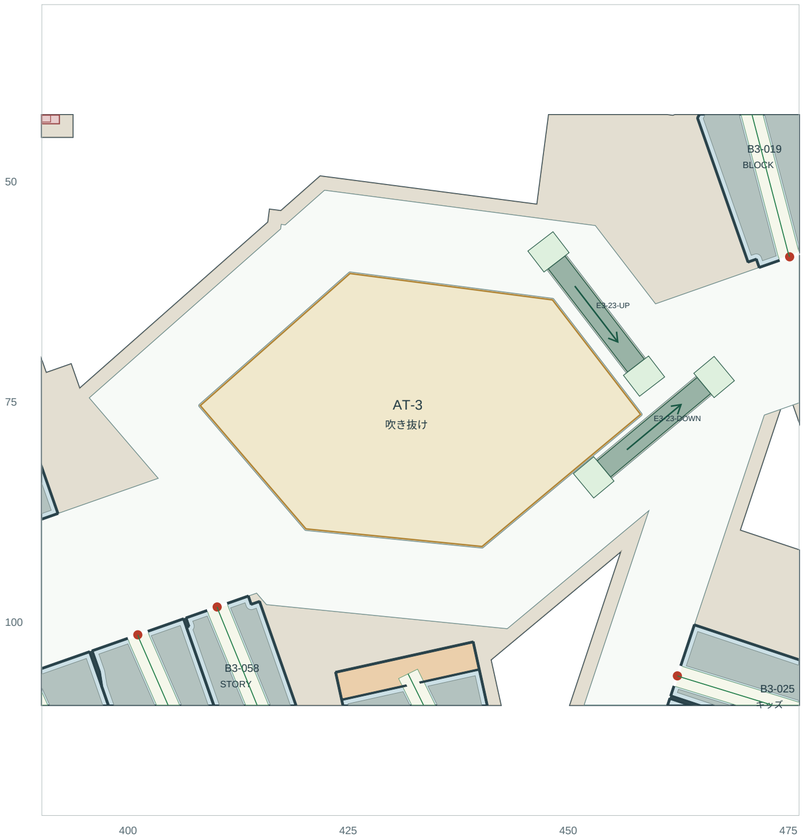

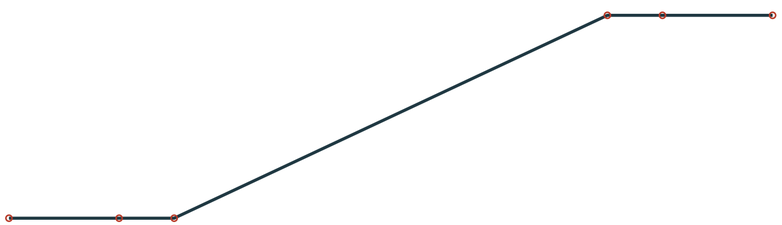

1F → 2F 高差 5.525m / 勾配 25.1°

有効乗降床3.0m ＋ 水平部1.5m ＋ 傾斜走行11.8m ＋ 水平部1.5m ＋ 乗降床3.0m

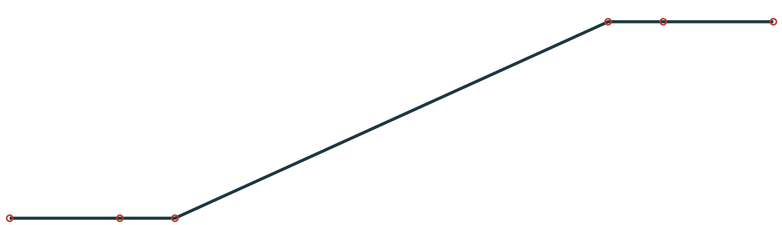


2F → 3F 高差 5.350m / 勾配 24.4°

有効乗降床3.0m ＋ 水平部1.5m ＋ 傾斜走行11.8m ＋ 水平部1.5m ＋ 乗降床3.0m

上階手すり：吹き抜け・床開口周囲 高1.2m、厚0.10mを計画。乗降床への開口を塞がない。頭上有効2.4mは3D施工後に確認。

K1 / トイレ・階段・エレベーター詳細（各階共通）

設備核26×20m。K2のみ180°回転。床高・階段蹴上げは階ごとに異なる。

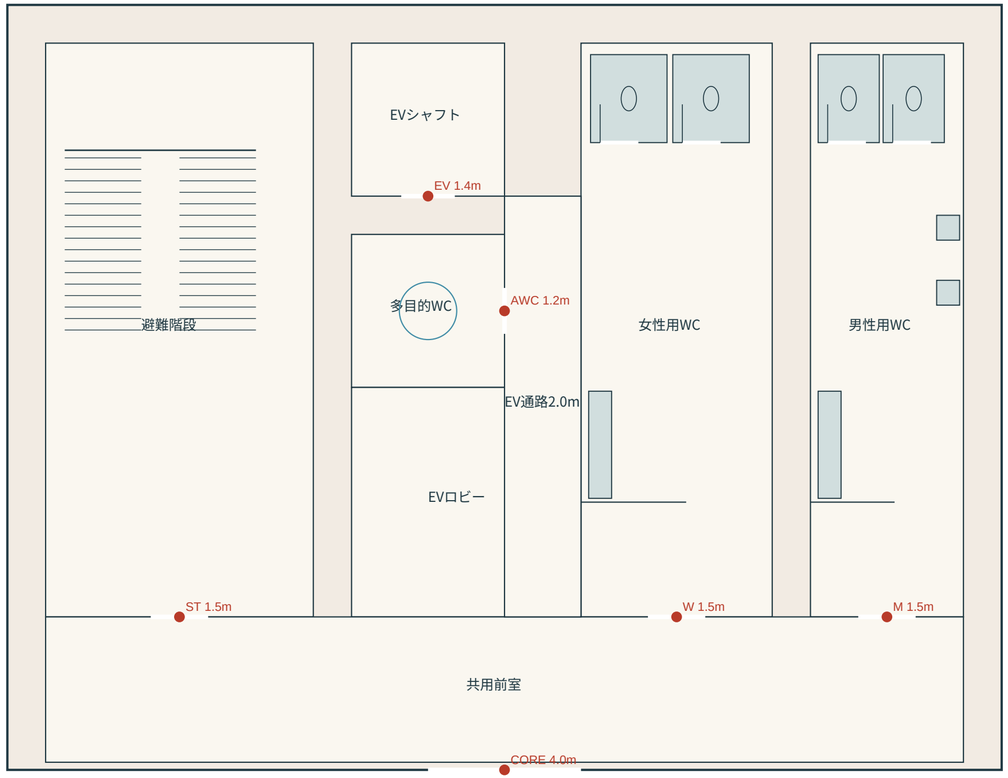

設備中心 Local(139,28) = World(-575, -2)

共用前室の4m開口へ外部アクセス8m。トイレ扉1.5m、階段1.5m。寸法はゲーム用仮設計。

上階との関係：K1/K2/K3は全階で同一XZ。B1/RFへ拡張する設備核を予約。

EV：シャフト4×4m。扉1.4m。正面に幅2.0mのアクセス路を確保。

多目的WC：4×4m（壁厚前）。扉1.2m、回転直径1.5mの余地を図示。

女性用：5×15m、個室2（約2.0×2.3m）、前室/洗面/奥通路。

男性用：4×15m、個室2（約1.6×2.3m）・小便器2、前室/洗面/奥通路。

洗面は側壁カウンター。前室を隔てて個室を直接見通さない配置。

設備の利用区分と個室数はゲーム用案。必要なら子ども用・授乳室を追加。

階段：各階32蹴上げ。16＋16の折返し。踏面0.30m、片側有効2.0m。


1F→2F：蹴上0.17266m。2F→3F：蹴上0.16719m。中間踊場1.8m。

階段室の防火扉・手すり・梁下高さは3D実装時に検証。

Fキー扉・EV呼び出し・経路切替は未実装。図面承認後の工事対象。

K2 / トイレ・階段・エレベーター詳細（各階共通）

設備核26×20m。K2のみ180°回転。床高・階段蹴上げは階ごとに異なる。

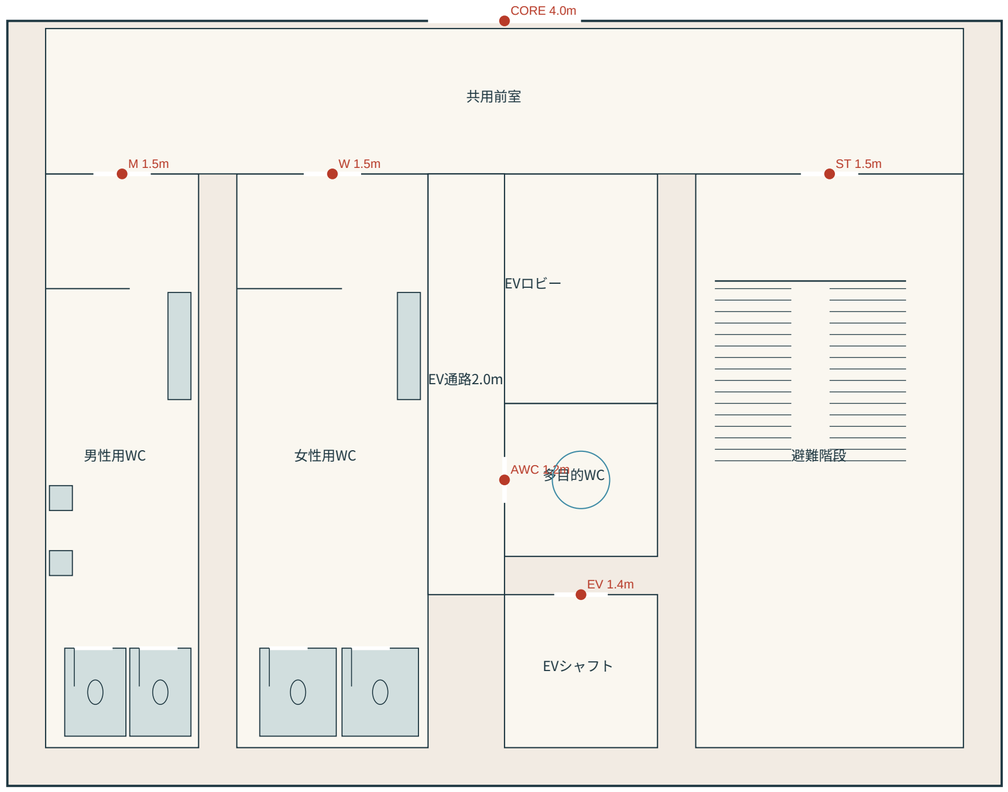

上階との関係：K1/K2/K3は全階で同一XZ。B1/RFへ拡張する設備核を予約。

EV：シャフト4×4m。扉1.4m。正面に幅2.0mのアクセス路を確保。

多目的WC：4×4m（壁厚前）。扉1.2m、回転直径1.5mの余地を図示。

女性用：5×15m、個室2（約2.0×2.3m）、前室/洗面/奥通路。

男性用：4×15m、個室2（約1.6×2.3m）・小便器2、前室/洗面/奥通路。

洗面は側壁カウンター。前室を隔てて個室を直接見通さない配置。

設備の利用区分と個室数はゲーム用案。必要なら子ども用・授乳室を追加。

階段：各階32蹴上げ。16＋16の折返し。踏面0.30m、片側有効2.0m。

1F→2F：蹴上0.17266m。2F→3F：蹴上0.16719m。中間踊場1.8m。

階段室の防火扉・手すり・梁下高さは3D実装時に検証。


Fキー扉・EV呼び出し・経路切替は未実装。図面承認後の工事対象。

設備中心 Local(243,135) = World(-471, 105)

共用前室の4m開口へ外部アクセス8m。トイレ扉1.5m、階段1.5m。寸法はゲーム用仮設計。

K3 / トイレ・階段・エレベーター詳細（各階共通）

設備核26×20m。K2のみ180°回転。床高・階段蹴上げは階ごとに異なる。

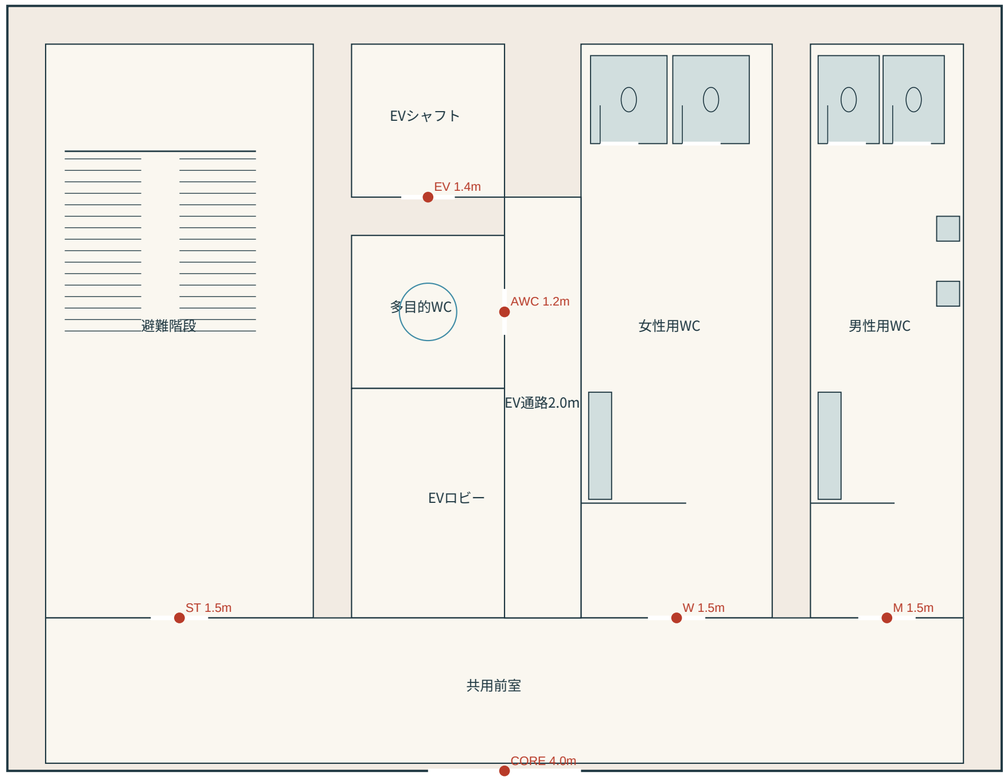

設備中心 Local(379,33) = World(-335, 3)

共用前室の4m開口へ外部アクセス8m。トイレ扉1.5m、階段1.5m。寸法はゲーム用仮設計。

上階との関係：K1/K2/K3は全階で同一XZ。B1/RFへ拡張する設備核を予約。

EV：シャフト4×4m。扉1.4m。正面に幅2.0mのアクセス路を確保。

多目的WC：4×4m（壁厚前）。扉1.2m、回転直径1.5mの余地を図示。

女性用：5×15m、個室2（約2.0×2.3m）、前室/洗面/奥通路。

男性用：4×15m、個室2（約1.6×2.3m）・小便器2、前室/洗面/奥通路。

洗面は側壁カウンター。前室を隔てて個室を直接見通さない配置。

設備の利用区分と個室数はゲーム用案。必要なら子ども用・授乳室を追加。

階段：各階32蹴上げ。16＋16の折返し。踏面0.30m、片側有効2.0m。


1F→2F：蹴上0.17266m。2F→3F：蹴上0.16719m。中間踊場1.8m。

階段室の防火扉・手すり・梁下高さは3D実装時に検証。

Fキー扉・EV呼び出し・経路切替は未実装。図面承認後の工事対象。

階段断面・EV上下階対応


平面図と同じ階高を使用。階段踏面0.30m、32蹴上げ、2方向折返し。EVシャフトは全階同じXZ。

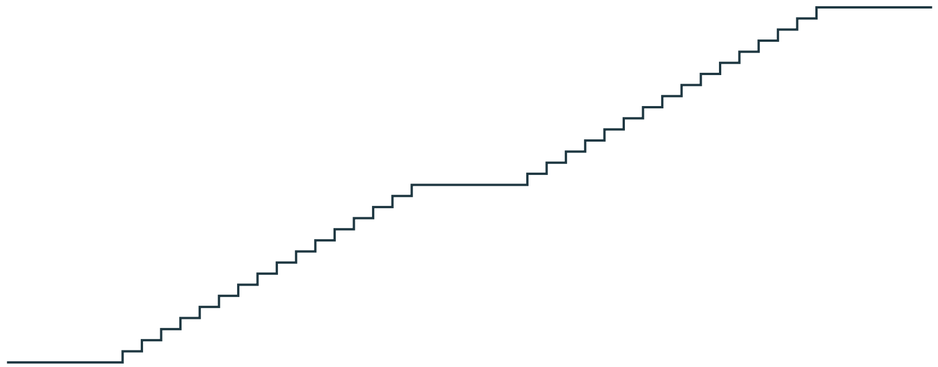

1F → 2F 高差5.525m / 蹴上0.17266m ×32

1段踏面0.30m ×15 / 16蹴上ごとに折返し / 踊場1.8m

断面は折返しを展開表示。平面の階段室7×15m内に2列で収納。

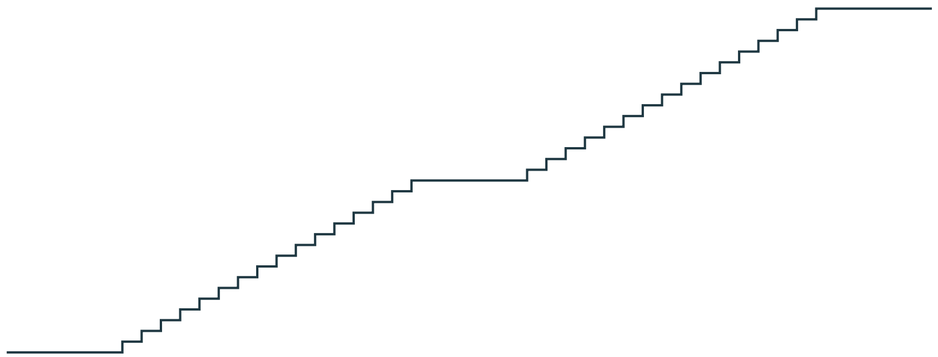

2F → 3F 高差5.350m / 蹴上0.16719m ×32

1段踏面0.30m ×15 / 16蹴上ごとに折返し / 踊場1.8m


断面は折返しを展開表示。平面の階段室7×15m内に2列で収納。

EV：全階のシャフト4×4mを一致。各階の正面ロビーは幅2.0m以上。扉敷居は床高に揃える。

未検証：頭上2.4mの確保、天井梁、手すり接続、EV駆動、階段/扉コリジョンとNPC通行。

A・B・C館 / 既存配置と新B館の接続

青＝既存A/Cの床。茶＝新B館。赤破線＝新しい館間移動中心線。既存A/C本体は変更対象外。

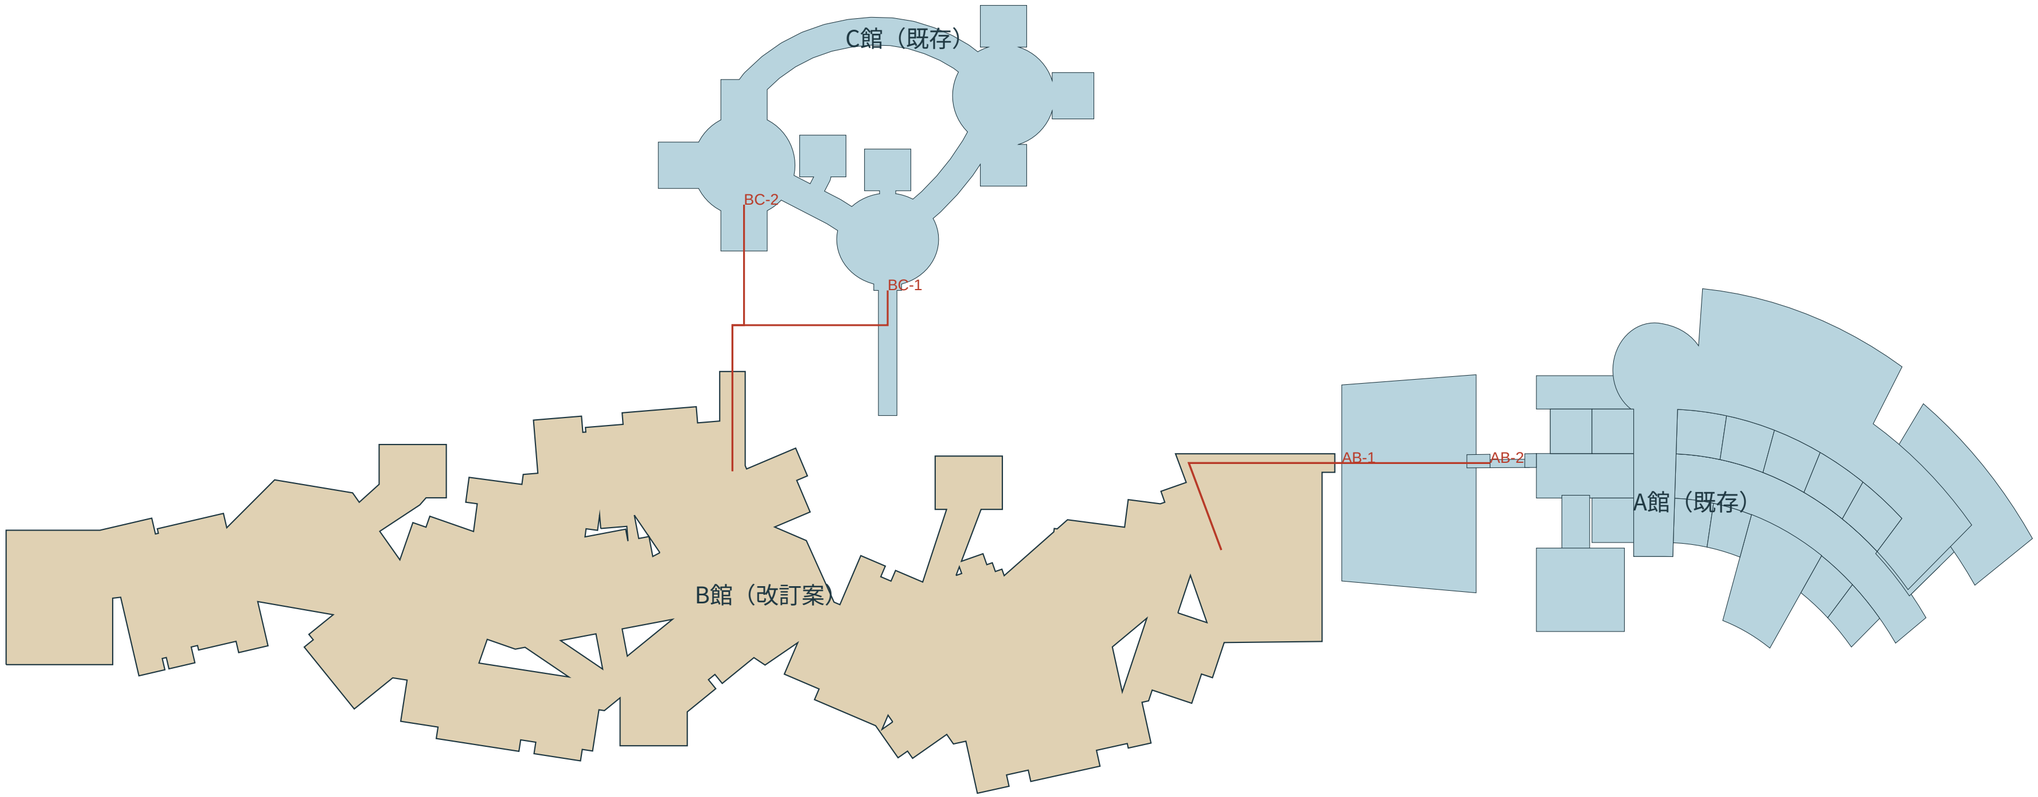

B館の本体は既存A/Cと平面上で重ならない。C側橋・歩行路は既存端点へ接続し、B側の線形を更新する案。

館間連絡路に残る既存ガラスや手すりは改修時に切り欠く。ここではシーンコリジョンの通過を保証しない。

座標整合・館間接続 / 改修境界

建物を変形させずに配置する案。旧店IDは移設先の別名として保持し、距離だけで用途を変えない。

旧アフィン変換の主倍率は約1.096と0.229。同じ1mが方向で異なるため不採用。

新配置：World=(LocalX−714, FloorY, LocalZ−30)。全店舗・設備・昇降機に同じ式を適用。

床高：1F 0.000m / 2F 5.525m / 3F 10.875m（現行の床高を継承）。

A/B 1F端点：Local(540,24.5) = World(−174,−5.5)。現行歩行路のA側端を保持。

A/B 2F端点：Local(604,24.5) = World(−110,−5.5)。橋は幅5m。

B/C 1F端点：Local(344,−50) = World(−370,−80)。地上歩行路、幅8m。

B/C 2F端点：Local(282,−87) = World(−432,−117)。現行C側テラス端点、幅5m。

3Fに館間橋は新設しない。B1/RFは上下設備の予約に留め、未施工。

38個の既存カタログ店舗IDと、カタログにない3F映画館の空間機能を個別に対応表へ記録。

旧座標は区画重心、新座標は入口。意味の異なる点であることをCSVに明記。

現行13売場/階という集計には映画館が含まれるが、3Fのカタログは12。単純なID39件ではない。

A/C本体との平面重複は検査。橋端のガラス・手すり撤去、開口、床段差は3D施工時に確認。

旧大判内装を新しい小区画へ縮尺変形して流用しない。棚・什器を入口と主路に合わせ再配置。

独立検査結果 / 未検証事項

添付の「全件合格」をそのまま採用せず、別の検査を実施。

改訂図面の幾何アサーション 9,508件 / 合格 9,508件 / 不合格 0件。

検査内容：区画相互の面積重複、入口と自店舗の一致、売場内通路、壁開口、設備核の内包。

共用域は半径0.45mの円を想定して内側へ縮小し、連結性と店舗/設備/乗降床への接近を検査。

入口への接近判定は共用域との接点から0.72m以内。家具込み3Dの到達保証ではない。

吹き抜けの2F/3F一致、歩行域からの開口除外、A/C端点、ファストトラベル候補を照合。

添付の不整合：B1-068入口が区画外2.13m、上階歩行域に開口3409m²、設備核とも重複。

この修正では階段・EV・トイレと共用廊下を別の領域として記録した。

未検証：3D頭上余裕、斜面/階段/扉コリジョン、EV動作、NPC回避、猫、宝箱の到達性。

未検証：GPU負荷、1000/5000人、実際の滞在時間。新図面のゲーム内実歩行は0回。

搬入は全店独立した裏回廊ではなく、営業時間外に売場主路を利用する運用案。

構造柱・梁・配管・防火/避難適合は確定していない。ゲーム設計承認と実建築の承認は別。

図面完成の意味：今回提示した区画・動線・設備・接続案が読める設計資料。ゲーム工事完了ではない。

実装順：B1F床/外壁→開口/昇降機→2/3F→店舗再配置→案内図/NPC/宝箱→実歩行と負荷試験。

旧→新対応表 / 1

完全な値と点の定義はcoordinate-migration.csv。旧IDの既存性と業種を照合した移設案。

旧ID / 階	旧 World X,Z	新ID	新 Local X,Z	新 World X,Z	維持する用途
b_anchor_0 / 1F	-669.00,0.00	B1-AW1	-1.00,93.00	-715.00,63.00	デジタルスクエア / 家電
b_0_-210_1 / 1F	-337.00,59.82	B1-052	383.91,106.99	-330.09,76.99	喫茶 リズム
b_0_-220_-1 / 1F	-272.26,-10.13	B1-032	467.69,60.65	-246.31,30.65	LIVING / インテリア
b_0_-260_-1 / 1F	-345.26,-0.44	B1-019	392.31,87.09	-321.69,57.09	FIELD / スポーツ
b_0_-266_1 / 1F	-500.00,59.32	B1-017	211.52,81.64	-502.48,51.64	ページの庭 / 書店・文具
b_0_-302_-1 / 1F	-492.89,-1.07	B1-026	206.06,29.33	-507.94,-0.67	DIGITAL / 家電と暮らし
b_0_-308_1 / 1F	-297.74,27.90	B1-068	478.36,73.86	-235.64,43.86	日々の道具 / 生活雑貨
b_0_-346_-1 / 1F	-567.89,-10.36	B1-025	186.02,45.79	-527.98,15.79	CLOSET / ファッション
b_0_-348_1 / 1F	-559.11,25.34	B1-057	166.23,97.27	-547.77,67.27	WALK / 靴と鞄
b_rear_0_0 / 1F	-590.00,-47.50	B1-002	141.61,71.74	-572.39,41.74	KITCHEN LAB / キッチン用品
b_rear_0_1 / 1F	-478.00,-53.50	B1-048	229.48,27.40	-484.52,-2.60	FRAME / 眼鏡
b_rear_0_2 / 1F	-351.00,-52.50	B1-066	267.64,24.26	-446.36,-5.74	SELECT / 服飾雑貨
b_rear_0_3 / 1F	-256.00,-46.50	B1-044	336.36,110.17	-377.64,80.17	FOCUS / 生活家電
b_anchor_1 / 2F	-669.00,0.00	B2-AW1	-1.00,93.00	-715.00,63.00	ホーム＆リビング
b_1_-210_1 / 2F	-337.00,59.82	B2-004	332.87,91.29	-381.13,61.29	MELLOW / カフェ
b_1_-220_-1 / 2F	-272.26,-10.13	B2-056	414.07,134.98	-299.93,104.98	ROOM / 寝具と暮らし
b_1_-260_-1 / 2F	-345.26,-0.44	B2-009	360.68,126.40	-353.32,96.40	ORBIT / バッグと旅行
b_1_-266_1 / 2F	-500.00,59.32	B2-017	224.91,79.11	-489.09,49.11	ページの庭 / 書店・文具
b_1_-302_-1 / 2F	-492.89,-1.07	B2-038	222.82,27.95	-491.18,-2.05	KITCHEN LAB / キッチン用品
b_1_-308_1 / 2F	-297.74,27.90	B2-054	398.37,101.91	-315.63,71.91	LUMI / コスメとケア
b_1_-346_-1 / 2F	-567.89,-10.36	B2-013	199.60,29.86	-514.40,-0.14	NOVA / レディース
b_1_-348_1 / 2F	-559.11,25.34	B2-037	194.66,49.11	-519.34,19.11	STUDIO / メンズ

旧→新対応表 / 2

完全な値と点の定義はcoordinate-migration.csv。旧IDの既存性と業種を照合した移設案。

旧ID / 階	旧 World X,Z	新ID	新 Local X,Z	新 World X,Z	維持する用途
b_rear_1_0 / 2F	-590.00,-47.50	B2-012	184.88,54.33	-529.12,24.33	LUMI / コスメとケア
b_rear_1_1 / 2F	-478.00,-53.50	B2-045	231.50,27.23	-482.50,-2.77	ORBIT / バッグと旅行
b_rear_1_2 / 2F	-351.00,-52.50	B2-014	284.85,34.99	-429.15,4.99	ROOM / 寝具と暮らし
b_rear_1_3 / 2F	-256.00,-46.50	B2-033	475.75,57.82	-238.25,27.82	STEP / 靴
b_2_-210_1 / 3F	-337.00,59.82	B3-033	375.82,109.82	-338.18,79.82	SWEET / デザートカフェ
b_2_-220_-1 / 3F	-272.26,-10.13	B3-060	434.06,130.57	-279.94,100.57	COLOR / 画材と文具
b_2_-260_-1 / 3F	-345.26,-0.44	B3-018	336.87,92.99	-377.13,62.99	ACTIVE / スポーツ
b_2_-266_1 / 3F	-500.00,59.32	B3-017	217.91,80.43	-496.09,50.43	SOUND / 楽器
b_2_-302_-1 / 3F	-492.89,-1.07	B3-046	195.55,42.40	-518.45,12.40	PLAY / ゲームコーナー
b_2_-308_1 / 3F	-297.74,27.90	B3-058	409.92,97.87	-304.08,67.87	STORY / 児童書
b_2_-346_-1 / 3F	-567.89,-10.36	B3-013	202.95,29.58	-511.05,-0.42	KIDS CLOSET / こども服
b_2_-348_1 / 3F	-559.11,25.34	B3-002	141.38,71.66	-572.62,41.66	HOBBY BASE / 模型
b_rear_2_0 / 3F	-590.00,-47.50	B3-026	186.89,39.28	-527.11,9.28	COLOR / 画材と文具
b_rear_2_1 / 3F	-478.00,-53.50	B3-038	224.62,27.80	-489.38,-2.20	HOBBY BASE / 模型
b_rear_2_2 / 3F	-351.00,-52.50	B3-005	387.82,88.66	-326.18,58.66	SOUND / 楽器
b_rear_2_3 / 3F	-256.00,-46.50	B3-019	474.93,58.11	-239.07,28.11	BLOCK / おもちゃ
（旧カタログIDなし）scripts/b_wing.gd::_cinema / 3F	-669.00,0.00	B3-AW1	-1.00,93.00	-715.00,63.00	シネマ・星あかり
翼の広場 / 1F	-624.00,0.00	AT-1	93.67,60.92	-620.33,30.92	広場・吹き抜け
時の広場 / 1F	-414.00,26.00	AT-2	286.54,76.99	-427.46,46.99	広場・吹き抜け
光の広場 / 1F	-218.00,0.00	AT-3	432.99,75.49	-281.01,45.49	広場・吹き抜け
翼の広場 / 2F	-624.00,0.00	AT-1	93.67,60.92	-620.33,30.92	広場・吹き抜け
時の広場 / 2F	-414.00,26.00	AT-2	286.54,76.99	-427.46,46.99	広場・吹き抜け

旧→新対応表 / 3

完全な値と点の定義はcoordinate-migration.csv。旧IDの既存性と業種を照合した移設案。

旧ID / 階	旧 World X,Z	新ID	新 Local X,Z	新 World X,Z	維持する用途
光の広場 / 2F	-218.00,0.00	AT-3	432.99,75.49	-281.01,45.49	広場・吹き抜け
翼の広場 / 3F	-624.00,0.00	AT-1	93.67,60.92	-620.33,30.92	広場・吹き抜け
時の広場 / 3F	-414.00,26.00	AT-2	286.54,76.99	-427.46,46.99	広場・吹き抜け
光の広場 / 3F	-218.00,0.00	AT-3	432.99,75.49	-281.01,45.49	広場・吹き抜け
AB-1 / 1F	-174.00,-5.50	AB-1	540.00,24.50	-174.00,-5.50	館間連絡
BC-1 / 1F	-370.00,-80.00	BC-1	344.00,-50.00	-370.00,-80.00	館間連絡
AB-2 / 2F	-110.00,-5.50	AB-2	604.00,24.50	-110.00,-5.50	館間連絡
BC-2 / 2F	-432.00,-117.00	BC-2	282.00,-87.00	-432.00,-117.00	館間連絡
b.entrance / 1F	-194.00,-5.50	b.entrance	530.00,24.50	-184.00,-5.50	ファストトラベル
b.lounge / 2F	-192.00,-5.50	b.lounge	522.00,24.50	-192.00,-5.50	ファストトラベル
b.cinema / 3F	-654.00,0.00	b.cinema	12.00,85.00	-702.00,55.00	ファストトラベル
b.digital / 1F	-676.00,0.00	b.digital	12.00,85.00	-702.00,55.00	ファストトラベル
ab.skybridge / 2F	-150.00,-5.50	ab.skybridge	564.00,24.50	-150.00,-5.50	ファストトラベル
bc.walkway / 1F	-370.00,-52.00	bc.walkway	344.00,-42.00	-370.00,-72.00	ファストトラベル
bc.skybridge / 2F	-442.00,-65.00	bc.skybridge	282.00,-35.00	-432.00,-65.00	ファストトラベル

店舗台帳 / 1

間口は入口のある現状辺の長さ。深さはその辺からの最大法線距離。大型核・不整形区画は最大寸法の参考値。

新ID / 用途	面積㎡ / 間口m / 奥行m	入口 Local X,Z	入口 World X,Y,Z	バックルーム㎡
B1-001 衣料	152.6 / 3.8 / 23.3	18.58,75.26	-695.42,0.000,45.26	13.8
B1-002 KITCHEN LAB / キッチン用品	335.0 / 16.0 / 23.3	141.61,71.74	-572.39,0.000,41.74	22.8
B1-003 靴・鞄	182.6 / 8.5 / 19.9	202.70,83.31	-511.30,0.000,53.31	20.7
B1-004 食品・カフェ	226.8 / 5.9 / 23.3	328.28,89.33	-385.72,0.000,59.33	25.4
B1-005 書籍・文具	183.0 / 7.5 / 23.3	383.77,90.08	-330.23,0.000,60.08	16.0
B1-006 美容・ケア	214.8 / 8.5 / 23.3	113.90,91.82	-600.10,0.000,61.82	22.9
B1-007 衣料	233.6 / 10.2 / 18.3	146.06,118.11	-567.94,0.000,88.11	37.3
B1-008 生活雑貨	141.8 / 11.3 / 13.7	255.35,115.21	-458.65,0.000,85.21	21.2
B1-009 靴・鞄	293.1 / 11.0 / 23.3	364.54,131.90	-349.46,0.000,101.90	37.1
B1-010 食品・カフェ	255.9 / 7.3 / 22.7	439.32,120.19	-274.68,0.000,90.19	15.6
B1-011 書籍・文具	142.3 / 6.4 / 18.3	458.23,117.53	-255.77,0.000,87.53	24.8
B1-012 美容・ケア	244.4 / 13.0 / 19.1	184.68,55.85	-529.32,0.000,25.85	23.2
B1-013 衣料	167.9 / 4.0 / 23.3	196.61,30.11	-517.39,0.000,0.11	16.7
B1-014 生活雑貨	246.4 / 10.0 / 23.3	284.26,33.61	-429.74,0.000,3.61	33.9
B1-015 靴・鞄	238.1 / 10.0 / 23.3	25.58,73.63	-688.42,0.000,43.63	33.0
B1-016 食品・カフェ	262.9 / 6.9 / 23.3	152.70,75.61	-561.30,0.000,45.61	35.3
B1-017 ページの庭 / 書店・文具	301.9 / 8.9 / 21.3	211.52,81.64	-502.48,0.000,51.64	13.5
B1-018 美容・ケア	288.3 / 13.0 / 23.3	341.01,94.76	-372.99,0.000,64.76	31.4
B1-019 FIELD / スポーツ	140.0 / 10.0 / 14.0	392.31,87.09	-321.69,0.000,57.09	32.0
B1-020 生活雑貨	352.9 / 16.0 / 23.3	121.79,101.58	-592.21,0.000,71.58	39.0
B1-021 靴・鞄	191.7 / 8.5 / 23.3	155.62,119.59	-558.38,0.000,89.59	18.1
B1-022 食品・カフェ	115.1 / 7.7 / 17.2	261.25,107.33	-452.75,0.000,77.33	15.1
B1-023 書籍・文具	253.0 / 9.6 / 23.0	383.59,141.71	-330.41,0.000,111.71	35.2
B1-024 美容・ケア	193.4 / 10.0 / 23.3	461.27,108.43	-252.73,0.000,78.43	14.6
B1-025 CLOSET / ファッション	168.6 / 6.7 / 23.3	186.02,45.79	-527.98,0.000,15.79	20.4
B1-026 DIGITAL / 家電と暮らし	239.5 / 7.4 / 23.3	206.06,29.33	-507.94,0.000,-0.67	34.7
B1-027 靴・鞄	249.8 / 13.0 / 18.3	288.87,44.48	-425.13,0.000,14.48	38.4

店舗台帳 / 2

間口は入口のある現状辺の長さ。深さはその辺からの最大法線距離。大型核・不整形区画は最大寸法の参考値。

新ID / 用途	面積㎡ / 間口m / 奥行m	入口 Local X,Z	入口 World X,Y,Z	バックルーム㎡
B1-028 食品・カフェ	231.7 / 13.0 / 18.3	37.07,70.96	-676.93,0.000,40.96	33.5
B1-029 書籍・文具	142.2 / 7.5 / 18.6	163.66,79.43	-550.34,0.000,49.43	18.4
B1-030 美容・ケア	271.2 / 11.0 / 23.3	228.59,78.41	-485.41,0.000,48.41	39.4
B1-031 衣料	161.7 / 4.4 / 23.3	323.68,104.76	-390.32,0.000,74.76	15.4
B1-032 LIVING / インテリア	280.2 / 12.4 / 23.3	467.69,60.65	-246.31,0.000,30.65	14.9
B1-033 靴・鞄	180.3 / 7.1 / 23.3	129.64,111.29	-584.36,0.000,81.29	24.8
B1-034 食品・カフェ	288.5 / 15.2 / 18.0	167.62,121.45	-546.38,0.000,91.45	51.2
B1-035 書籍・文具	187.0 / 10.3 / 19.9	266.84,99.88	-447.16,0.000,69.88	18.7
B1-036 美容・ケア	143.5 / 7.5 / 18.3	393.60,139.50	-320.40,0.000,109.50	23.3
B1-037 衣料	300.5 / 10.3 / 23.9	464.57,98.51	-249.43,0.000,68.51	32.1
B1-038 生活雑貨	345.9 / 16.0 / 23.3	194.20,52.58	-519.80,0.000,22.58	20.2
B1-039 靴・鞄	231.7 / 13.0 / 18.3	219.14,28.25	-494.86,0.000,-1.75	33.5
B1-040 食品・カフェ	334.3 / 8.2 / 34.9	275.73,36.55	-438.27,0.000,6.55	13.2
B1-041 書籍・文具	162.4 / 8.5 / 18.3	47.83,68.45	-666.17,0.000,38.45	31.6
B1-042 美容・ケア	178.6 / 10.0 / 19.0	172.21,82.41	-541.79,0.000,52.41	20.0
B1-043 衣料	160.8 / 7.5 / 25.1	237.97,76.63	-476.03,0.000,46.63	19.5
B1-044 FOCUS / 生活家電	288.3 / 9.4 / 18.0	336.36,110.17	-377.64,0.000,80.17	51.2
B1-045 靴・鞄	154.5 / 3.3 / 23.3	478.38,56.90	-235.62,0.000,26.90	14.9
B1-046 食品・カフェ	253.0 / 8.9 / 23.0	182.72,123.78	-531.28,0.000,93.78	35.2
B1-047 書籍・文具	192.0 / 5.8 / 23.3	404.48,137.10	-309.52,0.000,107.10	14.0
B1-048 FRAME / 眼鏡	163.4 / 7.2 / 22.3	229.48,27.40	-484.52,0.000,-2.60	13.9
B1-049 衣料	288.1 / 13.0 / 23.3	23.07,90.64	-690.93,0.000,60.64	29.1
B1-050 生活雑貨	207.8 / 8.3 / 16.0	158.03,94.41	-555.97,0.000,64.41	41.4
B1-051 靴・鞄	256.1 / 9.7 / 24.3	345.46,114.05	-368.54,0.000,84.05	25.0
B1-052 喫茶 リズム	309.1 / 10.4 / 25.1	383.91,106.99	-330.09,0.000,76.99	33.8
B1-053 書籍・文具	143.2 / 7.5 / 18.3	191.10,125.08	-522.90,0.000,95.08	23.3
B1-054 美容・ケア	256.2 / 6.5 / 23.3	417.12,134.31	-296.88,0.000,104.31	12.7

店舗台帳 / 3

間口は入口のある現状辺の長さ。深さはその辺からの最大法線距離。大型核・不整形区画は最大寸法の参考値。

新ID / 用途	面積㎡ / 間口m / 奥行m	入口 Local X,Z	入口 World X,Y,Z	バックルーム㎡
B1-055 衣料	359.2 / 16.0 / 23.3	242.66,26.31	-471.34,0.000,-3.69	42.5
B1-056 生活雑貨	204.4 / 8.5 / 23.3	33.83,88.14	-680.17,0.000,58.14	28.2
B1-057 WALK / 靴と鞄	127.6 / 8.5 / 15.8	166.23,97.27	-547.77,0.000,67.27	20.8
B1-058 食品・カフェ	215.3 / 8.5 / 24.9	393.12,103.76	-320.88,0.000,73.76	22.7
B1-059 書籍・文具	212.1 / 10.0 / 23.3	200.04,126.46	-513.96,0.000,96.46	20.9
B1-060 美容・ケア	213.5 / 8.2 / 23.3	424.58,132.66	-289.42,0.000,102.66	31.4
B1-061 衣料	260.0 / 11.0 / 23.3	256.41,25.18	-457.59,0.000,-4.82	36.2
B1-062 生活雑貨	256.0 / 12.9 / 16.0	47.54,84.95	-666.46,0.000,54.95	51.2
B1-063 靴・鞄	451.9 / 16.0 / 28.0	404.96,99.60	-309.04,0.000,69.60	33.1
B1-064 食品・カフェ	239.1 / 8.3 / 18.0	214.03,128.63	-499.97,0.000,98.63	42.6
B1-065 書籍・文具	276.4 / 14.7 / 17.9	437.61,129.78	-276.39,0.000,99.78	27.9
B1-066 SELECT / 服飾雑貨	121.5 / 4.1 / 16.3	267.64,24.26	-446.36,0.000,-5.74	23.3
B1-067 衣料	245.3 / 11.0 / 23.3	59.49,82.17	-654.51,0.000,52.17	20.8
B1-068 日々の道具 / 生活雑貨	63.6 / 3.4 / 23.8	478.36,73.86	-235.64,0.000,43.86	12.4
B1-AW1 デジタルスクエア / 家電	1976.6 / 18.0 / 17.0	-1.00,93.00	-715.00,0.000,63.00	172.0
B1-AE1 食品大型店	2822.3 / 12.0 / 23.0	494.00,54.00	-220.00,0.000,24.00	199.5
B2-001 衣料	252.7 / 10.0 / 23.3	17.98,75.40	-696.02,5.525,45.40	33.0
B2-002 生活雑貨	275.4 / 11.0 / 23.3	144.92,72.89	-569.08,5.525,42.89	36.2
B2-003 靴・鞄	253.0 / 5.9 / 23.0	213.00,81.36	-501.00,5.525,51.36	35.2
B2-004 MELLOW / カフェ	287.3 / 12.9 / 23.3	332.87,91.29	-381.13,5.525,61.29	21.8
B2-005 書籍・文具	175.3 / 10.0 / 19.9	376.92,92.48	-337.08,5.525,62.48	13.2
B2-006 美容・ケア	352.6 / 16.0 / 23.3	115.31,93.57	-598.69,5.525,63.57	32.4
B2-007 衣料	156.7 / 6.6 / 18.3	143.44,117.70	-570.56,5.525,87.70	25.1
B2-008 生活雑貨	105.1 / 7.7 / 14.1	255.81,114.59	-458.19,5.525,84.59	16.9
B2-009 ORBIT / バッグと旅行	164.6 / 7.4 / 23.3	360.68,126.40	-353.32,5.525,96.40	12.2
B2-010 食品・カフェ	338.6 / 10.5 / 27.1	426.71,122.98	-287.29,5.525,92.98	17.6
B2-011 書籍・文具	181.0 / 10.0 / 18.3	458.80,115.83	-255.20,5.525,85.83	30.2

店舗台帳 / 4

間口は入口のある現状辺の長さ。深さはその辺からの最大法線距離。大型核・不整形区画は最大寸法の参考値。

新ID / 用途	面積㎡ / 間口m / 奥行m	入口 Local X,Z	入口 World X,Y,Z	バックルーム㎡
B2-012 LUMI / コスメとケア	149.8 / 4.9 / 18.5	184.88,54.33	-529.12,5.525,24.33	19.0
B2-013 NOVA / レディース	249.6 / 10.0 / 23.3	199.60,29.86	-514.40,5.525,-0.14	36.2
B2-014 ROOM / 寝具と暮らし	296.2 / 13.0 / 23.3	284.85,34.99	-429.15,5.525,4.99	33.9
B2-015 靴・鞄	234.1 / 7.2 / 23.3	32.32,72.06	-681.68,5.525,42.06	12.4
B2-016 食品・カフェ	166.5 / 7.5 / 23.3	153.94,76.04	-560.06,5.525,46.04	16.9
B2-017 ページの庭 / 書店・文具	162.4 / 7.5 / 22.5	224.91,79.11	-489.09,5.525,49.11	13.8
B2-018 美容・ケア	197.3 / 5.1 / 23.3	344.64,96.31	-369.36,5.525,66.31	26.5
B2-019 衣料	304.2 / 13.0 / 23.3	388.06,88.58	-325.94,5.525,58.58	29.1
B2-020 生活雑貨	256.3 / 11.0 / 23.3	123.99,104.30	-590.01,5.525,74.30	35.2
B2-021 靴・鞄	288.7 / 16.0 / 18.0	154.88,119.48	-559.12,5.525,89.48	51.2
B2-022 食品・カフェ	166.3 / 10.3 / 17.5	261.41,107.13	-452.59,5.525,77.13	17.4
B2-023 書籍・文具	215.0 / 10.0 / 23.3	365.85,133.78	-348.15,5.525,103.78	20.7
B2-024 美容・ケア	163.1 / 4.7 / 21.9	440.56,119.92	-273.44,5.525,89.92	14.1
B2-025 衣料	234.0 / 13.0 / 18.0	462.53,104.64	-251.47,5.525,74.64	41.6
B2-026 生活雑貨	343.7 / 8.7 / 23.3	186.79,40.05	-527.21,5.525,10.05	27.0
B2-027 靴・鞄	242.5 / 13.0 / 23.3	211.36,28.89	-502.64,5.525,-1.11	16.0
B2-028 食品・カフェ	178.3 / 8.5 / 18.3	289.16,45.17	-424.84,5.525,15.17	31.6
B2-029 書籍・文具	156.4 / 6.4 / 18.3	39.23,70.45	-674.77,5.525,40.45	25.0
B2-030 美容・ケア	161.8 / 3.4 / 19.6	160.71,78.40	-553.29,5.525,48.40	15.5
B2-031 衣料	206.0 / 10.0 / 20.8	233.80,77.42	-480.20,5.525,47.42	18.9
B2-032 生活雑貨	316.8 / 14.3 / 23.3	323.74,104.78	-390.26,5.525,74.78	14.8
B2-033 STEP / 靴	337.7 / 8.9 / 23.3	475.75,57.82	-238.25,5.525,27.82	32.9
B2-034 食品・カフェ	266.0 / 11.0 / 23.3	168.52,121.59	-545.48,5.525,91.59	38.4
B2-035 書籍・文具	190.1 / 7.5 / 23.3	382.56,141.94	-331.44,5.525,111.94	28.2
B2-036 美容・ケア	199.9 / 5.5 / 25.1	466.50,92.72	-247.50,5.525,62.72	13.6
B2-037 STUDIO / メンズ	243.6 / 11.0 / 20.8	194.66,49.11	-519.34,5.525,19.11	16.7
B2-038 KITCHEN LAB / キッチン用品	158.9 / 7.6 / 18.3	222.82,27.95	-491.18,5.525,-2.05	28.5

店舗台帳 / 5

間口は入口のある現状辺の長さ。深さはその辺からの最大法線距離。大型核・不整形区画は最大寸法の参考値。

新ID / 用途	面積㎡ / 間口m / 奥行m	入口 Local X,Z	入口 World X,Y,Z	バックルーム㎡
B2-039 靴・鞄	291.1 / 16.0 / 18.0	52.46,67.38	-661.54,5.525,37.38	52.2
B2-040 食品・カフェ	229.0 / 8.4 / 19.1	149.65,91.49	-564.35,5.525,61.49	22.1
B2-041 書籍・文具	255.6 / 7.7 / 23.3	337.15,110.51	-376.85,5.525,80.51	34.5
B2-042 美容・ケア	323.0 / 11.2 / 24.2	374.50,110.29	-339.50,5.525,80.29	33.9
B2-043 衣料	171.5 / 7.5 / 23.3	177.95,123.05	-536.05,5.525,93.05	16.5
B2-044 生活雑貨	168.2 / 5.1 / 23.3	389.01,140.52	-324.99,5.525,110.52	18.1
B2-045 ORBIT / バッグと旅行	313.9 / 9.2 / 23.3	231.50,27.23	-482.50,5.525,-2.77	14.4
B2-046 食品・カフェ	204.7 / 8.5 / 23.3	20.87,91.15	-693.13,5.525,61.15	28.2
B2-047 書籍・文具	152.3 / 6.6 / 17.2	158.83,94.69	-555.17,5.525,64.69	20.7
B2-048 美容・ケア	179.6 / 7.5 / 23.3	344.43,113.61	-369.57,5.525,83.61	16.2
B2-049 衣料	213.9 / 8.5 / 25.1	385.76,106.34	-328.24,5.525,76.34	19.6
B2-050 生活雑貨	195.2 / 10.0 / 23.3	186.90,124.43	-527.10,5.525,94.43	14.8
B2-051 靴・鞄	262.0 / 13.0 / 23.3	402.92,137.44	-311.08,5.525,107.44	13.6
B2-052 食品・カフェ	274.5 / 11.0 / 23.3	248.64,25.82	-465.36,5.525,-4.18	41.6
B2-053 書籍・文具	256.0 / 16.0 / 16.0	33.10,88.31	-680.90,5.525,58.31	51.2
B2-054 LUMI / コスメとケア	432.5 / 14.4 / 27.3	398.37,101.91	-315.63,5.525,71.91	32.6
B2-055 衣料	234.0 / 13.0 / 18.0	198.56,126.24	-515.44,5.525,96.24	41.6
B2-056 ROOM / 寝具と暮らし	209.2 / 7.8 / 23.3	414.07,134.98	-299.93,5.525,104.98	30.4
B2-057 靴・鞄	158.0 / 7.5 / 23.3	258.15,25.04	-455.85,5.525,-4.96	14.2
B2-058 食品・カフェ	154.0 / 11.0 / 14.0	46.54,85.18	-667.46,5.525,55.18	35.2
B2-059 書籍・文具	86.4 / 3.7 / 12.0	449.40,54.11	-264.60,5.525,24.11	23.0
B2-060 美容・ケア	214.5 / 5.6 / 23.0	210.92,128.15	-503.08,5.525,98.15	28.2
B2-061 衣料	306.0 / 16.0 / 23.3	425.97,132.36	-288.03,5.525,102.36	20.0
B2-062 生活雑貨	140.3 / 8.9 / 14.0	266.62,24.34	-447.38,5.525,-5.66	32.0
B2-063 靴・鞄	146.0 / 7.5 / 18.3	55.84,83.02	-658.16,5.525,53.02	25.2
B2-064 食品・カフェ	154.7 / 11.0 / 14.0	439.44,129.38	-274.56,5.525,99.38	35.2
B2-065 書籍・文具	154.0 / 11.0 / 14.0	225.86,36.73	-488.14,5.525,6.73	35.2

店舗台帳 / 6

間口は入口のある現状辺の長さ。深さはその辺からの最大法線距離。大型核・不整形区画は最大寸法の参考値。

新ID / 用途	面積㎡ / 間口m / 奥行m	入口 Local X,Z	入口 World X,Y,Z	バックルーム㎡
B2-066 美容・ケア	236.5 / 10.0 / 23.3	64.66,80.97	-649.34,5.525,50.97	33.0
B2-067 衣料	127.0 / 5.6 / 18.0	447.83,127.53	-266.17,5.525,97.53	22.6
B2-068 生活雑貨	146.5 / 7.5 / 21.9	235.37,35.94	-478.63,5.525,5.94	17.8
B2-069 靴・鞄	264.6 / 10.0 / 28.6	244.39,35.20	-469.61,5.525,5.20	15.1
B2-070 食品・カフェ	296.1 / 13.0 / 24.8	256.15,34.23	-457.85,5.525,4.23	13.6
B2-AW1 ホーム＆リビング	1976.6 / 18.0 / 17.0	-1.00,93.00	-715.00,5.525,63.00	172.0
B2-AE1 大型衣料	2825.0 / 12.0 / 23.0	494.00,54.00	-220.00,5.525,24.00	199.5
B3-001 キッズ	323.2 / 13.0 / 23.3	19.44,75.06	-694.56,10.875,45.06	43.2
B3-002 HOBBY BASE / 模型	196.8 / 7.5 / 23.3	141.38,71.66	-572.62,10.875,41.66	21.8
B3-003 飲食	265.4 / 11.0 / 23.0	206.88,82.52	-507.12,10.875,52.52	35.5
B3-004 体験・ゲーム	197.7 / 6.2 / 23.3	329.14,89.69	-384.86,10.875,59.69	26.8
B3-005 SOUND / 楽器	217.1 / 8.5 / 23.3	387.82,88.66	-326.18,10.875,58.66	28.2
B3-006 生活雑貨	283.8 / 11.0 / 23.3	115.63,93.96	-598.37,10.875,63.96	39.4
B3-007 キッズ	288.7 / 9.5 / 18.0	149.39,118.63	-564.61,10.875,88.63	51.2
B3-008 ホビー	150.8 / 13.4 / 14.1	258.62,110.84	-455.38,10.875,80.84	13.6
B3-009 飲食	169.7 / 5.2 / 23.4	357.99,122.54	-356.01,10.875,92.54	22.0
B3-010 体験・ゲーム	288.0 / 8.4 / 18.0	438.78,120.31	-275.22,10.875,90.31	51.2
B3-011 楽器	242.3 / 13.0 / 18.3	459.27,114.41	-254.73,10.875,84.41	41.7
B3-012 生活雑貨	310.7 / 16.0 / 22.7	185.28,51.39	-528.72,10.875,21.39	30.7
B3-013 KIDS CLOSET / こども服	284.0 / 9.3 / 23.3	202.95,29.58	-511.05,10.875,-0.42	33.9
B3-014 ホビー	206.2 / 8.5 / 23.3	283.97,32.92	-430.03,10.875,2.92	27.7
B3-015 飲食	183.1 / 8.5 / 23.3	30.20,72.55	-683.80,10.875,42.55	15.3
B3-016 体験・ゲーム	140.0 / 10.0 / 14.0	149.92,74.64	-564.08,10.875,44.64	32.0
B3-017 SOUND / 楽器	152.1 / 4.1 / 21.6	217.91,80.43	-496.09,10.875,50.43	17.8
B3-018 ACTIVE / スポーツ	292.5 / 10.0 / 23.3	336.87,92.99	-377.13,10.875,62.99	12.2
B3-019 BLOCK / おもちゃ	268.8 / 7.3 / 23.3	474.93,58.11	-239.07,10.875,28.11	35.4
B3-020 ホビー	167.2 / 7.5 / 23.3	121.63,101.38	-592.37,10.875,71.38	16.5

店舗台帳 / 7

間口は入口のある現状辺の長さ。深さはその辺からの最大法線距離。大型核・不整形区画は最大寸法の参考値。

新ID / 用途	面積㎡ / 間口m / 奥行m	入口 Local X,Z	入口 World X,Y,Z	バックルーム㎡
B3-021 飲食	271.0 / 11.0 / 23.3	159.82,120.24	-554.18,10.875,90.24	39.4
B3-022 体験・ゲーム	204.2 / 8.8 / 19.0	265.46,101.72	-448.54,10.875,71.72	20.1
B3-023 楽器	291.8 / 13.0 / 23.3	366.14,134.19	-347.86,10.875,104.19	33.6
B3-024 生活雑貨	229.2 / 10.0 / 23.3	383.78,141.67	-330.22,10.875,111.67	28.4
B3-025 キッズ	197.2 / 4.8 / 23.3	462.18,105.69	-251.82,10.875,75.69	26.4
B3-026 COLOR / 画材と文具	196.1 / 7.8 / 23.3	186.89,39.28	-527.11,10.875,9.28	27.0
B3-027 飲食	179.5 / 8.5 / 23.3	212.11,28.83	-501.89,10.875,-1.17	15.3
B3-028 体験・ゲーム	308.0 / 16.0 / 23.3	288.87,44.48	-425.13,10.875,14.48	28.9
B3-029 楽器	289.4 / 9.9 / 18.3	39.48,70.40	-674.52,10.875,40.40	47.8
B3-030 生活雑貨	269.1 / 6.6 / 22.6	158.03,77.47	-555.97,10.875,47.47	19.2
B3-031 キッズ	211.7 / 10.0 / 23.3	225.15,79.06	-488.85,10.875,49.06	20.2
B3-032 ホビー	288.0 / 8.6 / 18.0	312.39,99.94	-401.61,10.875,69.94	51.2
B3-033 SWEET / デザートカフェ	214.9 / 8.0 / 24.0	375.82,109.82	-338.18,10.875,79.82	24.5
B3-034 体験・ゲーム	227.2 / 10.0 / 23.3	127.32,108.42	-586.68,10.875,78.42	28.7
B3-035 楽器	171.5 / 7.5 / 23.3	169.26,121.70	-544.74,10.875,91.70	16.5
B3-036 生活雑貨	252.4 / 13.0 / 23.3	395.30,139.13	-318.70,10.875,109.13	26.3
B3-037 キッズ	140.5 / 4.6 / 18.3	194.35,51.39	-519.65,10.875,21.39	22.9
B3-038 HOBBY BASE / 模型	290.8 / 16.0 / 18.3	224.62,27.80	-489.38,10.875,-2.20	49.2
B3-039 飲食	327.7 / 8.1 / 23.3	20.66,91.20	-693.34,10.875,61.20	29.1
B3-040 体験・ゲーム	199.3 / 8.5 / 23.0	171.50,82.17	-542.50,10.875,52.17	28.5
B3-041 楽器	359.0 / 13.0 / 34.5	236.75,76.86	-477.25,10.875,46.86	22.7
B3-042 生活雑貨	264.8 / 11.0 / 23.3	328.47,106.81	-385.53,10.875,76.81	38.4
B3-043 キッズ	383.9 / 16.0 / 26.0	387.88,105.59	-326.12,10.875,75.59	31.8
B3-044 ホビー	212.4 / 10.0 / 23.3	178.20,123.08	-535.80,10.875,93.08	20.9
B3-045 飲食	198.1 / 7.9 / 23.3	406.37,136.68	-307.63,10.875,106.68	27.2
B3-046 PLAY / ゲームコーナー	321.9 / 6.5 / 36.0	195.55,42.40	-518.45,10.875,12.40	15.8
B3-047 楽器	256.3 / 11.0 / 23.3	238.37,26.67	-475.63,10.875,-3.33	35.2

店舗台帳 / 8

間口は入口のある現状辺の長さ。深さはその辺からの最大法線距離。大型核・不整形区画は最大寸法の参考値。

新ID / 用途	面積㎡ / 間口m / 奥行m	入口 Local X,Z	入口 World X,Y,Z	バックルーム㎡
B3-048 生活雑貨	203.2 / 8.7 / 23.3	39.10,86.91	-674.90,10.875,56.91	14.3
B3-049 キッズ	163.1 / 5.5 / 19.1	143.96,89.51	-570.04,10.875,59.51	16.8
B3-050 ホビー	168.1 / 8.5 / 20.6	223.46,95.67	-490.54,10.875,65.67	19.0
B3-051 飲食	168.5 / 7.5 / 23.3	337.26,110.55	-376.74,10.875,80.55	16.5
B3-052 体験・ゲーム	324.8 / 11.0 / 27.8	400.90,101.03	-313.10,10.875,71.03	33.4
B3-053 楽器	264.1 / 13.0 / 23.3	189.86,124.89	-524.14,10.875,94.89	16.0
B3-054 生活雑貨	256.0 / 9.2 / 16.0	415.05,134.77	-298.95,10.875,104.77	51.2
B3-055 キッズ	146.8 / 4.8 / 23.3	246.55,25.99	-467.45,10.875,-4.01	14.7
B3-056 ホビー	137.2 / 7.5 / 18.3	47.27,85.01	-666.73,10.875,55.01	24.0
B3-057 飲食	217.8 / 9.7 / 23.3	345.46,114.05	-368.54,10.875,84.05	20.4
B3-058 STORY / 児童書	177.0 / 7.5 / 24.7	409.92,97.87	-304.08,10.875,67.87	15.5
B3-059 楽器	226.1 / 8.5 / 23.3	200.78,126.58	-513.22,10.875,96.58	31.4
B3-060 COLOR / 画材と文具	186.4 / 6.4 / 16.3	434.06,130.57	-279.94,10.875,100.57	30.2
B3-AW1 シネマ・星あかり	1976.6 / 18.0 / 17.0	-1.00,93.00	-715.00,10.875,63.00	172.0
B3-AE1 フードホール	2910.8 / 12.0 / 23.0	494.00,54.00	-220.00,10.875,24.00	200.0