

A館1F A1F-002 SUVEL STUDIO / 売場5558.4㎡

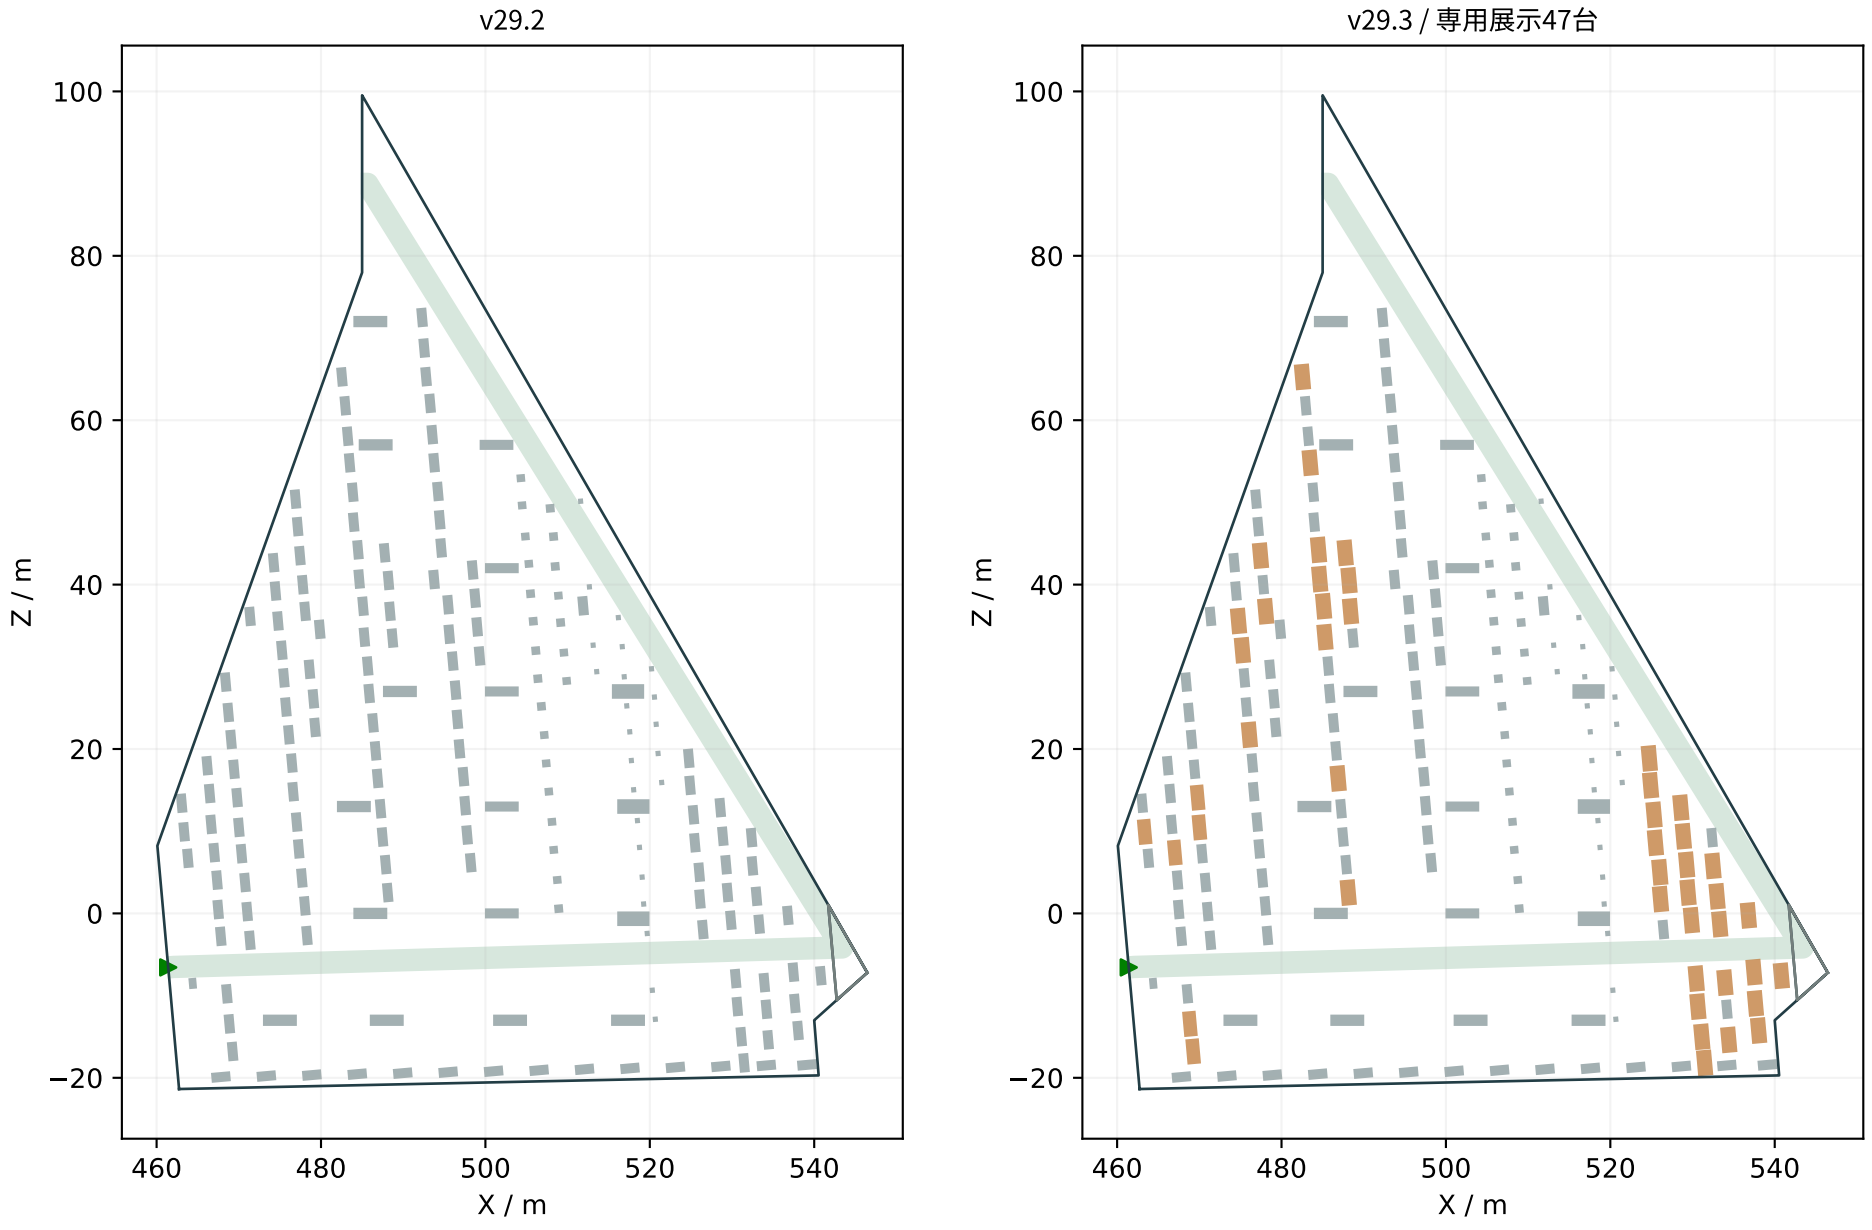

橙：今回の置換展示 灰：その他の台帳什器 緑：既存保護通路
躯体・入口・店舗区画は変更なし。旧ベイク済み家具は本図の集計に含まれないため、完成配置図ではありません。

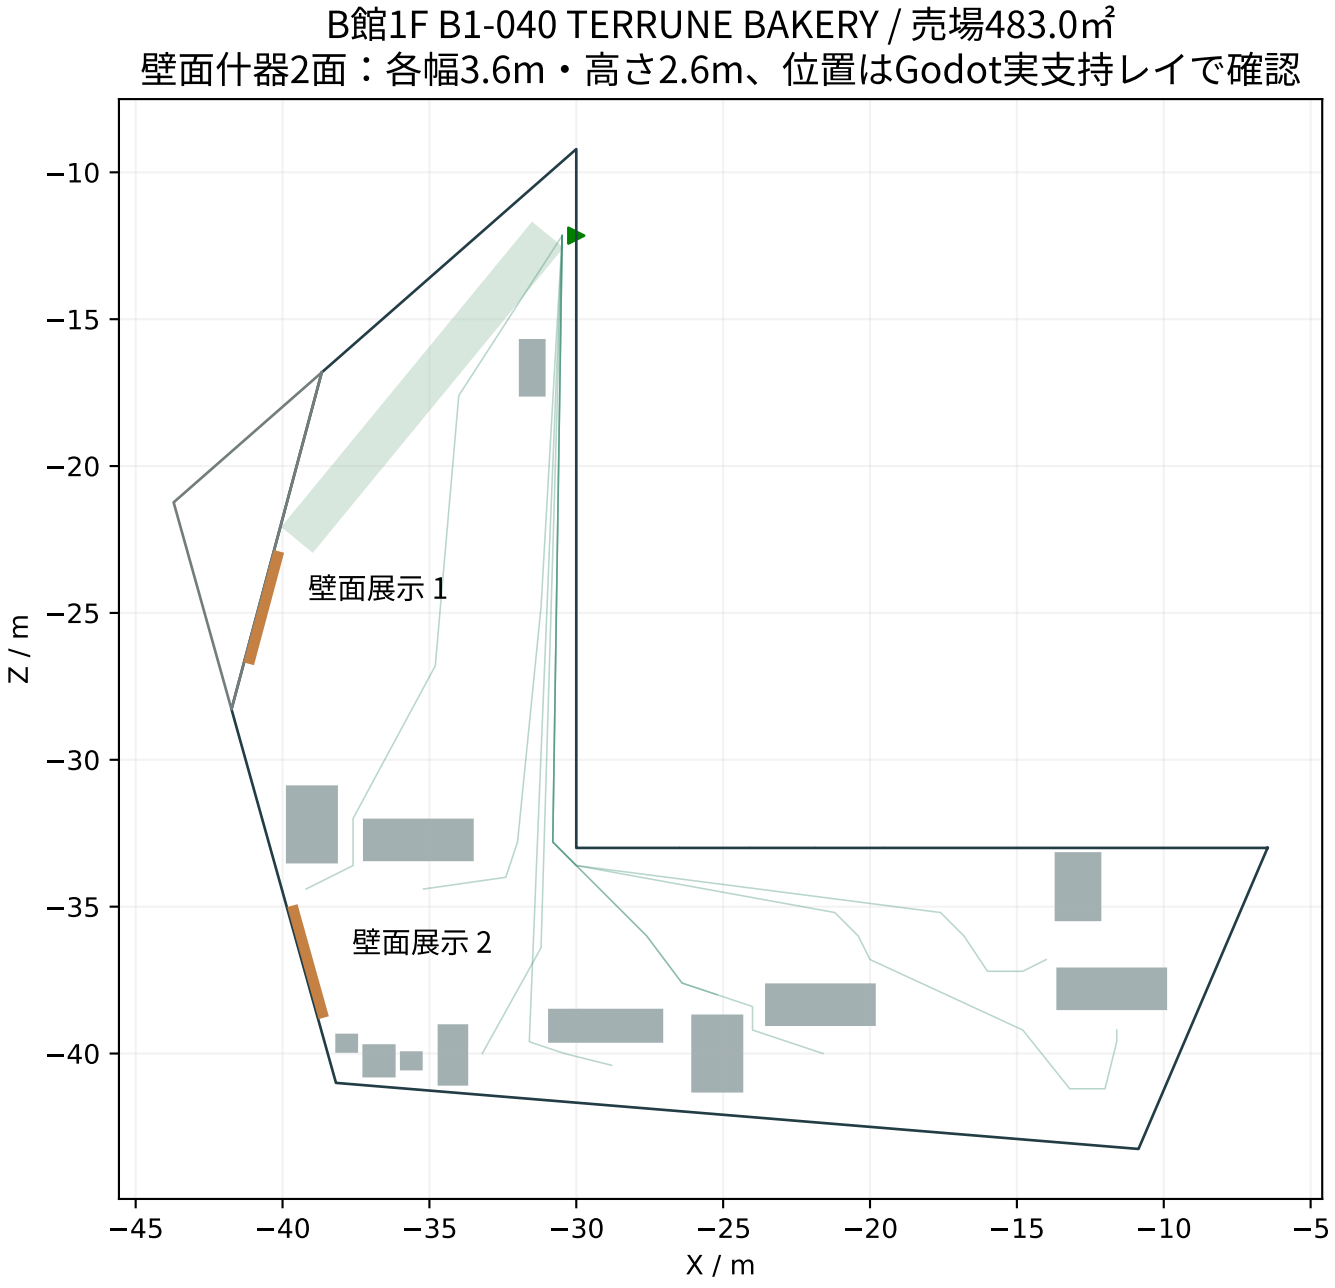

緑線：既存の店内確認経路（自動物理検査）。人間の実操作ではありません。
躯体・壁・客席・レジ・バックヤードの変更なし。旧ベイク済み家具は台帳図だけでは全てを表示していません。