FIND YOURSELF｜3館・駐車場・15層 詳細設計補完 v2

ユーザー確認用。A/C内部案とB館v4.1の1〜3Fを保存し、敷地計画・B1/RF・面積監査を追加。

図形として数えた駐車マスは合計 6,699台。外部6,369台＋既存A西22台＋B館B1 193台＋B館RF115台です。立体駐車場の屋上段を二重加算していません。

本資料には全15層の上面図と拡大図、3館全体配置、来客/搬入/歩行の区分、駐車場台帳、B館地下/屋上、C館面積の排他的集計を収録します。

承認が必要な局所案：A2Fの新到着口2か所、B1Fの翼広場南新到着口1か所、およびA/Bの既存階段・EV床開口。元のゲーム/原図データへは一切適用していません。

独立再検査では、固定したB館v4.1の1〜3Fに65件の微小不整合（店舗間56件・店舗/共用3件・入口座標6件）が残っています。原図を変更せず、局所修正案と案の再検査を別紙にしました。

今回の検査は設計ポリゴン上の重なり/接続/寸法です。実歩行、実車、NPCの経路、衝突、構造荷重、排水、法規、交通容量は未検証です。ゲーム完成や安全審査済みの図面として扱わないでください。

実在施設を参考にしたゲーム用オリジナル計画です。寸法・駐車台数・敷地境界はゲーム用設計値で、イオンレイクタウンの実測値ではありません。

図面の読み方・固定範囲・承認条件

緑=公開歩行／薄茶=店舗／濃灰=バックルーム／青=駐車・歩道橋／赤=開口・未適用局所案

15層＝A/B/CそれぞれB1・1F・2F・3F・RF。外部立体の中間駐車段は15層に混ぜず、別冊の17駐車面で扱います。

基準階高：B1 -5.350m、1F 0m、2F +5.525m、3F +10.875m、RF +16.400m。B1↔1Fと3F↔RFの追加エスカレーターは既存3対の平面位置を上下に積層し、既存B1〜3Fの開口拡張を要求しません。

新到着口3か所は既存店舗/設備核との重なり0㎡を検査し、原通路に接続する局所案を赤で示します。原図は未変更なので、これらの駐車場→店舗街の最終接続は承認を条件とします。

既存A/Bの設備核は、室割りの記号上は階段・EVがあっても構造床に穴が含まれていません。今回の床開口追加案を別JSON/CSVで提示します。C館のEV内法・階段開口は既存の設計を維持します。

図面の拡大率は閲覧環境に依存するため、印刷縮尺を断定せず、世界座標のグリッドとメートル尺度を示します。全店舗のID・入口・バックルーム・内部主路は原データに沿って描画。

敷地全体配置｜建物・駐車場・道路・歩道橋

灰=来客車／茶=搬入専用／緑=地上歩行／青=立体横断。白地は周辺街区未設計、外接矩形を敷地面積に算入しません。

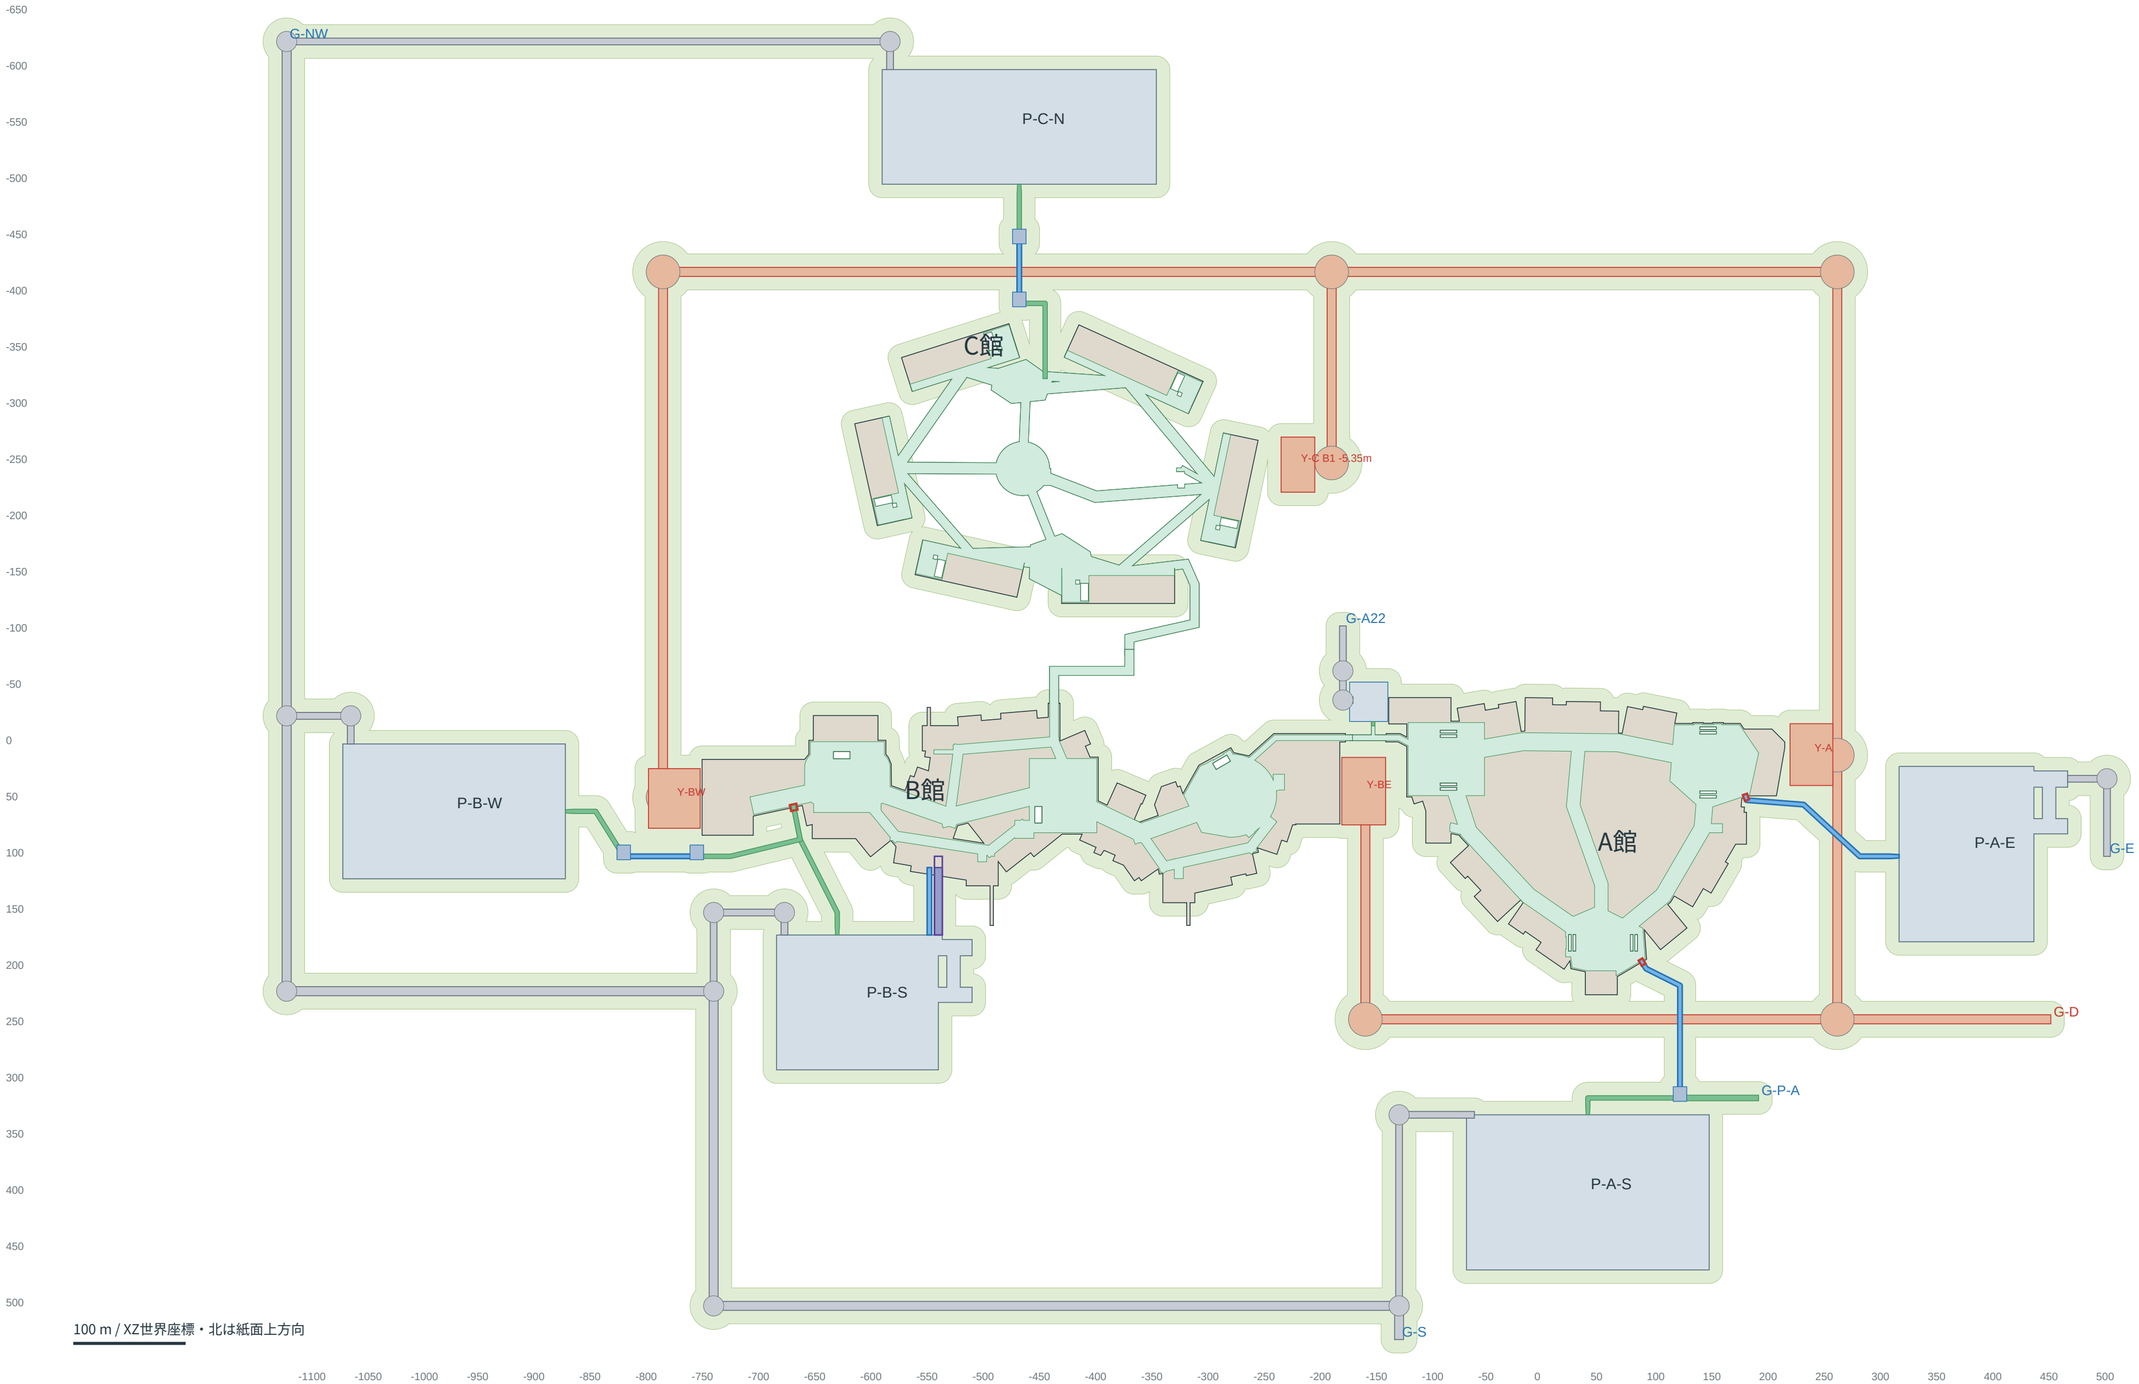

計画投影和集合 315,601.0㎡ / 排水・植栽管理帯 273,070.0㎡ / 合計 588,671.0㎡

敷地拡大｜A館周辺・東立体・南平面

車路は駐車入口/搬入口にだけ接続。各経路のIDと座標列はroad-path-register.csv。

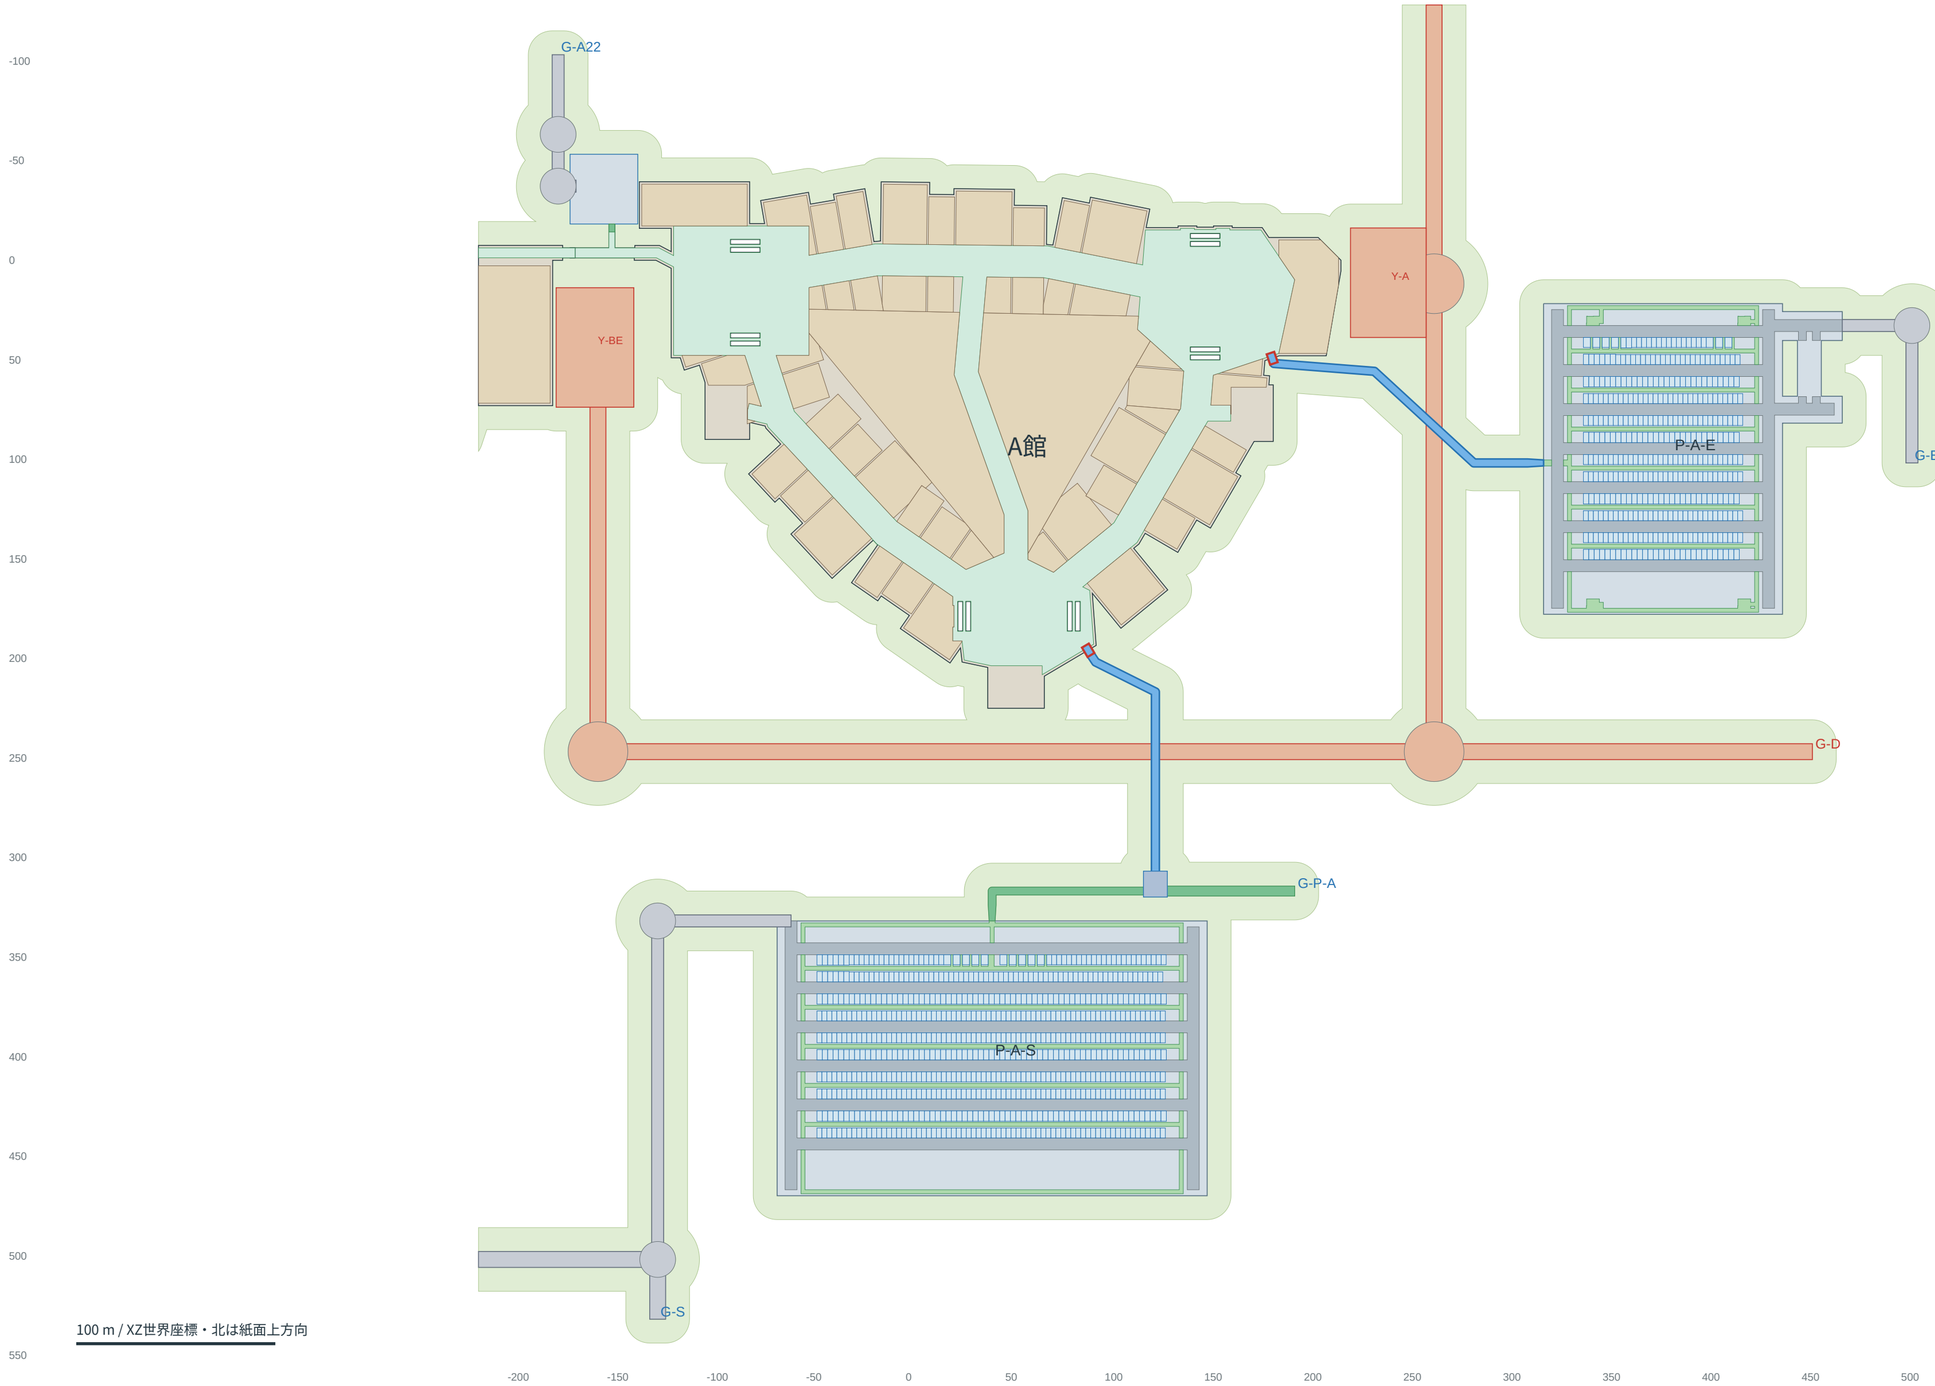

敷地拡大｜B館周辺・西平面・南立体

車路は駐車入口/搬入口にだけ接続。各経路のIDと座標列はroad-path-register.csv。

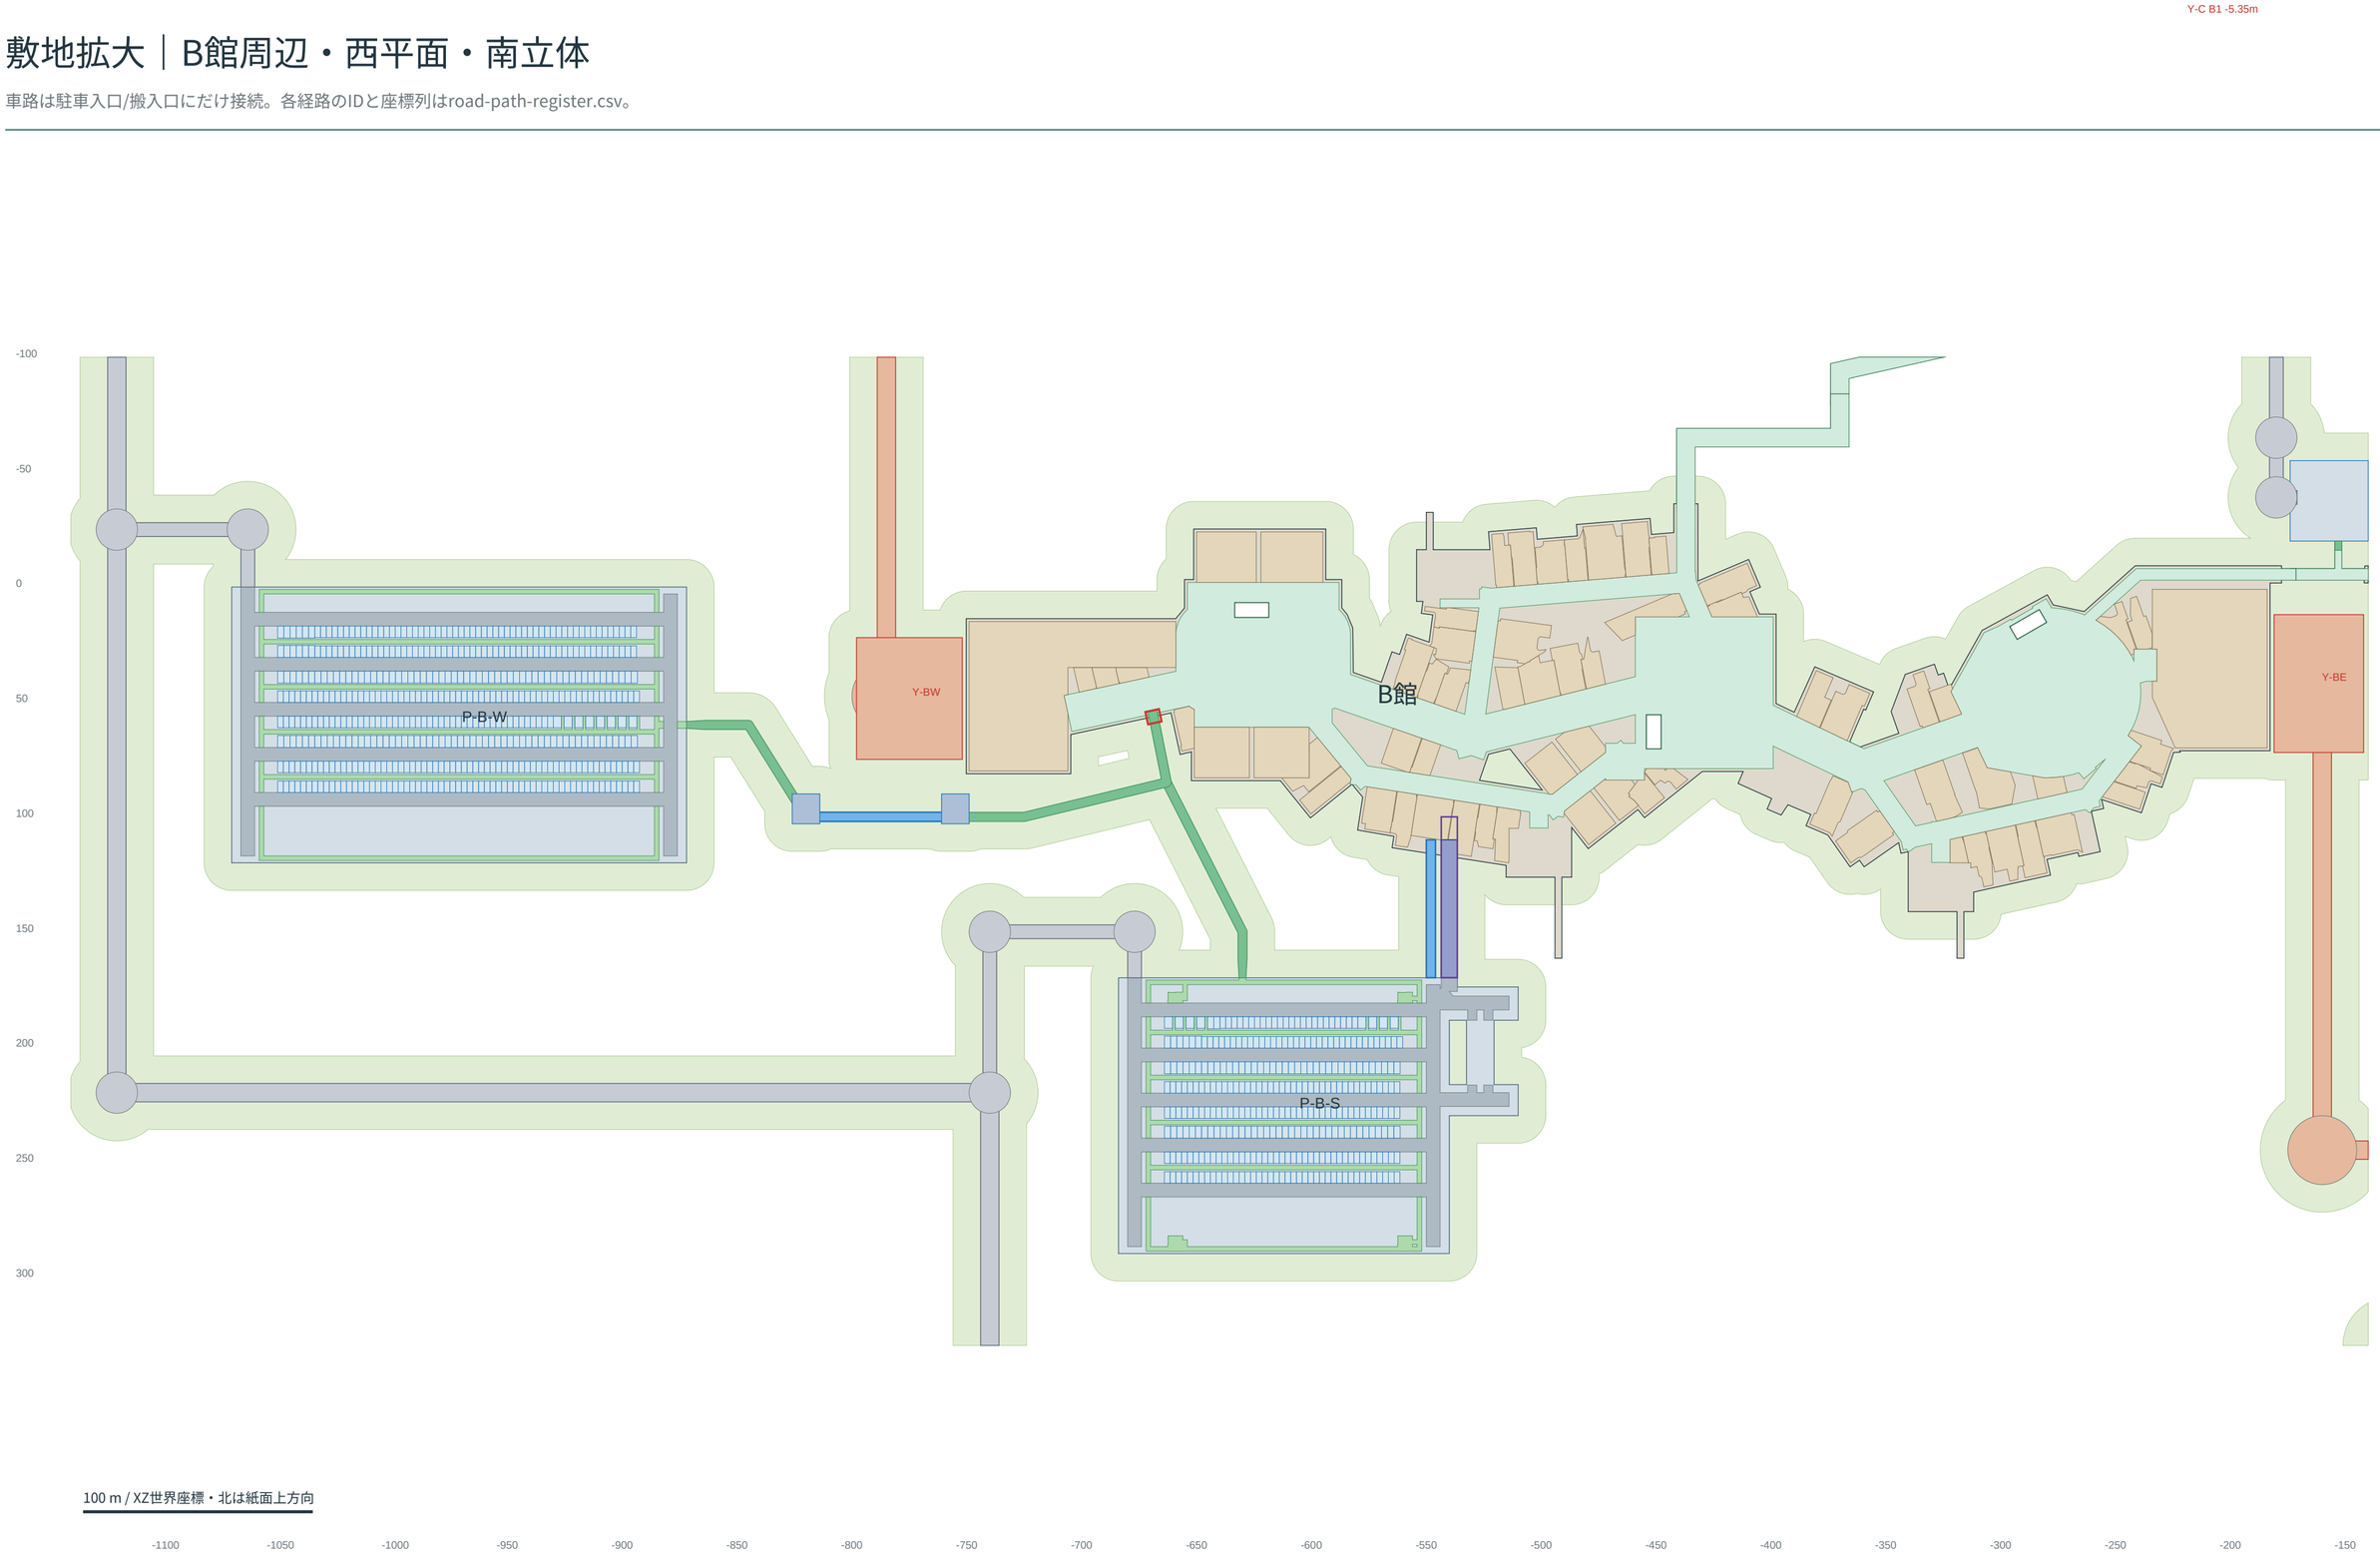

敷地拡大｜C館周辺・北平面

車路は駐車入口/搬入口にだけ接続。各経路のIDと座標列はroad-path-register.csv。

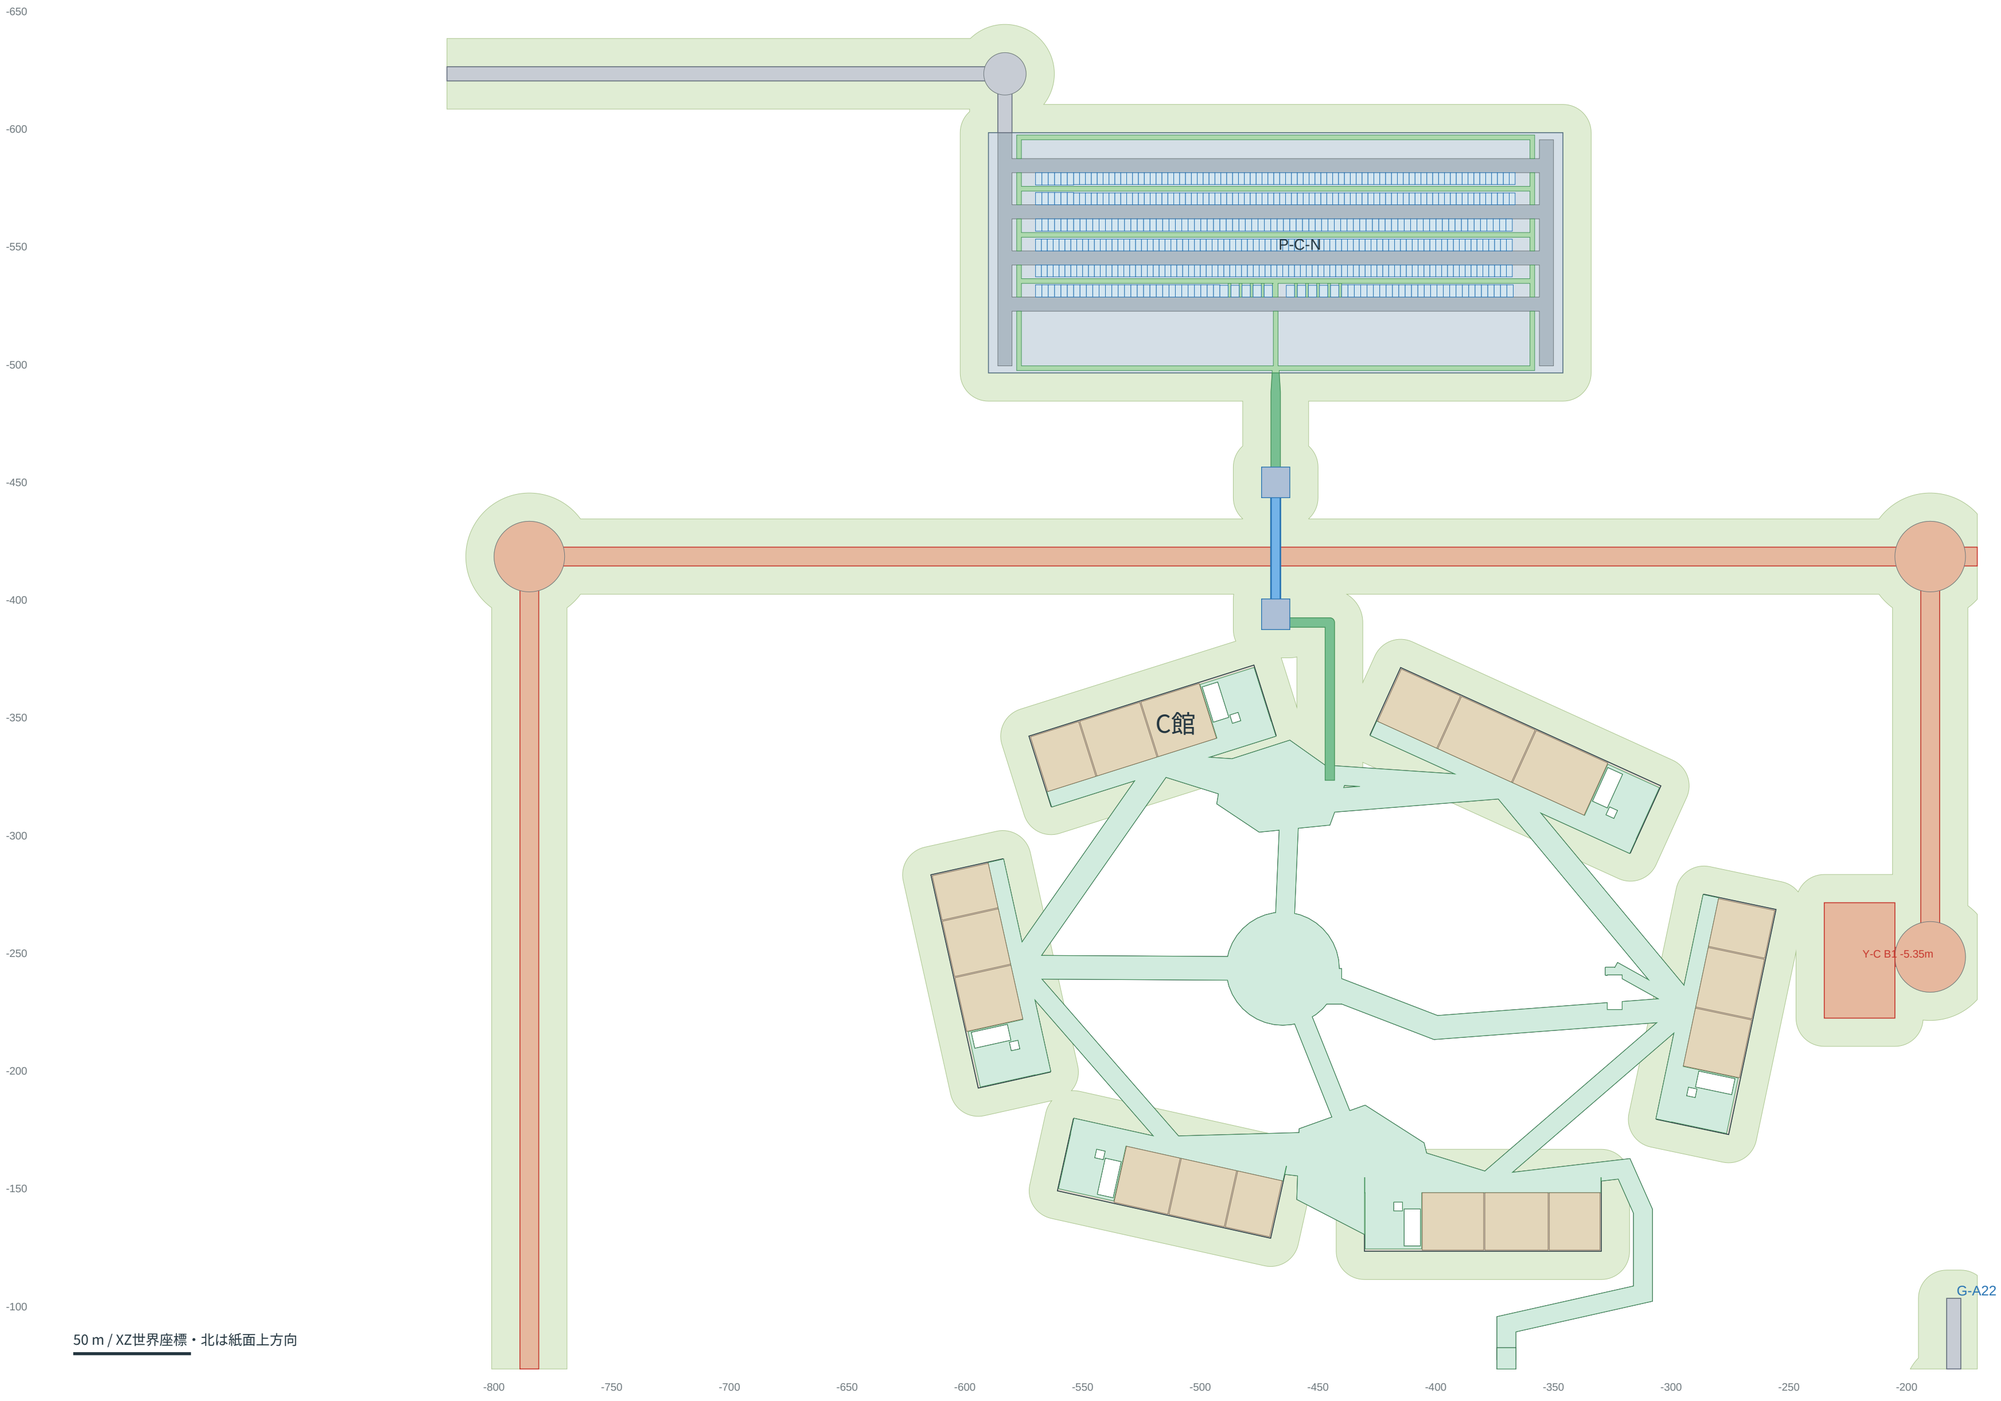

駐車台数・用途別台帳｜全8施設

一般/ゆとり/身障者用/EV/職員は同じマスの用途区分です。別枠容量として重複加算しません。

施設	駐車面数	一般	ゆとり	身障者	EV	職員	合計
P-A-E	7	1582	812	49	56	42	2541
P-A-OLD22	1	22	0	0	0	0	22
P-A-S	1	450	195	10	12	6	673
P-B-B1	1	166	0	3	9	15	193
P-B-RF	1	99	0	3	5	8	115
P-B-S	7	1477	532	56	56	84	2205
P-B-W	1	337	116	8	12	12	485
P-C-N	1	306	131	10	12	6	465

合計 6,699台 / 1マス1ID / 既存A西22台を含む

外部の各駐車面・全マス番号・斜路・保護歩道・コアは別冊35ページに収録。B館地下/屋上と既存A西22台は本資料の図面および全体台帳に収録。

容量の妥当性は巨大モールを想定したゲーム設計です。来客数・自動車分担率・ピーク回転率を使った需要予測や実際の交通処理能力は未検証です。

15層の寸法・用途・区画数一覧

外接寸法はshell投影のX/Z範囲。公開床と躯体投影を加算しません。RFの庭・公開床・空調保守は別用途。

館/階	高さm	外接X×Z寸法m	shell㎡	公開床㎡	店舗/施設区画		
A B1	-5.350	352.4 x 264.4	53,092.5	20,966.6	31		
A 1F	+0.000	387.2 x 264.4	57,606.7	21,021.2	52		
A 2F	+5.525	355.0 x 264.4	57,167.3	18,408.6	52		
A 3F	+10.875	352.4 x 264.4	57,150.5	18,310.5	51		
A RF	+16.400	352.4 x 264.4	57,168.7	47,207.0	15		
B B1	-5.350	572.5 x 177.5	53,759.8	3,196.0	2		
B 1F	+0.000	572.5 x 177.5	53,759.8	23,262.8	65		
B 2F	+5.525	572.5 x 177.5	53,759.8	18,749.3	66		
B 3F	+10.875	572.5 x 177.5	53,759.8	17,663.2	57		
B RF	+16.400	572.5 x 177.5	53,759.8	2,556.6	1		
C B1	-5.350	410.1 x 249.6	35,210.5	20,057.1	18		
C 1F	+0.000	359.0 x 248.9	18,953.0	21,418.4	18		
C 2F	+5.525	359.0 x 248.9	18,953.0	12,020.6	18		
C 3F	+10.875	359.0 x 248.9	18,953.0	11,162.8	18		
C RF	+16.400	359.0 x 248.9	18,953.0	16,923.9	6		

B館B1：地下食品/受取2区画＋193台＋共同倉庫/受変電/ポンプ・空調保守。RF：カフェ1区画＋115台＋3光庭前庭＋PV/空調保守。保守ベイは商業店舗数に含めません。

この一覧のA/C区画には地下や屋上の施設区画も含みます。純粋な専門店数と同義ではありません。C1Fのshellは独立6棟の投影であり、屋外床を除きます。

A館 B1｜詳細平面図 全体

既存内部形状を維持 / Y=-5.350m / 区画数 31 / 入口緑線・主路青線・バックルーム灰。赤の局所案は未適用。

A館 B1｜詳細拡大 1/2

入口幅・売場主路・バックルーム・設備室を原ポリゴンで表示 / 範囲X -143.2〜41.0m

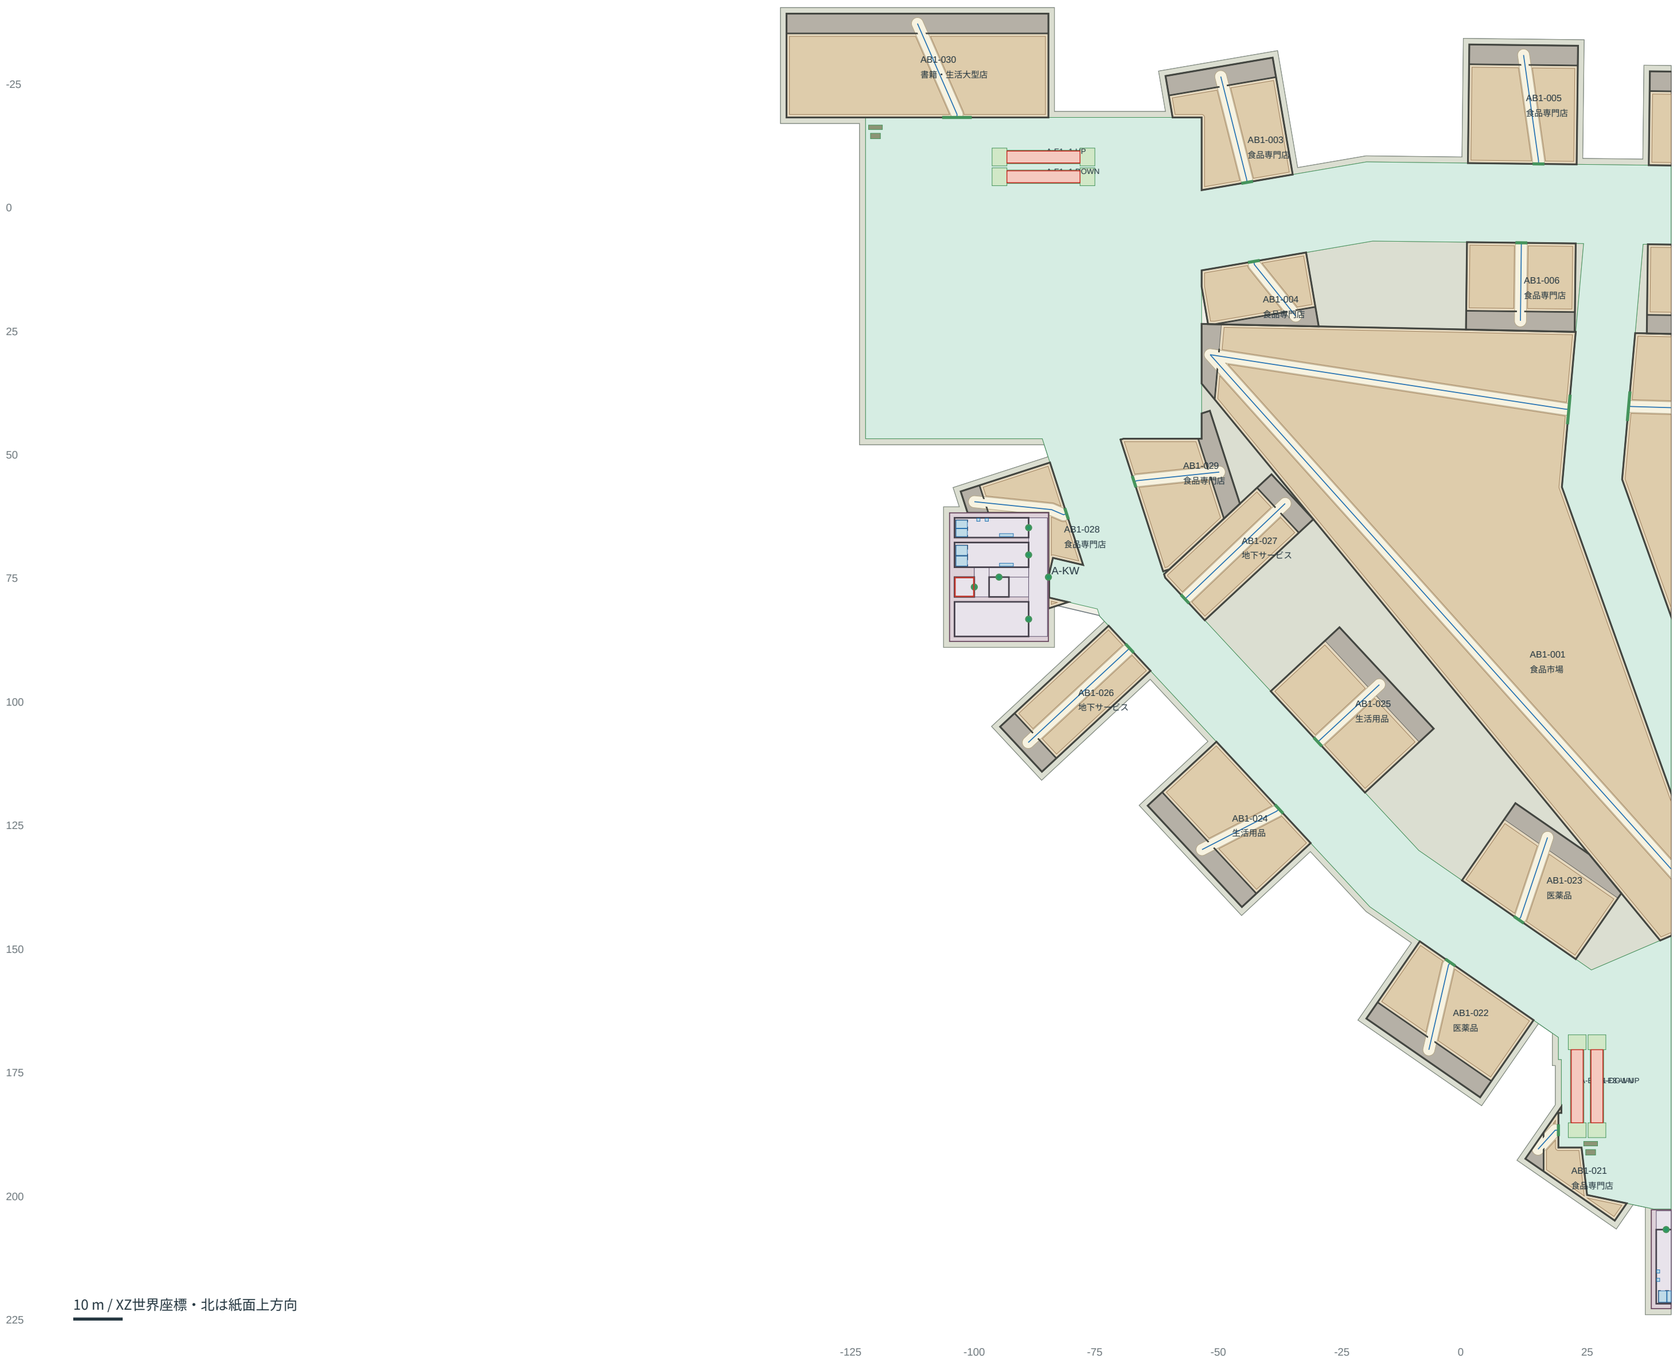

A館 B1｜詳細拡大 2/2

入口幅・売場主路・バックルーム・設備室を原ポリゴンで表示 / 範囲X 33.0〜217.2m

A館 1F｜詳細平面図 全体

既存内部形状を維持 / Y=+0.000m / 区画数 52 / 入口緑線・主路青線・バックルーム灰。赤の局所案は未適用。

A館 1F｜詳細拡大 1/2

入口幅・売場主路・バックルーム・設備室を原ポリゴンで表示 / 範囲X -178.0〜23.6m

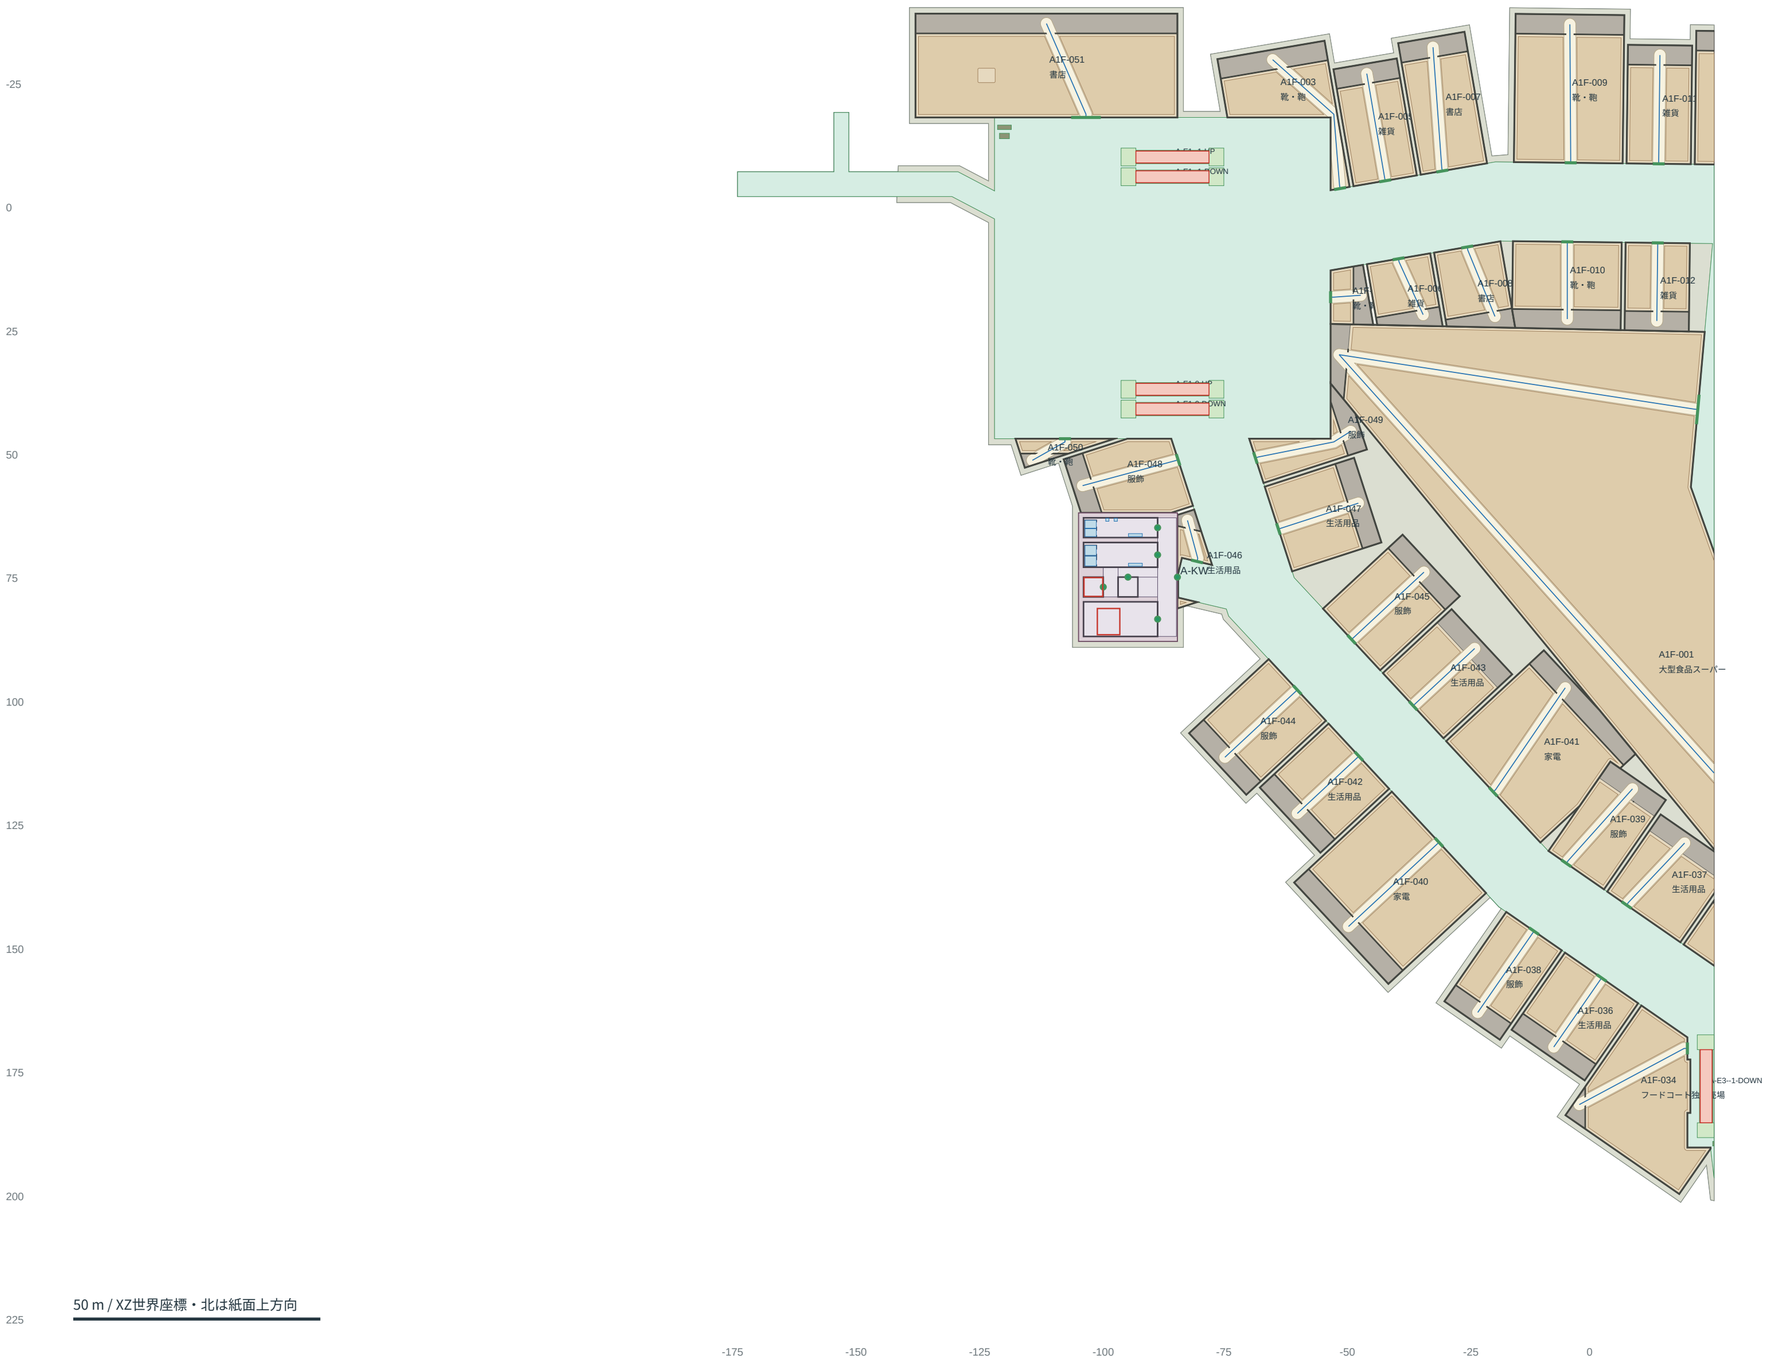

50 m / XZ世界座標・北は紙面上方向

A館 1F｜詳細拡大 2/2

入口幅・売場主路・バックルーム・設備室を原ポリゴンで表示 / 範囲X 15.6〜217.2m

A館 2F｜詳細平面図 全体

既存内部形状を維持 / Y=+5.525m / 区画数 52 / 入口緑線・主路青線・バックルーム灰。赤の局所案は未適用。

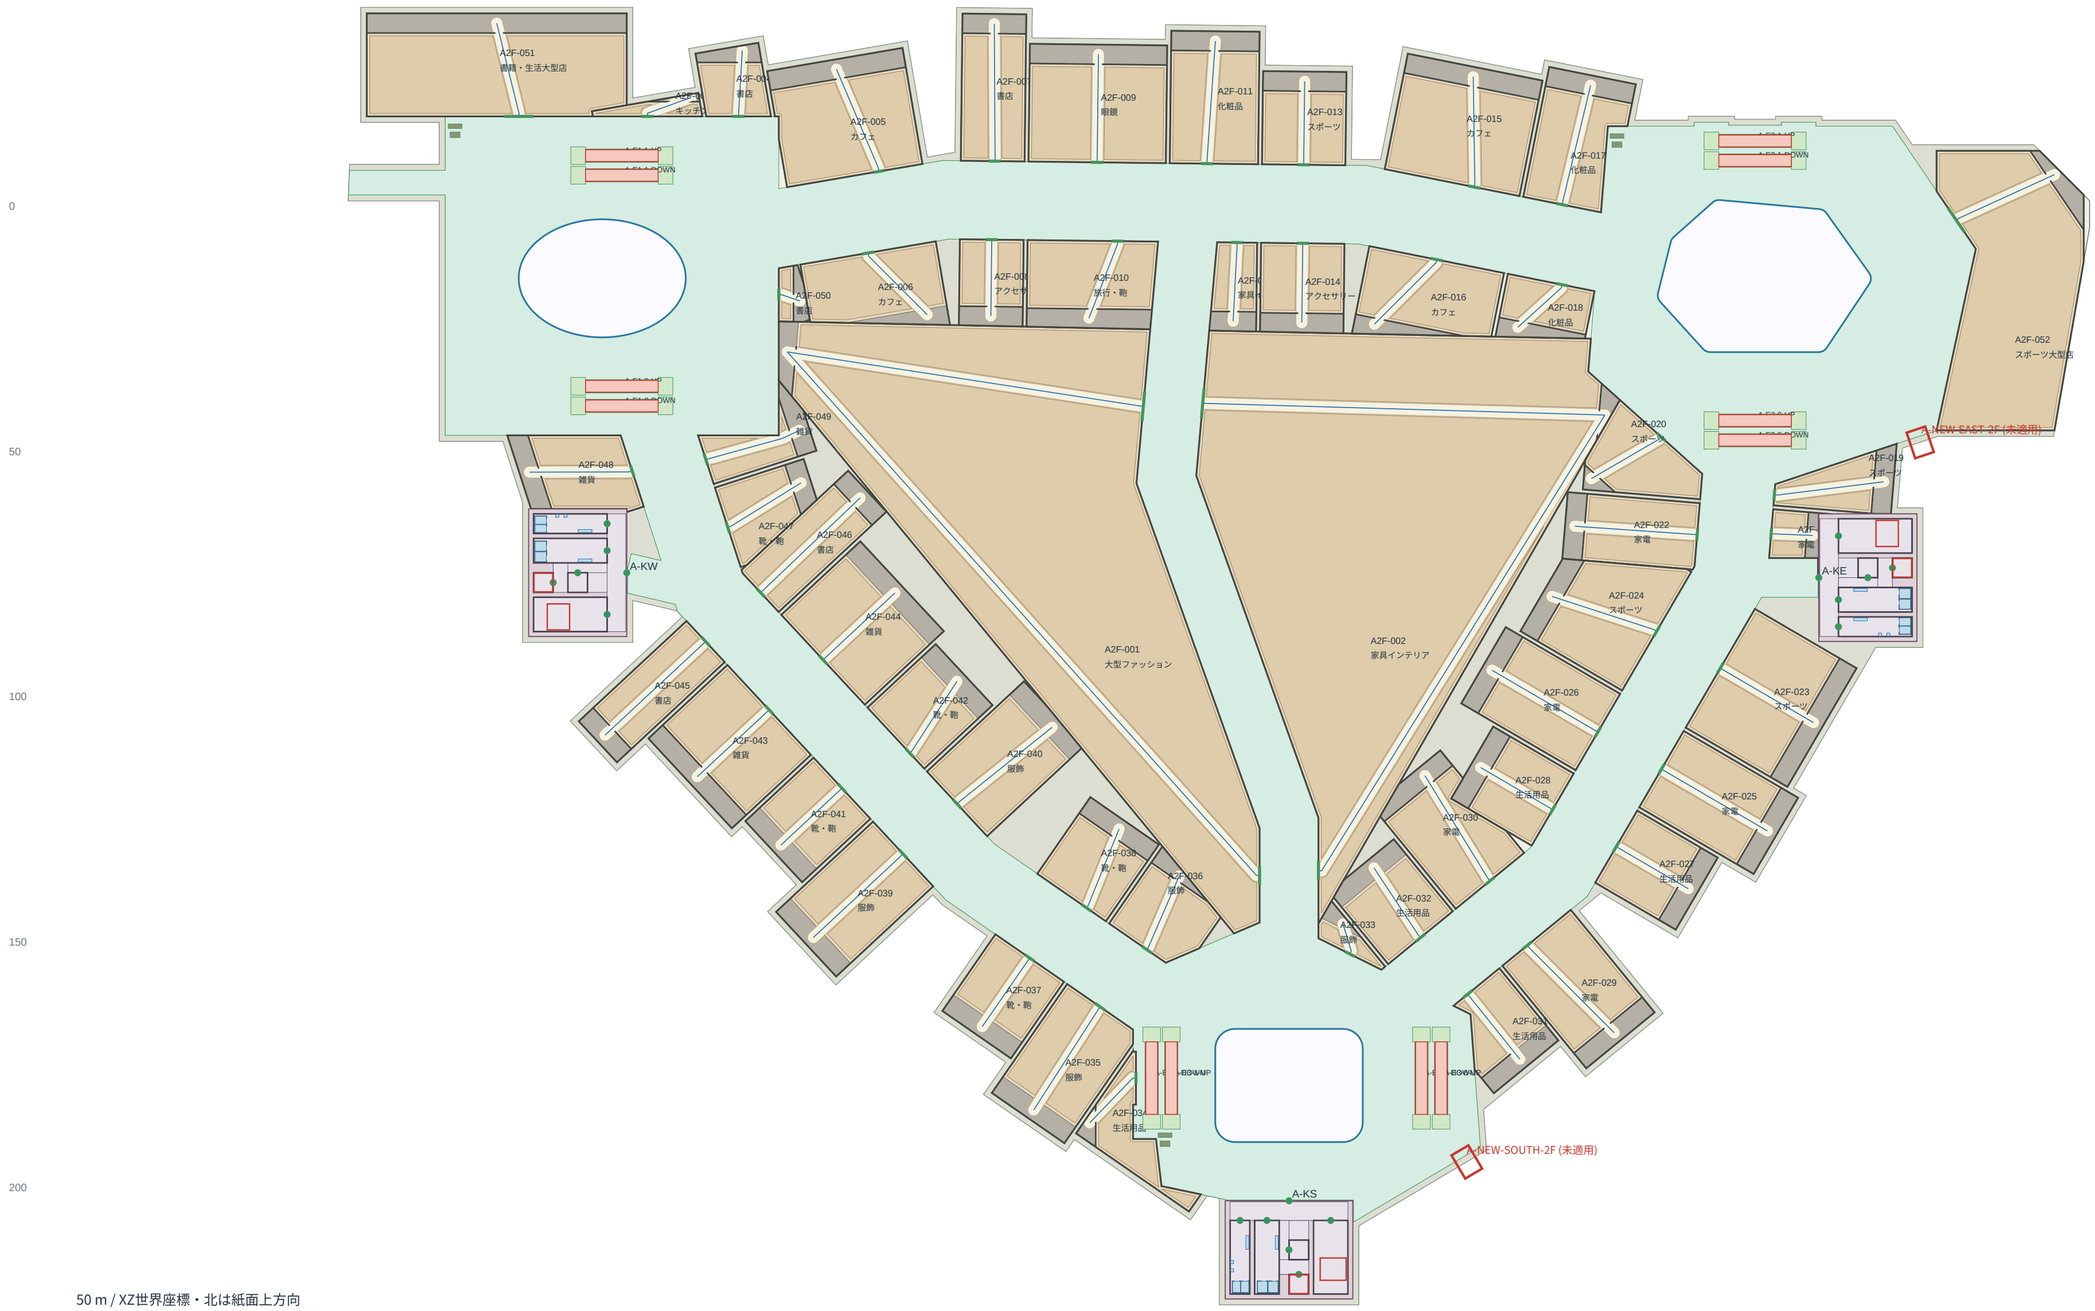

A館 2F｜詳細拡大 1/2

入口幅・売場主路・バックルーム・設備室を原ポリゴンで表示 / 範囲X -145.8〜39.7m

A館 2F｜詳細拡大 2/2

入口幅・売場主路・バックルーム・設備室を原ポリゴンで表示 / 範囲X 31.7〜217.2m

A館 3F｜詳細平面図 全体

既存内部形状を維持 / Y=+10.875m / 区画数 51 / 入口緑線・主路青線・バックルーム灰。赤の局所案は未適用。

A館 3F｜詳細拡大 1/2

入口幅・売場主路・バックルーム・設備室を原ポリゴンで表示 / 範囲X -143.2〜41.0m

10 m / XZ世界座標・北は紙面上方向

A館 3F｜詳細拡大 2/2

入口幅・売場主路・バックルーム・設備室を原ポリゴンで表示 / 範囲X 33.0〜217.2m

A館 RF｜詳細平面図 全体

既存内部形状を維持 / Y=+16.400m / 区画数 15 / 入口緑線・主路青線・バックルーム灰。赤の局所案は未適用。

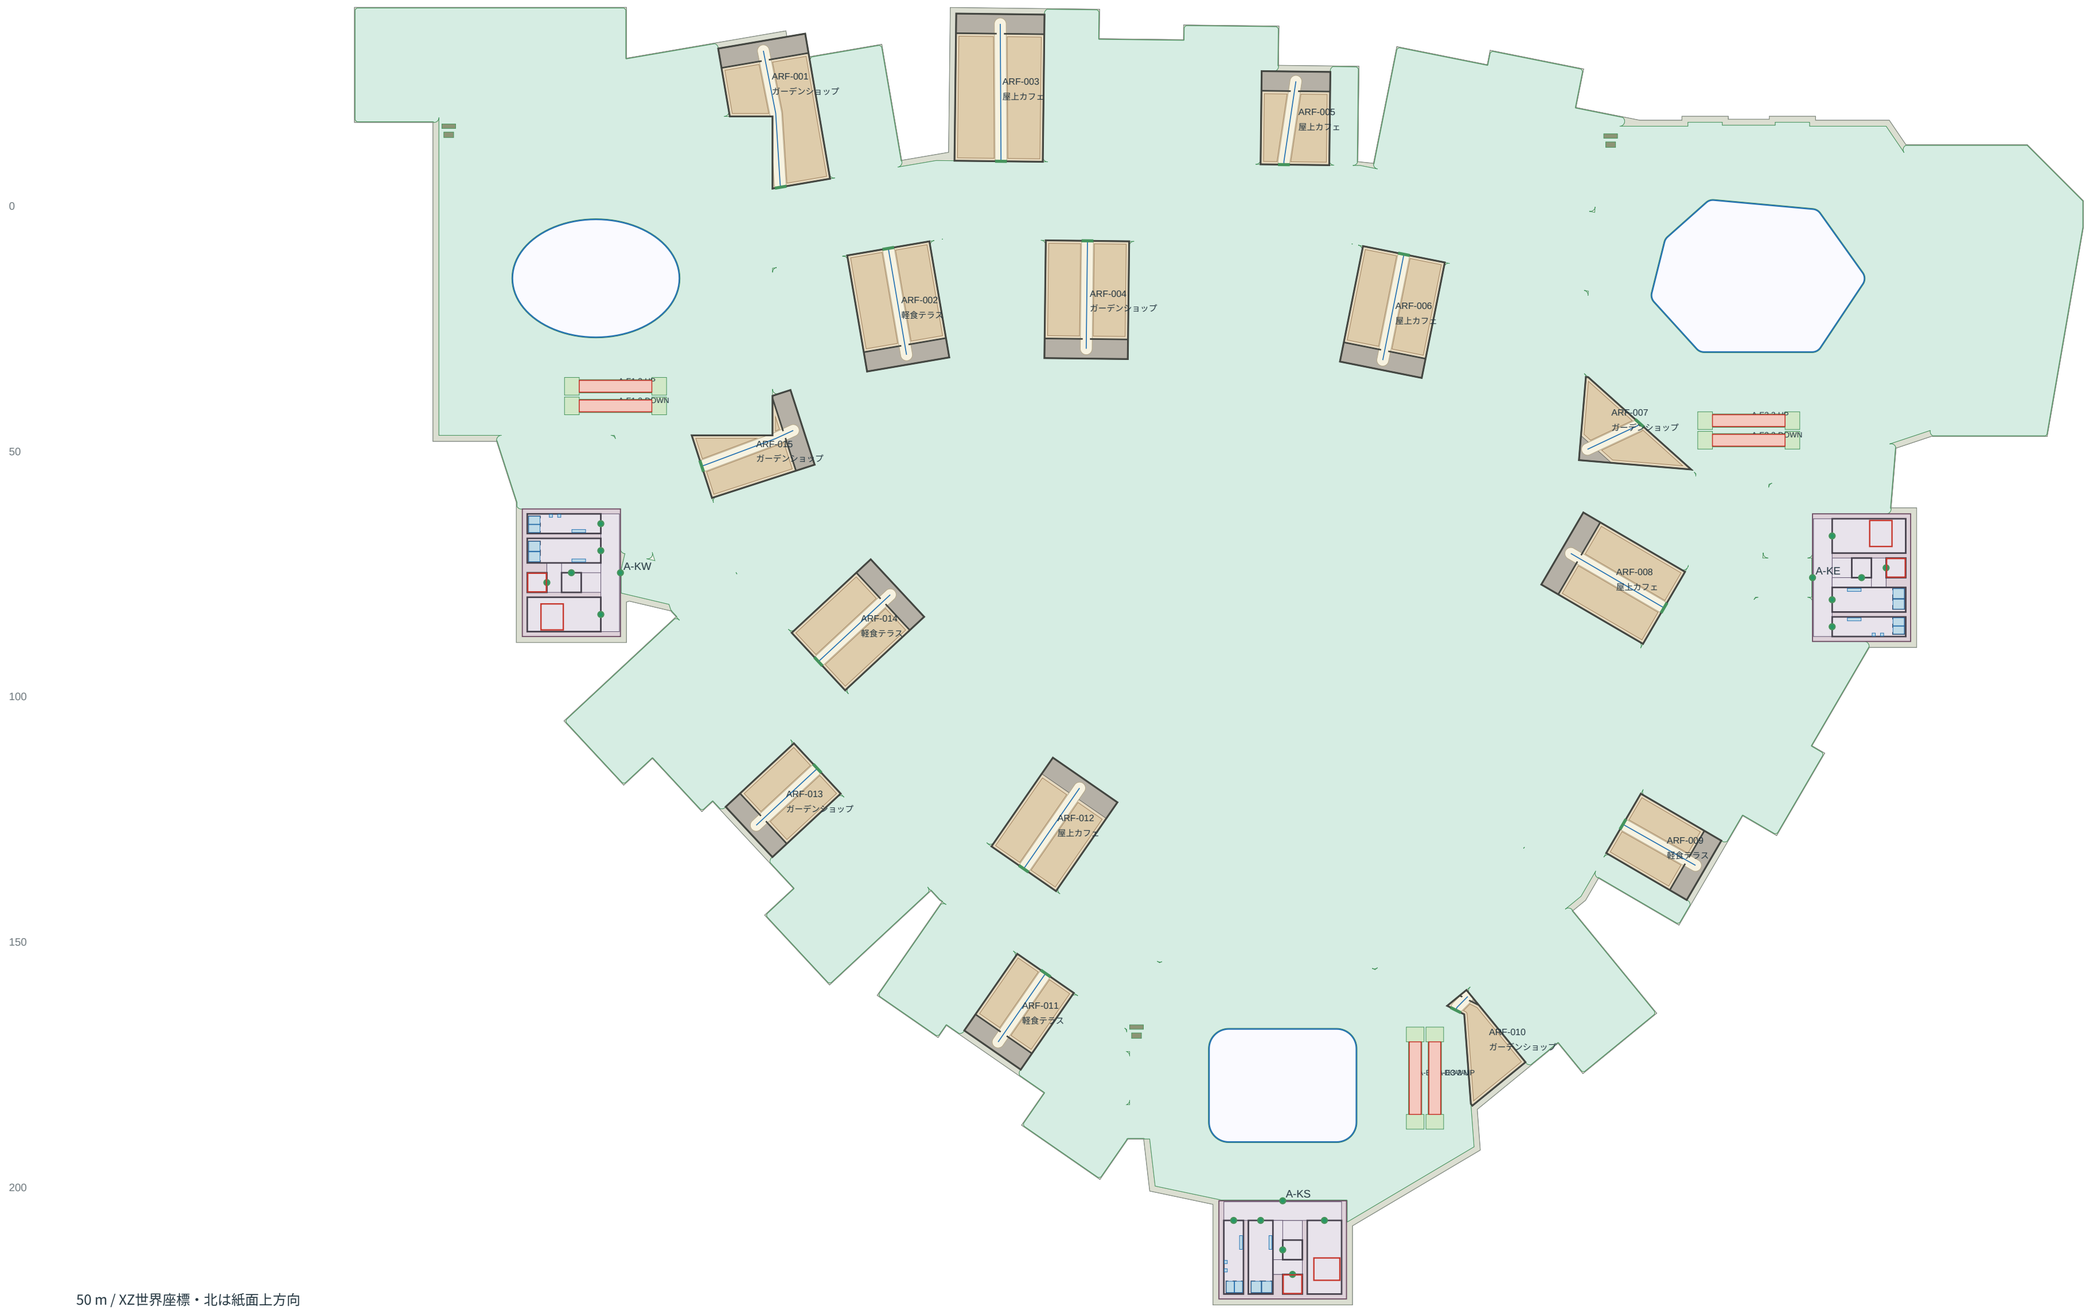

A館 RF｜詳細拡大 1/2

入口幅・売場主路・バックルーム・設備室を原ポリゴンで表示 / 範囲X -143.2〜41.0m

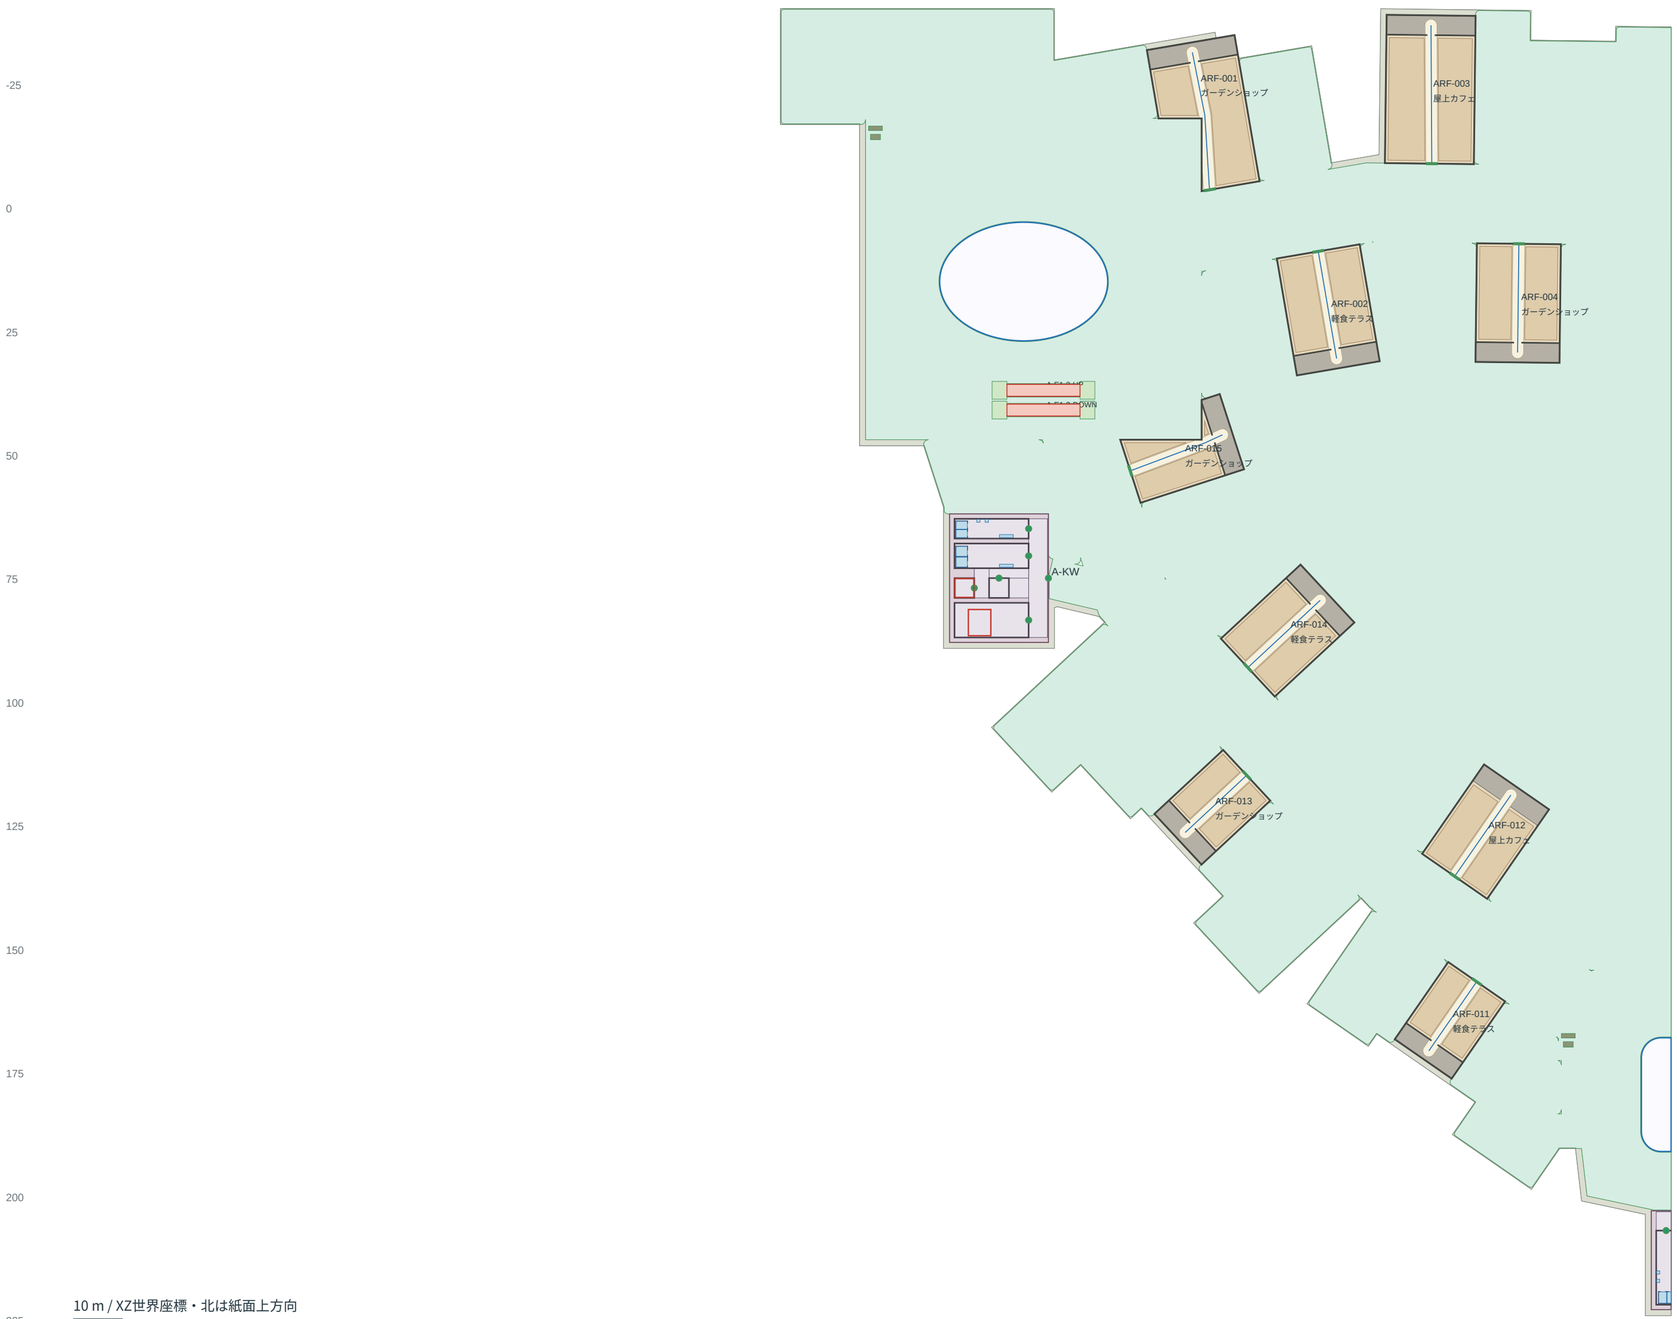

A館 RF｜詳細拡大 2/2

入口幅・売場主路・バックルーム・設備室を原ポリゴンで表示 / 範囲X 33.0〜217.2m

B館 B1｜詳細平面図 全体

今回新設計 / Y=-5.350m / 区画数 2 / 入口緑線・主路青線・バックルーム灰。赤の局所案は未適用。

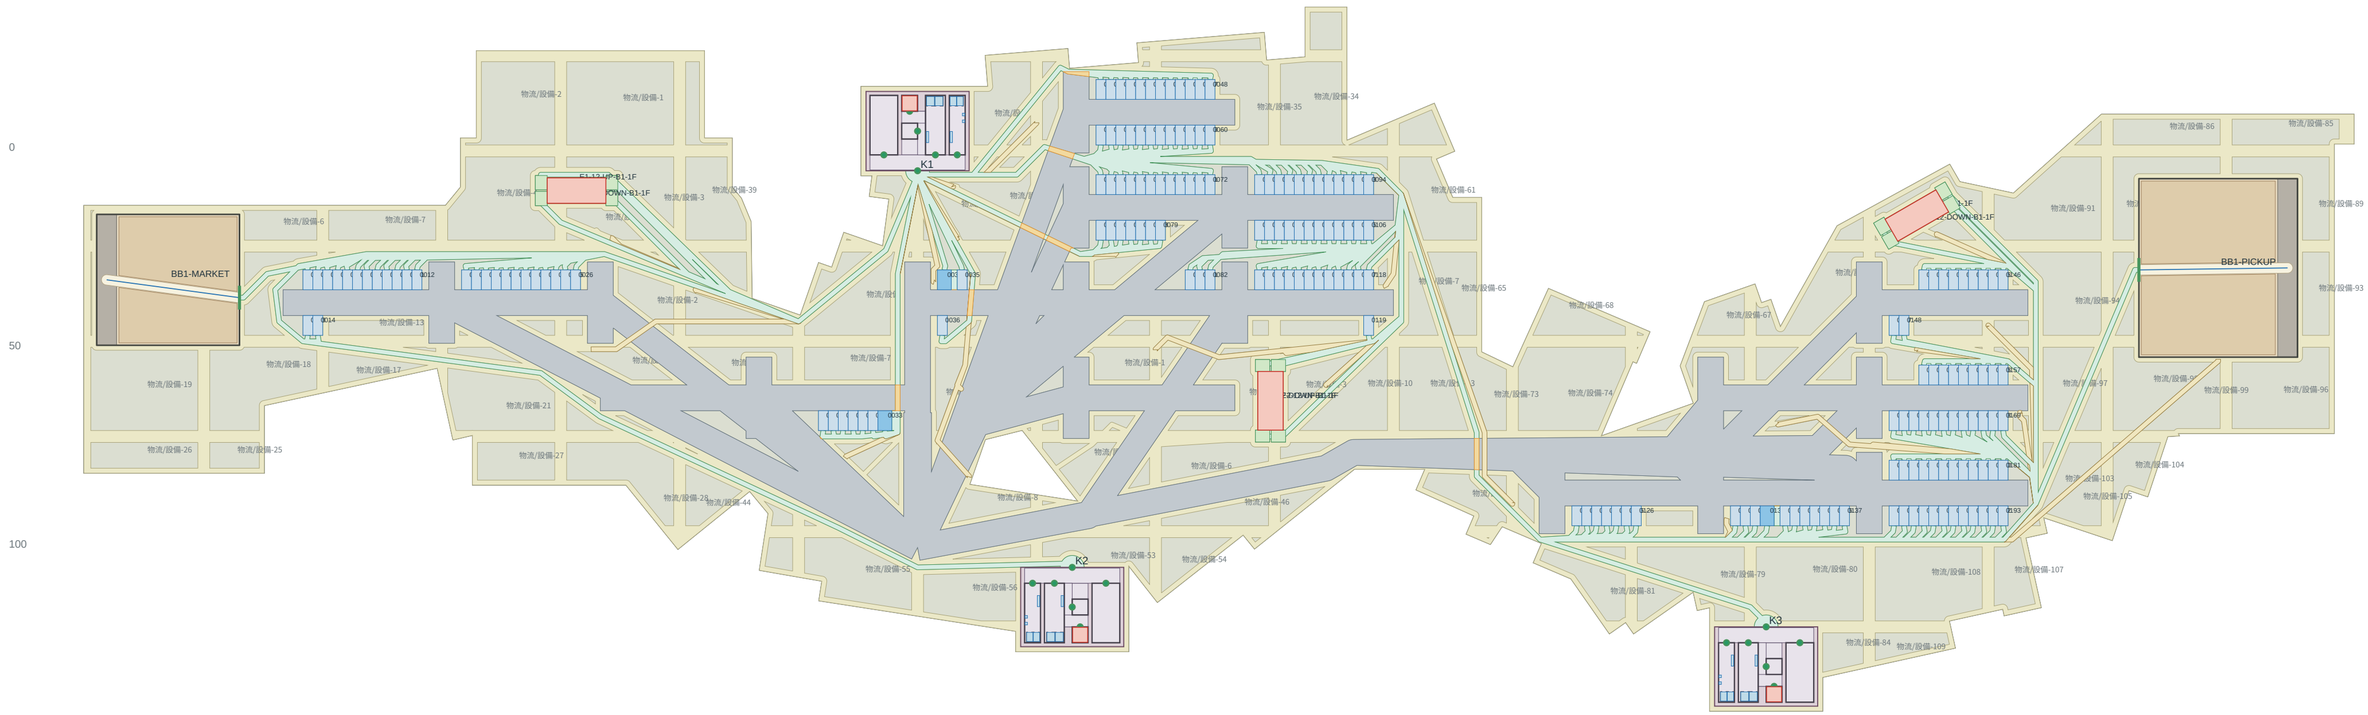

B館 B1｜詳細拡大 1/3

入口幅・売場主路・バックルーム・設備室を原ポリゴンで表示 / 範囲X -754.2〜-555.4m

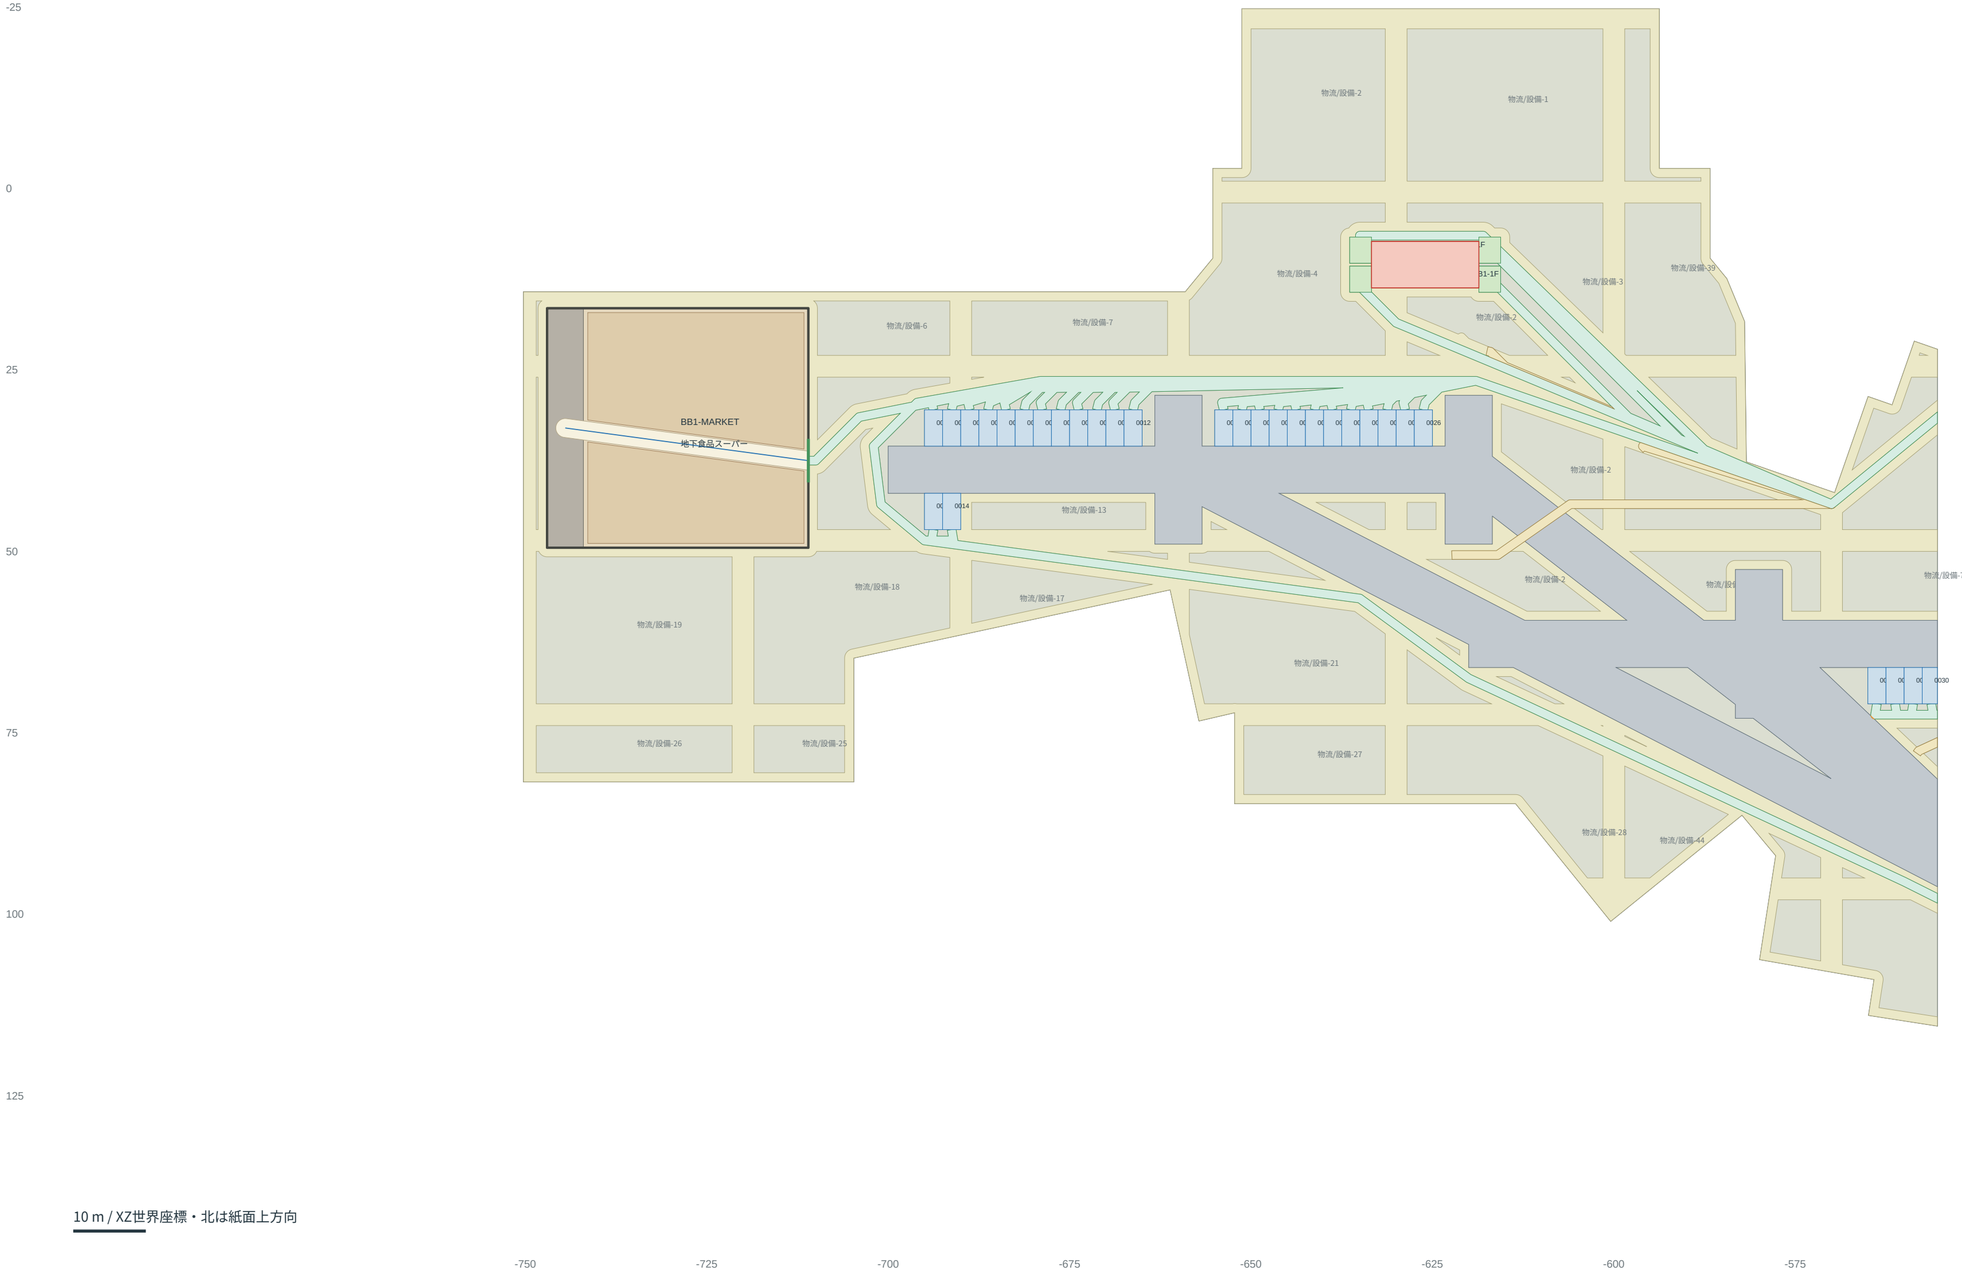

B館 B1｜詳細拡大 2/3

入口幅・売場主路・バックルーム・設備室を原ポリゴンで表示 / 範囲X -563.4〜-364.6m

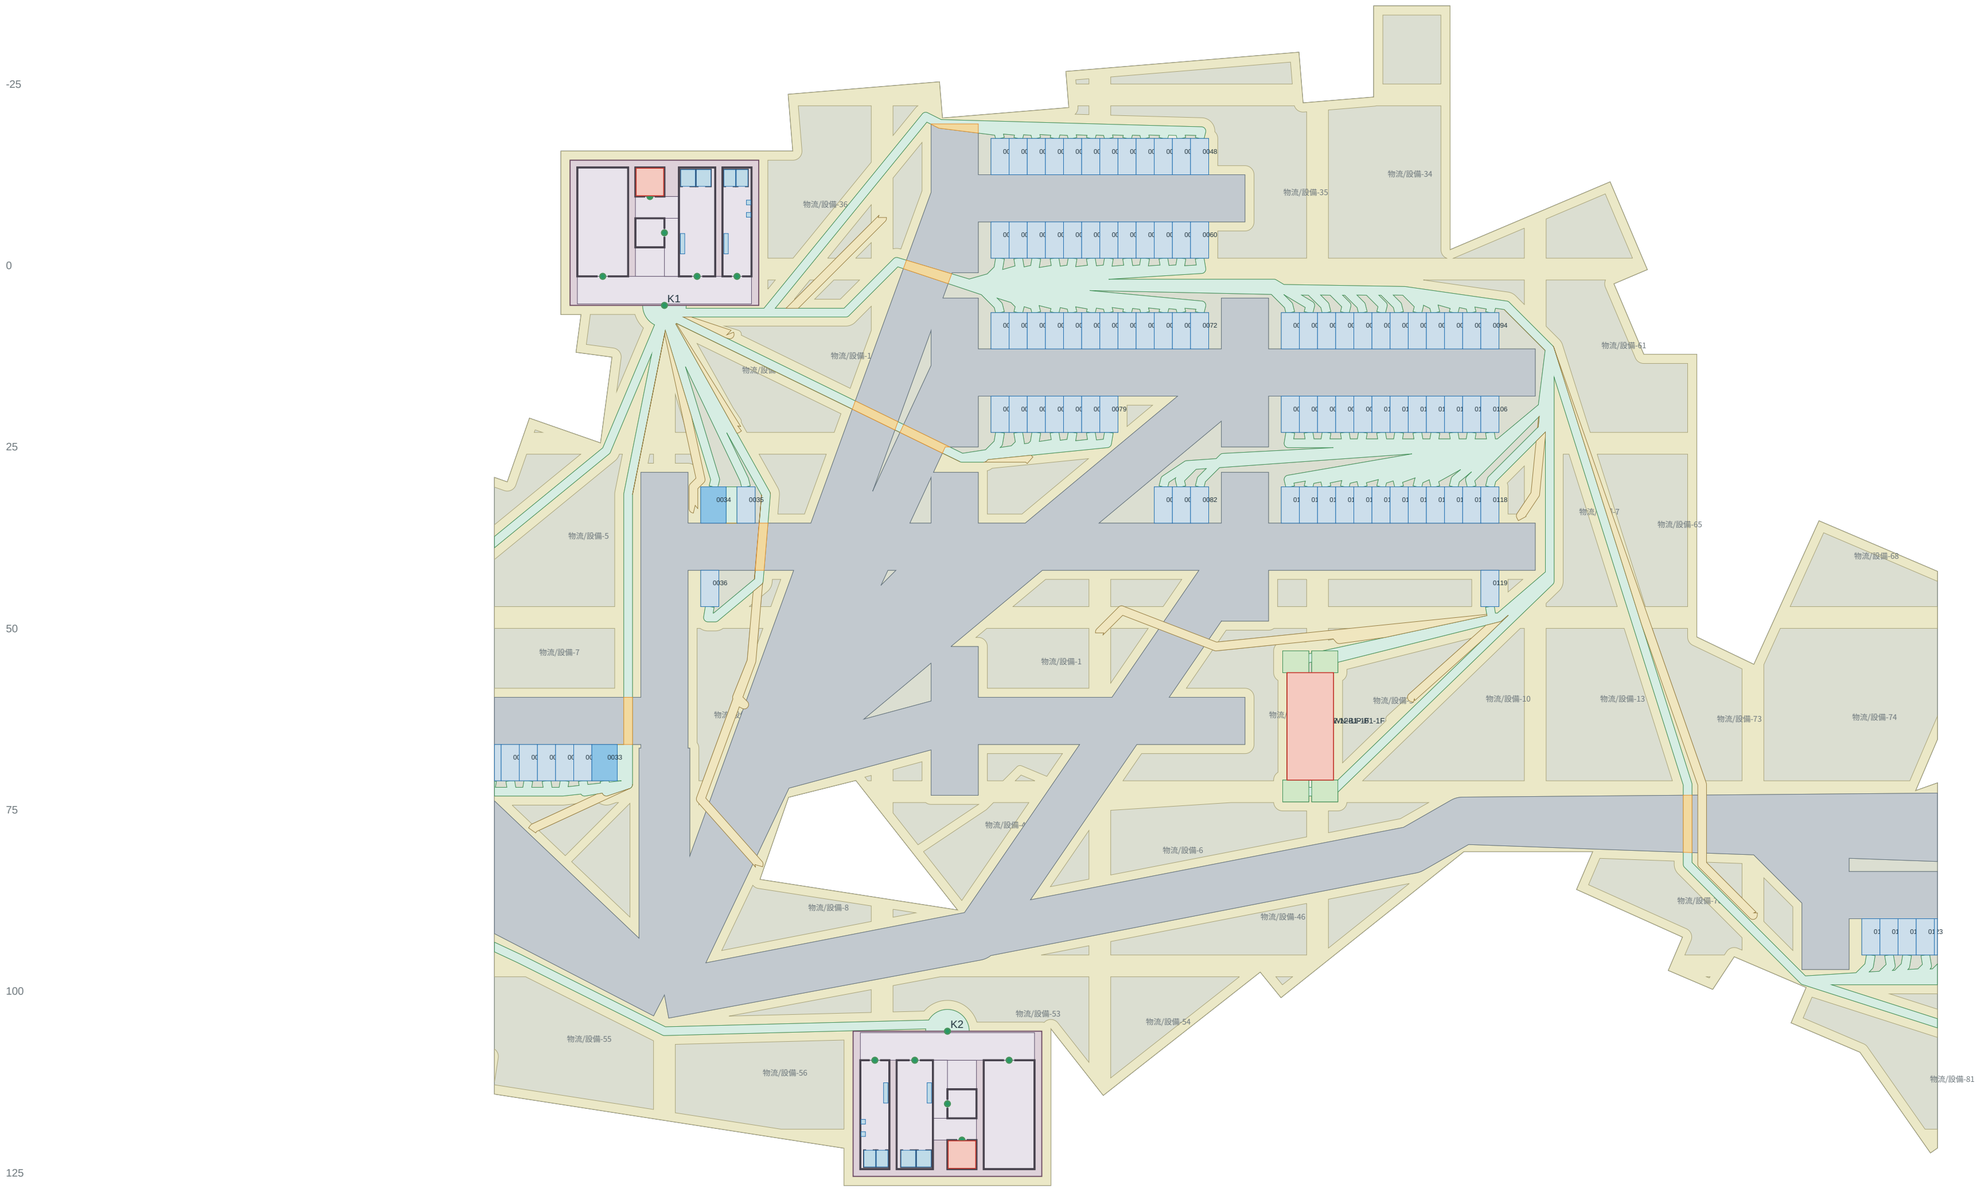

10 m / XZ世界座標・北は紙面上方向

B館 B1｜詳細拡大 3/3

入口幅・売場主路・バックルーム・設備室を原ポリゴンで表示 / 範囲X -372.6〜-173.8m

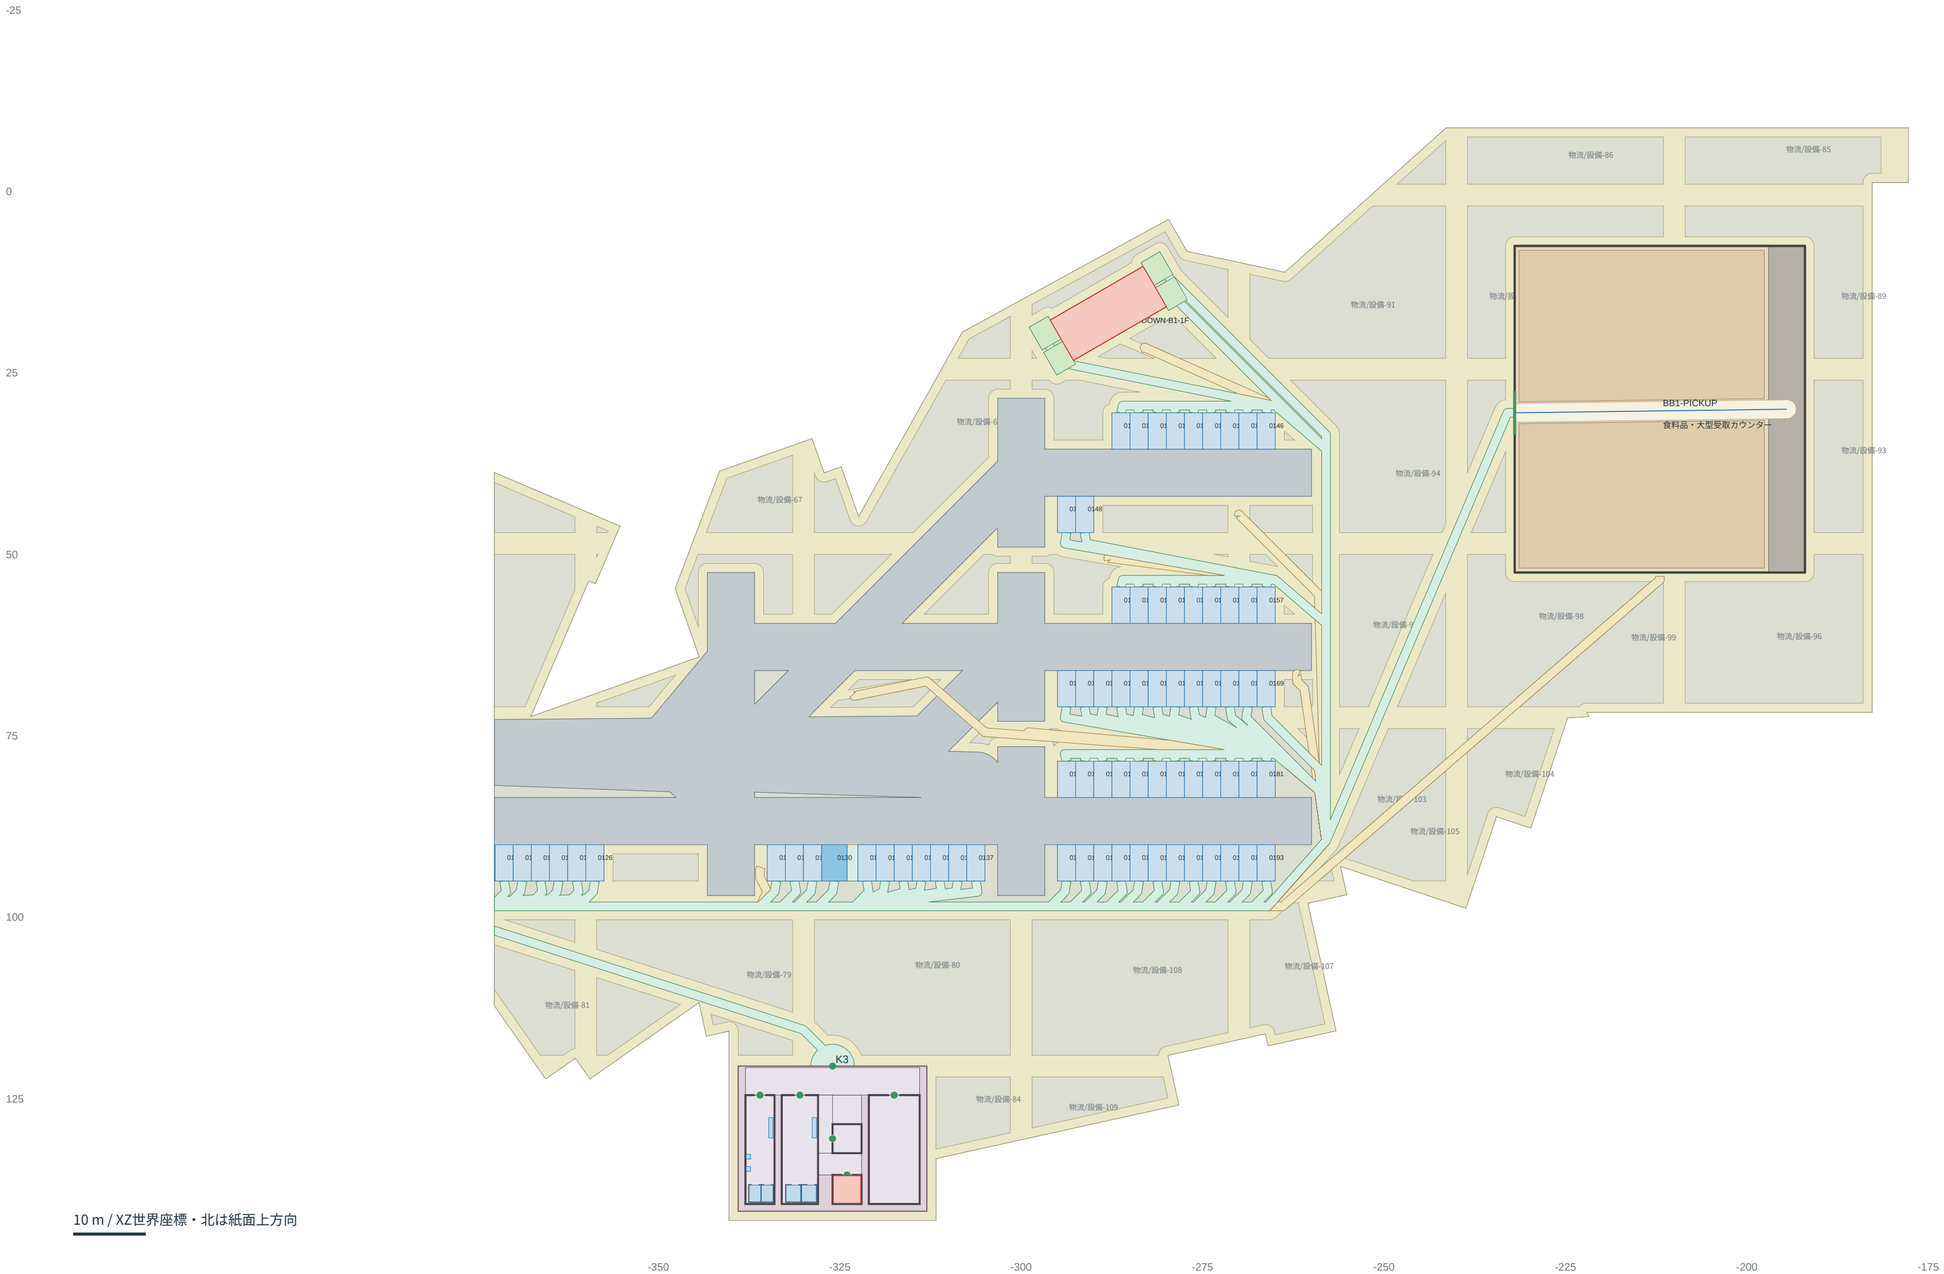

B館 1F｜詳細平面図 全体

既存内部形状を維持 / Y=+0.000m / 区画数 65 / 入口緑線・主路青線・バックルーム灰。赤の局所案は未適用。

B館 1F｜詳細拡大 1/3

入口幅・売場主路・バックルーム・設備室を原ポリゴンで表示 / 範囲X -754.2〜-553.3m

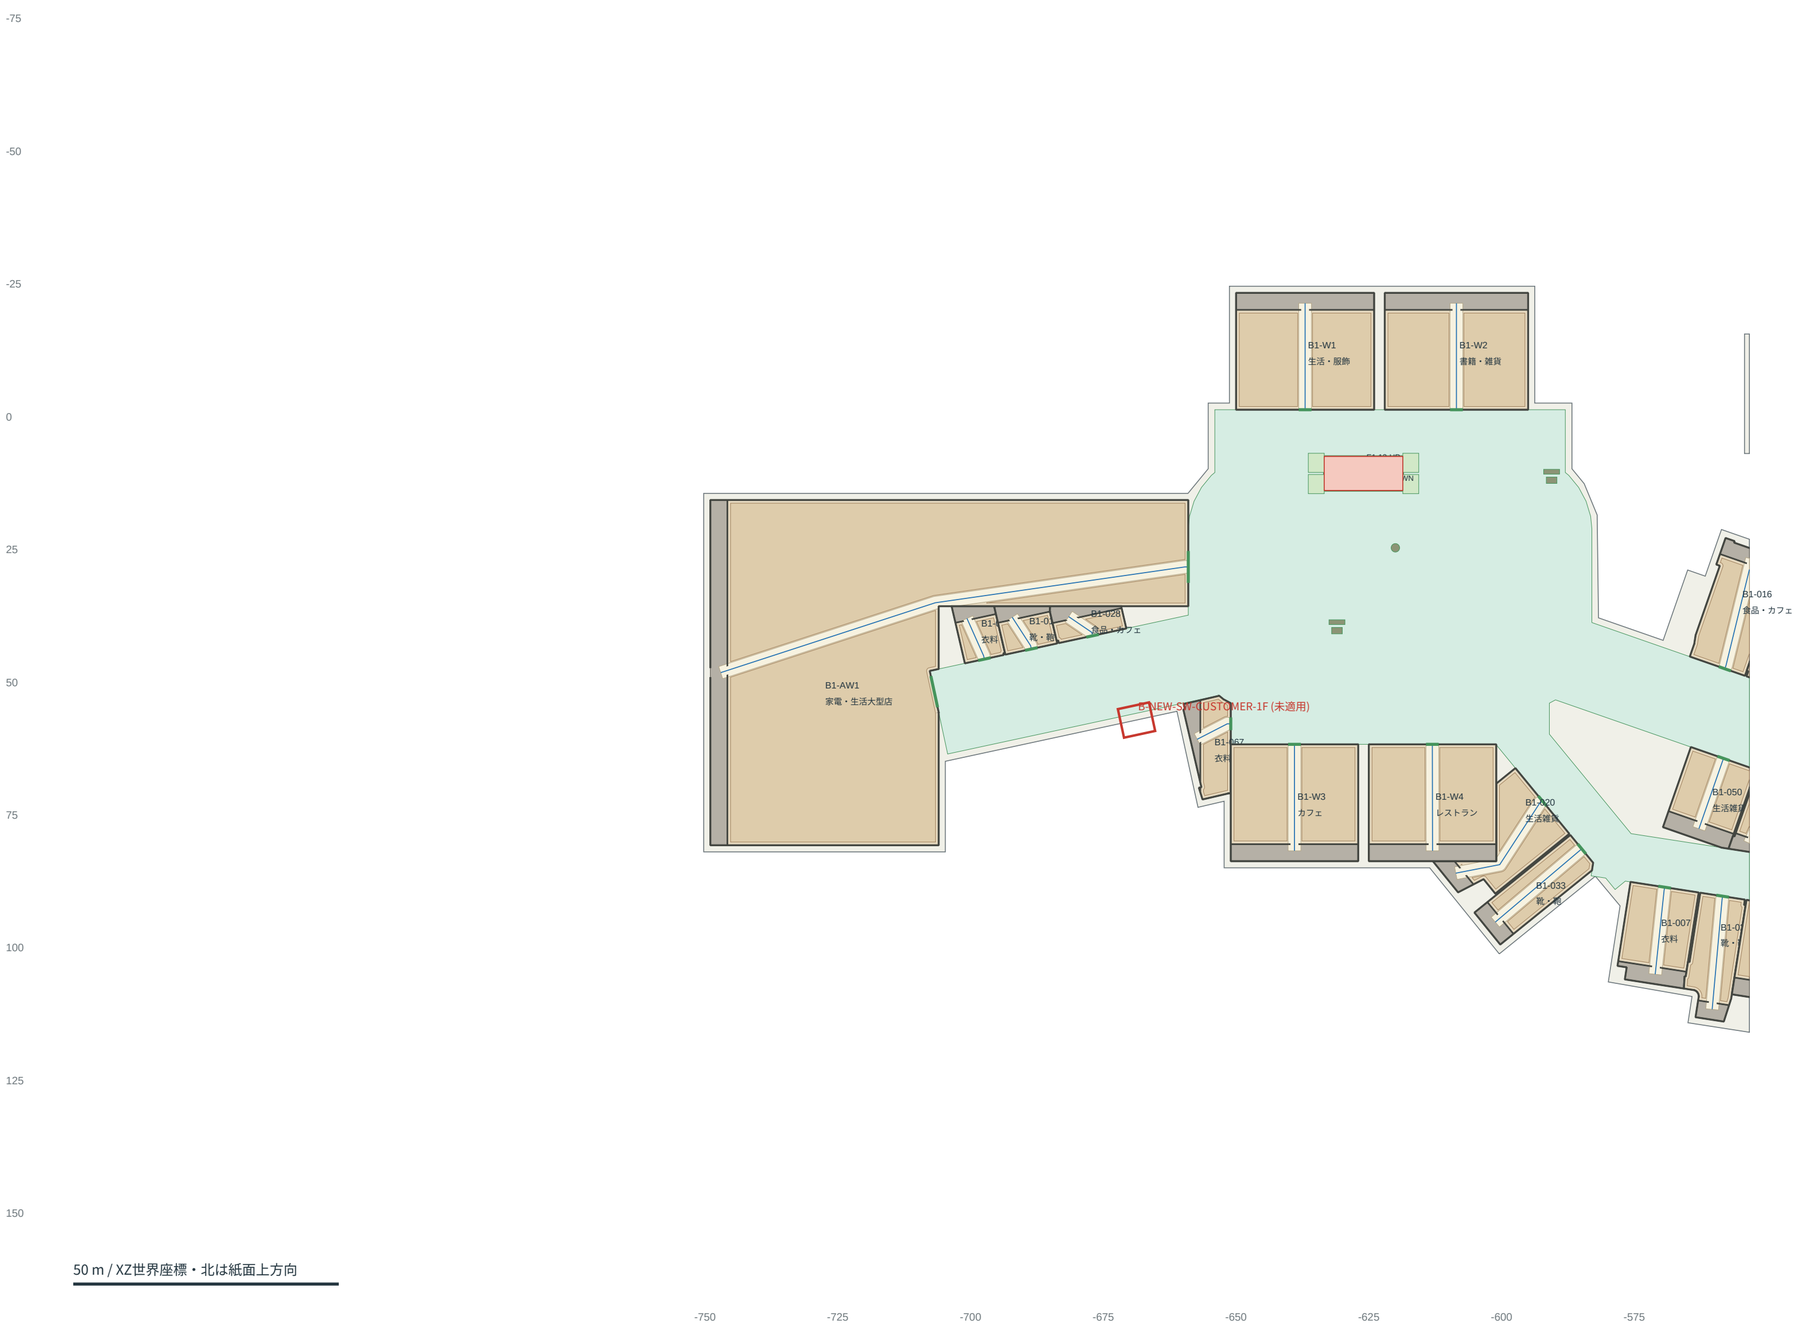

B館 1F｜詳細拡大 2/3

入口幅・売場主路・バックルーム・設備室を原ポリゴンで表示 / 範囲X -561.3〜-360.4m

B館 1F｜詳細拡大 3/3

入口幅・売場主路・バックルーム・設備室を原ポリゴンで表示 / 範囲X -368.4〜-167.5m

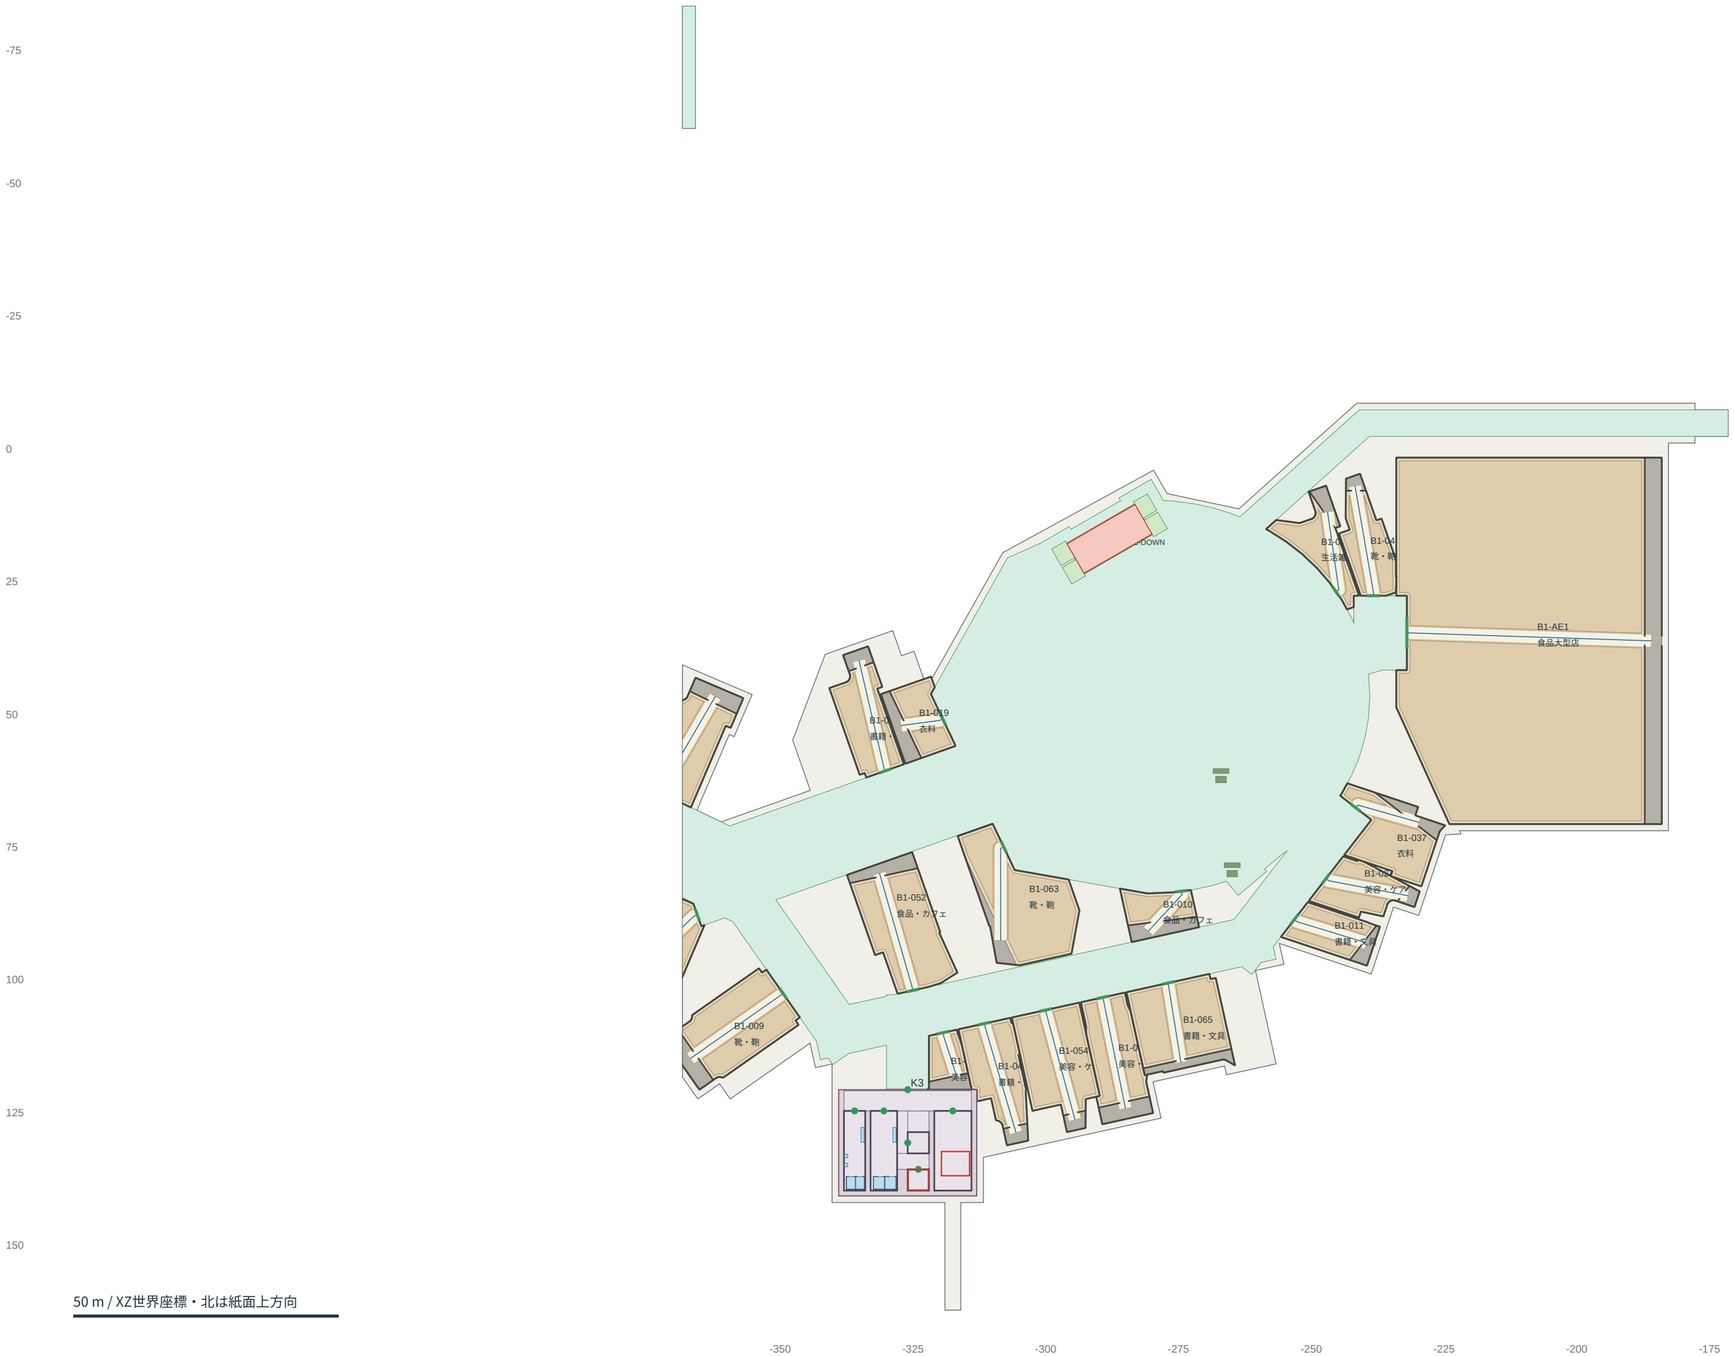

B館 2F｜詳細平面図 全体

既存内部形状を維持 / Y=+5.525m / 区画数 66 / 入口緑線・主路青線・バックルーム灰。赤の局所案は未適用。

B館 2F｜詳細拡大 1/3

入口幅・売場主路・バックルーム・設備室を原ポリゴンで表示 / 範囲X -754.2〜-532.0m

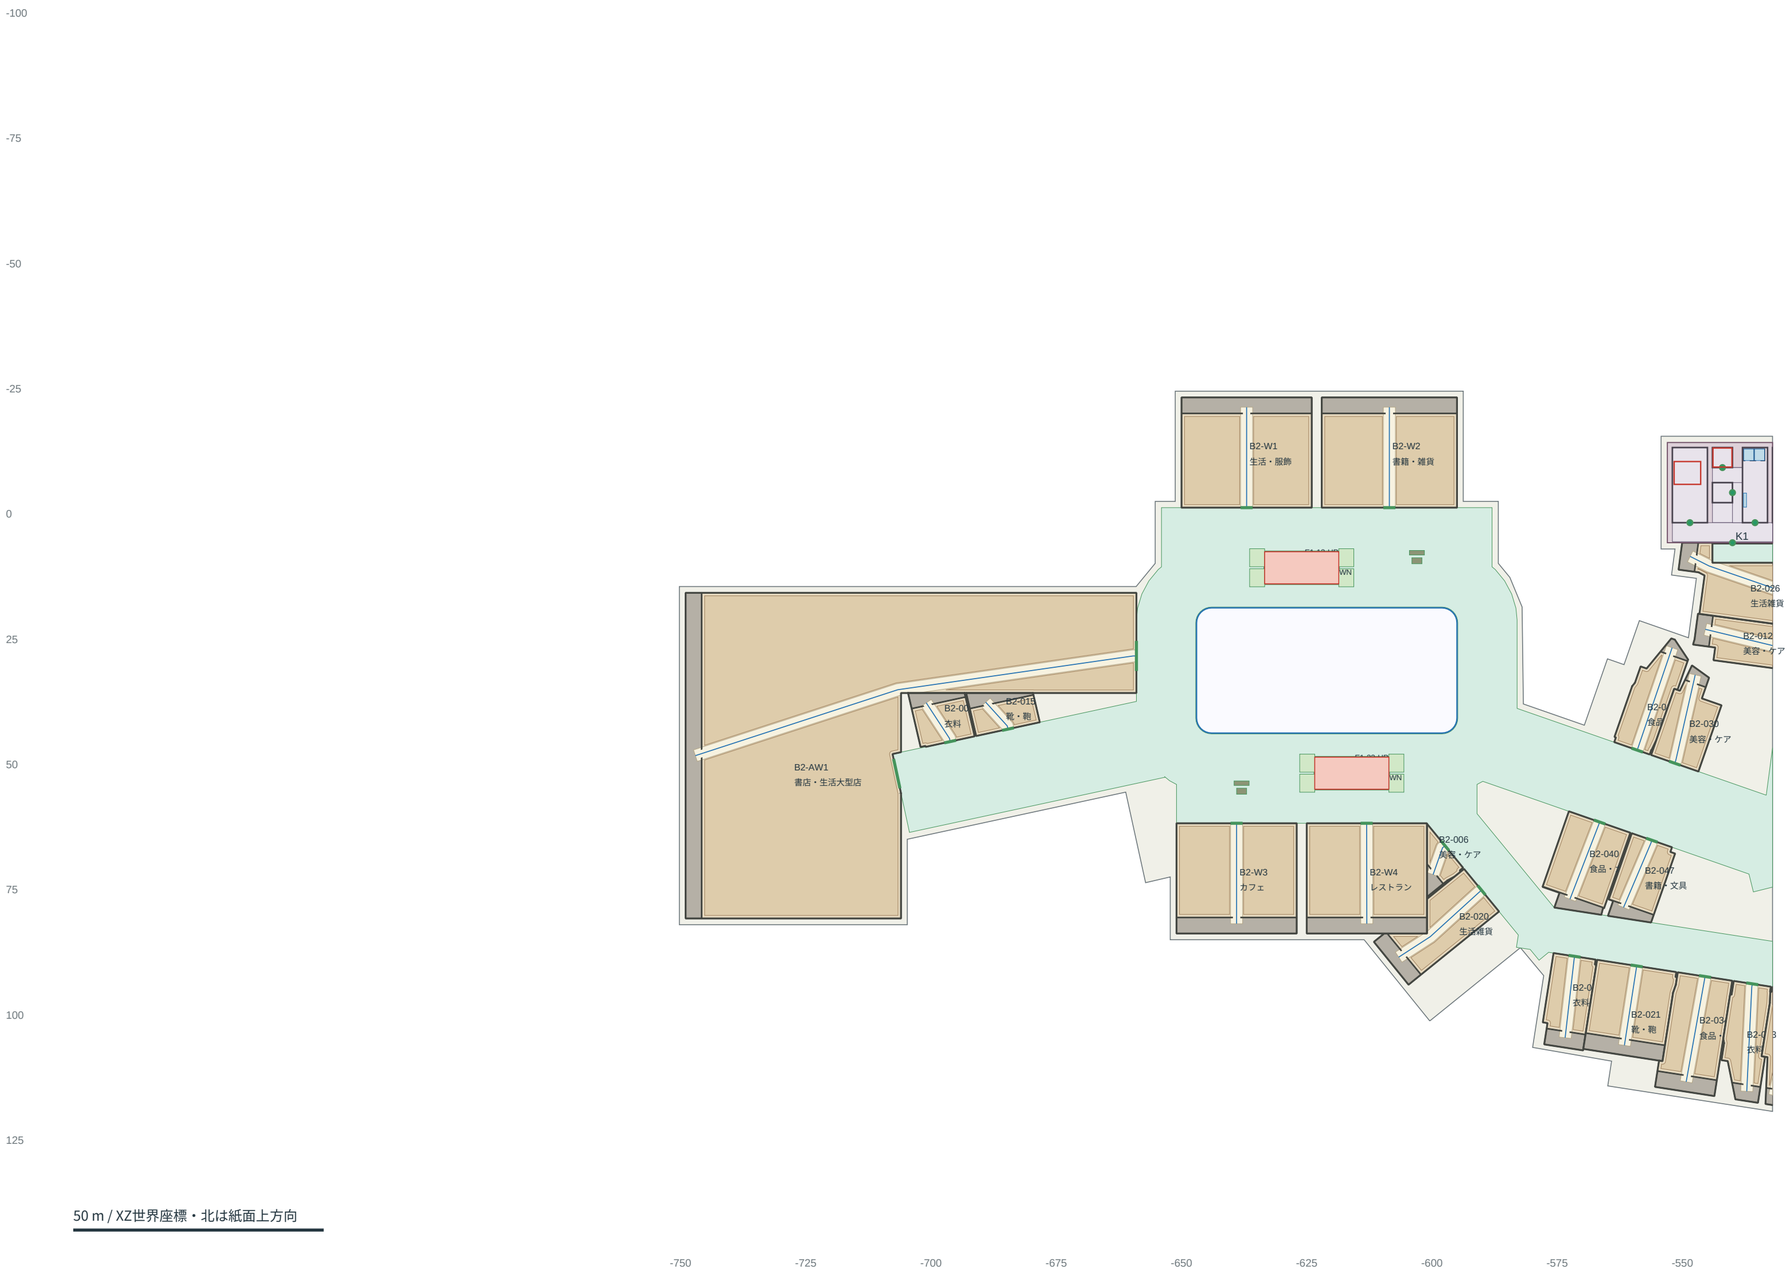

B館 2F｜詳細拡大 2/3

入口幅・売場主路・バックルーム・設備室を原ポリゴンで表示 / 範囲X -540.0〜-317.8m

50 m / XZ世界座標・北は紙面上方向

B館 2F｜詳細拡大 3/3

入口幅・売場主路・バックルーム・設備室を原ポリゴンで表示 / 範囲X -325.8〜-103.5m

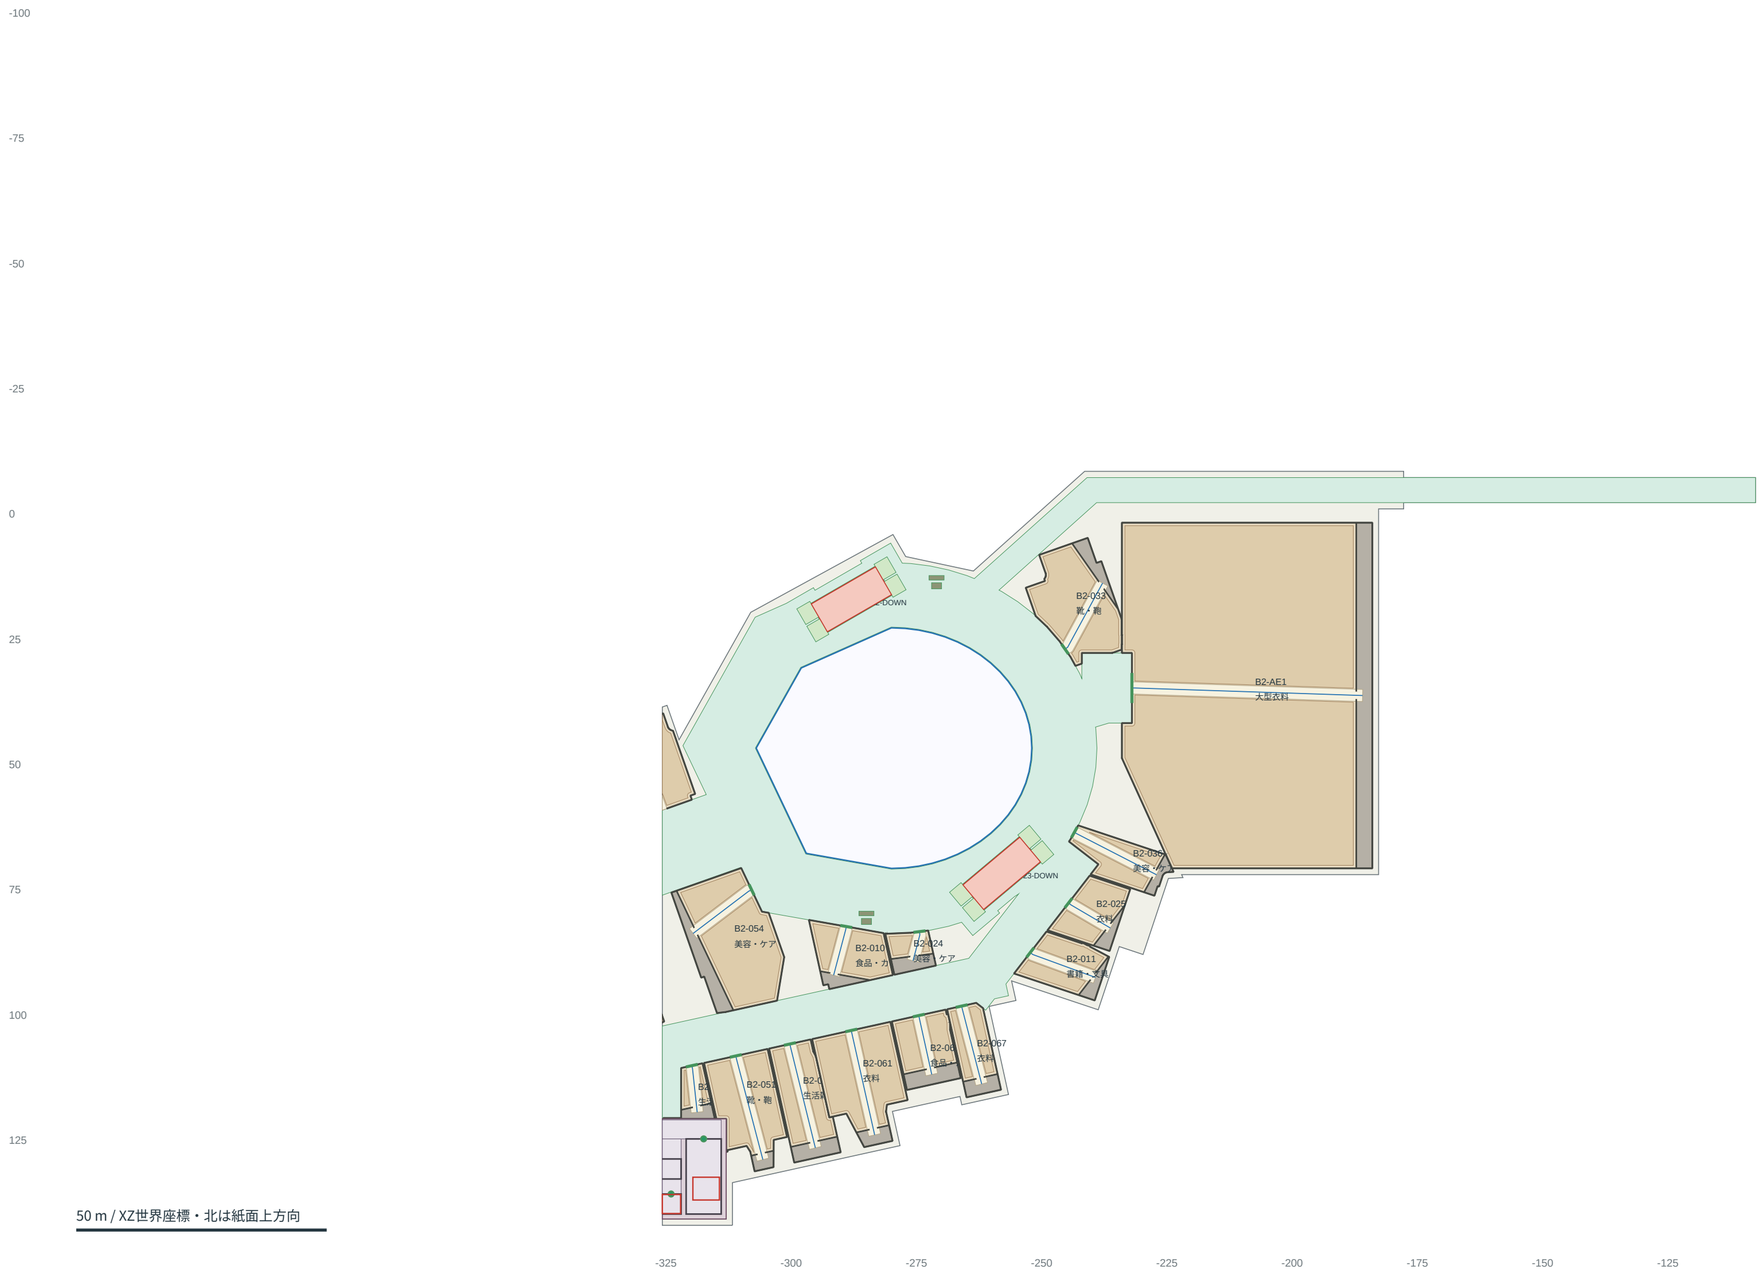

B館 3F｜詳細平面図 全体

既存内部形状を維持 / Y=+10.875m / 区画数 57 / 入口緑線・主路青線・バックルーム灰。赤の局所案は未適用。

B館 3F｜詳細拡大 1/3

入口幅・売場主路・バックルーム・設備室を原ポリゴンで表示 / 範囲X -754.2〜-555.4m

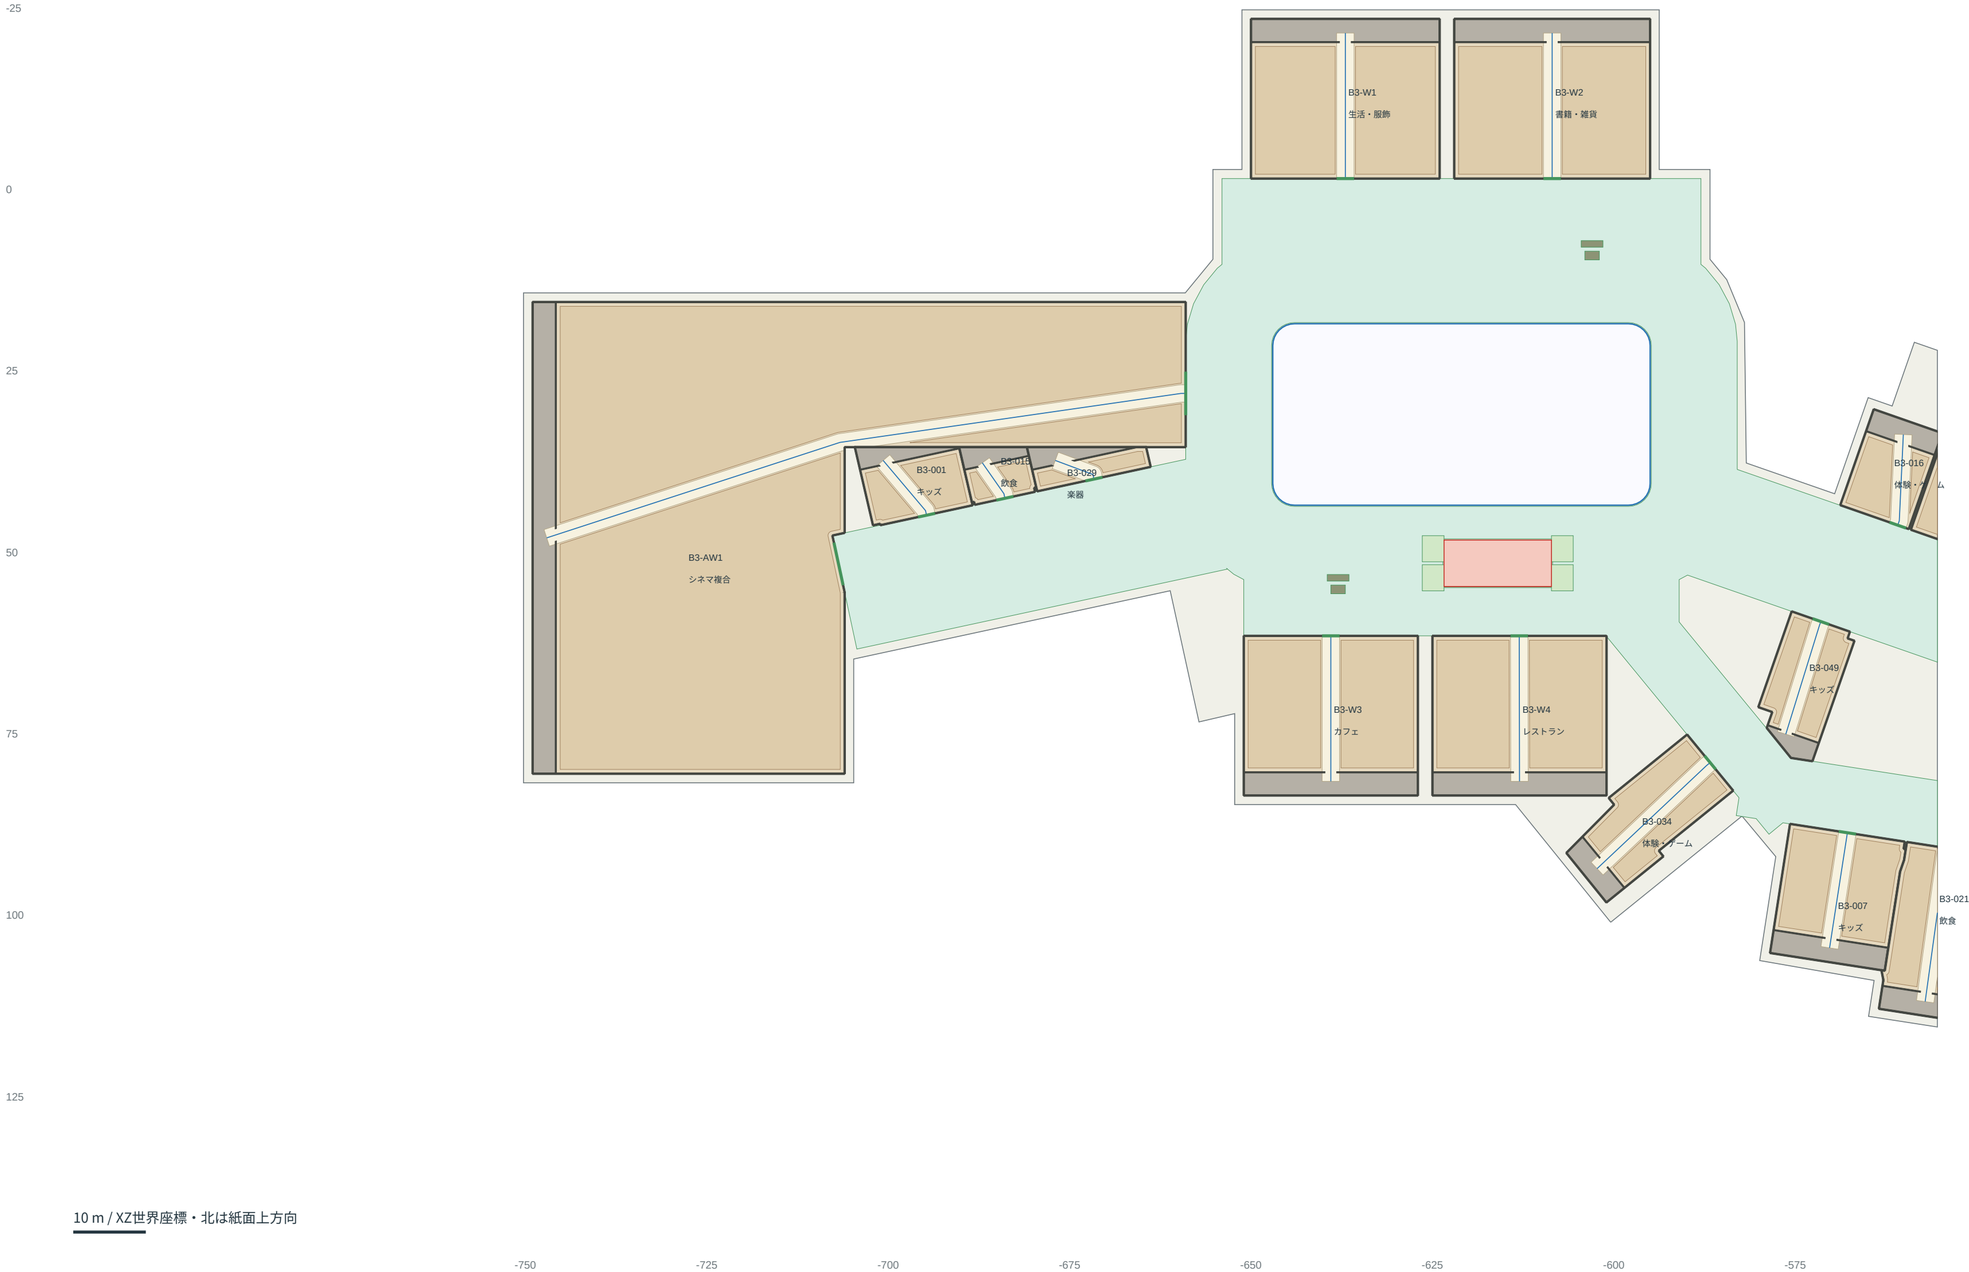

B館 3F｜詳細拡大 2/3

入口幅・売場主路・バックルーム・設備室を原ポリゴンで表示 / 範囲X -563.4〜-364.6m

10 m / XZ世界座標・北は紙面上方向

B館 3F｜詳細拡大 3/3

入口幅・売場主路・バックルーム・設備室を原ポリゴンで表示 / 範囲X -372.6〜-173.8m

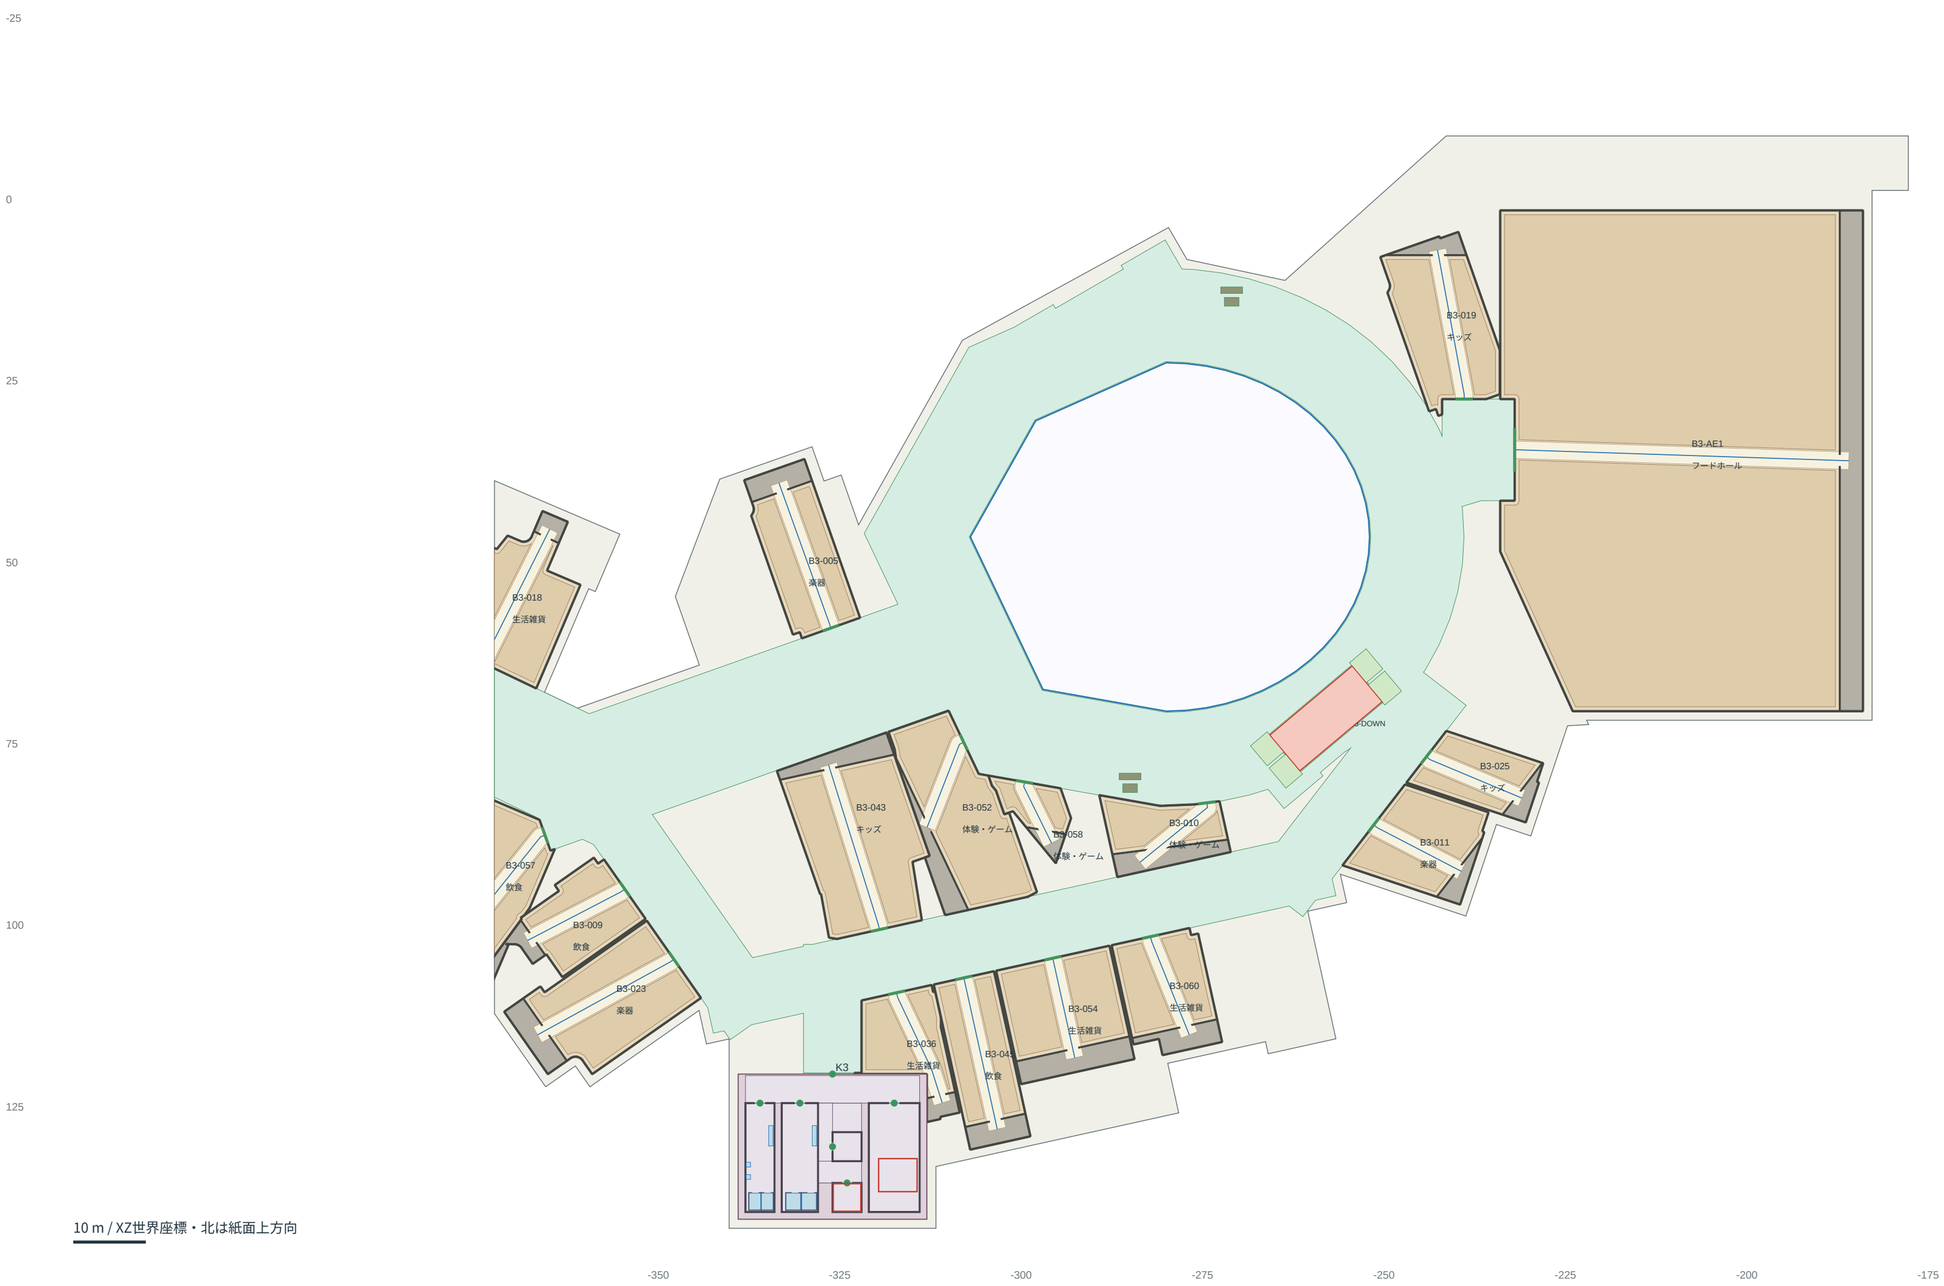

B館 RF｜詳細平面図 全体

今回新設計 / Y=+16.400m / 区画数 1 / 入口緑線・主路青線・バックルーム灰。赤の局所案は未適用。

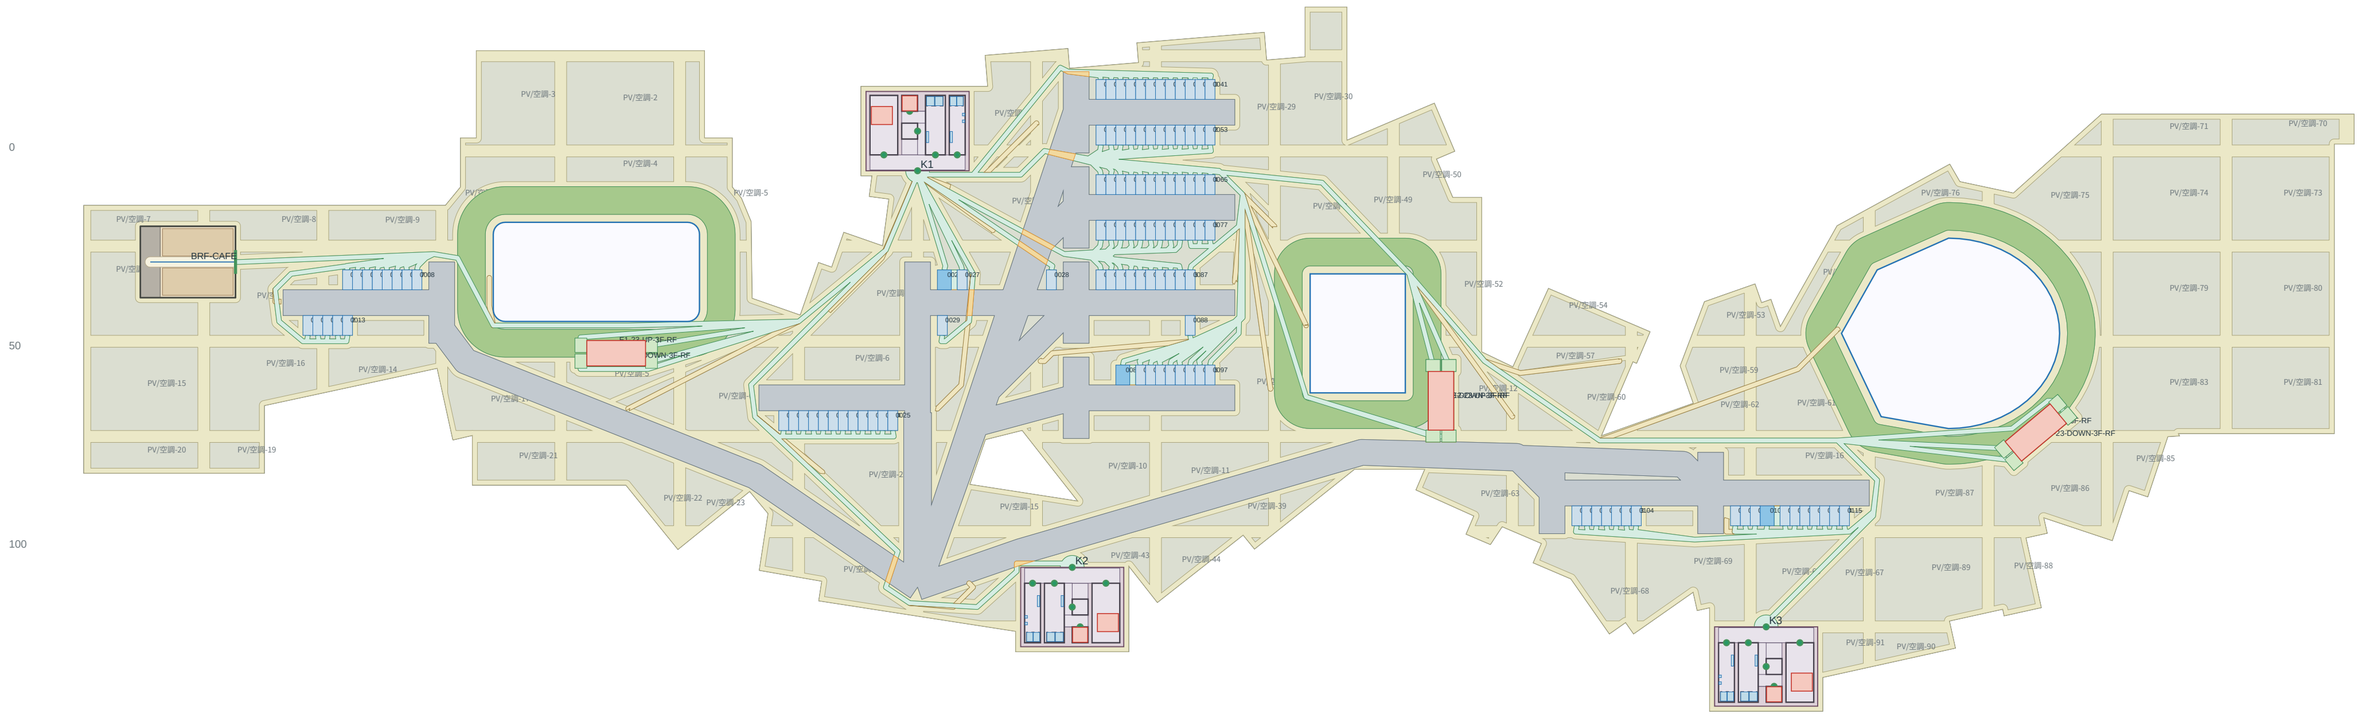

B館 RF｜詳細拡大 1/3

入口幅・売場主路・バックルーム・設備室を原ポリゴンで表示 / 範囲X -754.2〜-555.4m

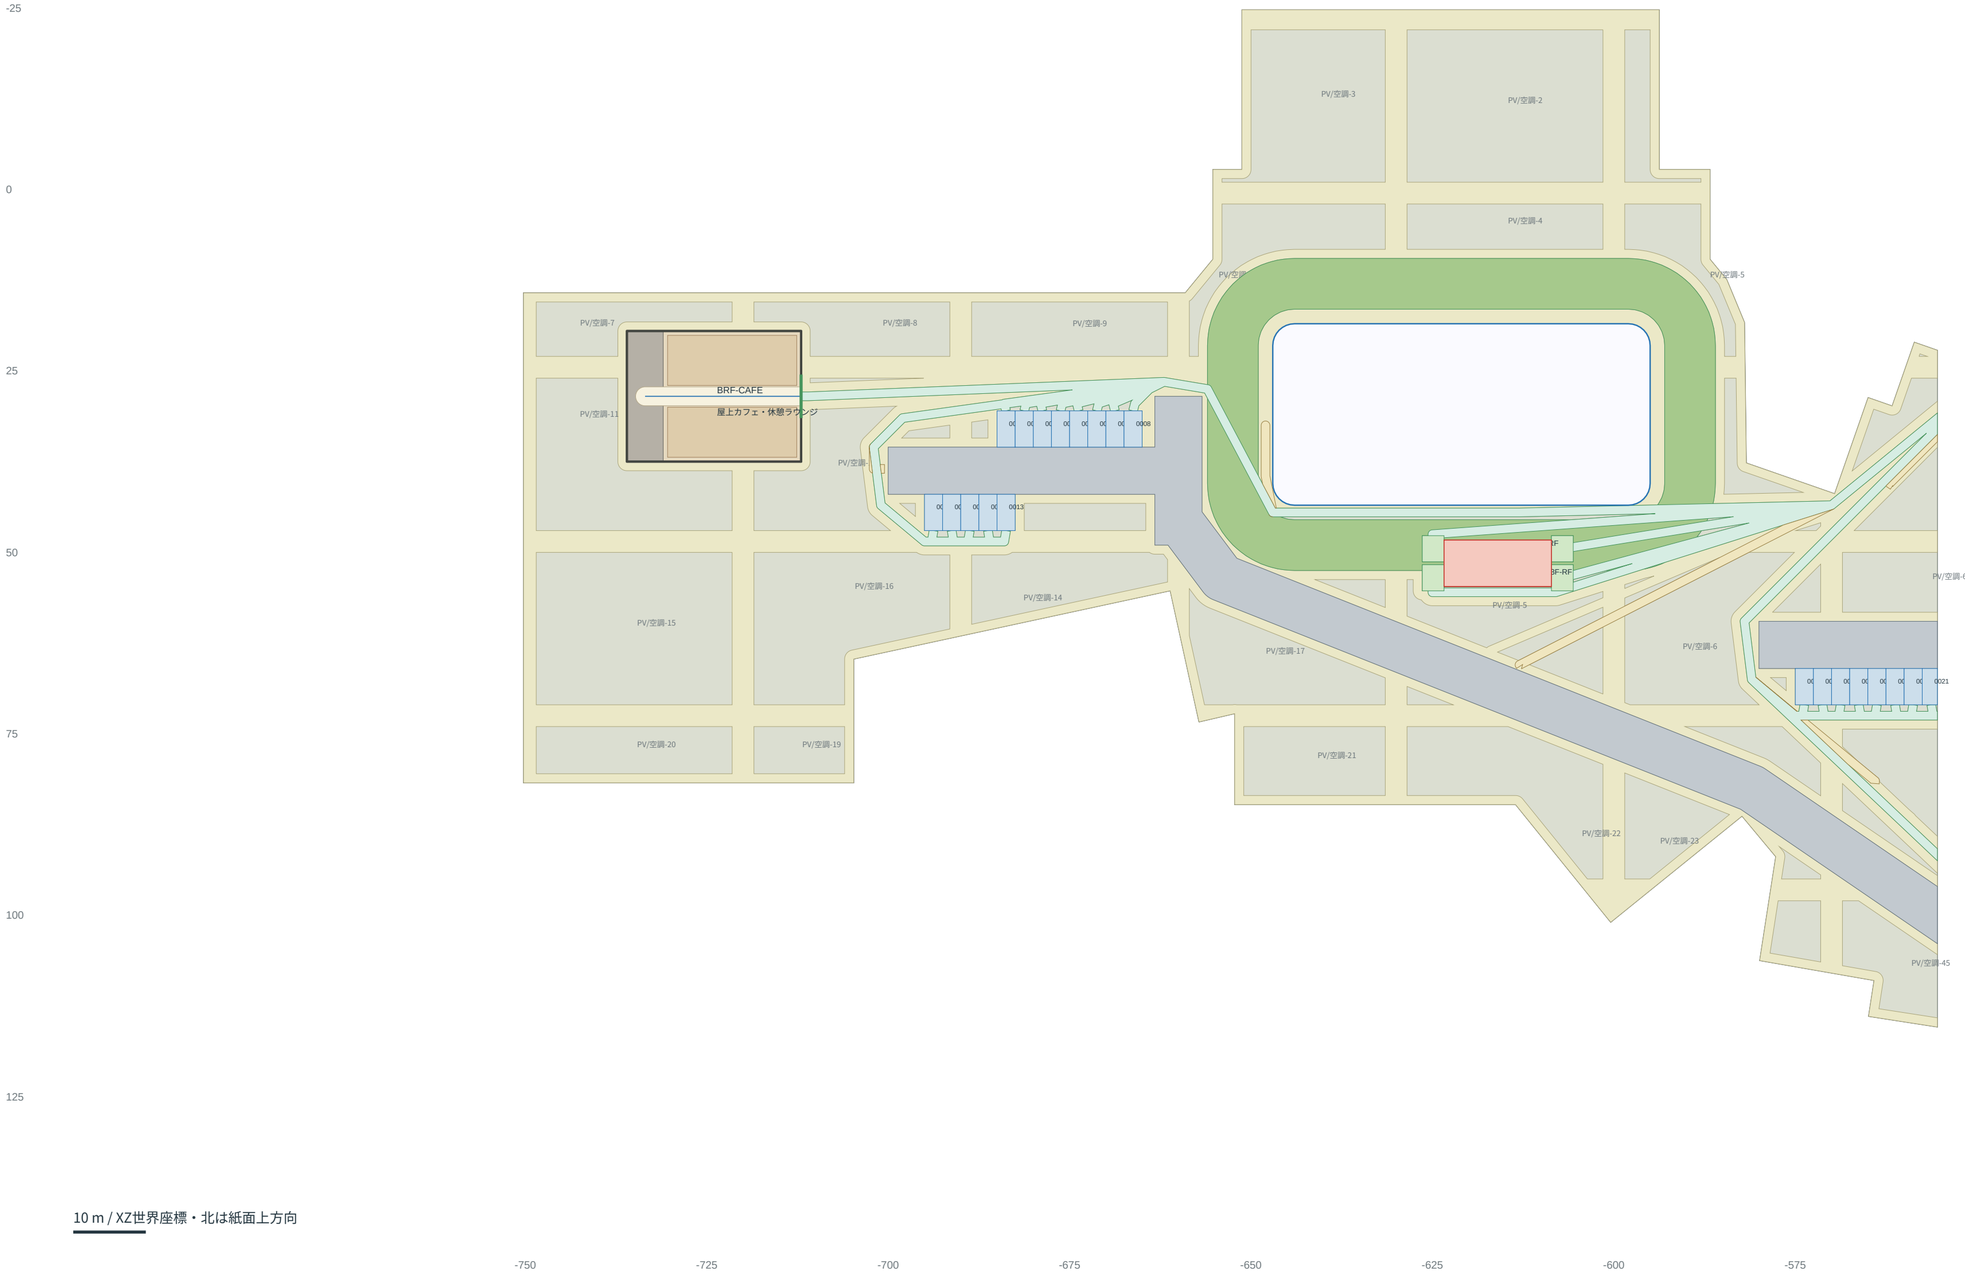

B館 RF｜詳細拡大 2/3

入口幅・売場主路・バックルーム・設備室を原ポリゴンで表示 / 範囲X -563.4〜-364.6m

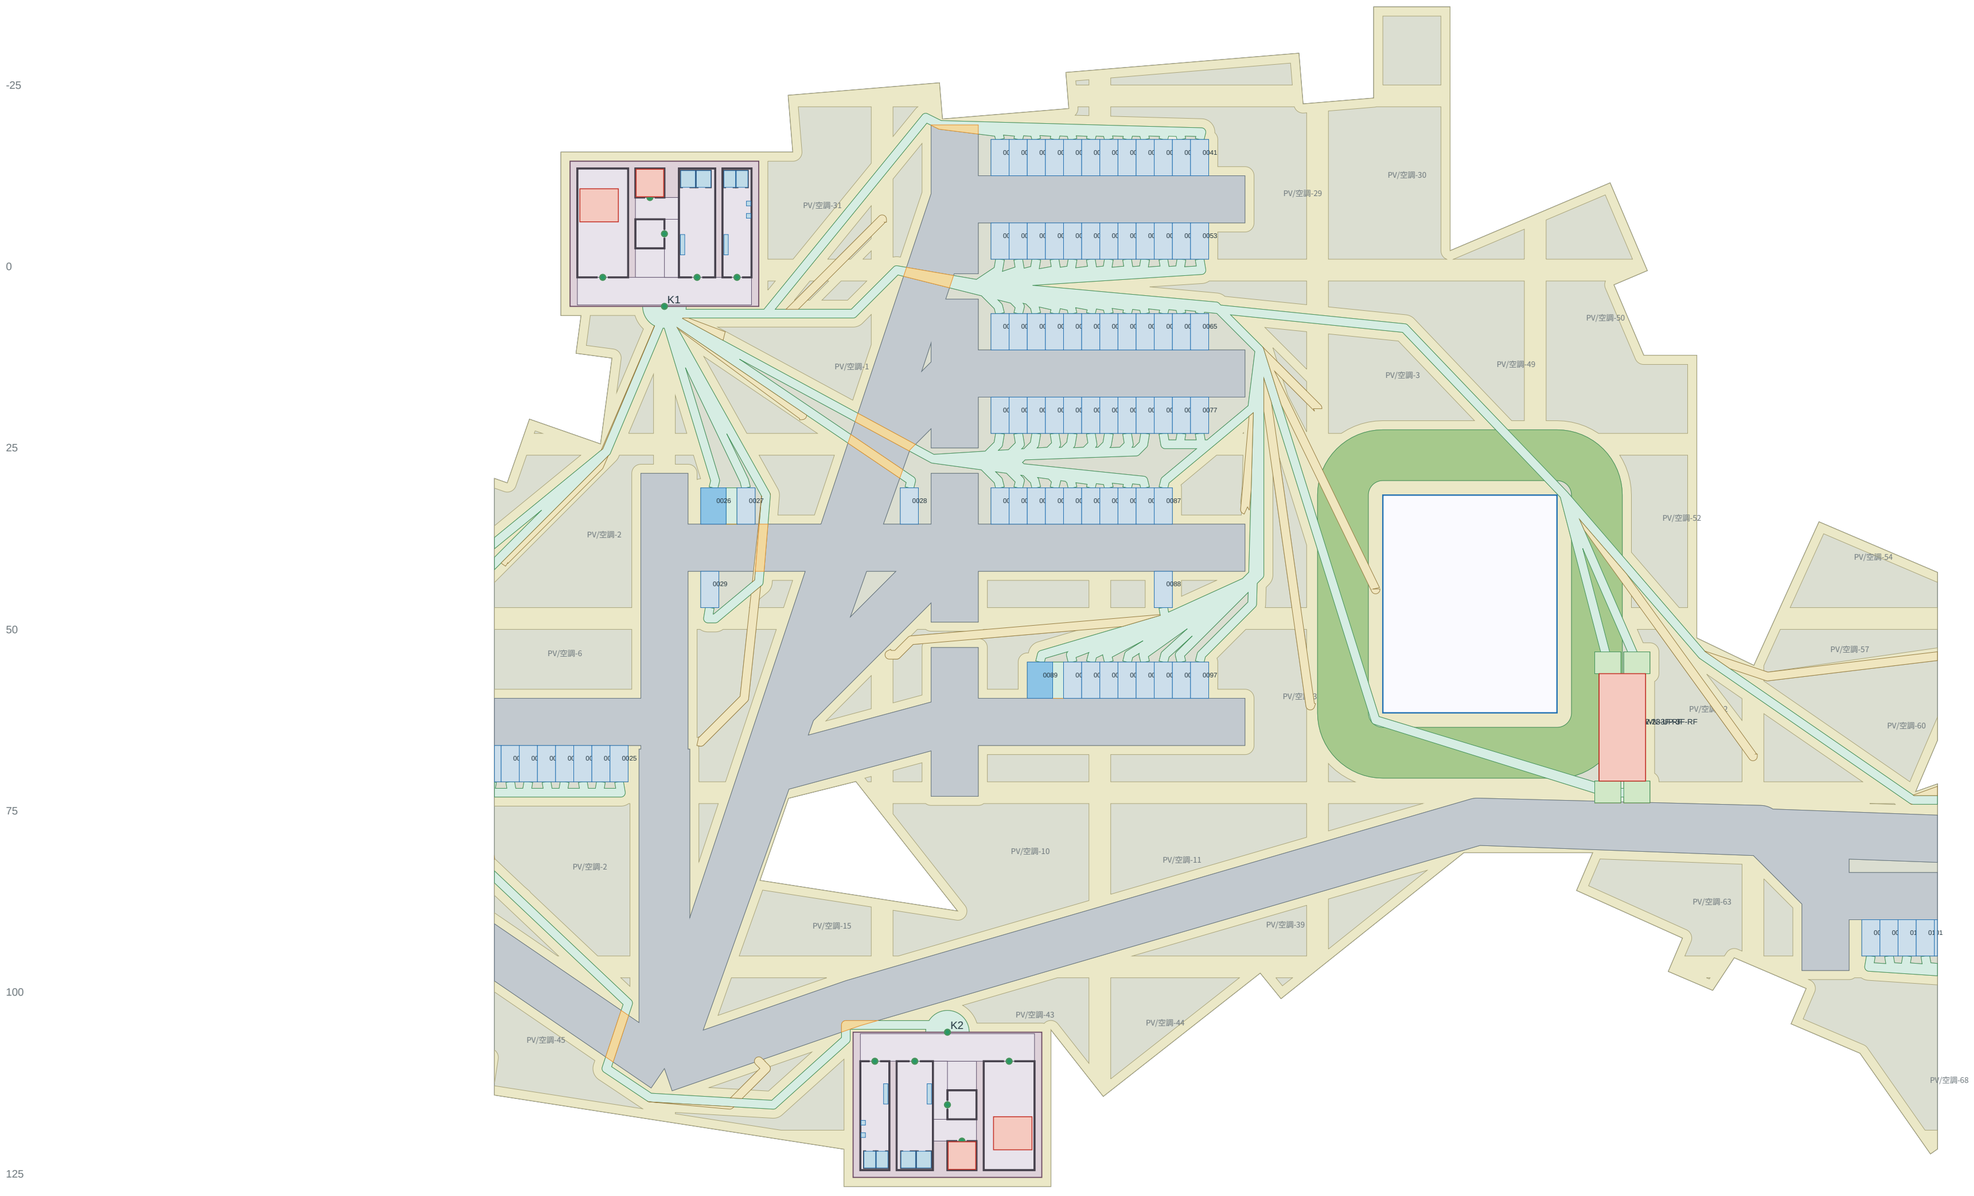

B館 RF｜詳細拡大 3/3

入口幅・売場主路・バックルーム・設備室を原ポリゴンで表示 / 範囲X -372.6〜-173.8m

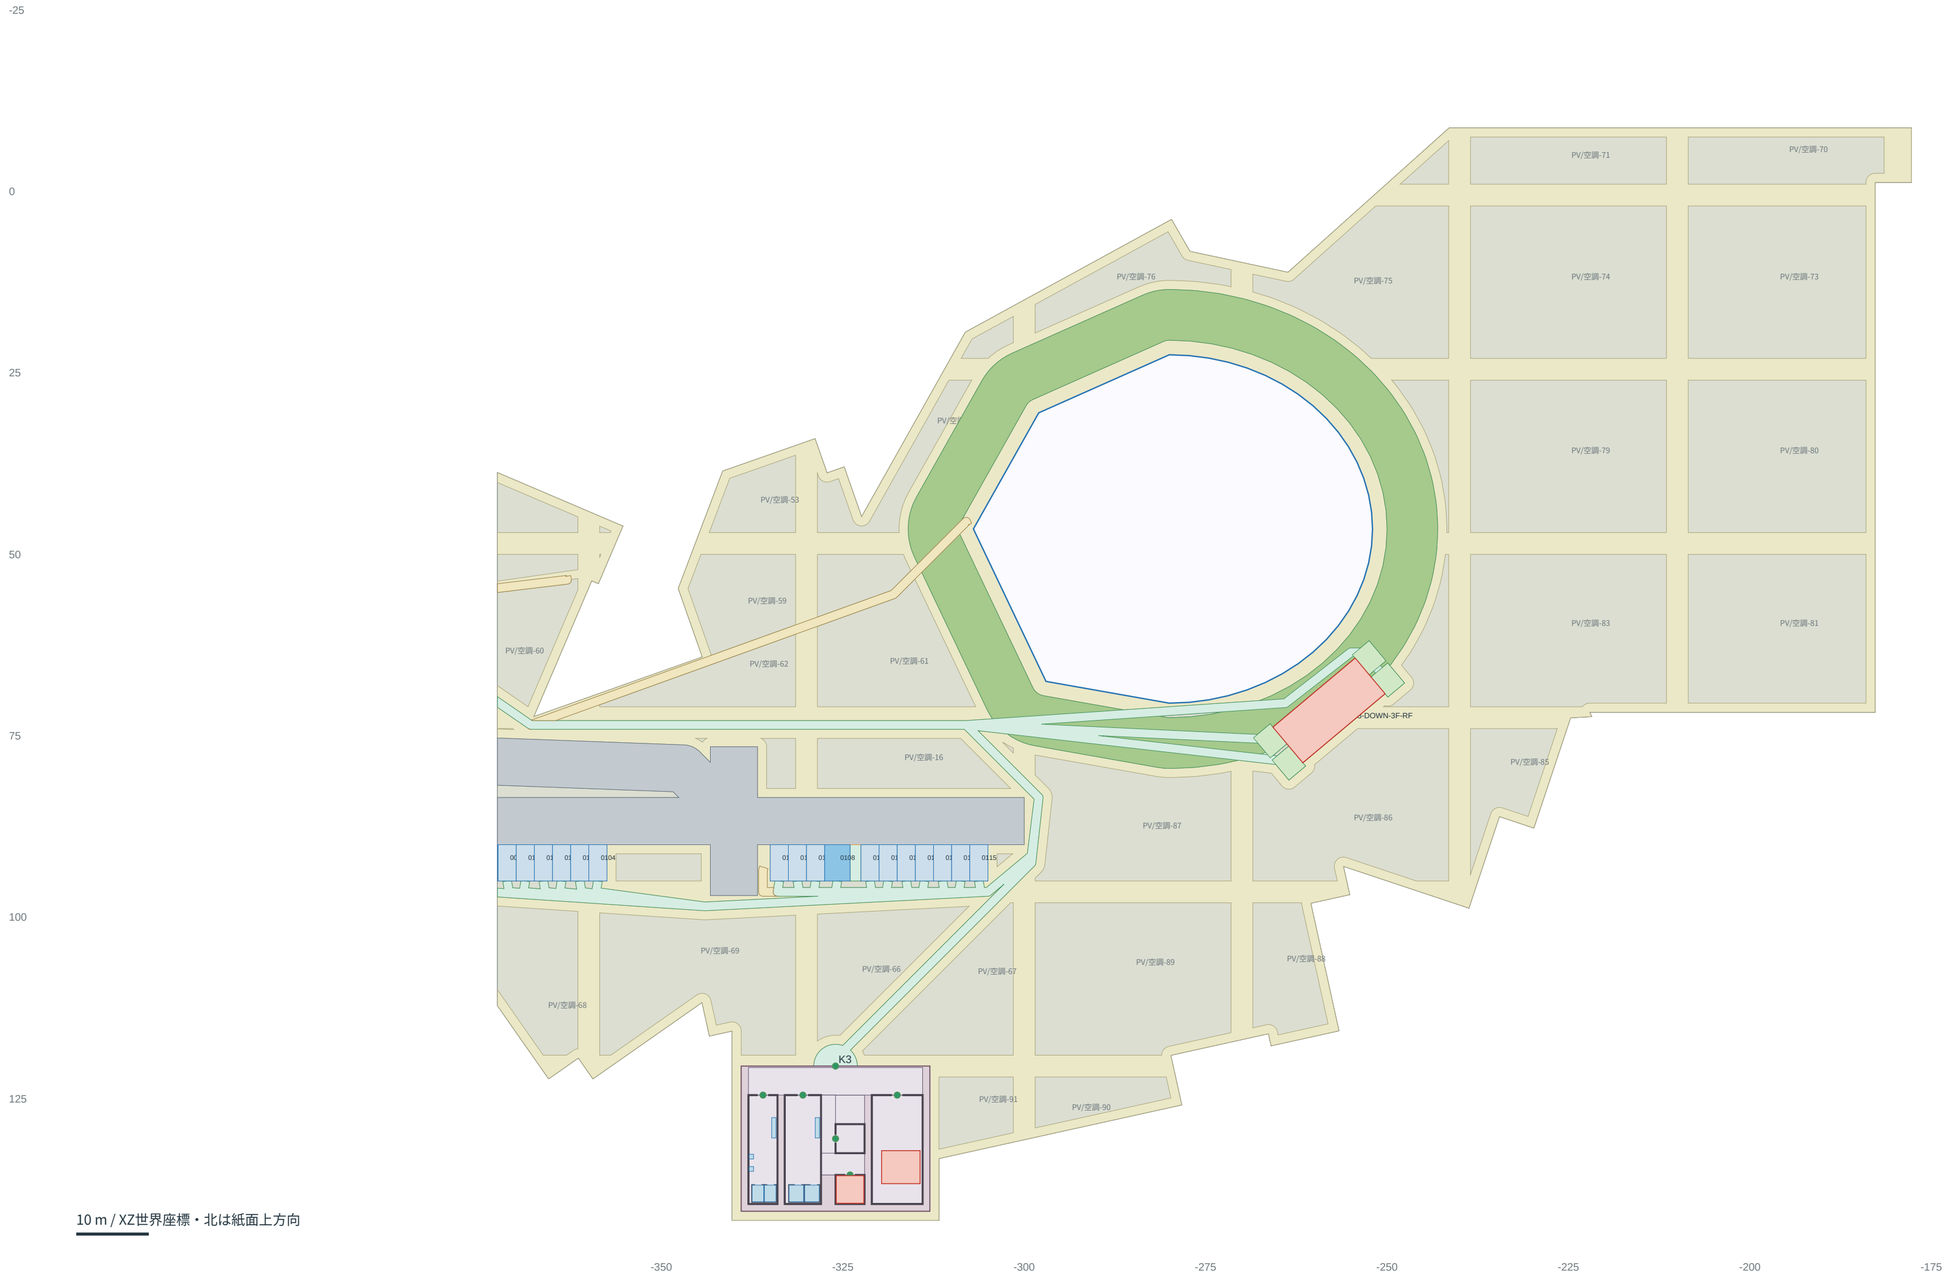

C館 B1｜詳細平面図 全体

既存内部形状を維持 / Y=-5.350m / 区画数 18 / 入口緑線・主路青線・バックルーム灰。赤の局所案は未適用。

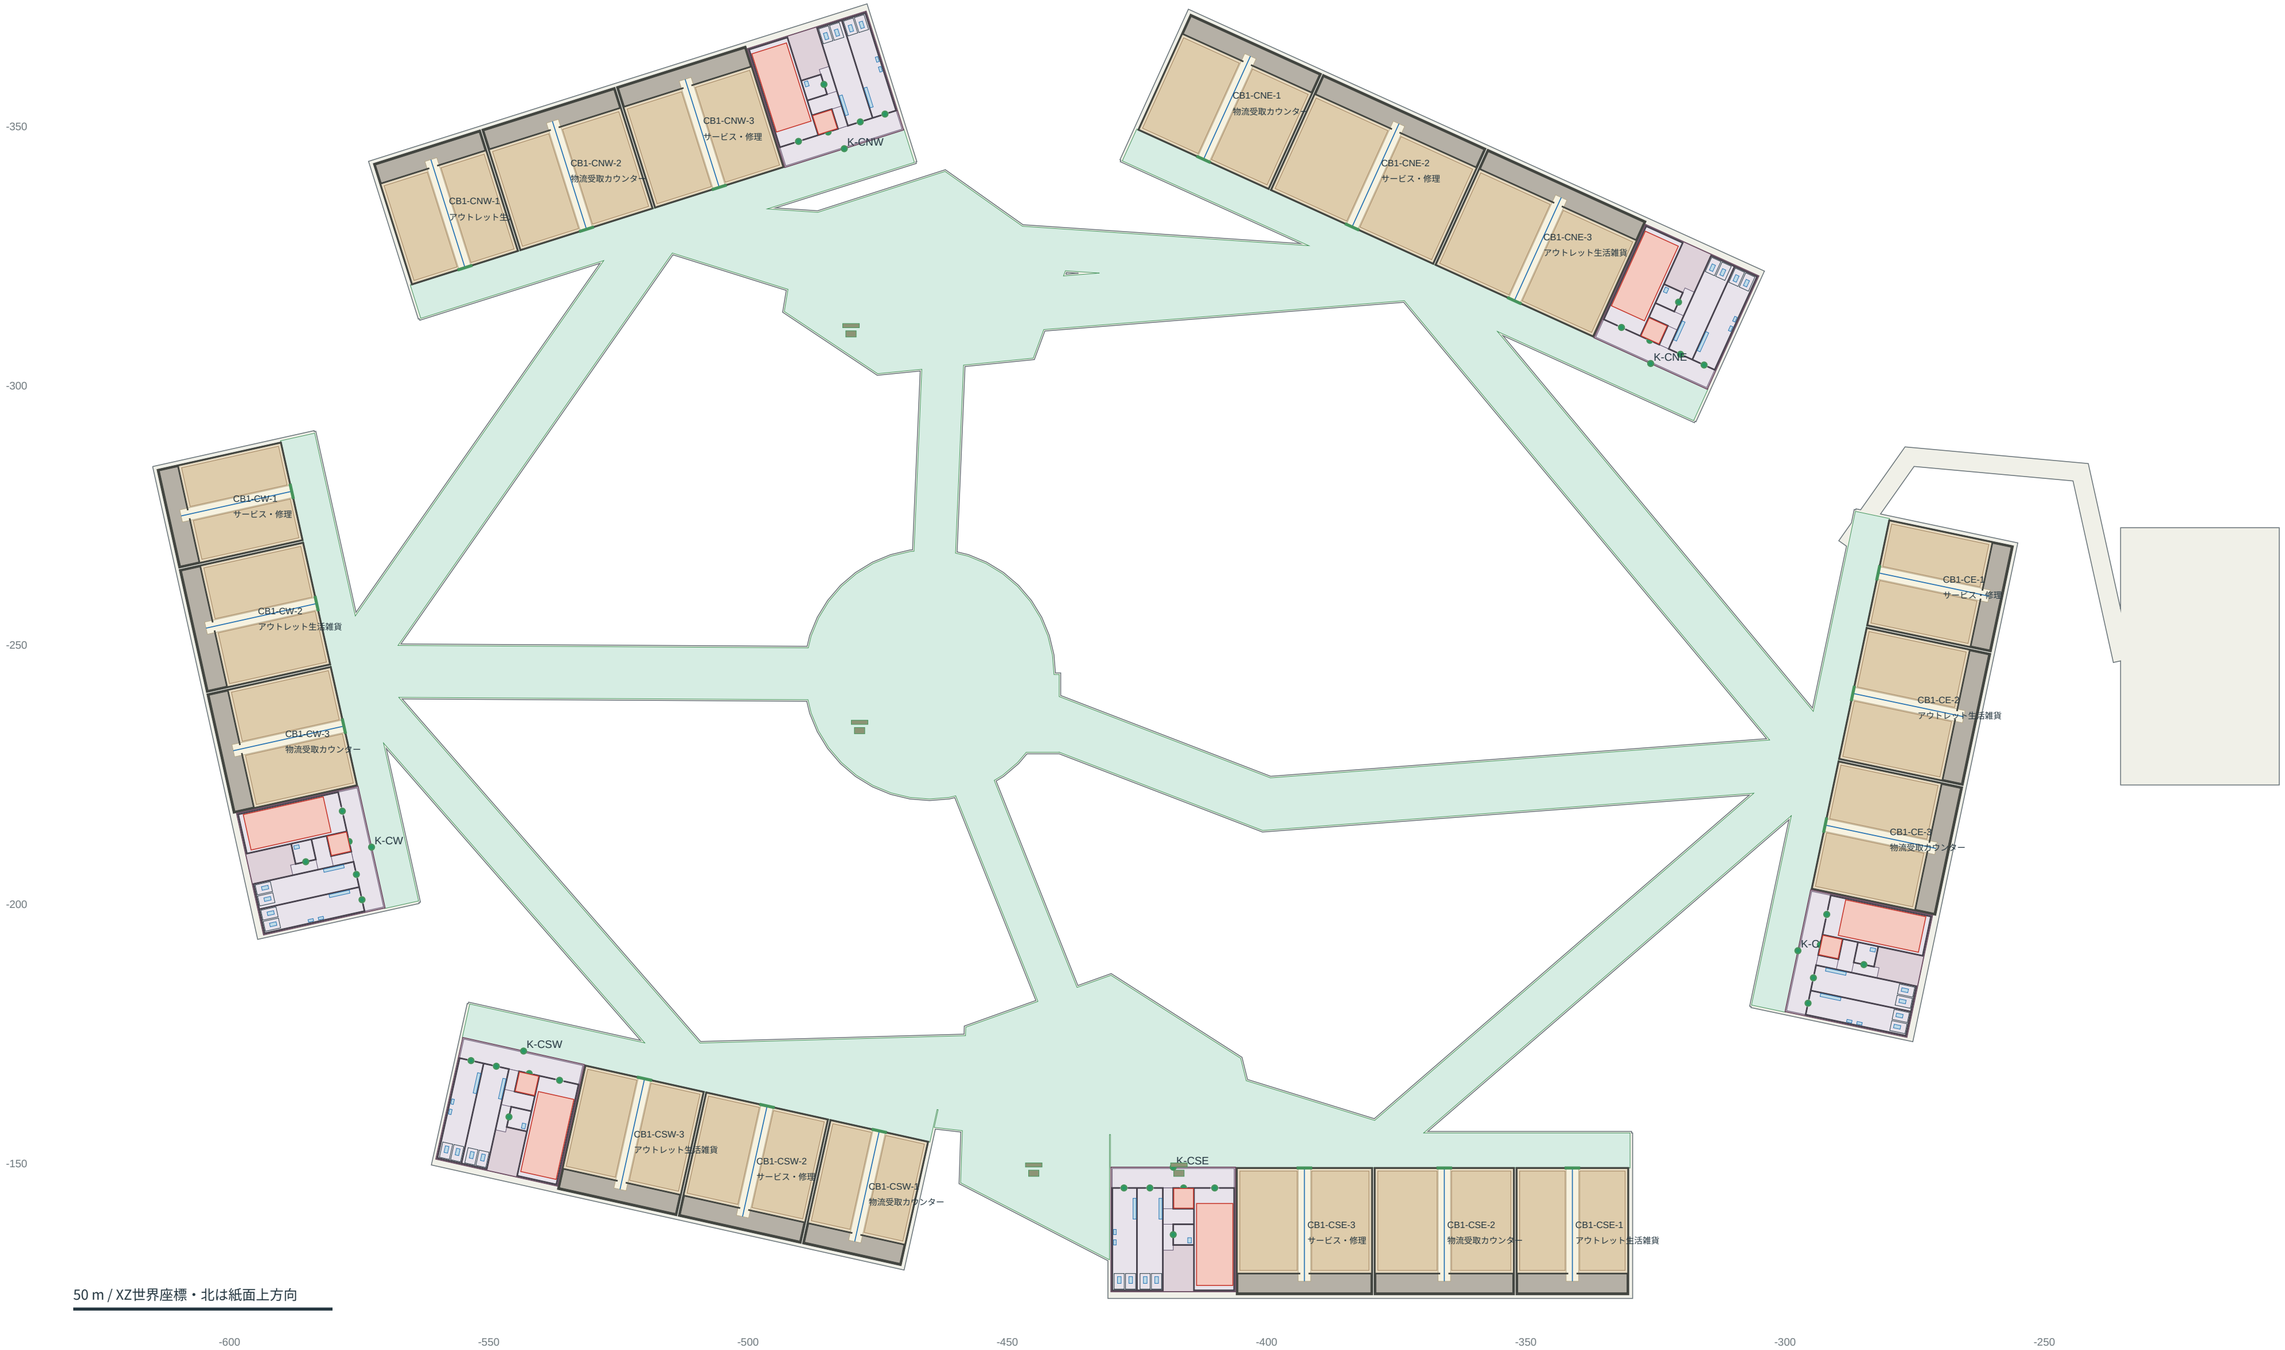

C館 B1｜詳細拡大 1/2

入口幅・売場主路・バックルーム・設備室を原ポリゴンで表示 / 範囲X -618.8〜-405.8m

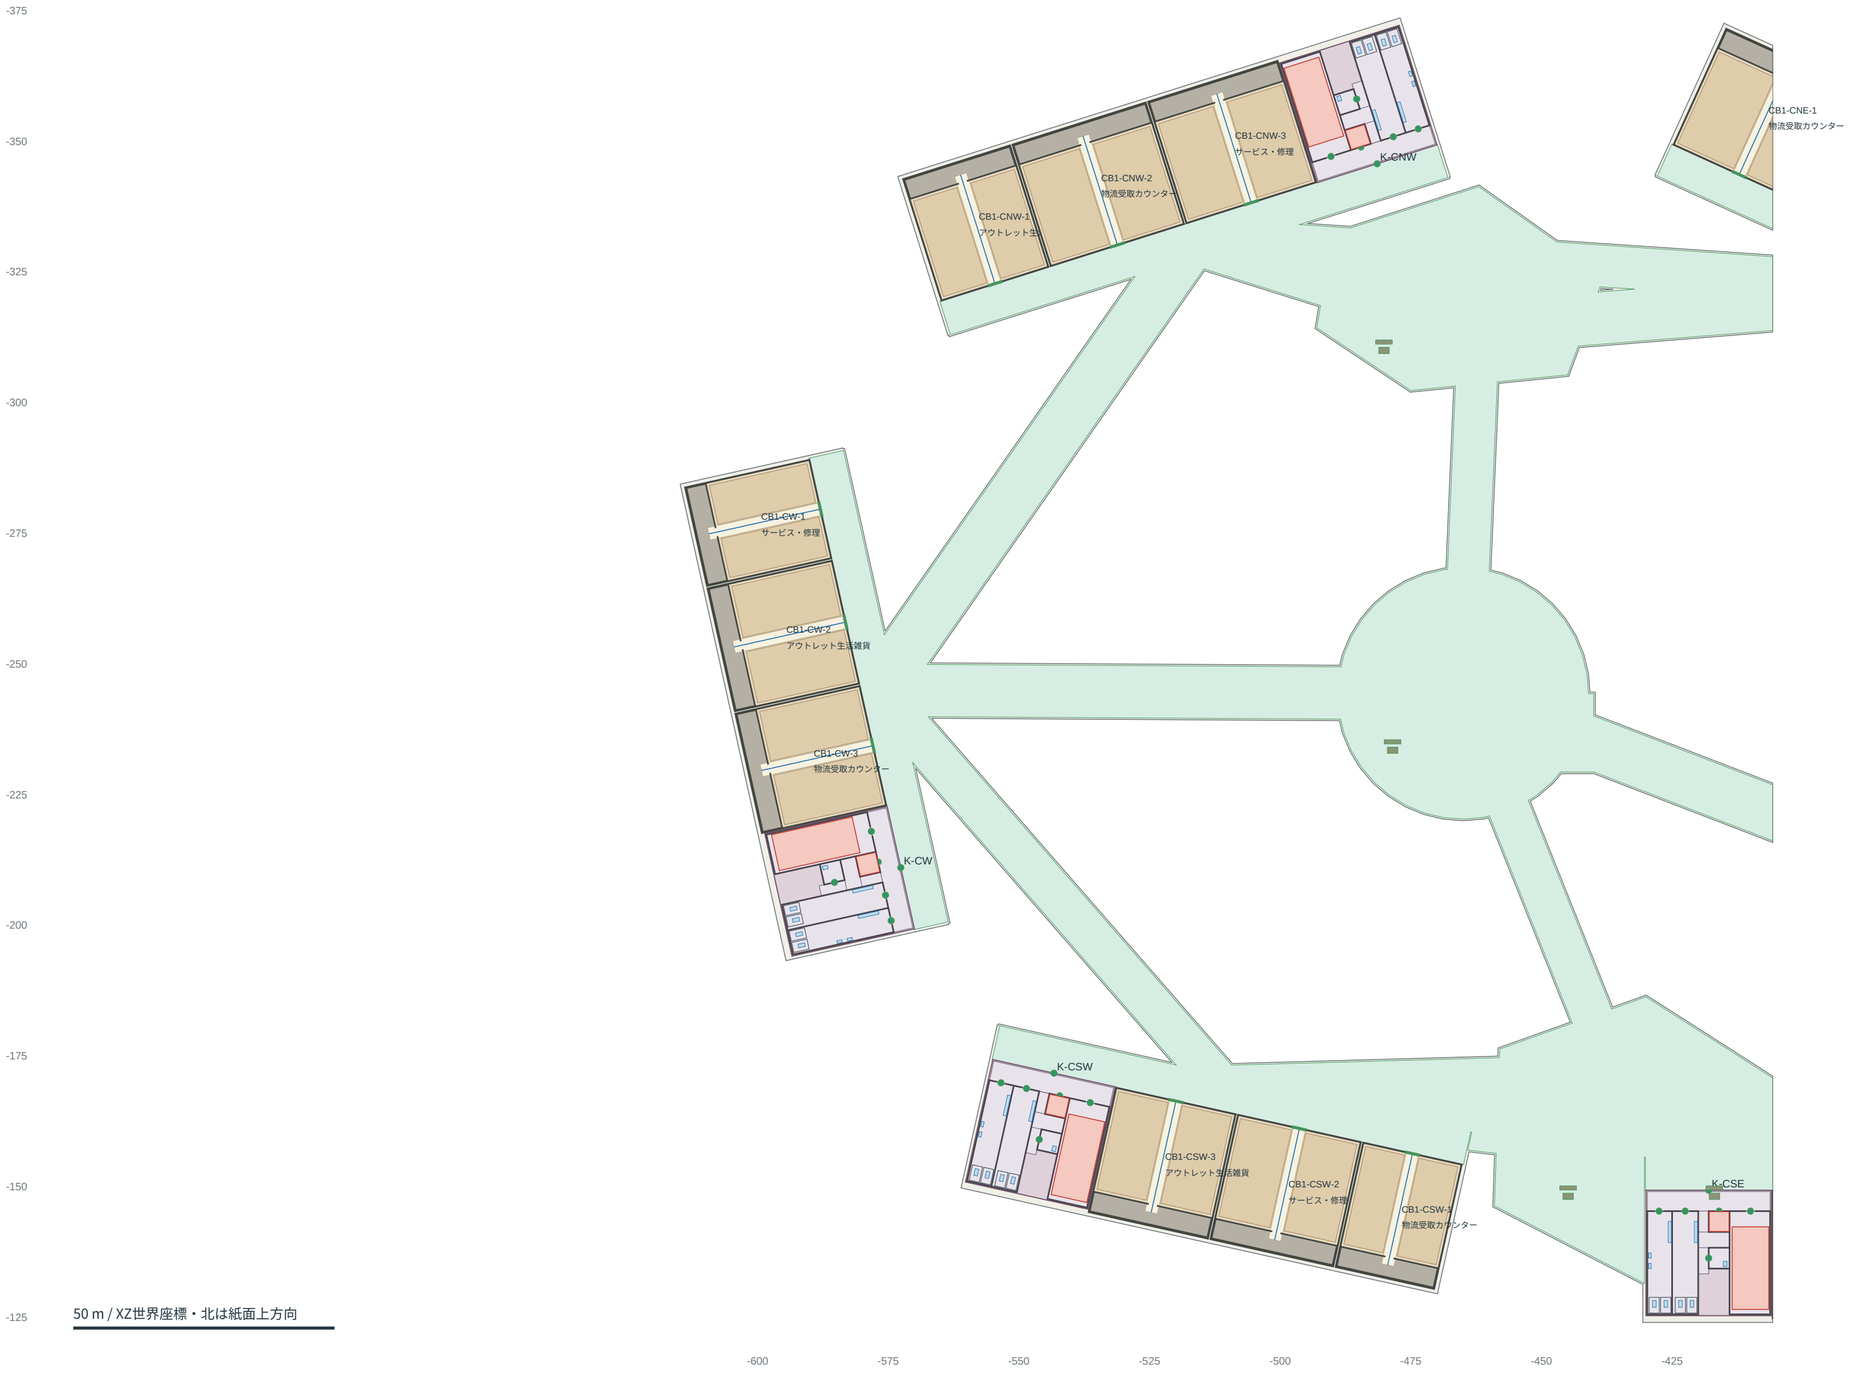

C館 B1｜詳細拡大 2/2

入口幅・売場主路・バックルーム・設備室を原ポリゴンで表示 / 範囲X -413.8〜-200.7m

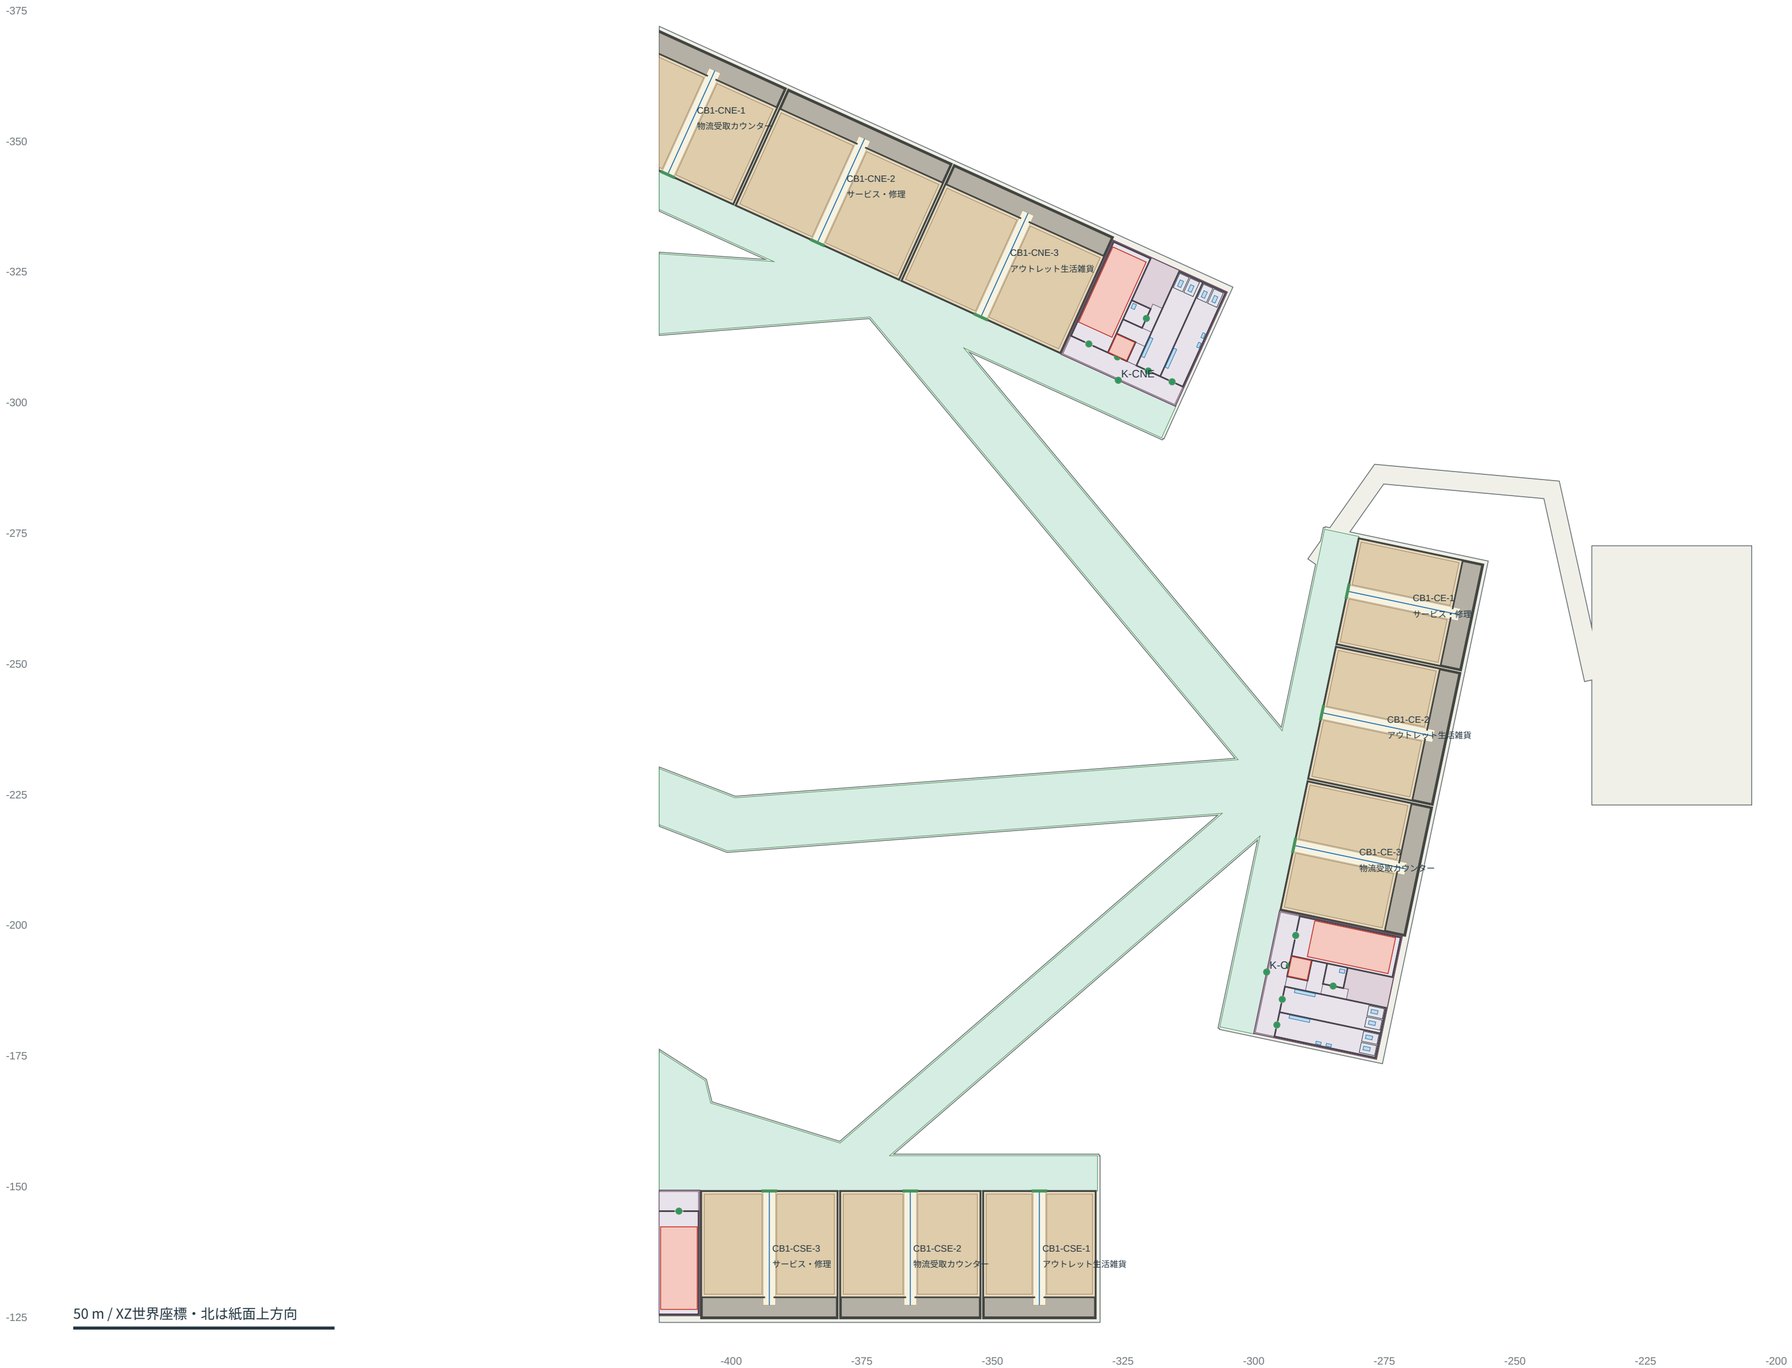

C館 1F｜詳細平面図 全体

既存内部形状を維持 / Y=+0.000m / 区画数 18 / 入口緑線・主路青線・バックルーム灰。赤の局所案は未適用。

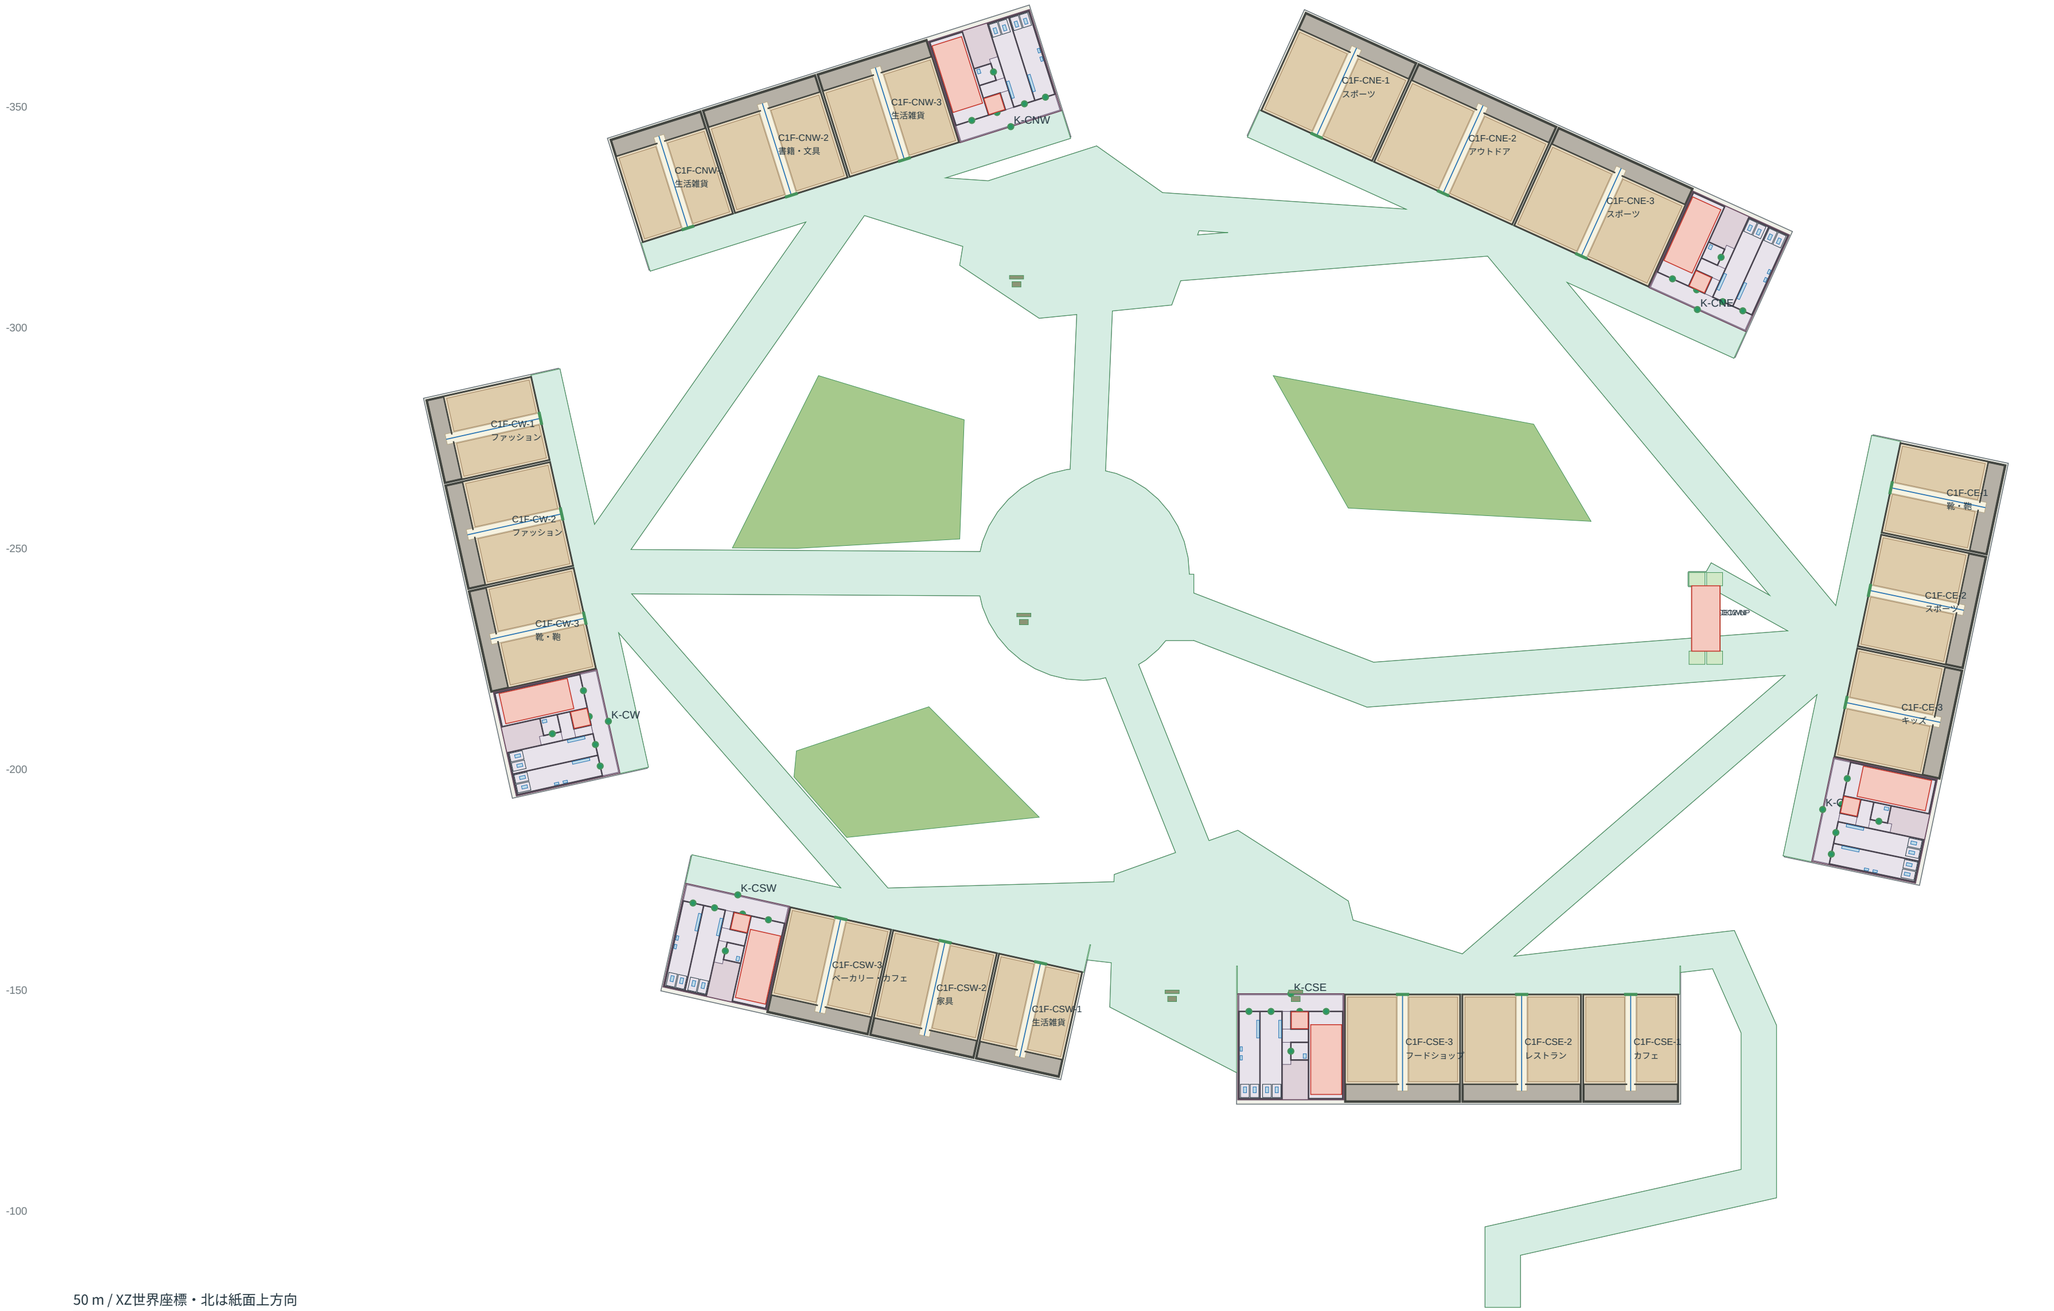

C館 1F｜詳細拡大 1/2

入口幅・売場主路・バックルーム・設備室を原ポリゴンで表示 / 範囲X -618.5〜-431.0m

C館 1F｜詳細拡大 2/2

入口幅・売場主路・バックルーム・設備室を原ポリゴンで表示 / 範囲X -439.0〜-251.5m

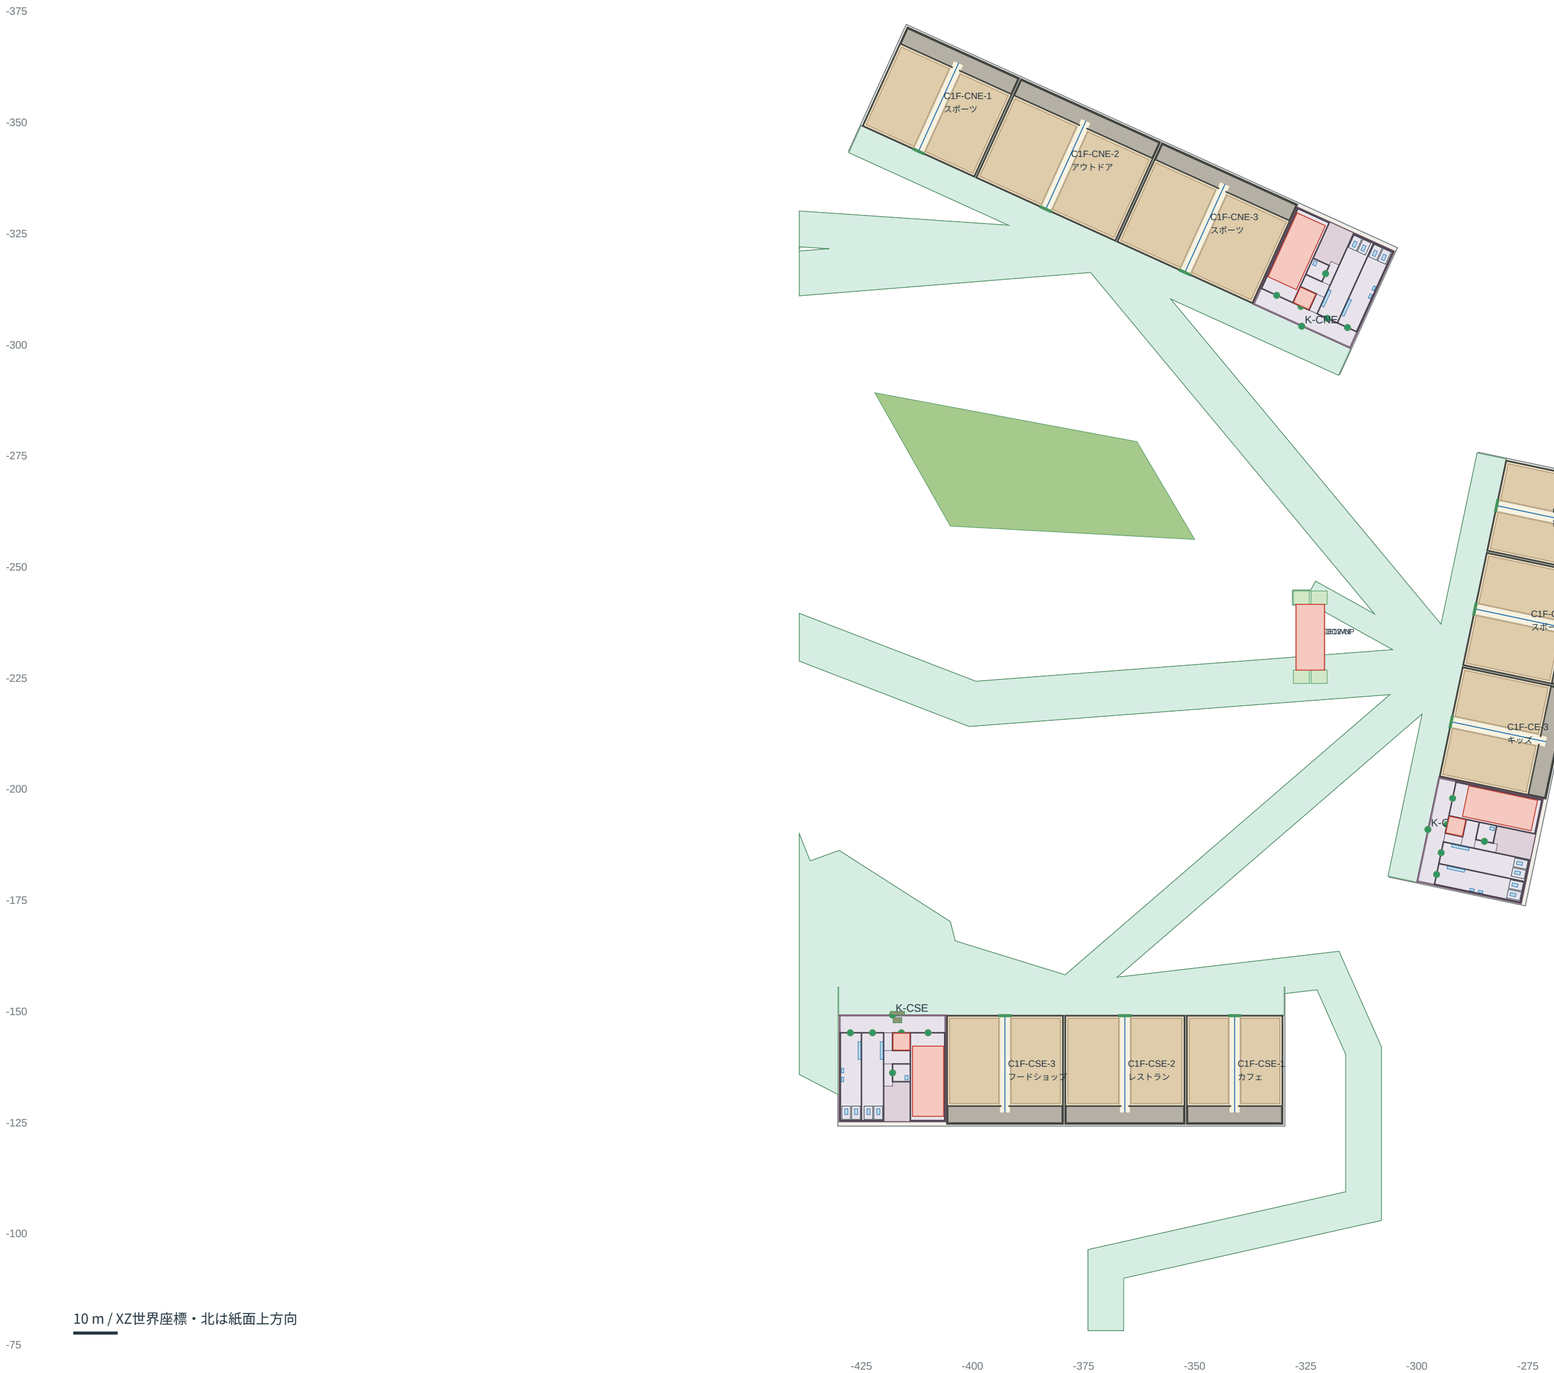

C館 2F｜詳細平面図 全体

既存内部形状を維持 / Y=+5.525m / 区画数 18 / 入口緑線・主路青線・バックルーム灰。赤の局所案は未適用。

C館 2F｜詳細拡大 1/2

入口幅・売場主路・バックルーム・設備室を原ポリゴンで表示 / 範囲X -618.5〜-431.0m

C館 2F｜詳細拡大 2/2

入口幅・売場主路・バックルーム・設備室を原ポリゴンで表示 / 範囲X -439.0〜-251.5m

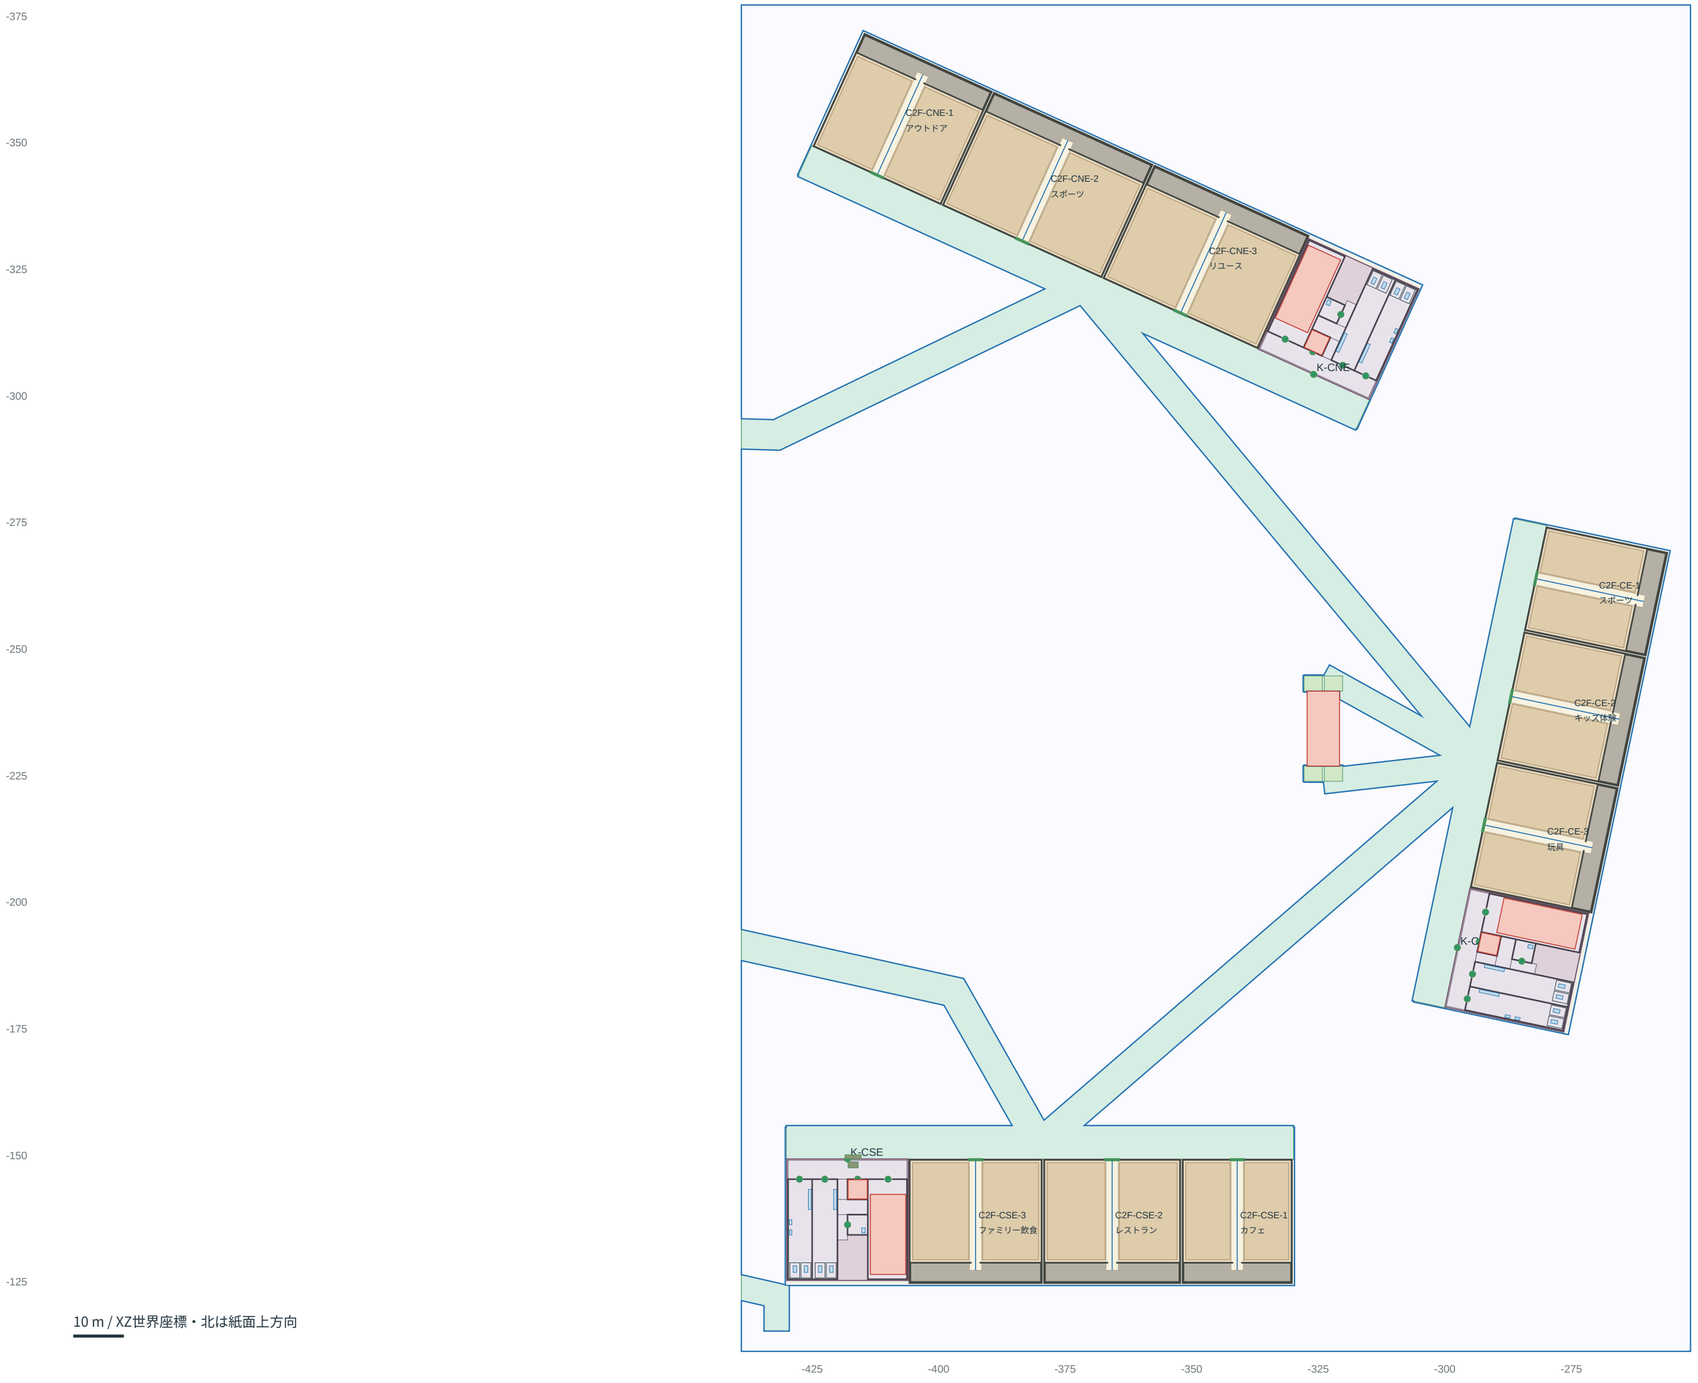

10 m / XZ世界座標・北は紙面上方向

C館 3F｜詳細平面図 全体

既存内部形状を維持 / Y=+10.875m / 区画数 18 / 入口緑線・主路青線・バックルーム灰。赤の局所案は未適用。

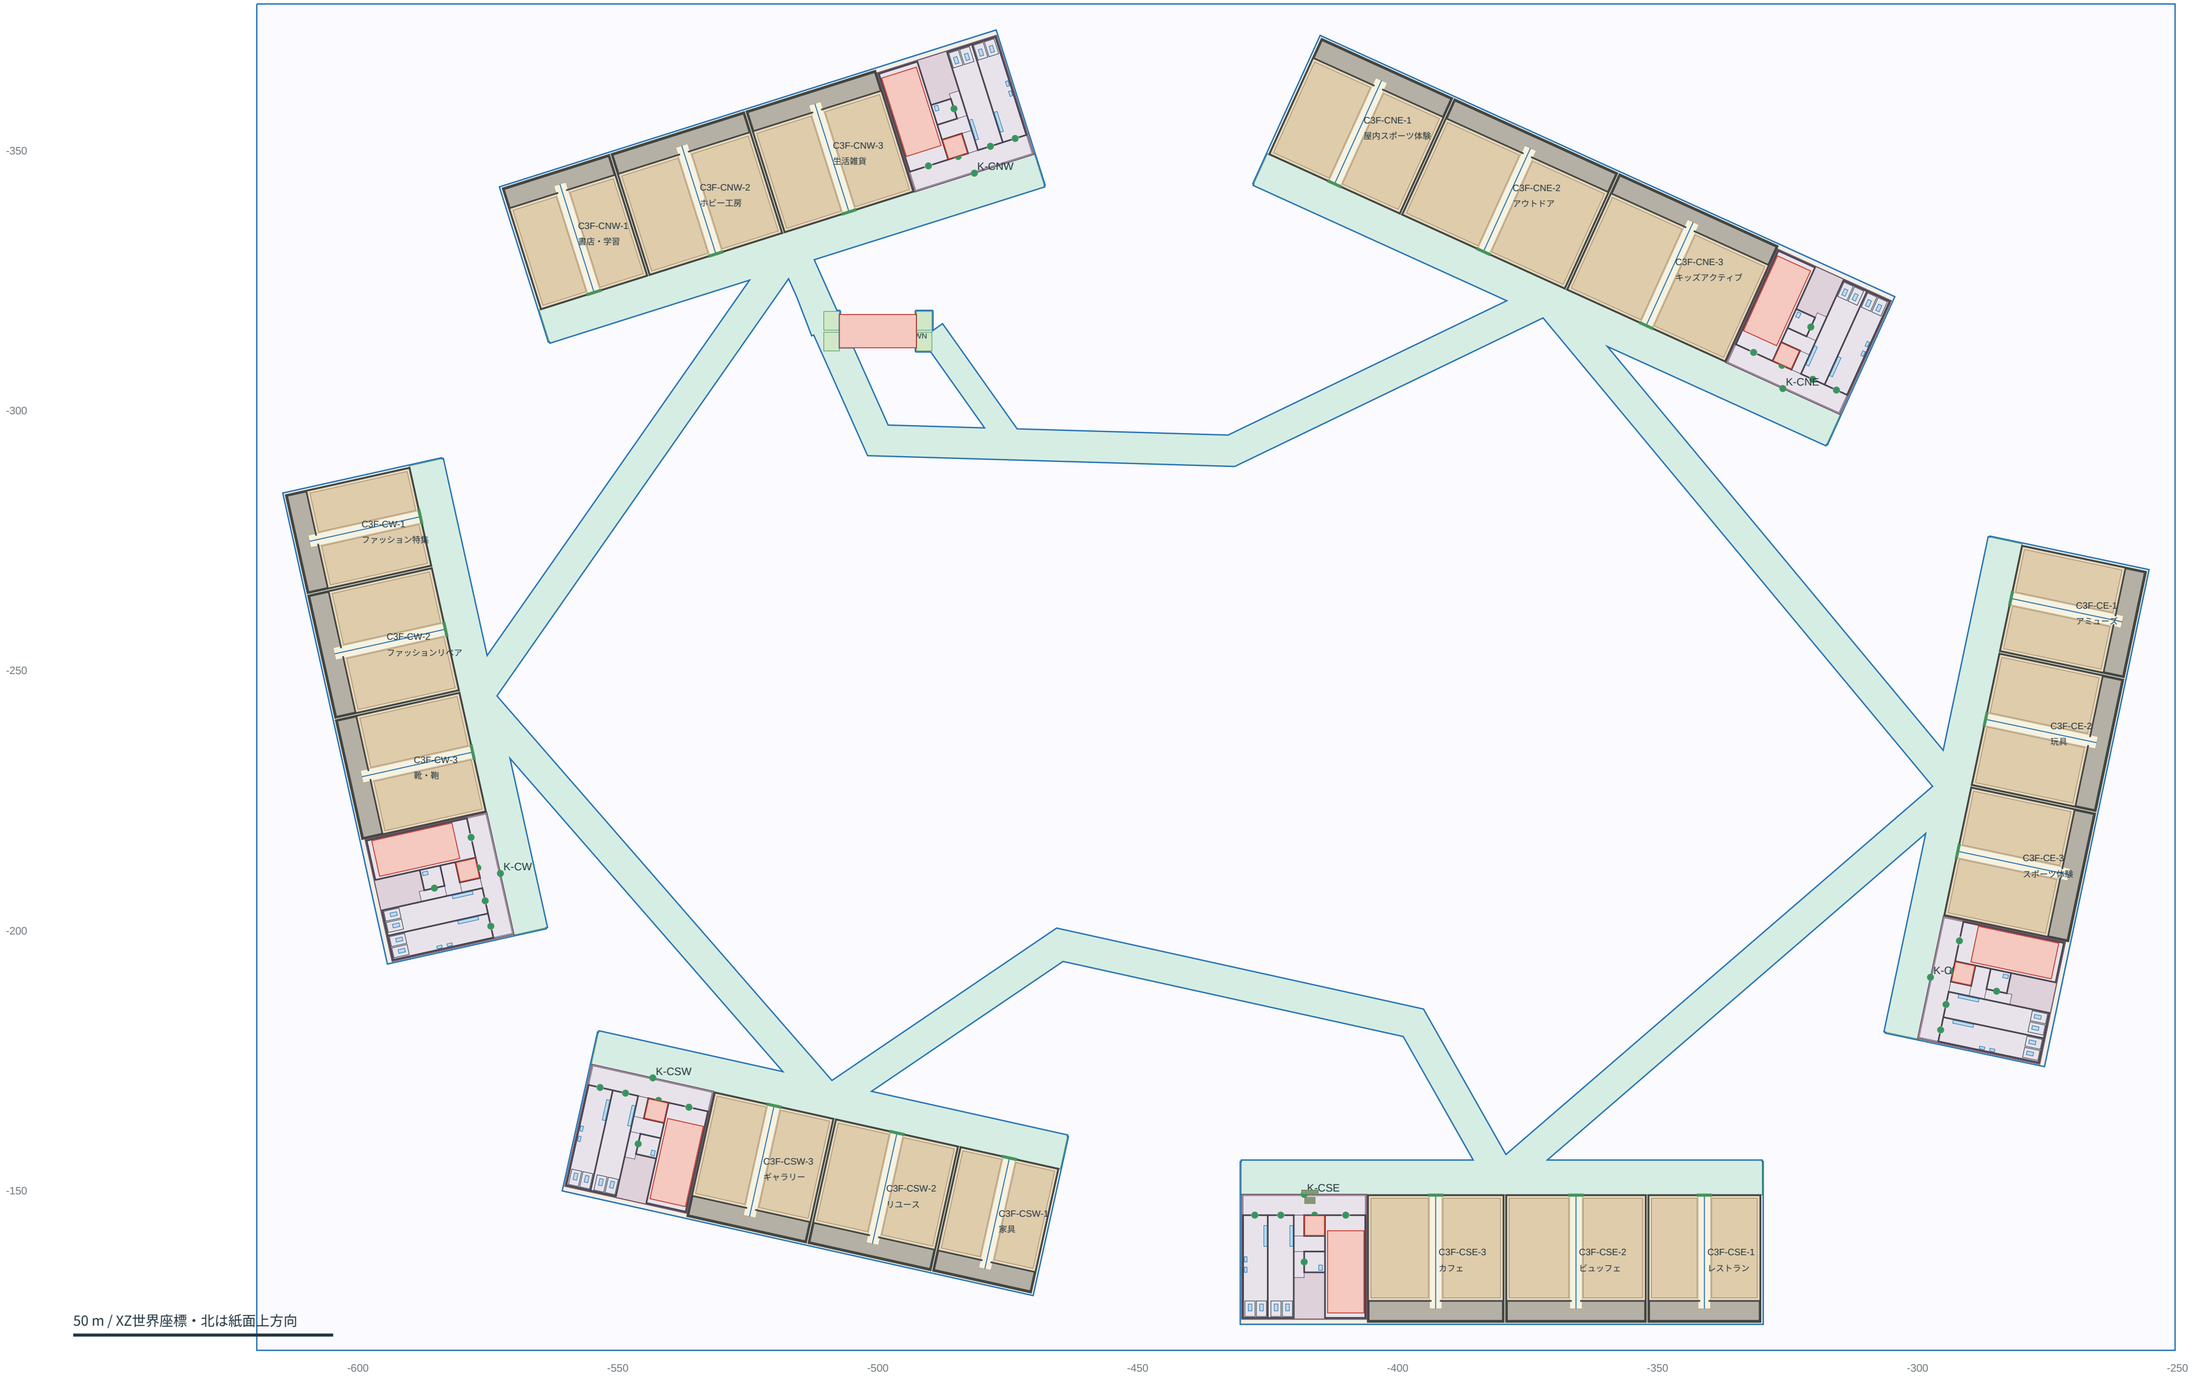

C館 3F｜詳細拡大 1/2

入口幅・売場主路・バックルーム・設備室を原ポリゴンで表示 / 範囲X -618.5〜-431.0m

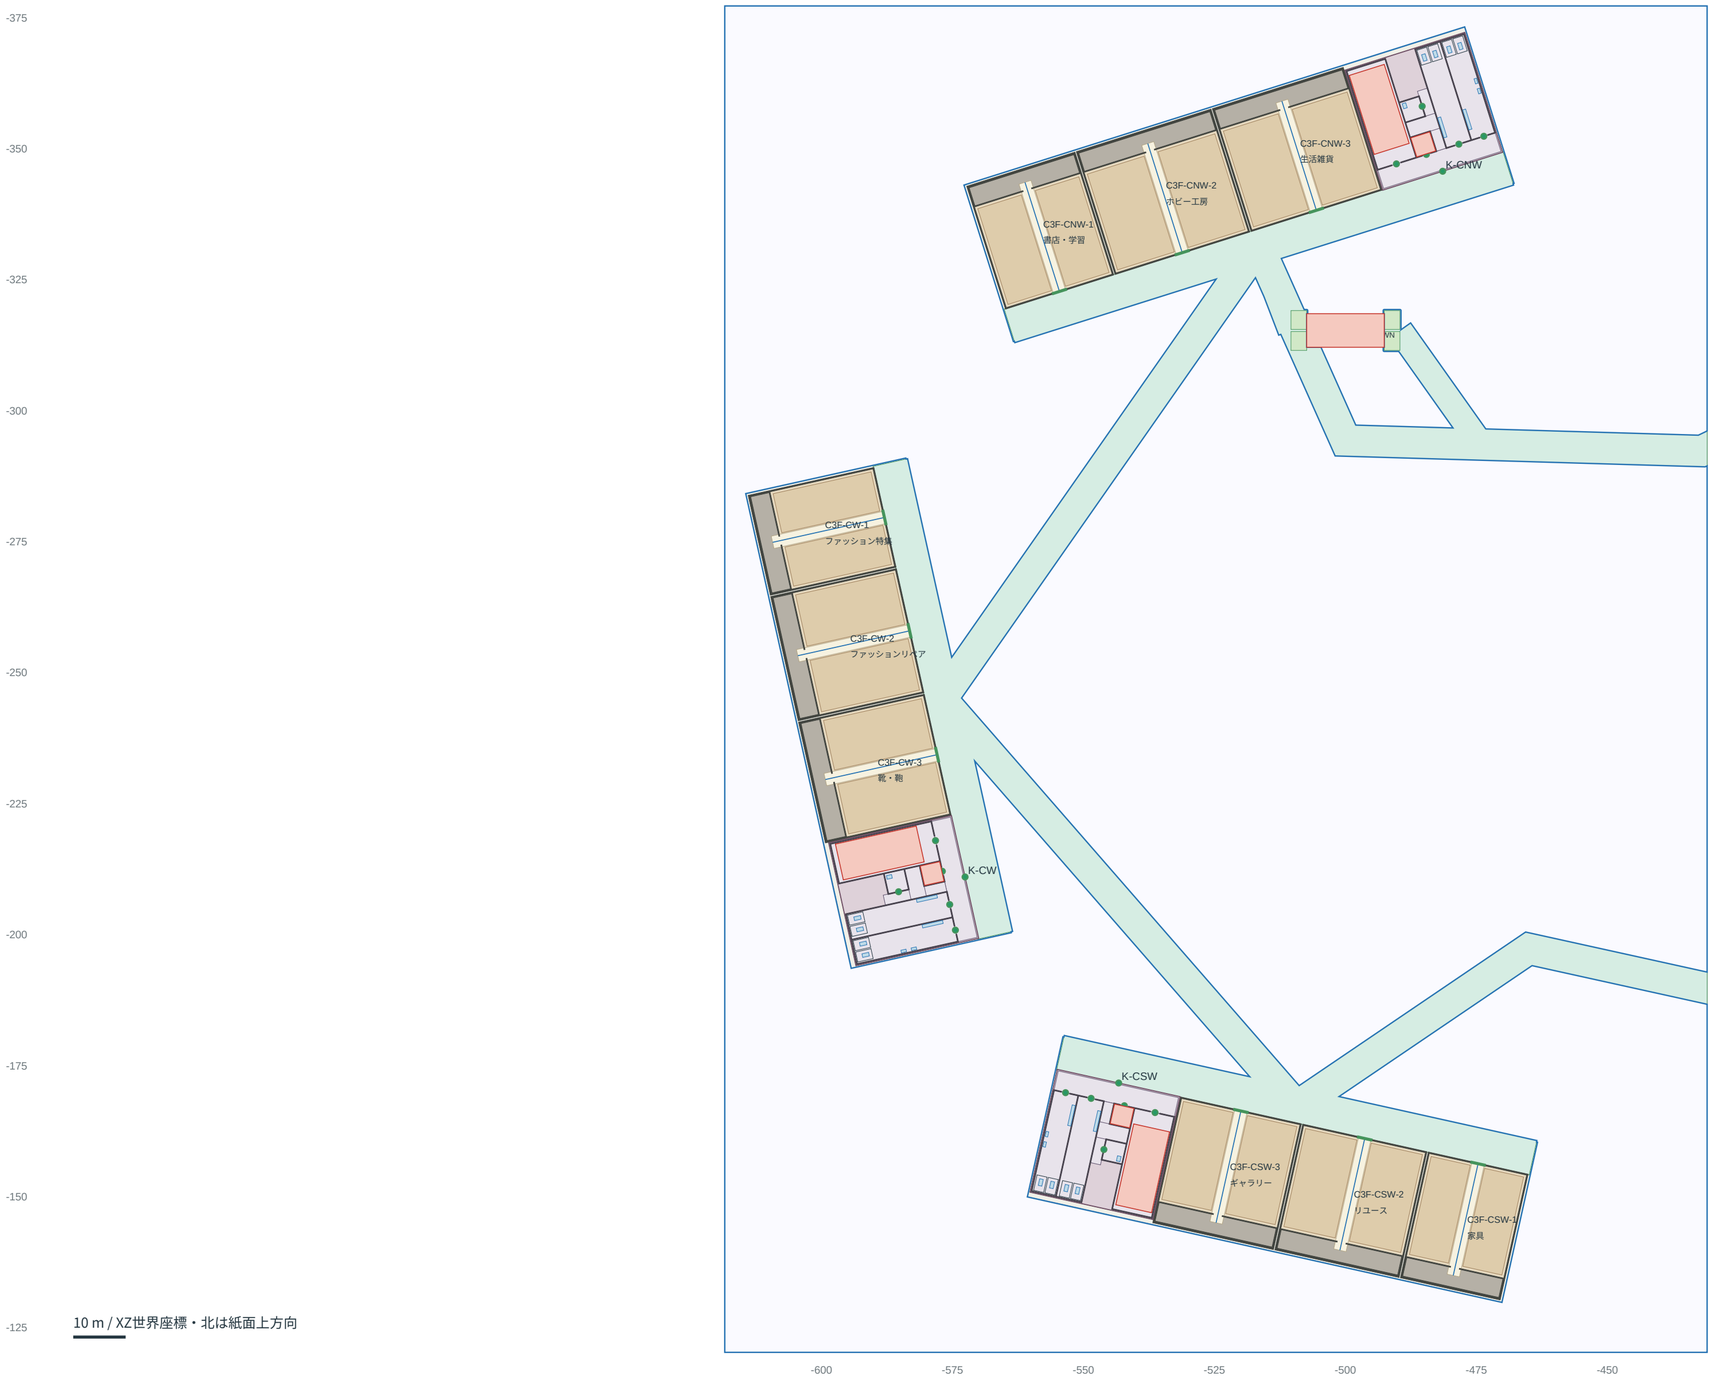

C館 3F｜詳細拡大 2/2

入口幅・売場主路・バックルーム・設備室を原ポリゴンで表示 / 範囲X -439.0〜-251.5m

C館 RF｜詳細平面図 全体

既存内部形状を維持 / Y=+16.400m / 区画数 6 / 入口緑線・主路青線・バックルーム灰。赤の局所案は未適用。

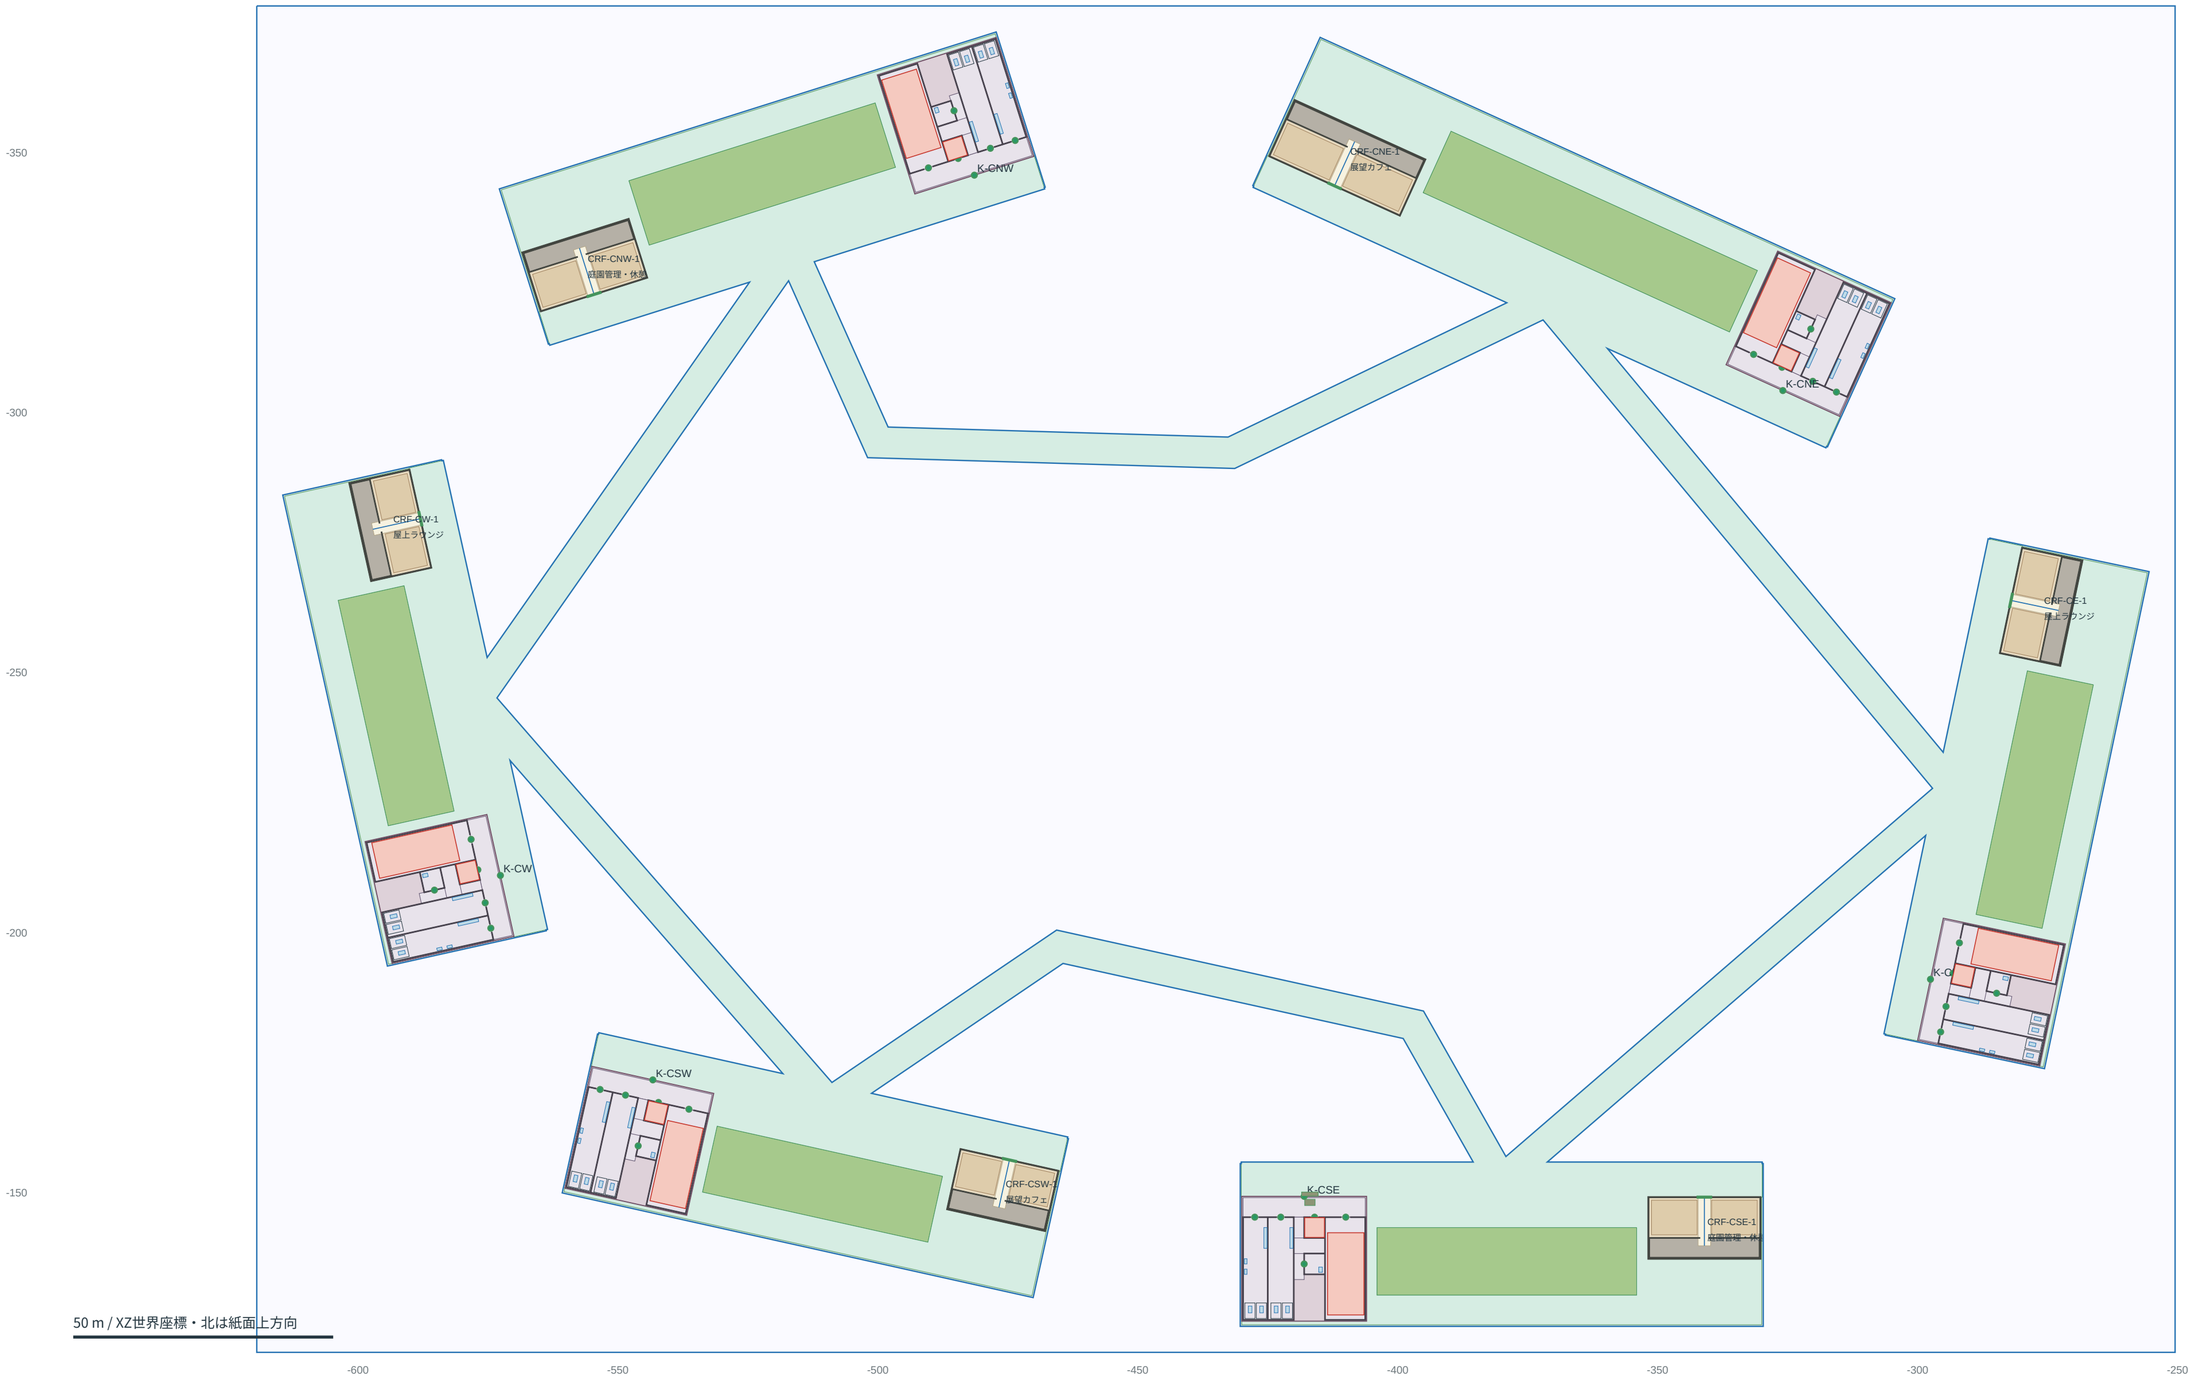

C館 RF｜詳細拡大 1/2

入口幅・売場主路・バックルーム・設備室を原ポリゴンで表示 / 範囲X -618.5〜-431.0m

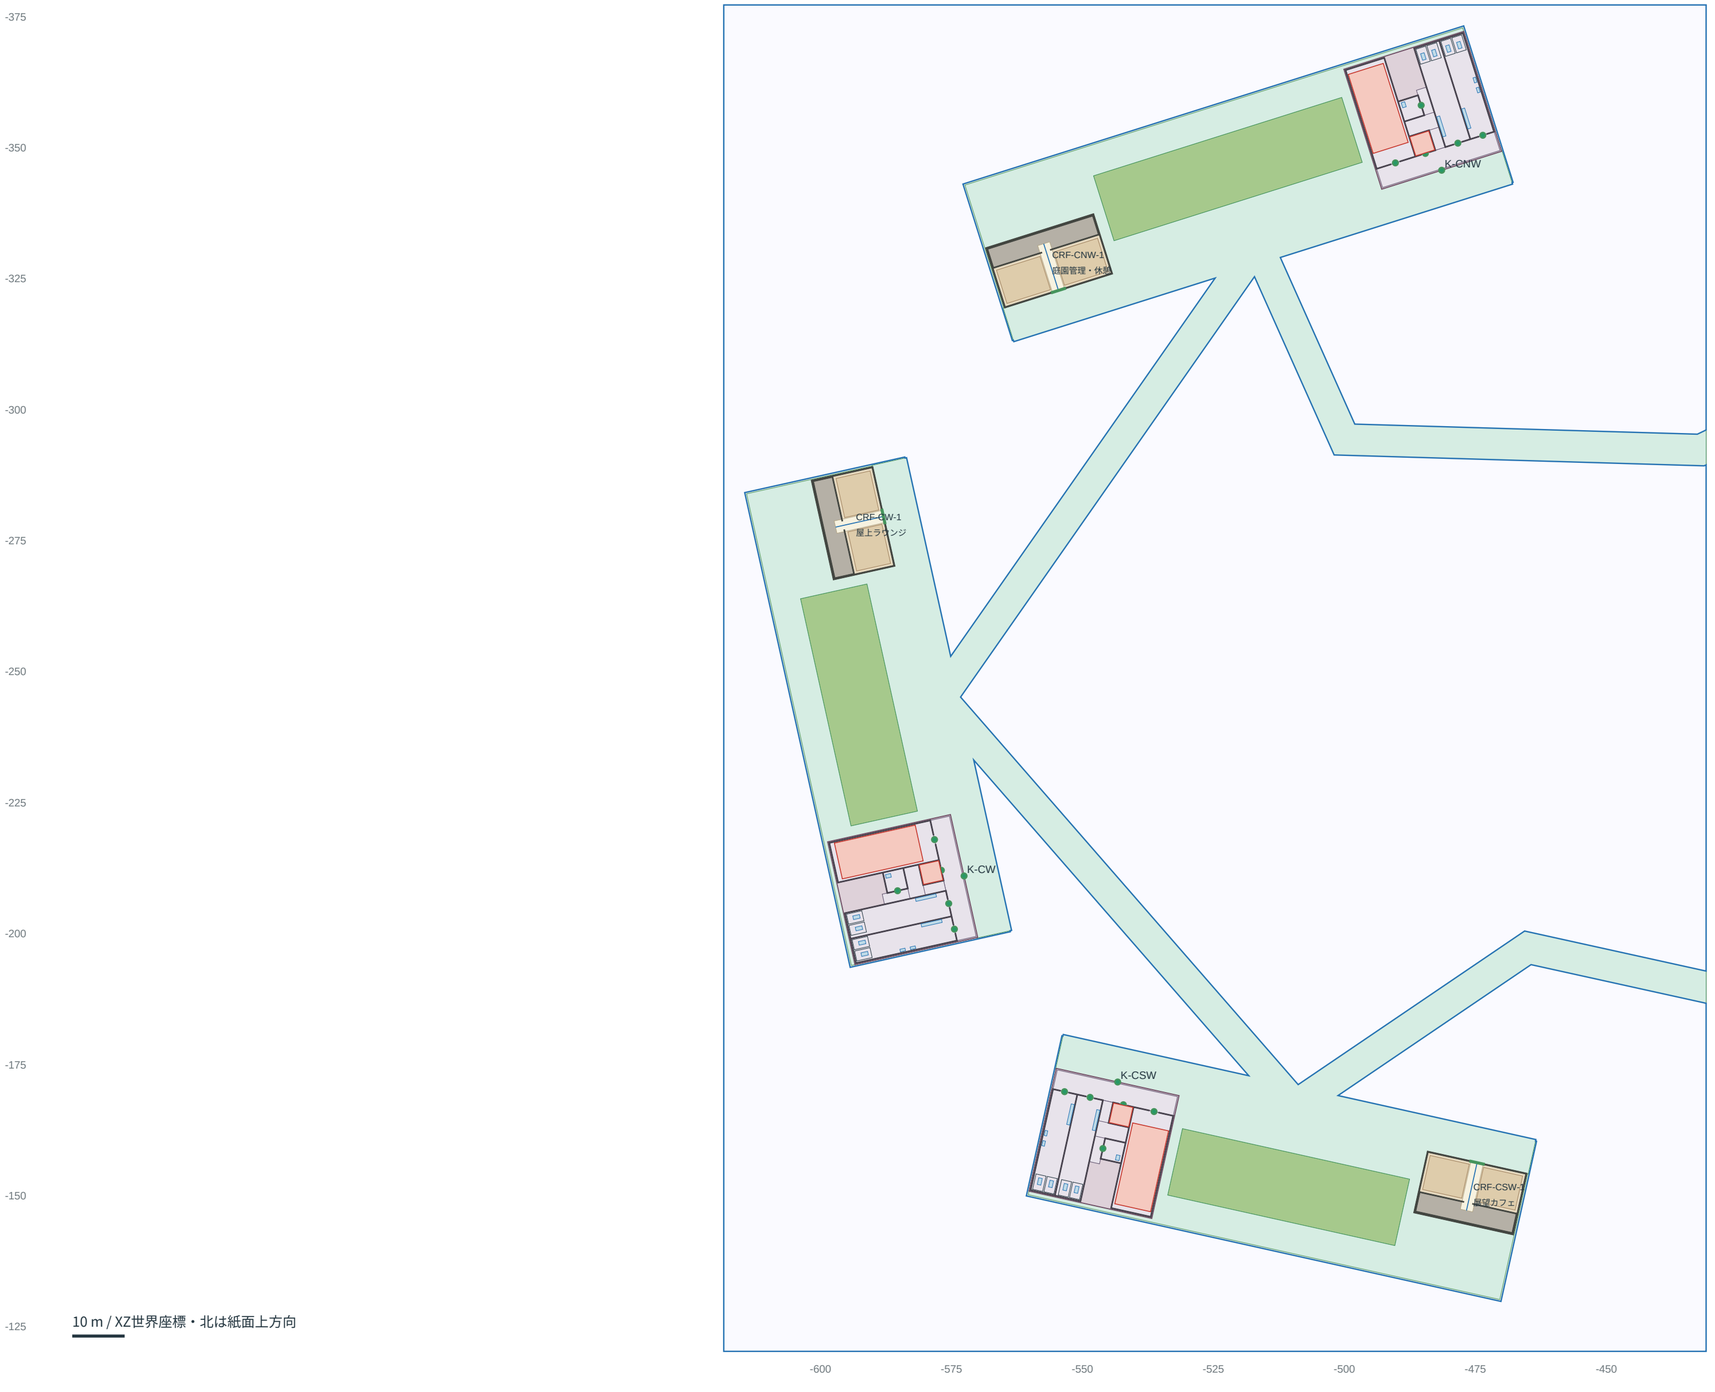

C館 RF｜詳細拡大 2/2

入口幅・売場主路・バックルーム・設備室を原ポリゴンで表示 / 範囲X -439.0〜-251.5m

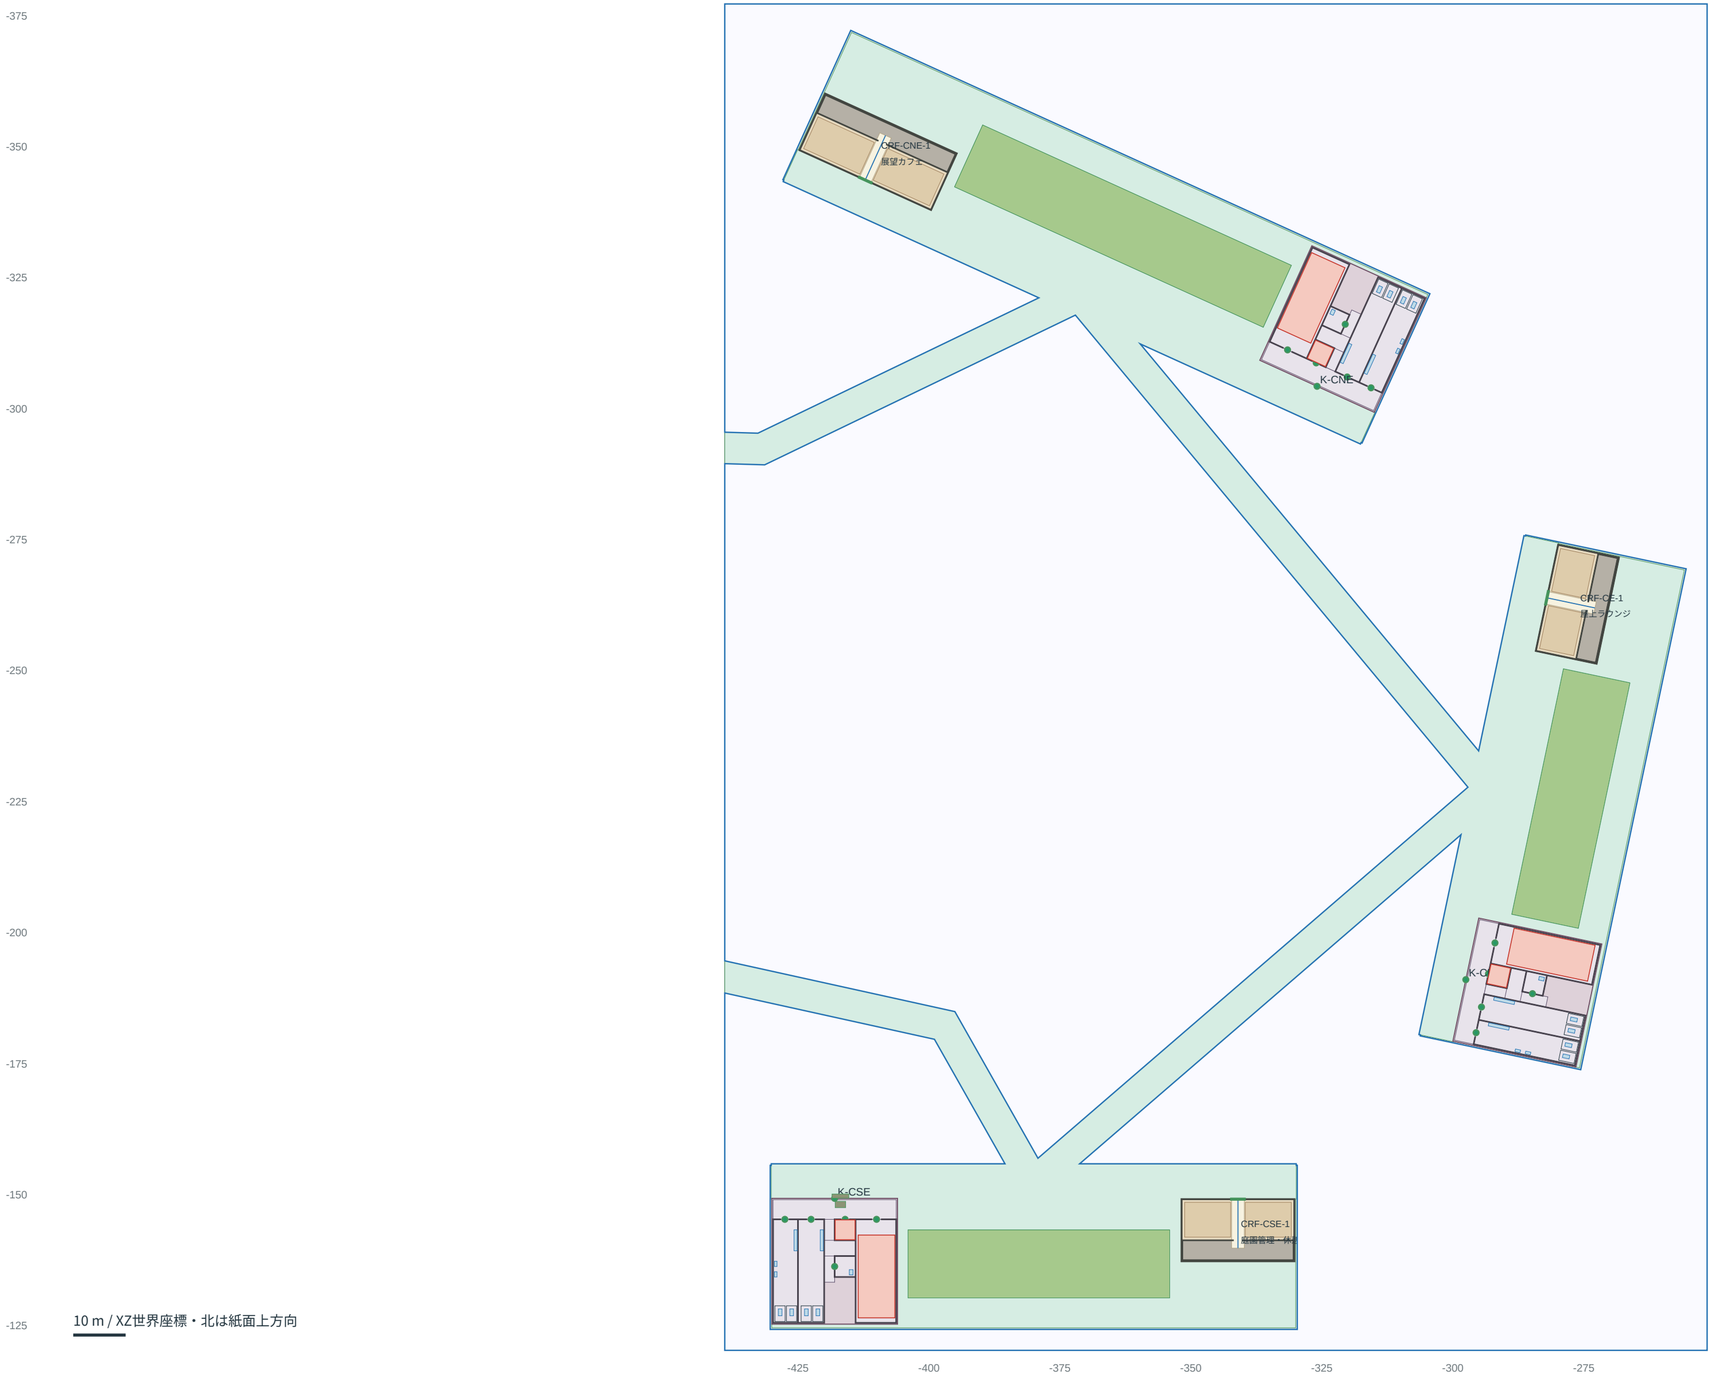

新来客玄関の局所案｜B-NEW-SW-CUSTOMER-1F

未適用。館内の原通路・店舗区画・広場を変更せず、外周閉鎖帯の局所だけを開口する案。

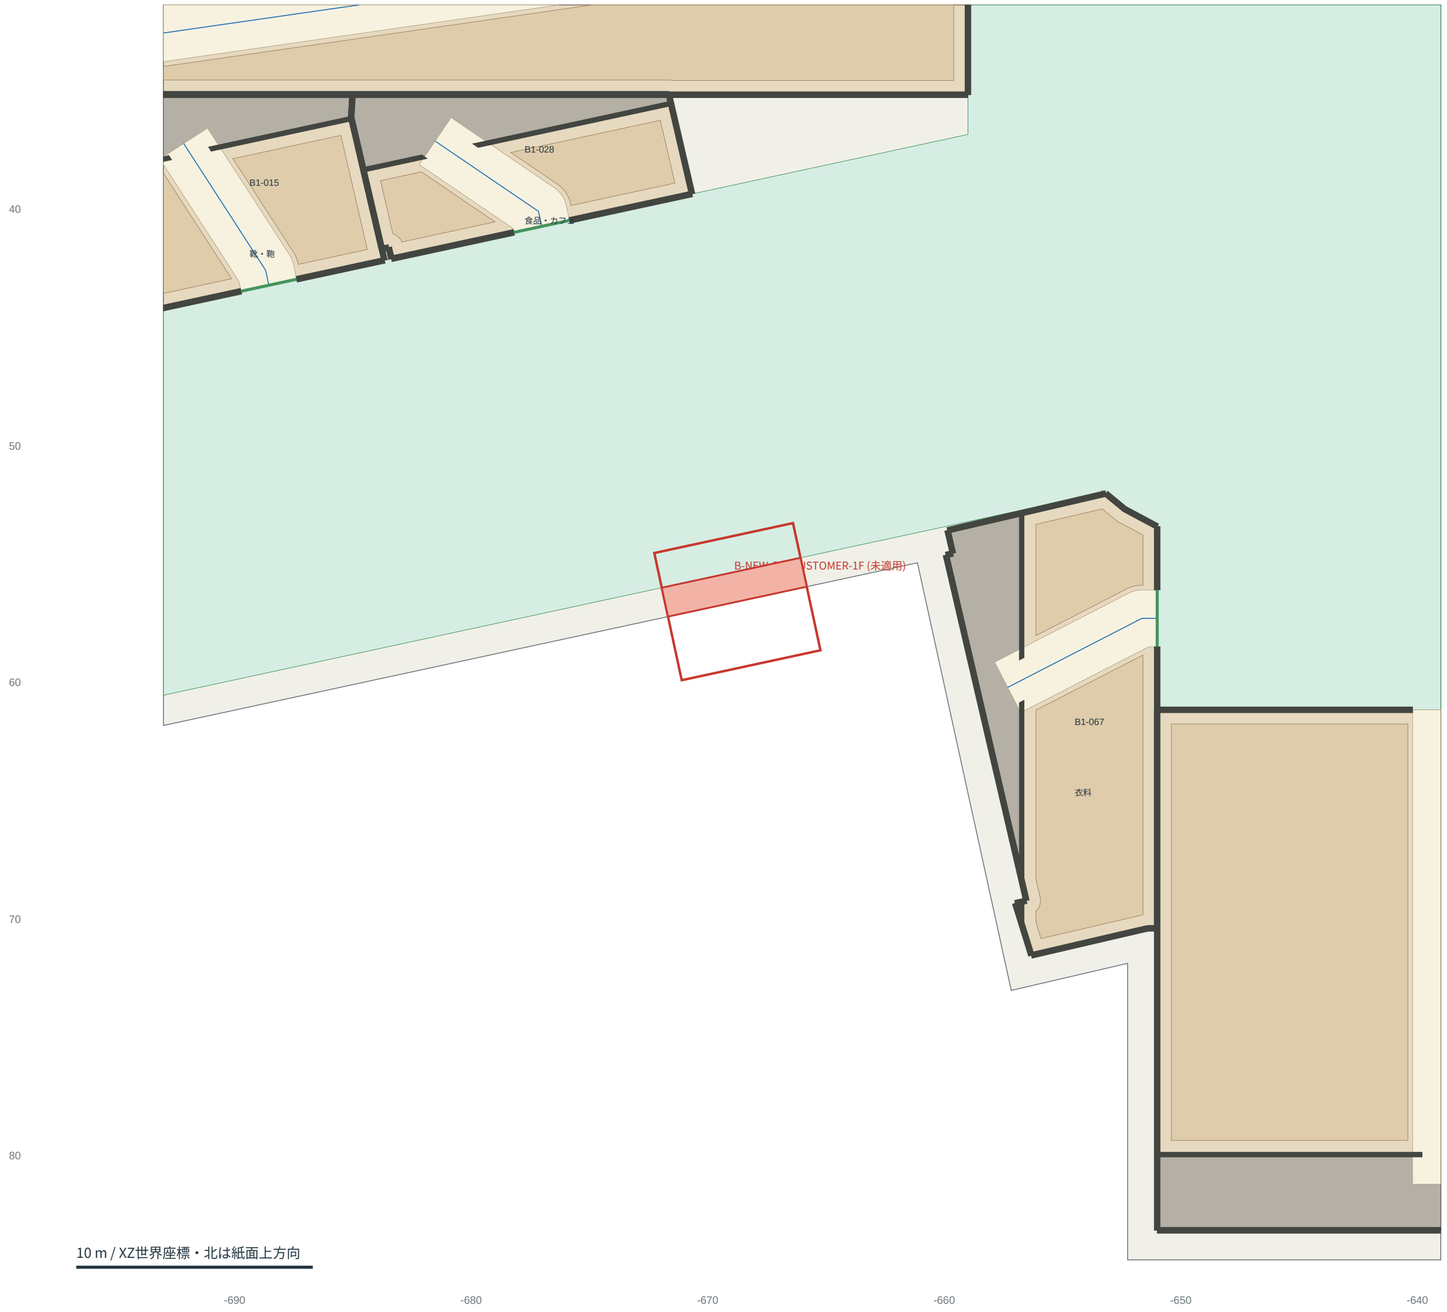

玄関幅 6.0m / Y 0.000m

既存店舗・設備核との重なり 0.000000000㎡

外壁/閉鎖帯の局所開口 7.501㎡

新玄関床支持 16.499㎡

到着橋/地上歩道はこの案の承認が前提。自動実装補正で解決した扱いにしない。

B館v4.1 1〜3Fの原本、A館v1原本、ゲーム本体はいずれも未変更。

新来客玄関の局所案｜A-NEW-EAST-2F

未適用。館内の原通路・店舗区画・広場を変更せず、外周閉鎖帯の局所だけを開口する案。

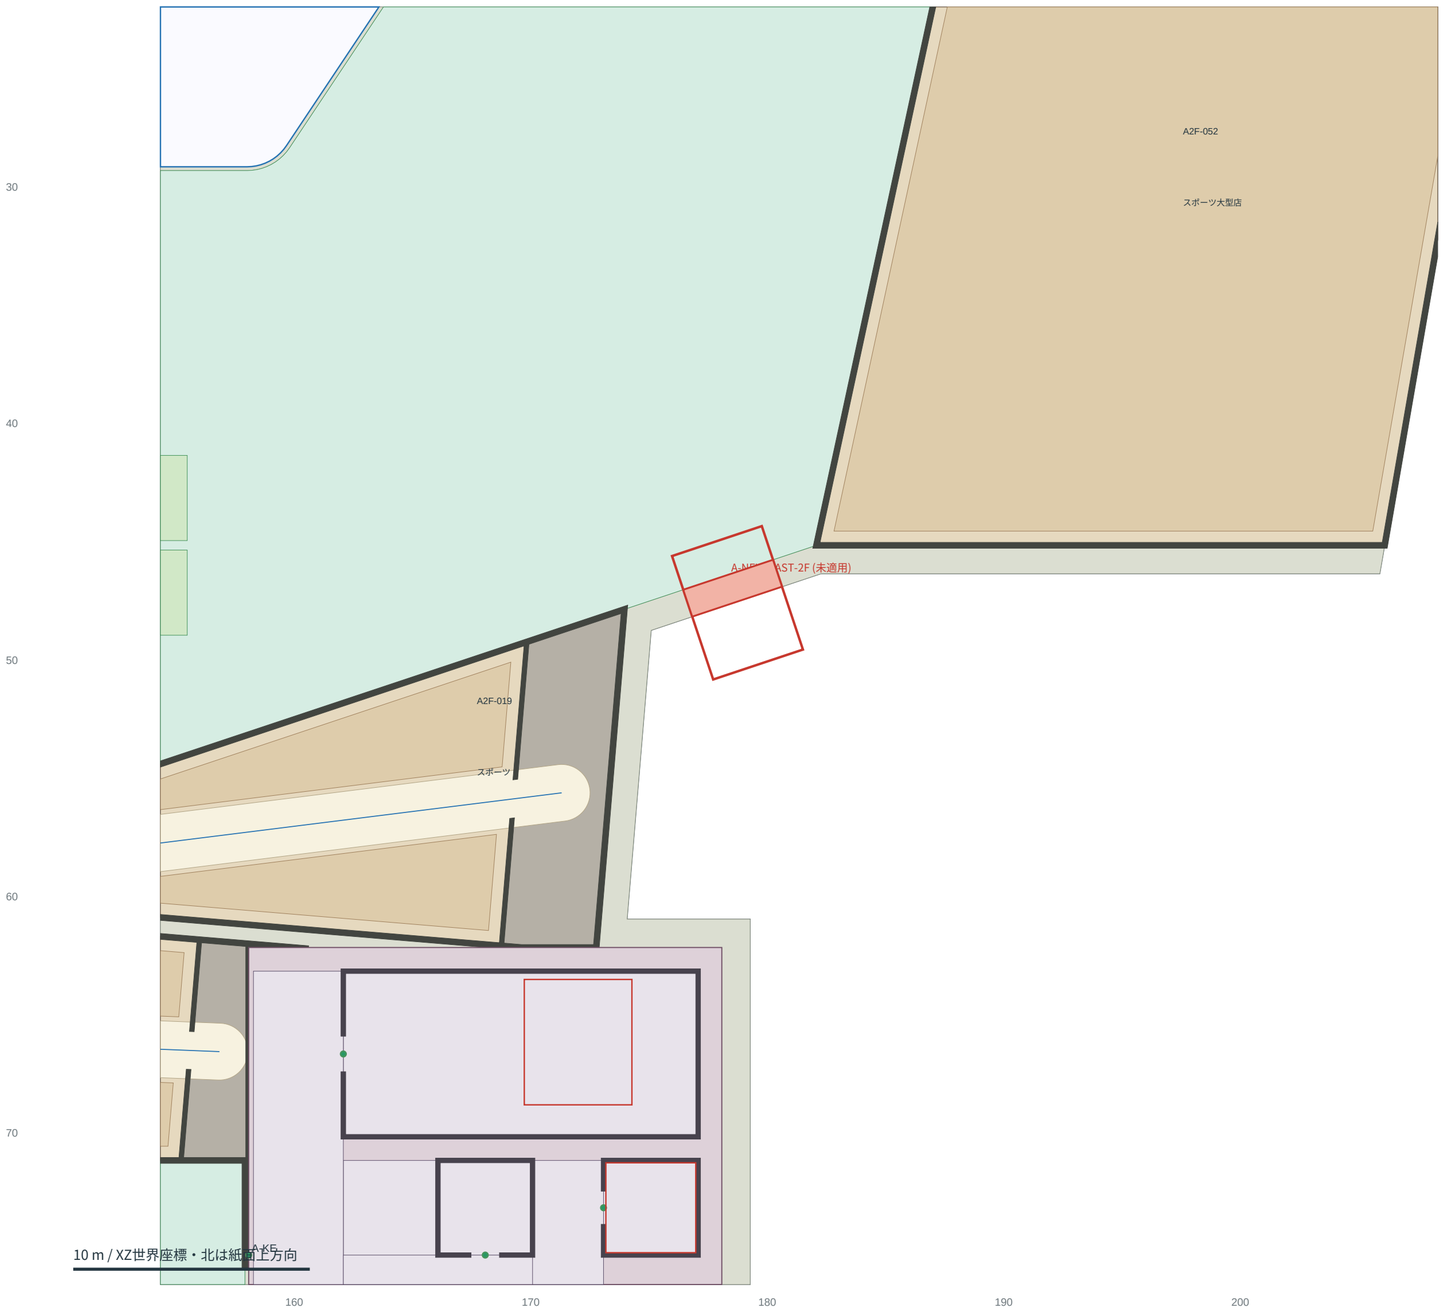

玄関幅 4.0m / Y 5.525m

既存店舗・設備核との重なり 0.000000000㎡

外壁/閉鎖帯の局所開口 4.800㎡

新玄関床支持 11.200㎡

到着橋/地上歩道はこの案の承認が前提。自動実装補正で解決した扱いにしない。

B館v4.1 1〜3Fの原本、A館v1原本、ゲーム本体はいずれも未変更。

新来客玄関の局所案｜A-NEW-SOUTH-2F

未適用。館内の原通路・店舗区画・広場を変更せず、外周閉鎖帯の局所だけを開口する案。

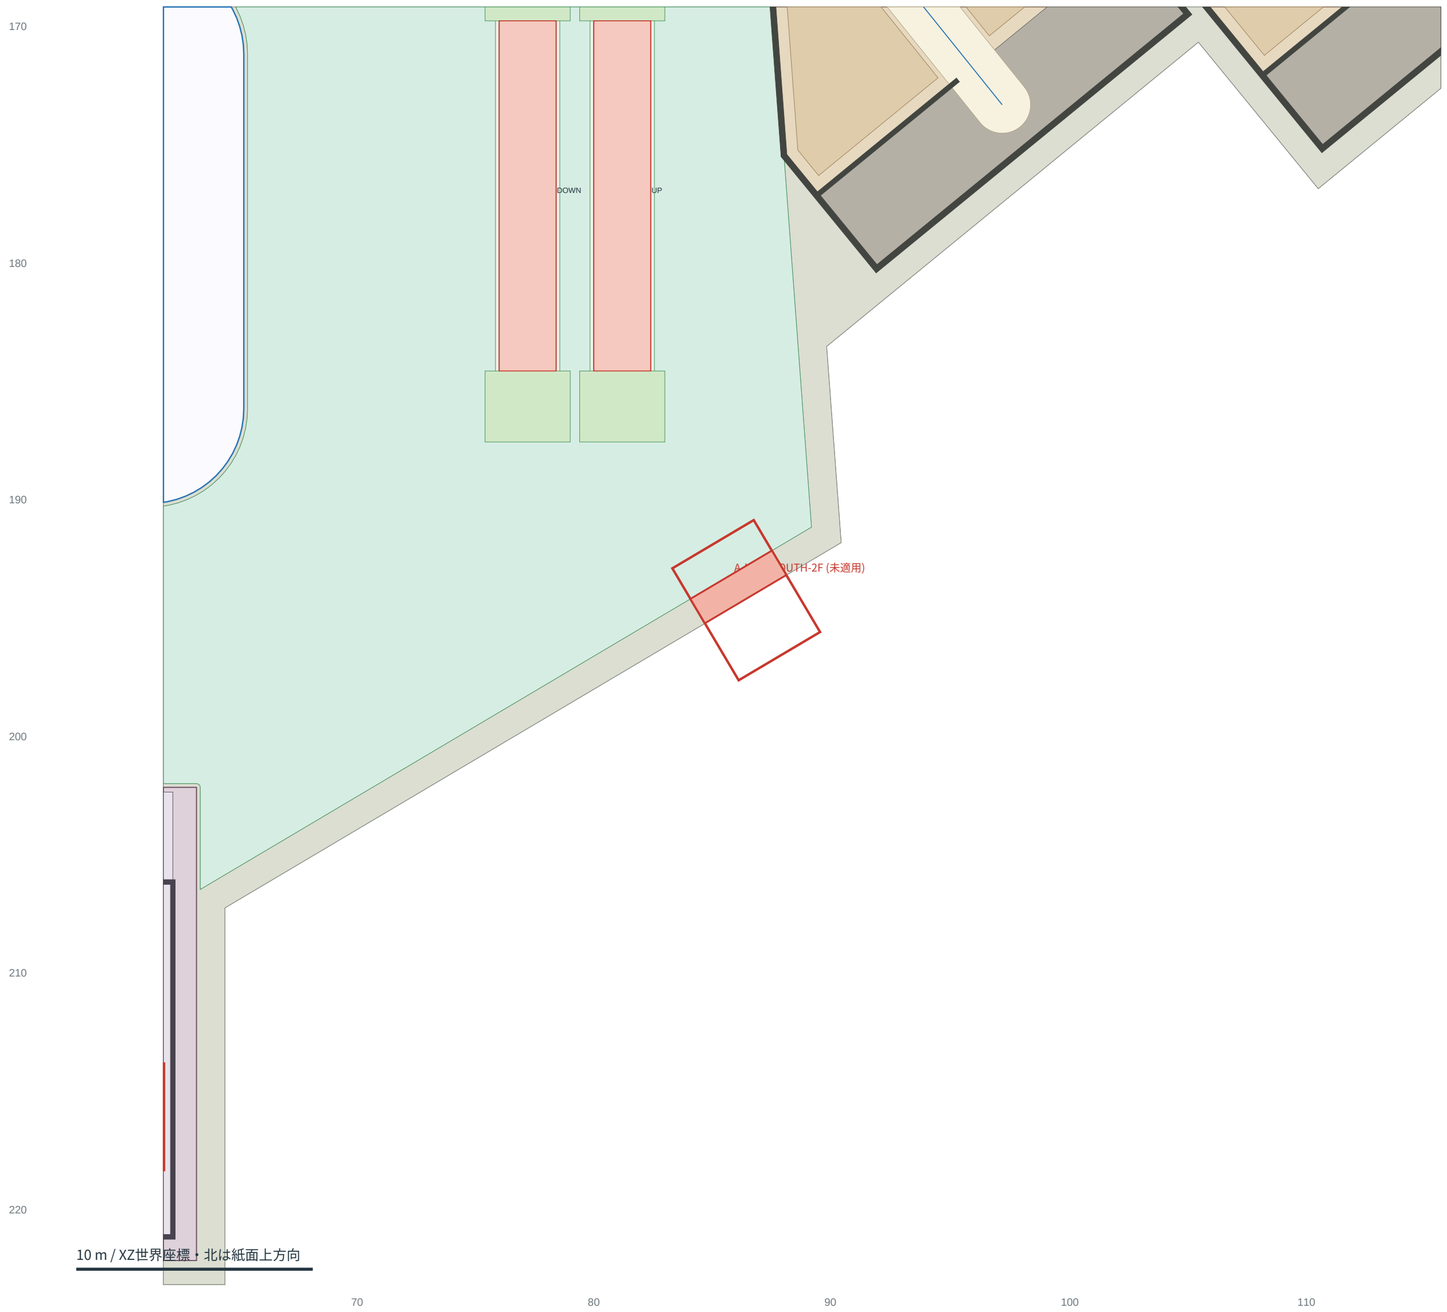

玄関幅 4.0m / Y 5.525m

既存店舗・設備核との重なり 0.000000000㎡

外壁/閉鎖帯の局所開口 4.800㎡

新玄関床支持 11.200㎡

到着橋/地上歩道はこの案の承認が前提。自動実装補正で解決した扱いにしない。

B館v4.1 1〜3Fの原本、A館v1原本、ゲーム本体はいずれも未変更。

歩道橋の昇降塔｜階段・EV・地上/橋上接続

共通寸法を5基へ適用。2m幅の折返し階段・34段・EV1m扉。地上から橋面5.525m、橋桁下5.205m。

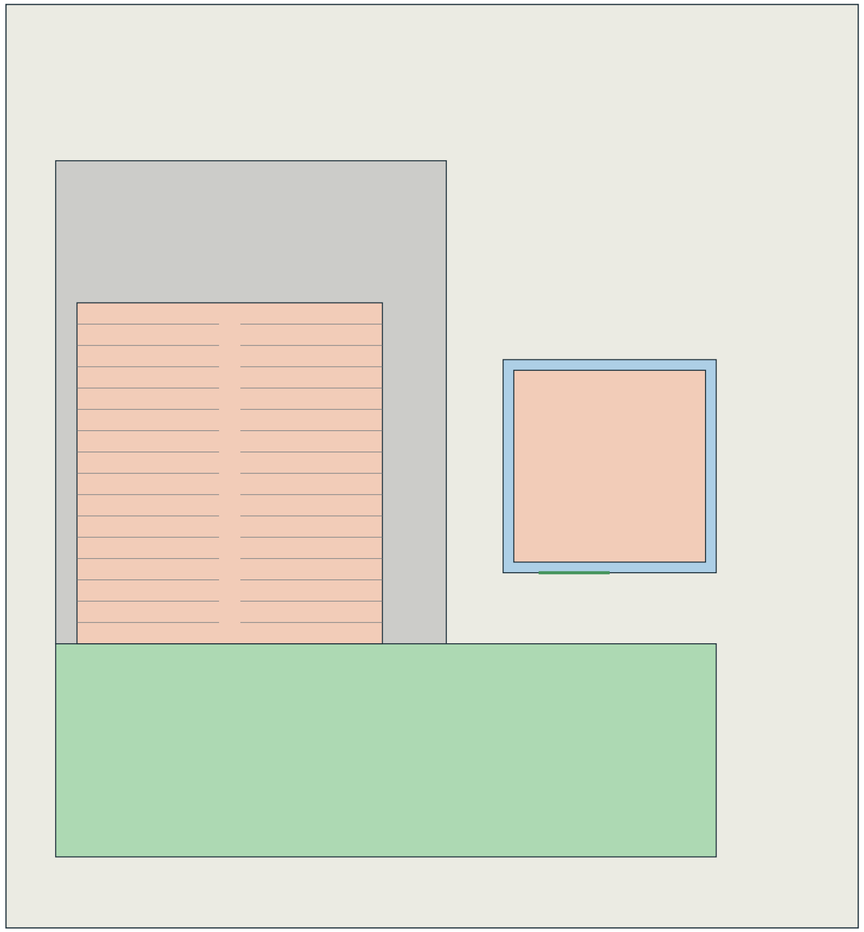

昇降塔の設置位置（X,Z）

TW-PAS = [120, 315]

TW-PCN-N = [-468, -448]

TW-PCN-S = [-468, -392]

TW-PBW-W = [-820, 100]

TW-PBW-E = [-755, 100]

各塔は地上歩道と橋上歩道の同一点へ接続。階段/EV機器・構造柱/地盤は未実装。桁・基礎の構造計算は未検証。

B館地下車路・屋上連絡橋｜平面と縦断

B館

地下スロープはP-B-S地上からB B1へ。屋上は別の水平橋でP7と接続。既存B1〜3Fを車路で貫通しません。

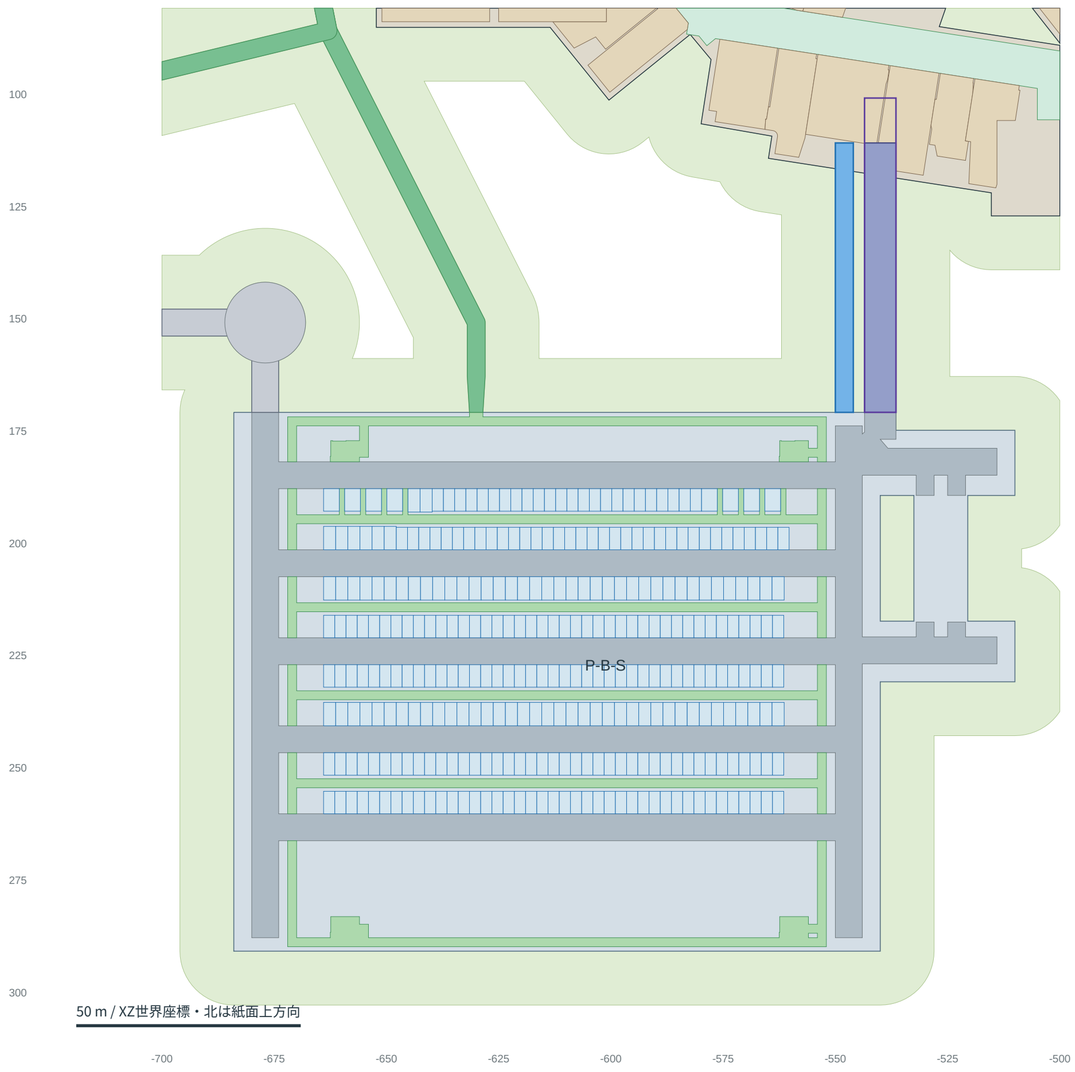

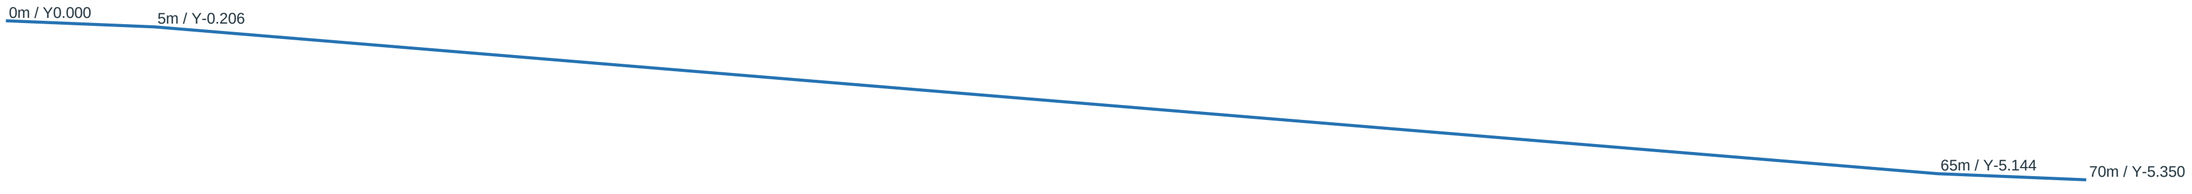

地下：幅7m、延長70m、5m緩和×2＋60m本勾配。最大約8.23%。車高2.1m制限、設計内空2.4m。

歩行者出口3mの駐車場では、敷地側を8mかけて4mへ広げる。駐車場受け口や端部柵を4mに広げた扱いにはしません。

屋上：車路幅7m、歩道幅4m、両者の離隔2.5m。Y16.4mで別支持。B側とP-B-S側の口を全幅で支持する設計。

地下車路口は(-540,170)→(-540,100)、屋上車路は(-540,170)→(-540,110)、屋上歩道はX=-548に分離。

地上搬入車路を横断する橋はY5.525m、桁厚0.32mの設計仮定で桁下5.205m。トラック4.2m＋余裕0.5mを上回る。構造成立の実証ではない。

A館 設備核｜トイレ・階段・EV 詳細 1

既存室割りを維持。赤枠はA/B既存構造床に必要な穴の別提案。Cは原設計の穴を維持。

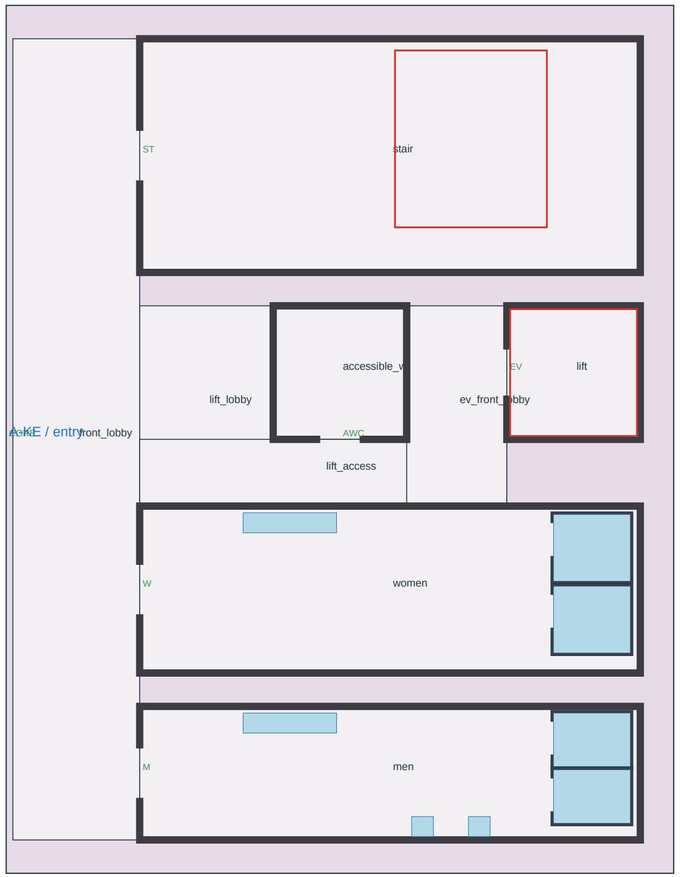

A/B別案：EV内法は室境界から0.1m壁厚を残して切欠き。階段は2本の2m有効幅、踊り場は保持。既存階の床穴を未施工のまま上下移動可能と報告しません。

B1階段底部は基礎床を保持。B1↔1F、3F↔RFの追加ESCは既存の吹き抜け周辺3対に積層。機器仕様・衝突・実歩行・法定避難は実装後に検証。

B館 設備核｜トイレ・階段・EV 詳細 1

既存室割りを維持。赤枠はA/B既存構造床に必要な穴の別提案。Cは原設計の穴を維持。

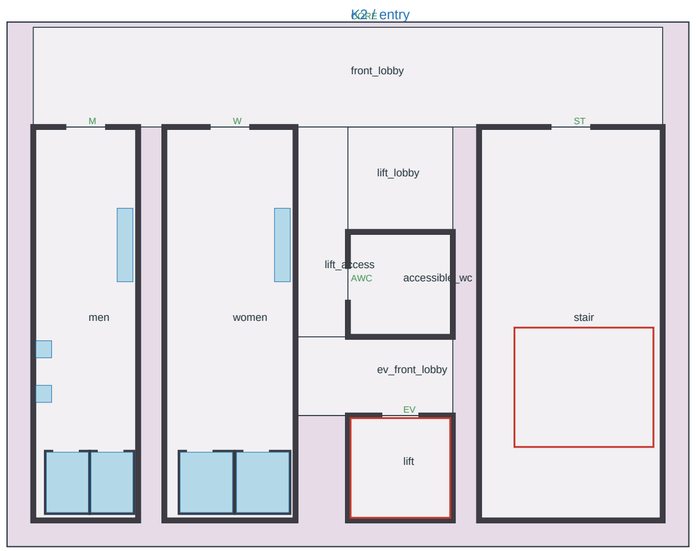

A/B別案：EV内法は室境界から0.1m壁厚を残して切欠き。階段は2本の2m有効幅、踊り場は保持。既存階の床穴を未施工のまま上下移動可能と報告しません。

B1階段底部は基礎床を保持。B1↔1F、3F↔RFの追加ESCは既存の吹き抜け周辺3対に積層。機器仕様・衝突・実歩行・法定避難は実装後に検証。

C館 設備核｜トイレ・階段・EV 詳細 1

既存室割りを維持。赤枠はA/B既存構造床に必要な穴の別提案。Cは原設計の穴を維持。

A/B別案：EV内法は室境界から0.1m壁厚を残して切欠き。階段は2本の2m有効幅、踊り場は保持。既存階の床穴を未施工のまま上下移動可能と報告しません。

B1階段底部は基礎床を保持。B1↔1F、3F↔RFの追加ESCは既存の吹き抜け周辺3対に積層。機器仕様・衝突・実歩行・法定避難は実装後に検証。

C館 設備核｜トイレ・階段・EV 詳細 2

既存室割りを維持。赤枠はA/B既存構造床に必要な穴の別提案。Cは原設計の穴を維持。

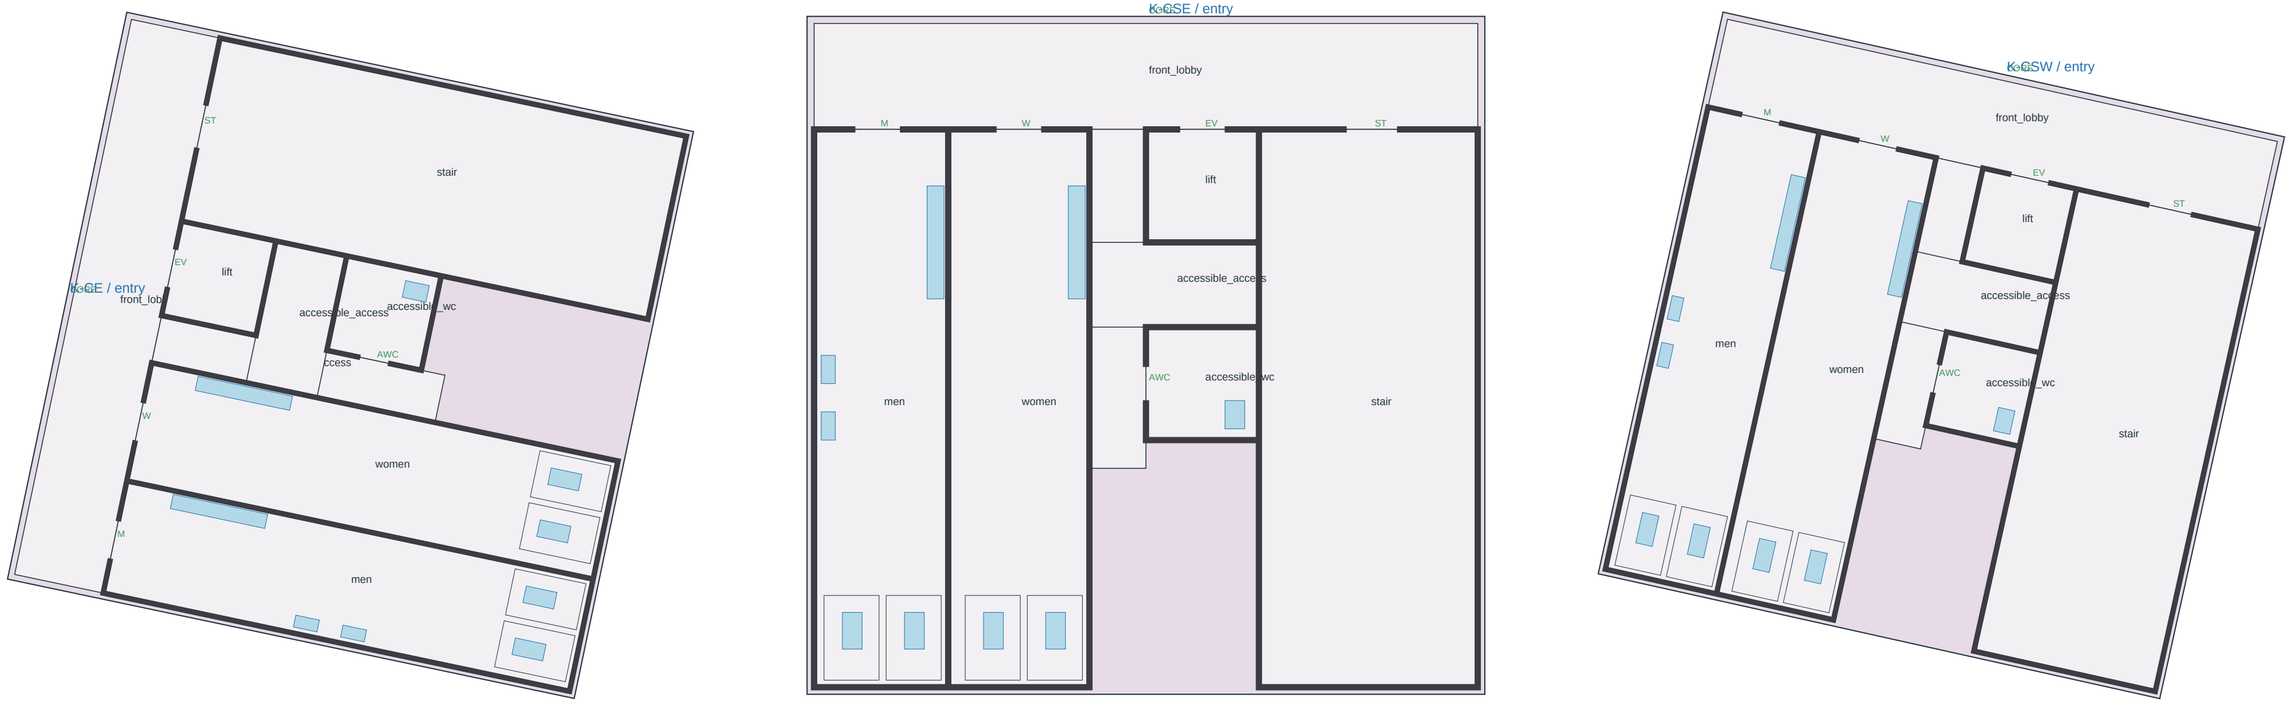

A/B別案：EV内法は室境界から0.1m壁厚を残して切欠き。階段は2本の2m有効幅、踊り場は保持。既存階の床穴を未施工のまま上下移動可能と報告しません。

B1階段底部は基礎床を保持。B1↔1F、3F↔RFの追加ESCは既存の吹き抜け周辺3対に積層。機器仕様・衝突・実歩行・法定避難は実装後に検証。

15層の接続断面｜床高さ・吹き抜け・追加ESC

各館は同じ床高。連絡橋は1F/2F既存接続を維持。B館地下/屋上は同じ核・既存ESC位置に接続。

A館

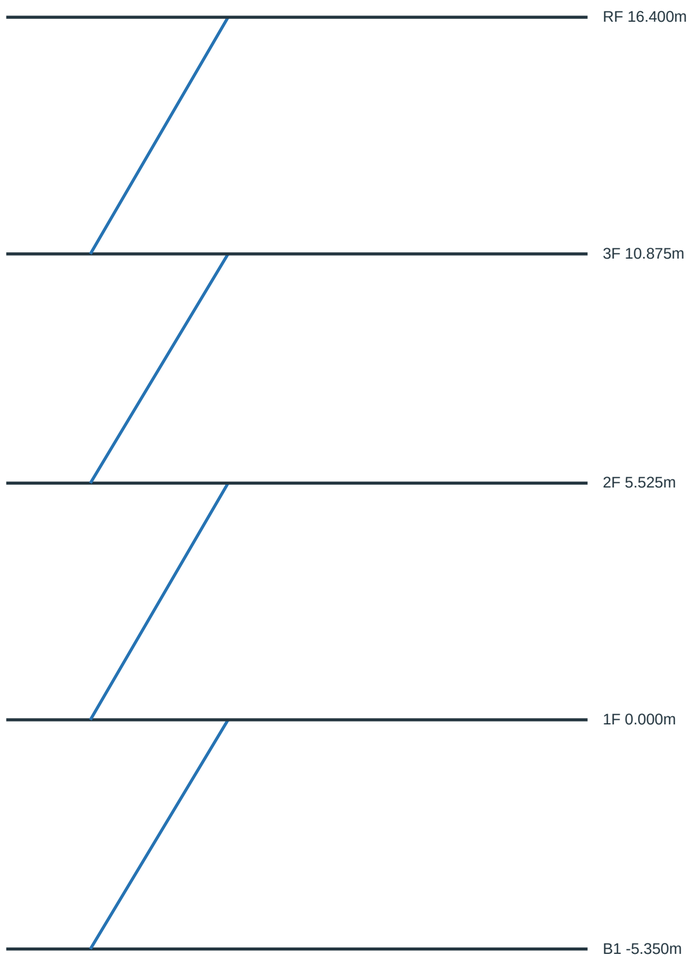

同一コア・階高維持 / 斜線は接続関係

B館

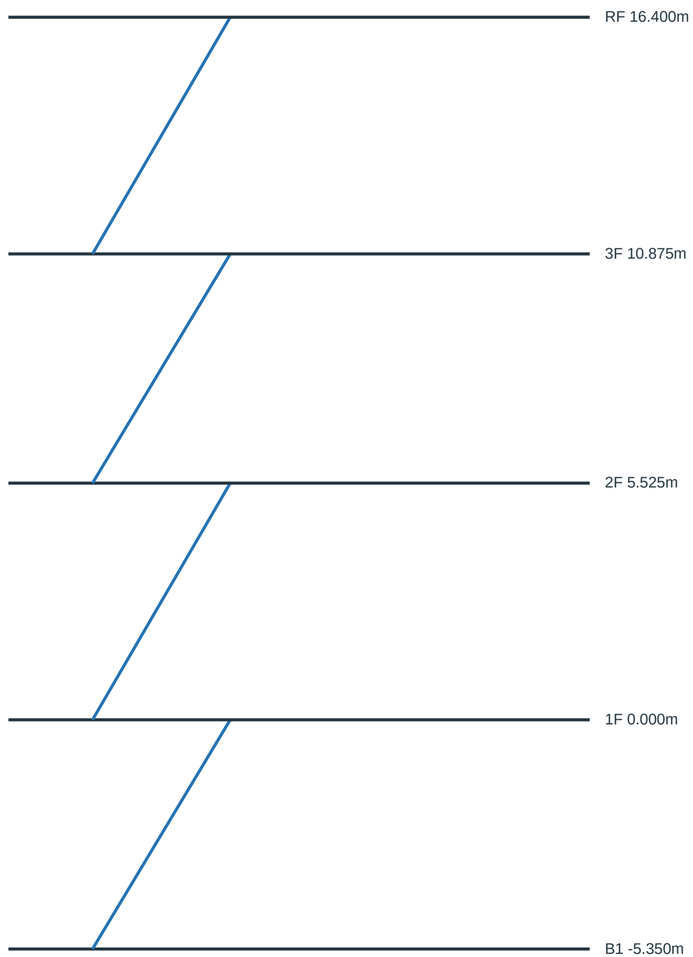

同一コア・階高維持 / 斜線は接続関係

C館

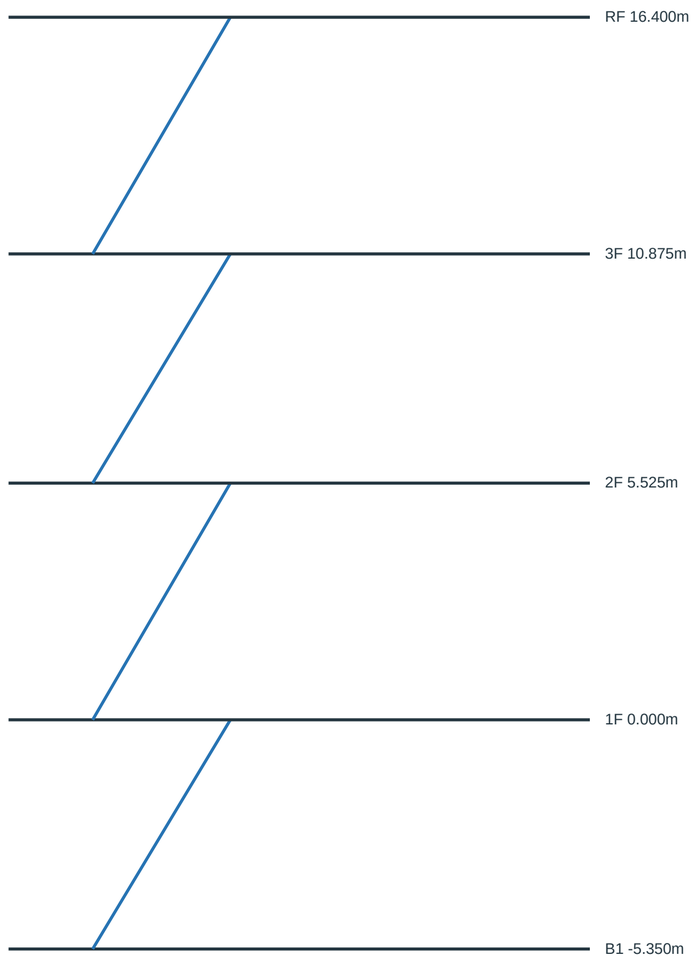

同一コア・階高維持 / 斜線は接続関係

これは接続関係の断面で、全建物の外形を直線断面として誤表示するものではありません。B新ESCは旧12/23バンクの投影を再使用し、開口と乗降床を一致。

A/BのEV・階段に関する赤い別案を承認するまで、全15層のバリアフリー連続性は「条件付き」です。ESC経由の図面上の経路と区別しています。

C館1F 面積の集計範囲｜投影・公開床・屋外を区別

同じ位置の複数名目（前廊/公開床/設備核）を足し合わせず、排他的区分で集計。

6つの独立棟の躯体投影和集合：18,953.028976㎡。屋外通路や庭園・棟間デッキはこの「6棟投影」に含めません。

1F公開床：21,418.377759㎡。うち6棟投影内6,574.336131㎡、投影外の屋外公開床14,844.041628㎡。公開床は室内だけの面積ではありません。

1F構造床板：33,046.830604㎡。店舗・設備核に加えて屋外歩行床などを含みます。6棟投影や延床面積の別名として使いません。

6棟投影内の非公開部分：12,378.692845㎡。公開6,574.336131㎡と足して投影18,953.028976㎡になります。

名目前廊4,071.114556㎡をそのまま屋内公開床に加算しません。投影外の前廊接続180.938425㎡と設備核との名目交差21.6㎡があり、前廊/設備核/屋外通路の排他的台帳へ配分済み。

面積監査：1,611件、失敗0件。監査専用1e-12mグリッド正規化の最大面積差1.74e-10㎡未満。原図は無変更。raw-source-vs-audit-precision.jsonに元精度値を保持。

C館の共用publicとwalkableの差には固定什器の占有が含まれます。通路を含む名目面積を、障害物を除いた有効歩行面積と混同しません。

C館 1F｜排他的面積台帳

区分ポリゴンはexclusive-area-zones.geojson、原図との名目重複はnominal-overlaps.json。0㎡区分も定義を残しています。

区分	用途	面積㎡	うち元public㎡
A01	階段・EV・機械開口	844.960000	0.000000
A02	専用バックルーム	1,685.406713	0.000000
A03	店舗・施設区画（裏室除く）	9,245.992091	0.000000
A04	共用設備核床（開口除く）	2,705.760000	2,705.760000
A05	6棟投影内の前廊床	3,868.576131	3,868.576131
A06	6棟投影外の前廊接続帯	180.938425	180.938425
A07	地下屋内連絡ホール	0.000000	0.000000
A08	屋内共用の残り	0.000000	0.000000
A09	地上広場・庭の歩行床	5,154.582490	5,154.582490
A10	地上屋外通路	9,508.520713	9,508.520713
A11	上階の棟間デッキ	0.000000	0.000000
A12	屋上庭園の露天歩行床	0.000000	0.000000
A13	非公開の植栽床	3,822.699354	0.000000
A14	閉鎖搬入ヤード	0.000000	0.000000
A15	管理・搬入用の専用通路	0.000000	0.000000
A16	残余躯体・境界調整帯	697.054041	0.000000

排他的監査範囲合計 37,714.489958㎡

C館 B1｜排他的面積台帳

区分ポリゴンはexclusive-area-zones.geojson、原図との名目重複はnominal-overlaps.json。0㎡区分も定義を残しています。

区分	用途	面積㎡	うち元public㎡
A01	階段・EV・機械開口	750.240000	0.000000
A02	専用バックルーム	1,685.406713	0.000000
A03	店舗・施設区画（裏室除く）	9,245.992091	0.000000
A04	共用設備核床（開口除く）	2,705.760000	2,705.760000
A05	6棟投影内の前廊床	3,868.576131	3,868.576131
A06	6棟投影外の前廊接続帯	180.938425	180.938425
A07	地下屋内連絡ホール	13,301.811616	13,301.811616
A08	屋内共用の残り	0.000000	0.000000
A09	地上広場・庭の歩行床	0.000000	0.000000
A10	地上屋外通路	0.000000	0.000000
A11	上階の棟間デッキ	0.000000	0.000000
A12	屋上庭園の露天歩行床	0.000000	0.000000
A13	非公開の植栽床	0.000000	0.000000
A14	閉鎖搬入ヤード	1,470.000000	0.000000
A15	管理・搬入用の専用通路	249.123978	0.000000
A16	残余躯体・境界調整帯	1,752.626274	0.000000

排他的監査範囲合計 35,210.475227㎡

C館 2F｜排他的面積台帳

区分ポリゴンはexclusive-area-zones.geojson、原図との名目重複はnominal-overlaps.json。0㎡区分も定義を残しています。

区分	用途	面積㎡	うち元public㎡
A01	階段・EV・機械開口	939.680000	0.000000
A02	専用バックルーム	1,685.406713	0.000000
A03	店舗・施設区画（裏室除く）	9,245.992091	0.000000
A04	共用設備核床（開口除く）	2,705.760000	2,705.760000
A05	6棟投影内の前廊床	3,868.576131	3,868.576131
A06	6棟投影外の前廊接続帯	180.938425	180.938425
A07	地下屋内連絡ホール	0.000000	0.000000
A08	屋内共用の残り	0.000000	0.000000
A09	地上広場・庭の歩行床	0.000000	0.000000
A10	地上屋外通路	0.000000	0.000000
A11	上階の棟間デッキ	5,265.279831	5,265.279831
A12	屋上庭園の露天歩行床	0.000000	0.000000
A13	非公開の植栽床	0.000000	0.000000
A14	閉鎖搬入ヤード	0.000000	0.000000
A15	管理・搬入用の専用通路	0.000000	0.000000
A16	残余躯体・境界調整帯	697.054041	0.000000

排他的監査範囲合計 24,588.687232㎡

C館 3F｜排他的面積台帳

区分ポリゴンはexclusive-area-zones.geojson、原図との名目重複はnominal-overlaps.json。0㎡区分も定義を残しています。

区分	用途	面積㎡	うち元public㎡
A01	階段・EV・機械開口	844.960000	0.000000
A02	専用バックルーム	1,685.406713	0.000000
A03	店舗・施設区画（裏室除く）	9,245.992091	0.000000
A04	共用設備核床（開口除く）	2,705.760000	2,705.760000
A05	6棟投影内の前廊床	3,868.576131	3,868.576131
A06	6棟投影外の前廊接続帯	180.938425	180.938425
A07	地下屋内連絡ホール	0.000000	0.000000
A08	屋内共用の残り	0.000000	0.000000
A09	地上広場・庭の歩行床	0.000000	0.000000
A10	地上屋外通路	0.000000	0.000000
A11	上階の棟間デッキ	4,407.537015	4,407.537015
A12	屋上庭園の露天歩行床	0.000000	0.000000
A13	非公開の植栽床	0.000000	0.000000
A14	閉鎖搬入ヤード	0.000000	0.000000
A15	管理・搬入用の専用通路	0.000000	0.000000
A16	残余躯体・境界調整帯	697.054041	0.000000

排他的監査範囲合計 23,636.224416㎡

C館 RF｜排他的面積台帳

区分ポリゴンはexclusive-area-zones.geojson、原図との名目重複はnominal-overlaps.json。0㎡区分も定義を残しています。

区分	用途	面積㎡	うち元public㎡
A01	階段・EV・機械開口	750.240000	0.000000
A02	専用バックルーム	486.396747	0.000000
A03	店舗・施設区画（裏室除く）	1,051.723108	0.000000
A04	共用設備核床（開口除く）	2,705.760000	2,705.760000
A05	6棟投影内の前廊床	3,868.576131	3,868.576131
A06	6棟投影外の前廊接続帯	180.938425	180.938425
A07	地下屋内連絡ホール	0.000000	0.000000
A08	屋内共用の残り	0.000000	0.000000
A09	地上広場・庭の歩行床	0.000000	0.000000
A10	地上屋外通路	0.000000	0.000000
A11	上階の棟間デッキ	4,278.497828	4,278.497828
A12	屋上庭園の露天歩行床	5,890.138366	5,890.138366
A13	非公開の植栽床	3,914.676200	0.000000
A14	閉鎖搬入ヤード	0.000000	0.000000
A15	管理・搬入用の専用通路	0.000000	0.000000
A16	残余躯体・境界調整帯	285.518425	0.000000

排他的監査範囲合計 23,412.465229㎡

C館1F｜排他的用途ポリゴン図

公開床が6棟躯体投影を越える理由を可視化。前廊/屋外/庭園/設備核を排他的に区分。

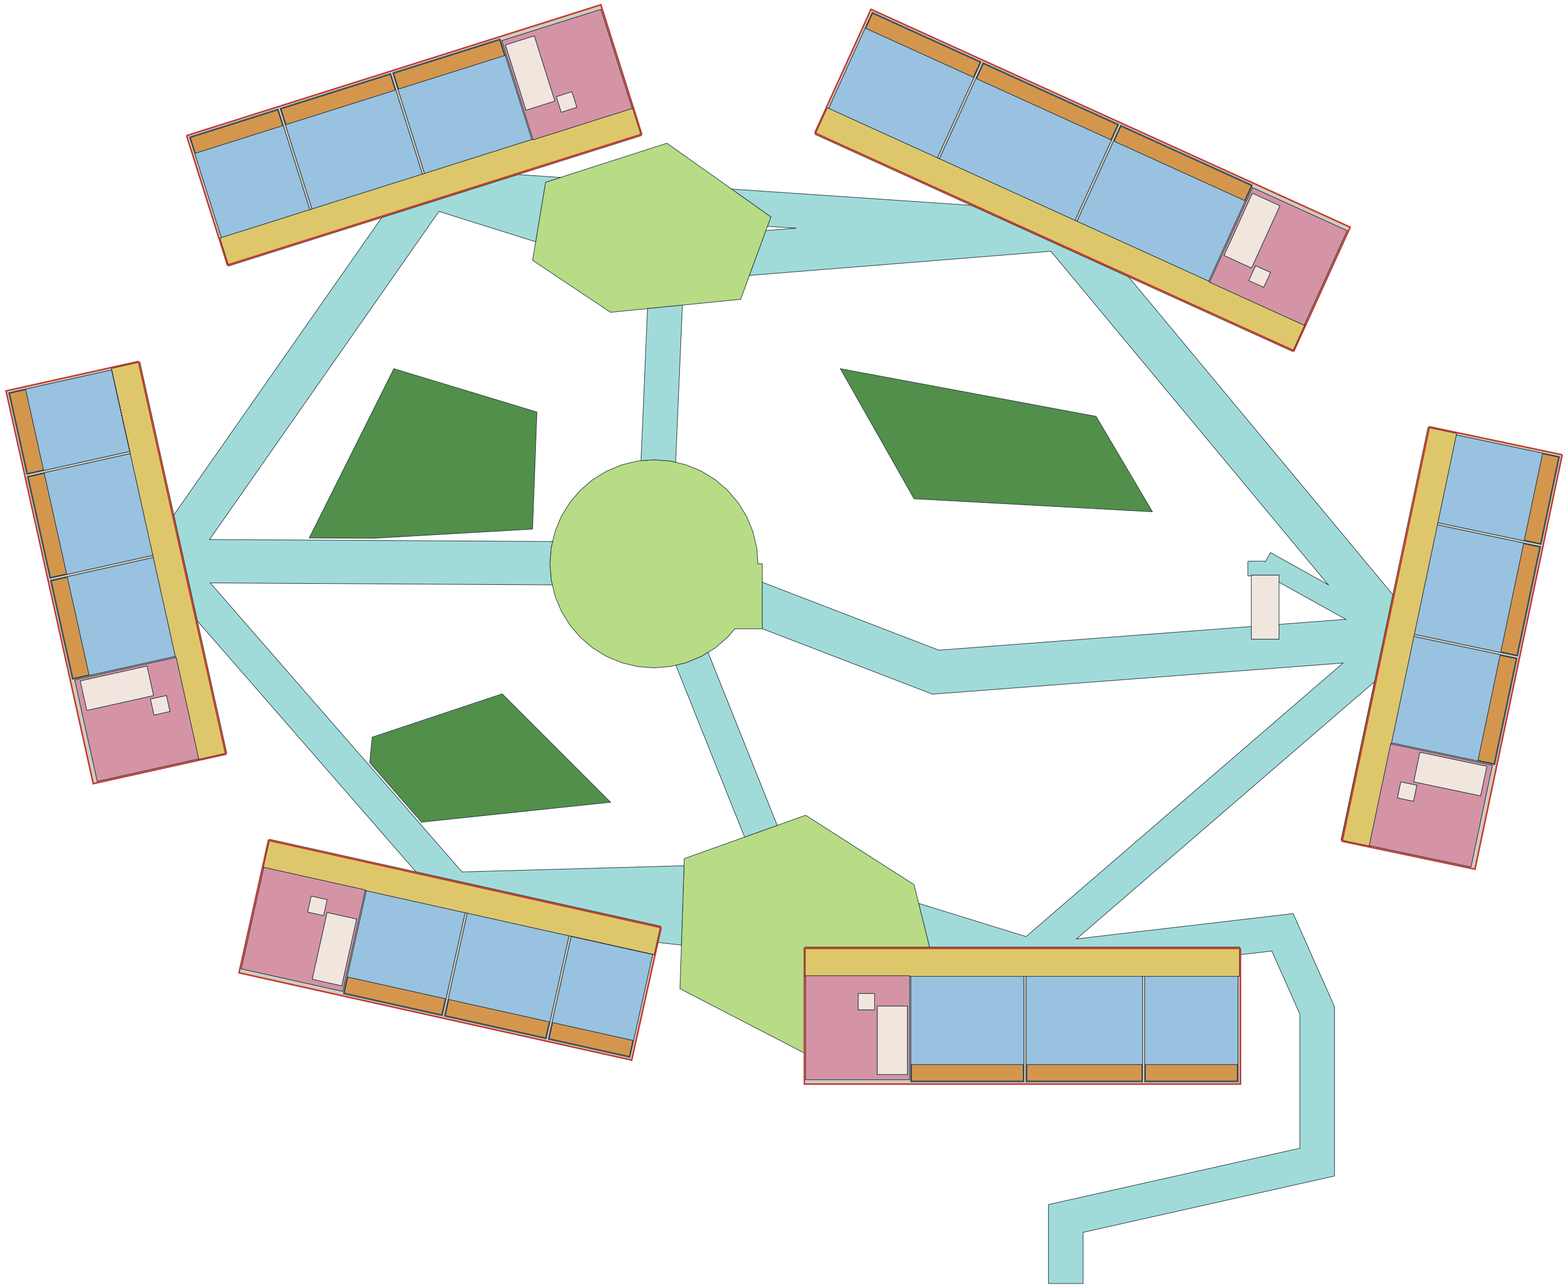

A01 階段・EV・機械開口
844.960000 ㎡

A02 専用バックルーム
1,685.406713 ㎡

A03 店舗・施設区画（裏室除く）
9,245.992091 ㎡

A04 共用設備核床（開口除く）
2,705.760000 ㎡

A05 6棟投影内の前廊床
3,868.576131 ㎡

A06 6棟投影外の前廊接続帯
180.938425 ㎡

A09 地上広場・庭の歩行床
5,154.582490 ㎡

A10 地上屋外通路
9,508.520713 ㎡

A13 非公開の植栽床
3,822.699354 ㎡

A16 残余躯体・境界調整帯
697.054041 ㎡

赤線＝6棟躯体投影

B館追加ESC｜上下階開口・乗降・積層断面

既存12/23バンクを下/上へ積層。平面投影・乗降口・3m平場を保持し、既存1〜3Fの開口を拡張しません。

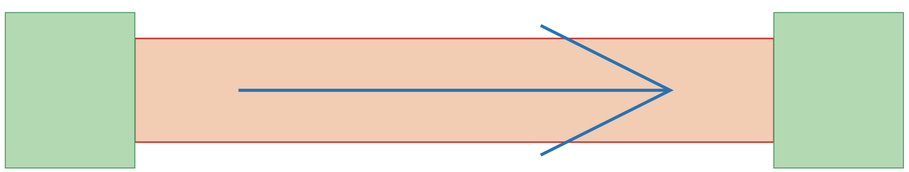

斜路本体の投影11.8m＋くし板平場1.5m×2、幅2.4m。乗降床は3m×3.6m。隣接上下行の中央機器帯は歩行床に含めません。

B1→1F：高低差5.350m。3F→RF：高低差5.525m。同じ投影でも勾配角は約24.4/25.1度。

上下の投影が重なる機器は、階高5.35m以上から機器厚0.4mを引いて4.95m以上を確保する設計仮定。機器ベンダーの実仕様・頭上判定は未確認。

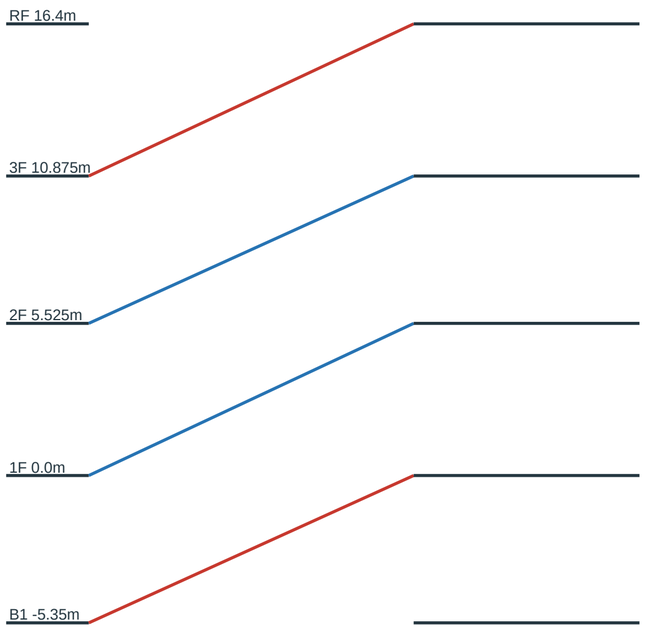

赤＝今回追加する地下/屋上接続、青＝既存層間。断面はUPバンクの投影、DOWNは隣の別レーン。

C館地下搬入ヤード｜新しい屋外トラック下降路

既存C搬入ヤードはB1 -5.35m。敷地側の新スロープだけで接続し、既存C1Fの床や店舗を変更しません。

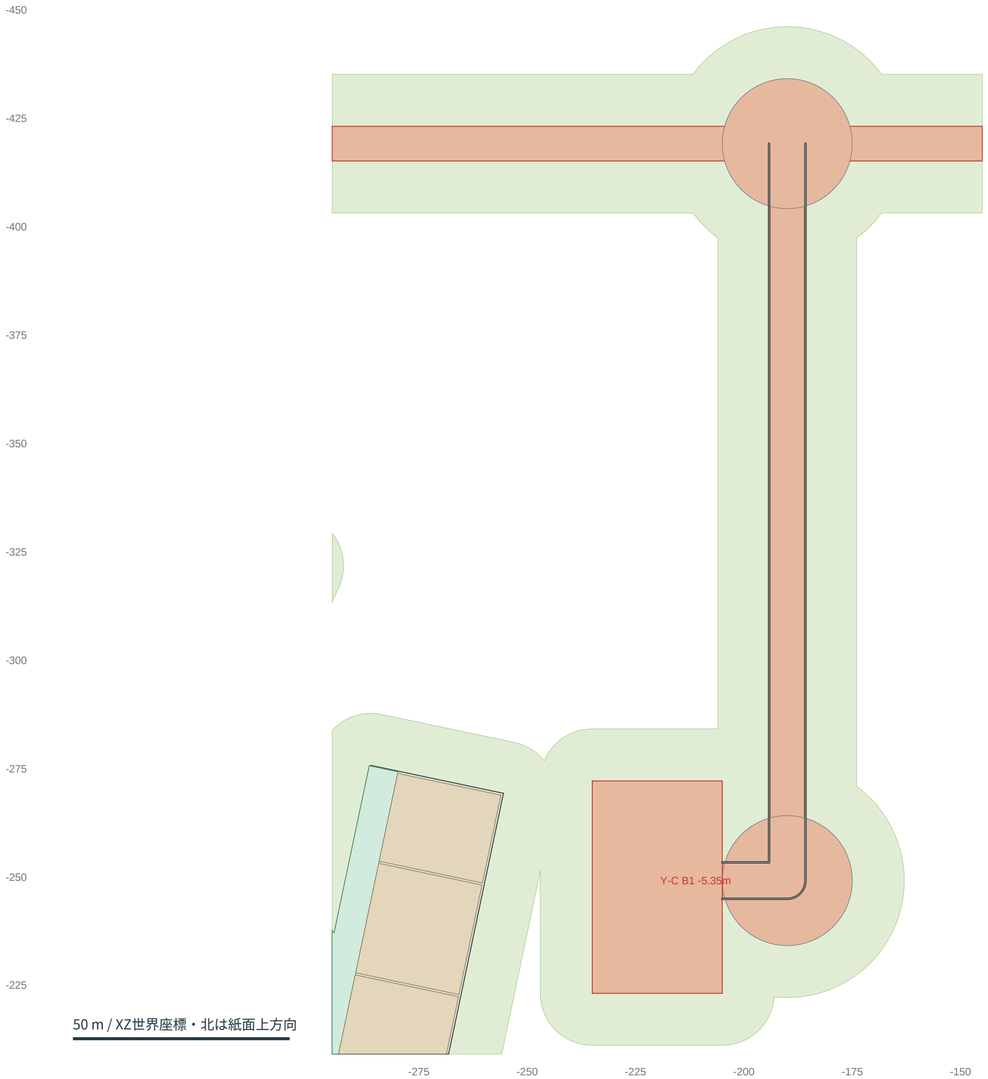

搬入専用幹線(-190,-420,Y0)→直線下降150m→地下水平20m→ヤード入口(-205,-250,Y-5.35)。最後の15mは水平で西へ折れる。

幅8m、上下緩和10mずつ、最大勾配約3.82%。地下の曲がり角は半径15mの旋回予約。12m級単車トラックの動的軌跡は未検証。

地下ヤードは30×49m、既存面積1,470㎡。Cの旧truck_gate/地下床/台車用ゲートに高さを一致。ピットとスロープは露天で、地上駐車場として加算しない。

1Fの6棟投影18,953.028976㎡、公開床21,418.377759㎡のいずれにも、この地下ヤードを新しく足しません。

保護歩道橋はこの下降路ではなく、北側の地上搬入幹線を跨ぐ。地上歩行者を下降路へ誘導しない。擁壁・排水ポンプ・雨水貯留・構造は未設計。

A西既存22台｜車路・後方歩道の局所補完

既存22マスは位置/寸法/IDを保持。車路前の2m離隔を進入エプロンで、後方を保護歩道でつなぐ敷地側案。

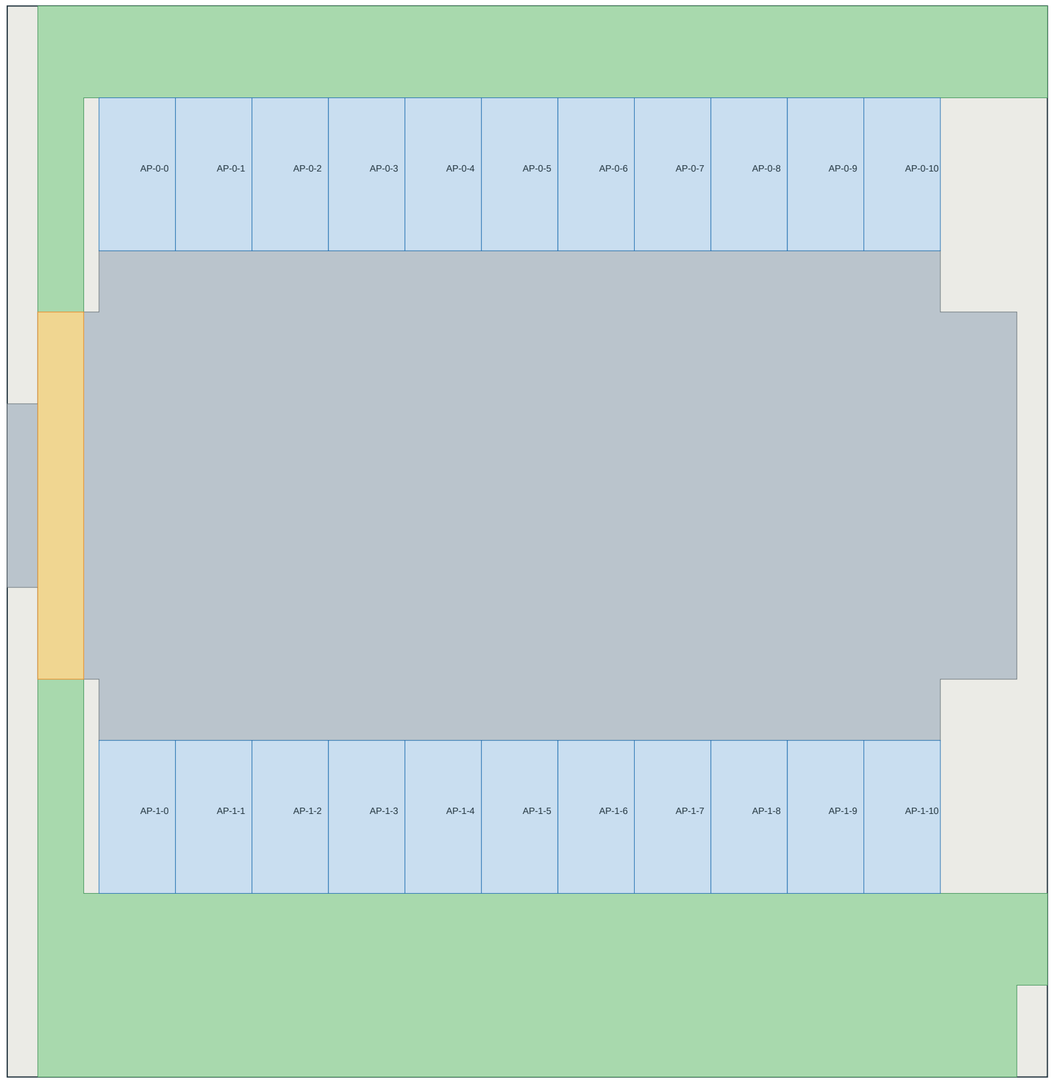

元のマス22台は無変更。一般枠として計上。

入口車路は西側(-174,-39)から幅6mでエプロンへ。後方歩道は車路を横断する指定1か所へ集約。

歩行到着点(-153,-20)からA西既存公開部へ接続。身障者用/EV/ゆとり枠は大規模駐車場で別途確保。

A館搬入口｜東核店バックルームへ直接接続する局所案

貨物車路は客用車路と分離。既存バックルームの外壁に2m搬入扉を提案し、売場をトラックで通過させません。

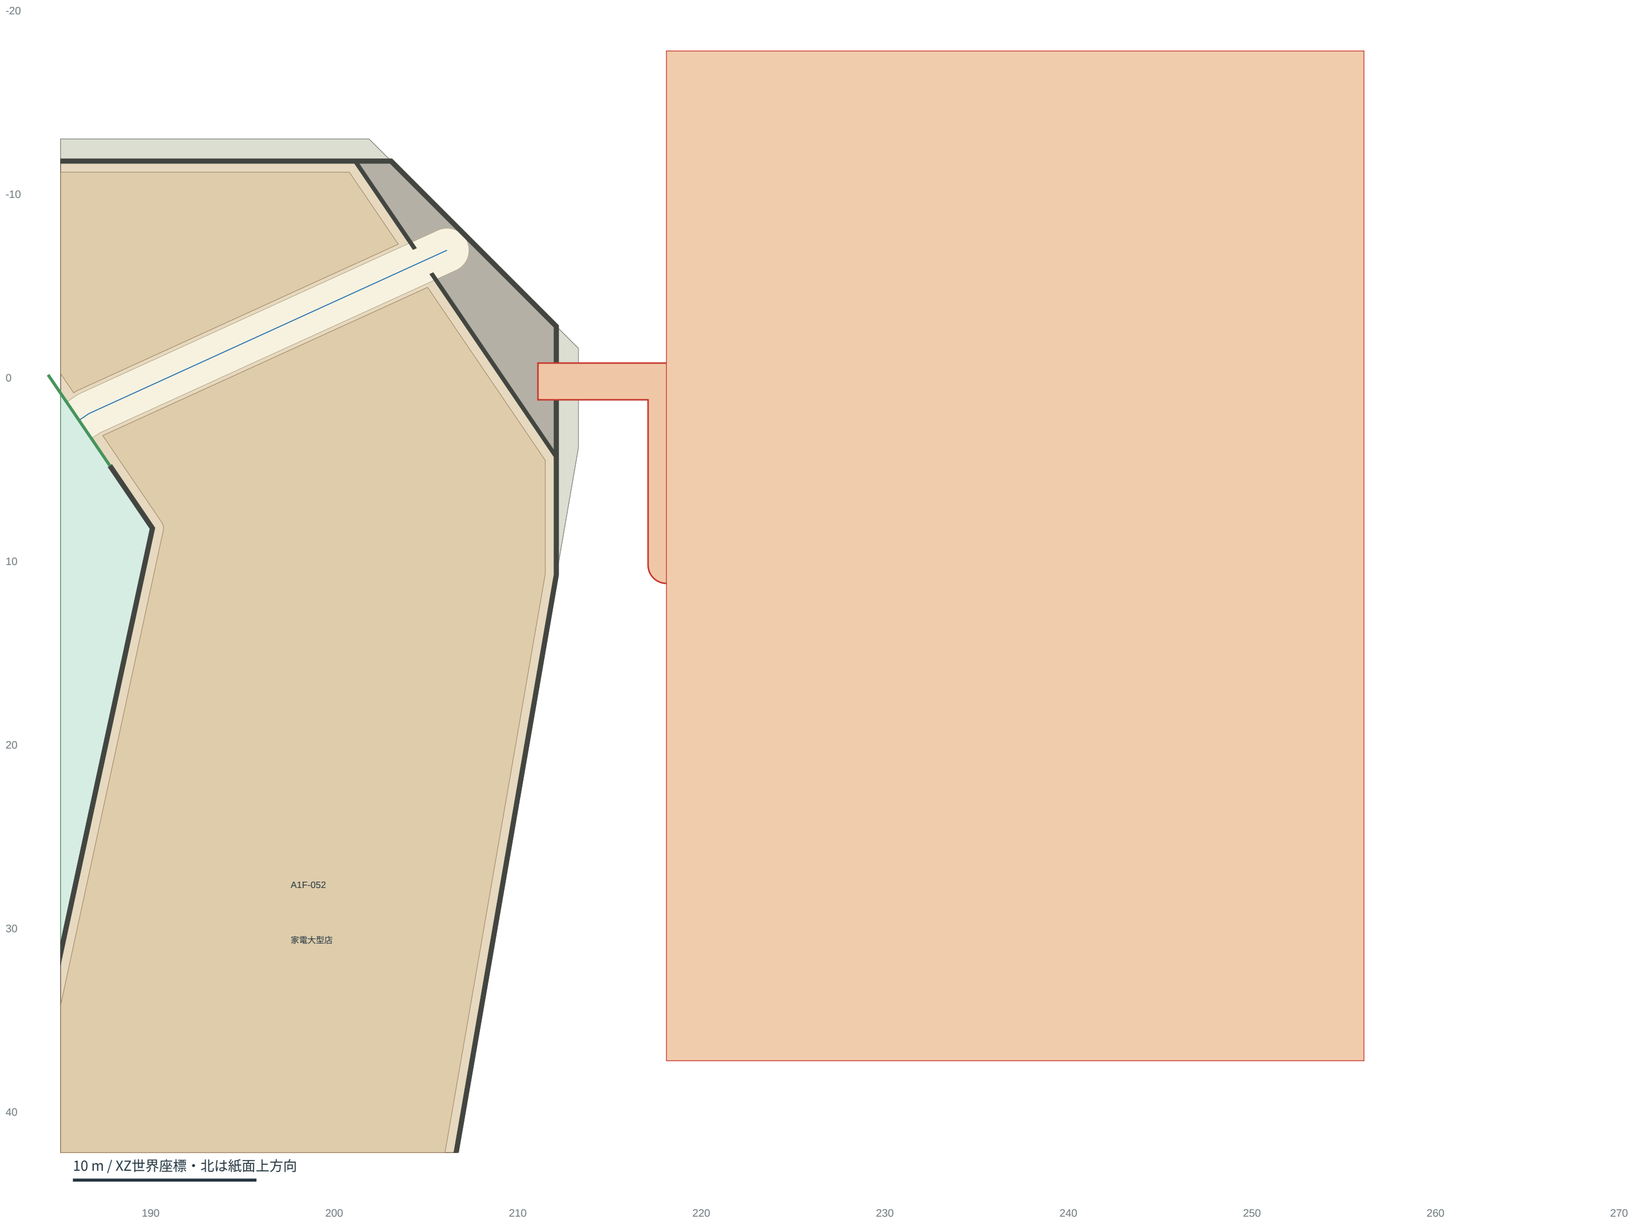

未適用の新搬入扉：A1F-052バックルーム外壁、幅2m。原店舗区画や内部主路は維持。

荷捌きヤード38×55m、接続貨物車路8m。トラックはヤードで停止し、先は台車のみ。

荷物は閉館後の共用路と兼用EVで各店へ輸送する想定。来客通路を営業中に常時配送台車が縦走する計画ではありません。

A/B兼用EVは既存床開口案の承認が前提。動力・積載・EV実仕様/作業運用は未検証。

固定B館v4.1｜今回の独立再検査で残った65項目

B館1〜3Fは原本を保持。原本の失敗を、局所修正案の合格で上書きしていません。

全15層の独立検査 3,701件：原本合格3,636件／不合格65件。すべて固定B館1〜3Fに限定。新B地下/屋上、A/C原図には今回の検査条件で不合格なし。

内訳：店舗間微小重複56件、共用床と店舗の微小重複3件、入口中心と公開床の距離が1cmを超えるもの6件（最大約1.9cm）。全失敗のID/面積/距離はindependent-checks.json。

別案：共用床を優先して店舗境界の微小重複だけ切り欠き、入口前の短い床の切れを局所充填。既存店舗数・通路網・広場・建物外形は不変更。

別案の入口中心は元位置から0.7mm未満の数値調整に限定。原本へ一切適用せずB-v4.1-local-cleanup-UNAPPLIED.jsonへ保存。別案再検査9集約項目は全合格。

これは原本65項目を解消済みにした報告ではありません。既存Bの変更禁止を守ったまま、承認判断できる比較資料を提出するものです。

A/Bの設備核床穴24件と新来客口3件・A搬入扉1件も未適用の承認対象です。実歩行/ゲーム動作は全て未検証です。

固定B館 1F｜微小境界修正の比較案

未適用。通常の見た目が変わらない範囲を拡大し、青/赤で数値境界の差分を示します。

原本（保持）

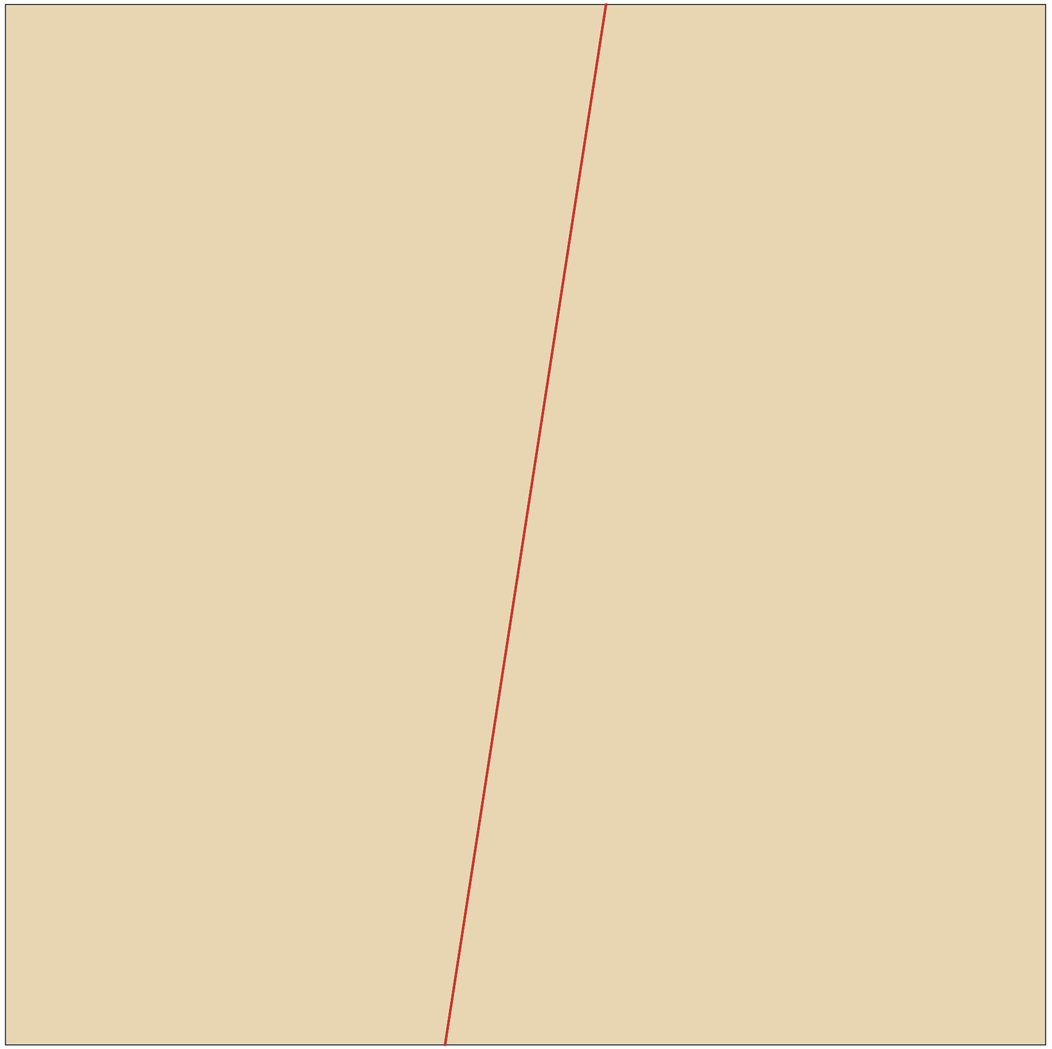

局所案（未適用）

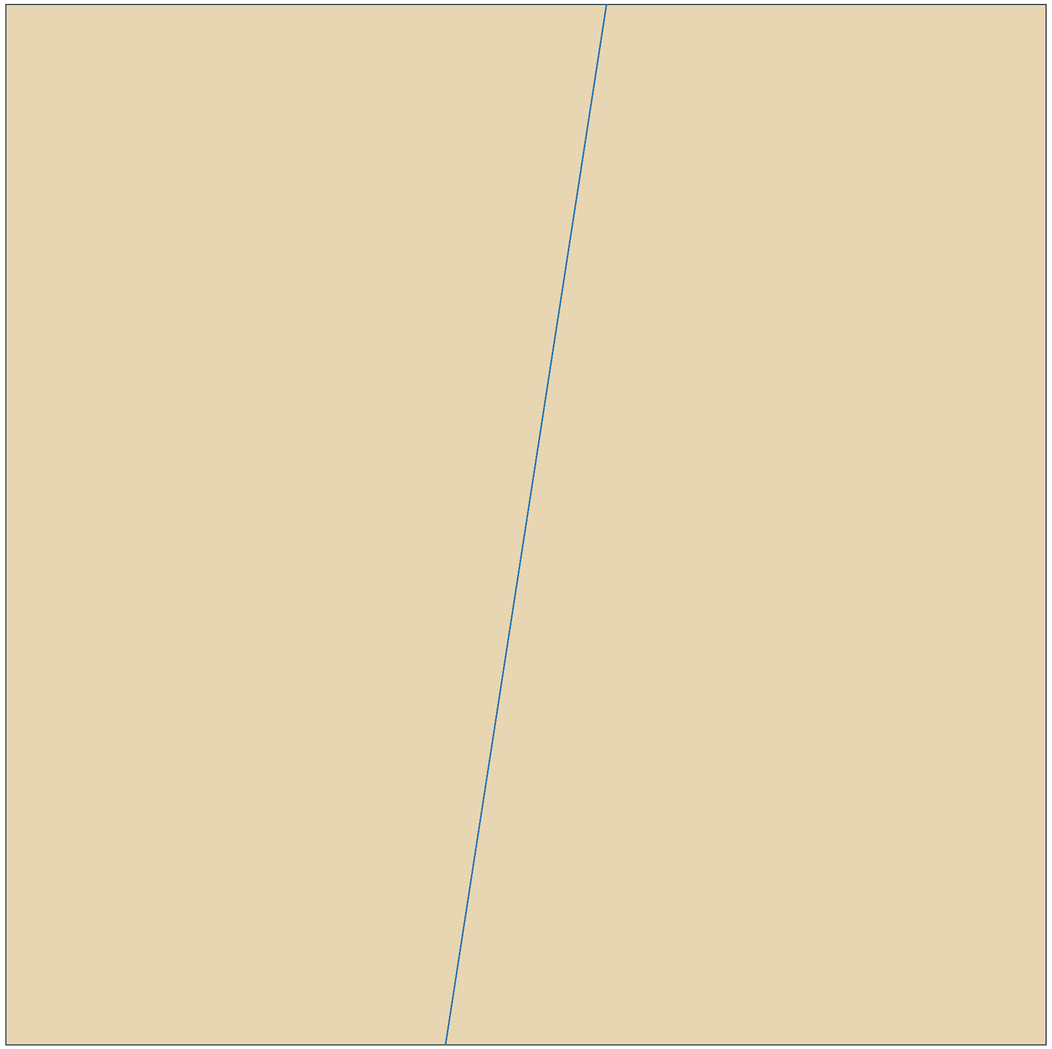

例：B1-021 / B1-034 の原本重複 0.003643720㎡。赤い細線は数値重複で、面積を拡大誇張した店舗区画ではありません。

この階の原本共用/店舗重複 0.042652630㎡、局所案の入口前床充填 0.139645511㎡、店舗境界除去合計 0.094055045㎡。

店舗区画内の細部は、この局所案が承認された後に境界へ再クリップして再出図する対象です。B館v4.1原本とゲームは今回変更していません。

固定B館 2F｜微小境界修正の比較案

未適用。通常の見た目が変わらない範囲を拡大し、青/赤で数値境界の差分を示します。

原本（保持）

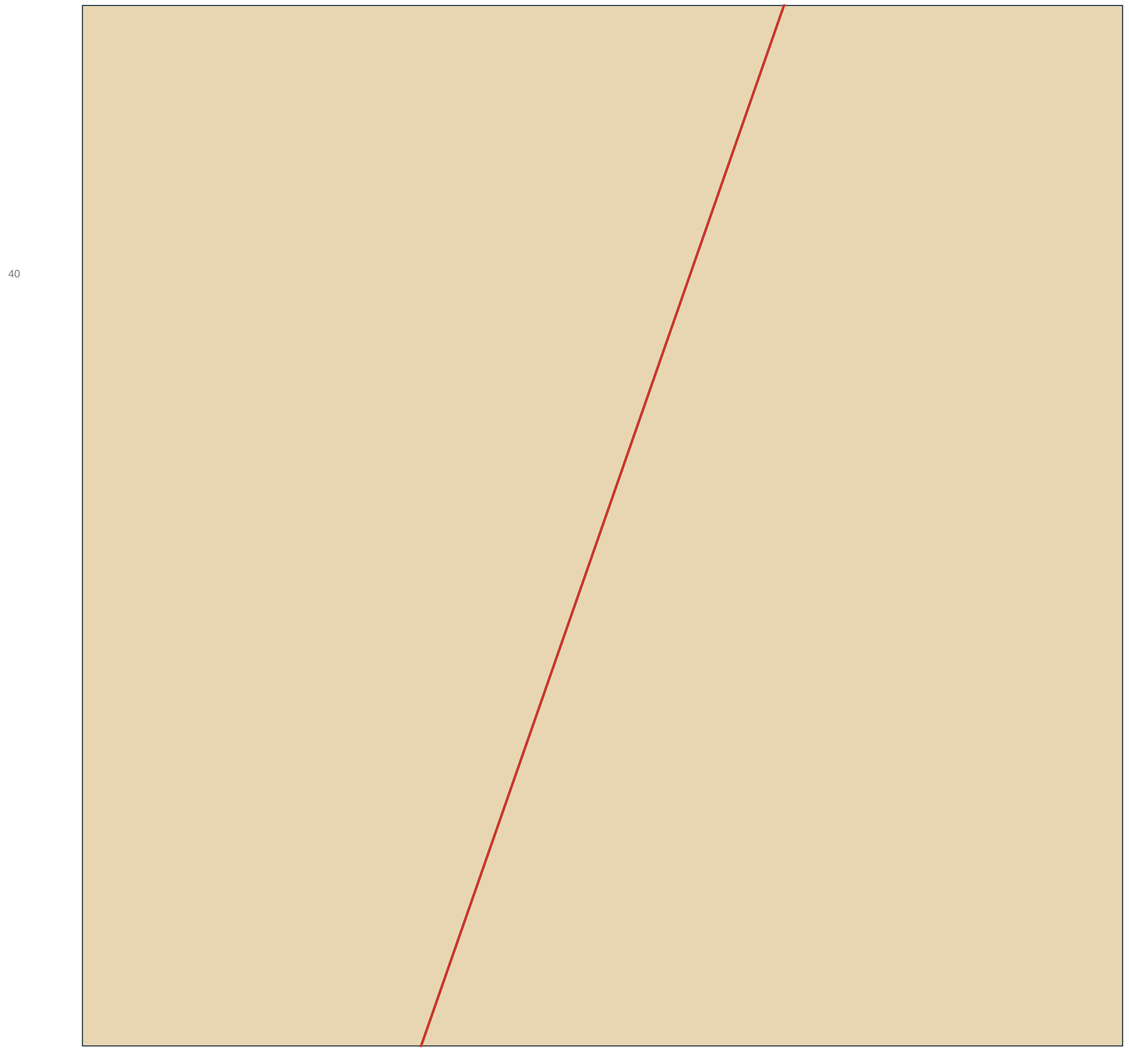

局所案（未適用）

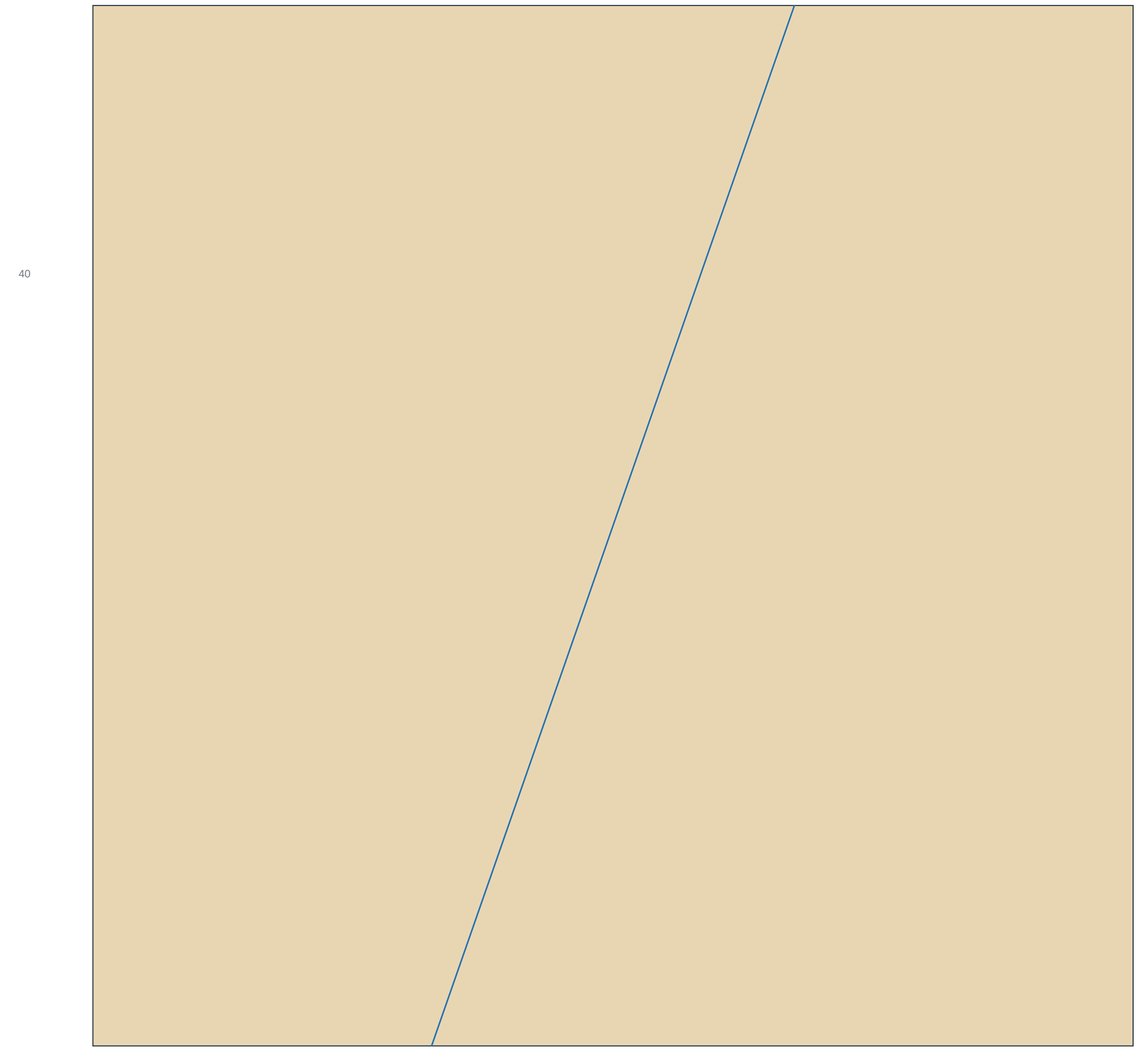

例：B2-016 / B2-030 の原本重複 0.004070684㎡。赤い細線は数値重複で、面積を拡大誇張した店舗区画ではありません。

この階の原本共用/店舗重複 0.046392481㎡、局所案の入口前床充填 0.121547153㎡、店舗境界除去合計 0.098458946㎡。

店舗区画内の細部は、この局所案が承認された後に境界へ再クリップして再出図する対象です。B館v4.1原本とゲームは今回変更していません。

固定B館 3F｜微小境界修正の比較案

未適用。通常の見た目が変わらない範囲を拡大し、青/赤で数値境界の差分を示します。

原本（保持）

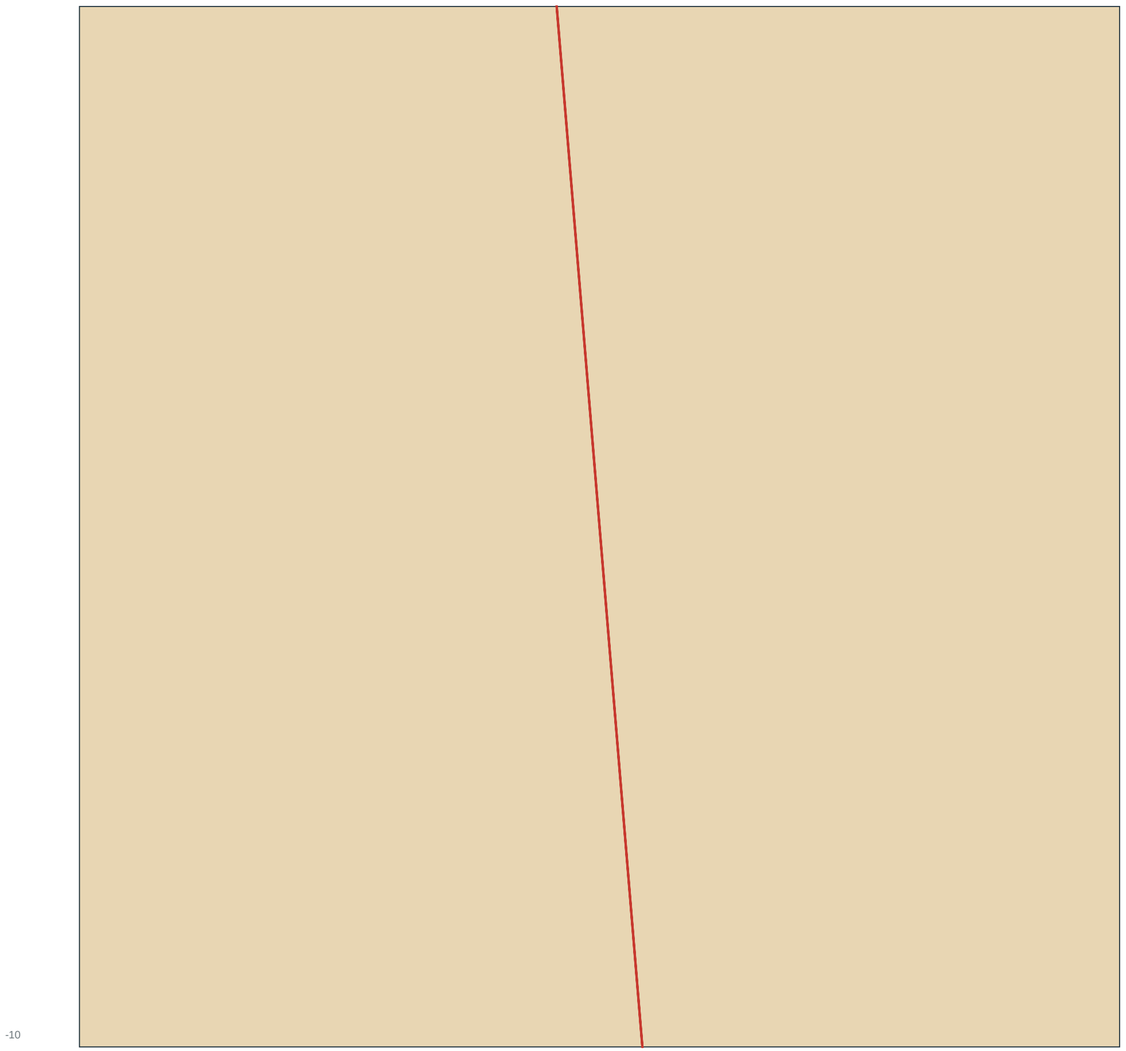

局所案（未適用）

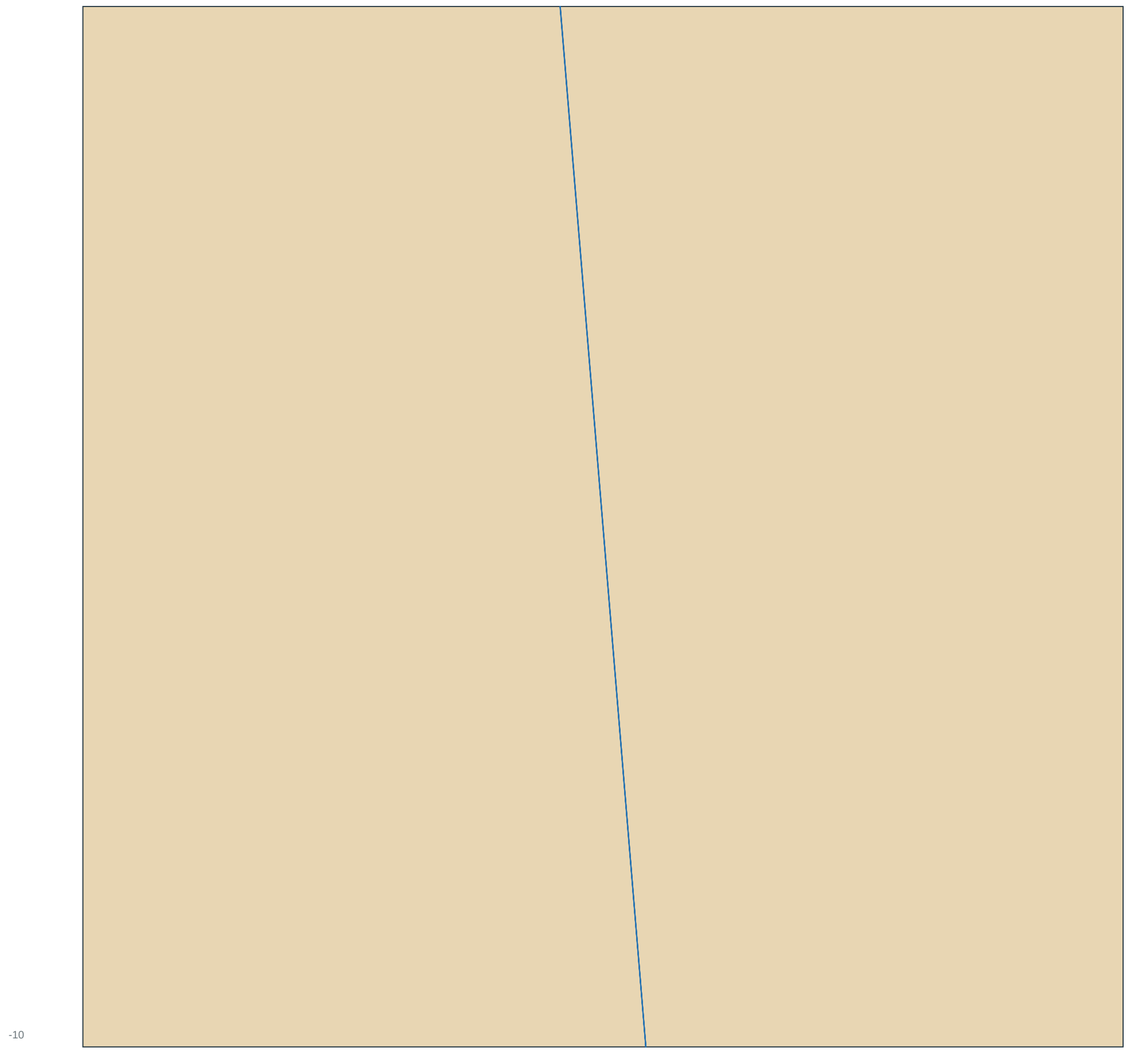

例：B3-047 / B3-055 の原本重複 0.003256026㎡。赤い細線は数値重複で、面積を拡大誇張した店舗区画ではありません。

この階の原本共用/店舗重複 0.043148223㎡、局所案の入口前床充填 0.138962234㎡、店舗境界除去合計 0.089720506㎡。

店舗区画内の細部は、この局所案が承認された後に境界へ再クリップして再出図する対象です。B館v4.1原本とゲームは今回変更していません。

検査結果と承認条件｜設計検査と実動作を分離

図面上の合格は実装済み・実歩行済みを意味しません。設計データ、全検査行、原本SHAをZIPに収録。

外部駐車：6,369台、17面。source44,815件＋独立43,445件の検査は全合格（端段防護、全マスID、台数、支持床、車路/歩道、PDF記載）。

B館B1/RF：新規入力の検査 1091件、失敗 0件。機械的な連結と床開口の検査であり、交通流や快適さの合格判定ではありません。

敷地統合：78件、失敗 0件。原本418ファイルのSHA一致、歩行者の搬入車路地上交差0、駐車入口から敷地外ゲートへ到達。

C面積監査：1611件全合格。独立棟・屋外・庭・デッキ・開口を排他的に計上。全15層の既存店舗入口経路と原図形状の無変更を統合再検査。

全15層独立再検査：3701件中65件は固定B館に残存。局所案の9集約再検査は全合格。原本の不合格と区別。

残る承認条件：新玄関3か所・A搬入扉・A/B既存階の床開口・固定Bの微小境界局所案。自動補正やゲーム改変は行っていません。既存バリアフリー移動を完成扱いしません。

B地下/屋上の車路は幅・前面接続・連結を検査。6m最小回転は設計目標で、全枠の切返し/動的車体軌跡は未検証。台数は図面の区画実数であり実車保証値ではありません。

未検証：実歩行・衝突・NPC1000/5000人・宝箱/案内図/セーブ/FT・階段/EV/ESCの動作・駐車/荷捌き交通容量・構造/防災/避難/排水/建築法規。

屋上設備と地下共同倉庫は保守通路と作業ベイを図示した用途割付です。設備機器の製作図、配管・配線・ラック品番、柱梁/耐荷重、倉庫運営計画は設計していません。

全館外部駐車ブロック｜詳細設計 v2

2棟の7段立体＋3か所の平面駐車場。既存A/C内部・B館v4.1・Godotゲーム本体は変更していません。

実際に描画・ID化した外部駐車マスは6,369台です。A館既存22台、B館地下/屋上等のroot統合追加分を含めて水増ししていません。

A東/B南は各7段、P1 0m／P2 2.750m／P3 5.525m／P4 8.200m／P5 10.875m／P6 13.625m／P7屋上16.400m。P3/P5/P7はモールの2F/3F/RFの高さに一致します。

主車路は双方向6m。上下斜路は別々の4m一方向、緩和3m＋直線22m＋緩和3m。P1の高端/P7の低端は防護壁で閉鎖し、架空の次階へ進ませません。最急勾配11.1%、水平平場は下端10.5m/上端9.5mを確保します。

標準2.5×5m、ゆとり2.7×5.2m、身障者3.5×5m＋側方1.2m。後方2m保護歩道、列末の保護歩道、指定横断歩道で階段/EV/地上出口へ接続。

身障者/EV/職員は一般駐車と区分して数えます。大型配送トラックやバスの荷捌きは本設計へ混ぜず、root側の別系統で扱います。

指定敷地ブロック全部を舗装せず、実際のコンパクトな施設範囲を設計。外部の全体車路・モール接続・地下へのスロープはroot統合資料と照合してください。

構造荷重・地盤・排水・法定駐車/避難基準や実車走行、ゲーム車両/歩行AIの検証結果ではありません。ゲーム用設計値として承認を求める資料です。

全台数・用途内訳

各階の台数は図面上の個別ID付きマスを集計。EVや職員を別カウントして総数に二重計上しません。

施設	階層	一般	ゆとり	身障者	EV	職員	合計
P-A-E A東立体駐車場	7	1582	812	49	56	42	2541
P-B-S B南立体駐車場	7	1477	532	56	56	84	2205
P-C-N C北平面駐車場	1	306	131	10	12	6	465
P-B-W B西平面駐車場	1	337	116	8	12	12	485
P-A-S A南平面駐車場	1	450	195	10	12	6	673

外部合計 6,369台 / 立体屋上P7も個別マスを配置 / 既存A22台・B追加区画は別集計

駐車マスはstall-ledger.csvとgeometry.jsonに facility/level/id/category/width/length/車路前面点/後方歩道接続点/実ポリゴンを収録。全IDは施設-段-4桁番号です。

図面内は4桁番号を表示し、各ページの接頭辞と組み合わせて一意に照合できます。集計上の台数と実図形の数が一致することを検査します。

EV充電の受電容量・充電器実型式、身障者指定数の法的充足、歩行実測・運用費・収益は未検証です。用途を物理マスと別の架空容量として加算していません。

A東立体駐車場｜P1 +0.000m / 363台

モール1F / ID接頭辞 P-A-E-L00- / 青=一般・黄=ゆとり・水色=身障者・緑=EV・灰=職員

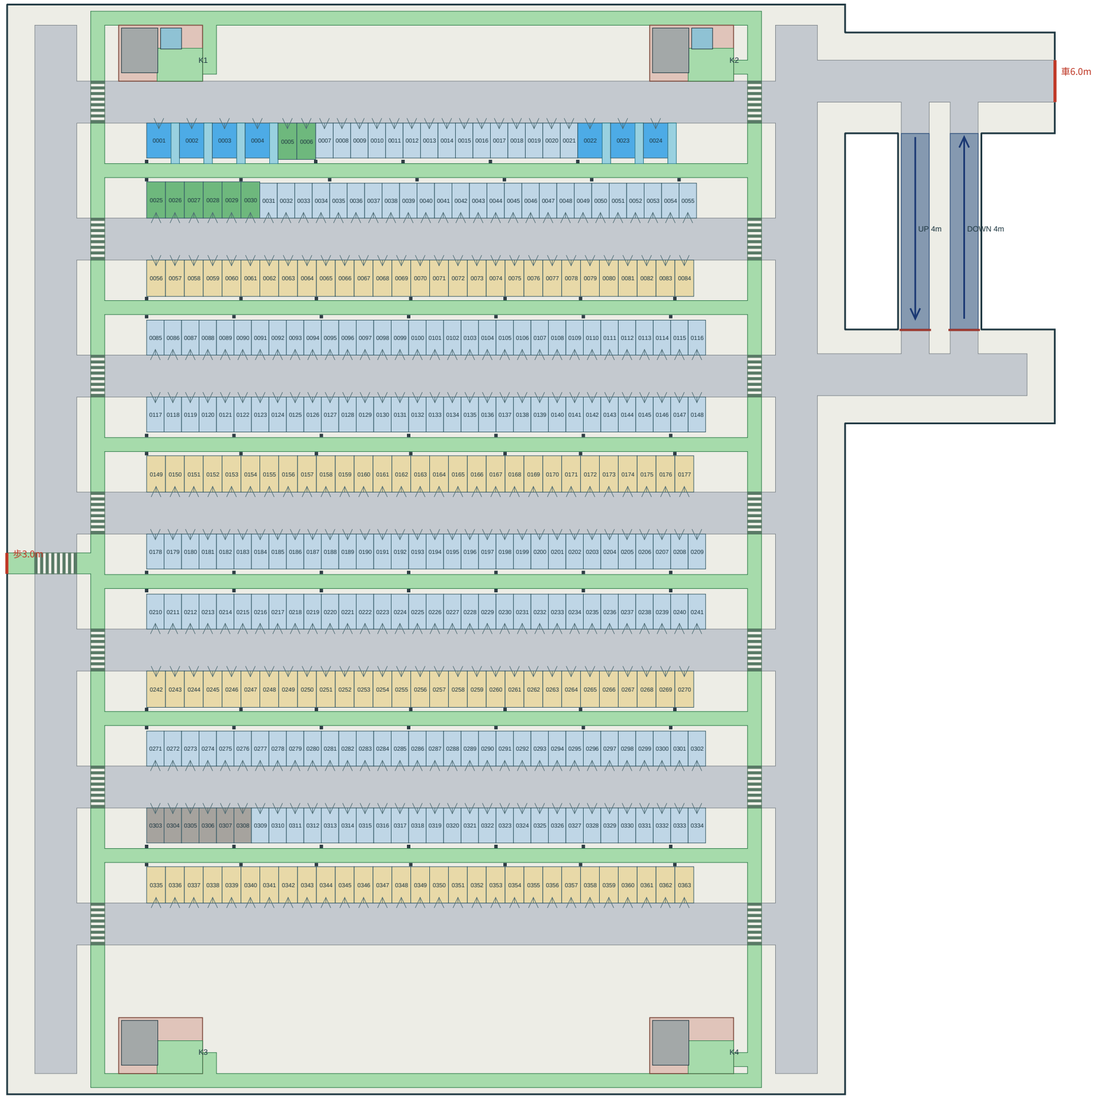

ID prefix: P-A-E-L00- / 4-digit bay labels + prefix = full stall ID

台数：一般226 / ゆとり116 / 身障者用7 / 充電EV8 / 職員6。赤は地上/橋受け口、緑は保護歩道、縞は指定横断歩道。

外周防護/転落防止1.2m。P1高端/P7低端の斜路口は赤茶の防護壁で閉鎖。上階の未接続口は仮設柵を維持し、橋が実際につながるまで開放しない。

4.8×2.0m車両のR6m旋回図形を車路・斜路平場内で検査。個々の駐車の切返しや実車制御を実測した結果ではありません。

A東立体駐車場｜P2 +2.750m / 363台

中間駐車段（モール直結なし） / ID接頭辞 P-A-E-L01- / 青=一般・黄=ゆとり・水色=身障者・緑=EV・灰=職員

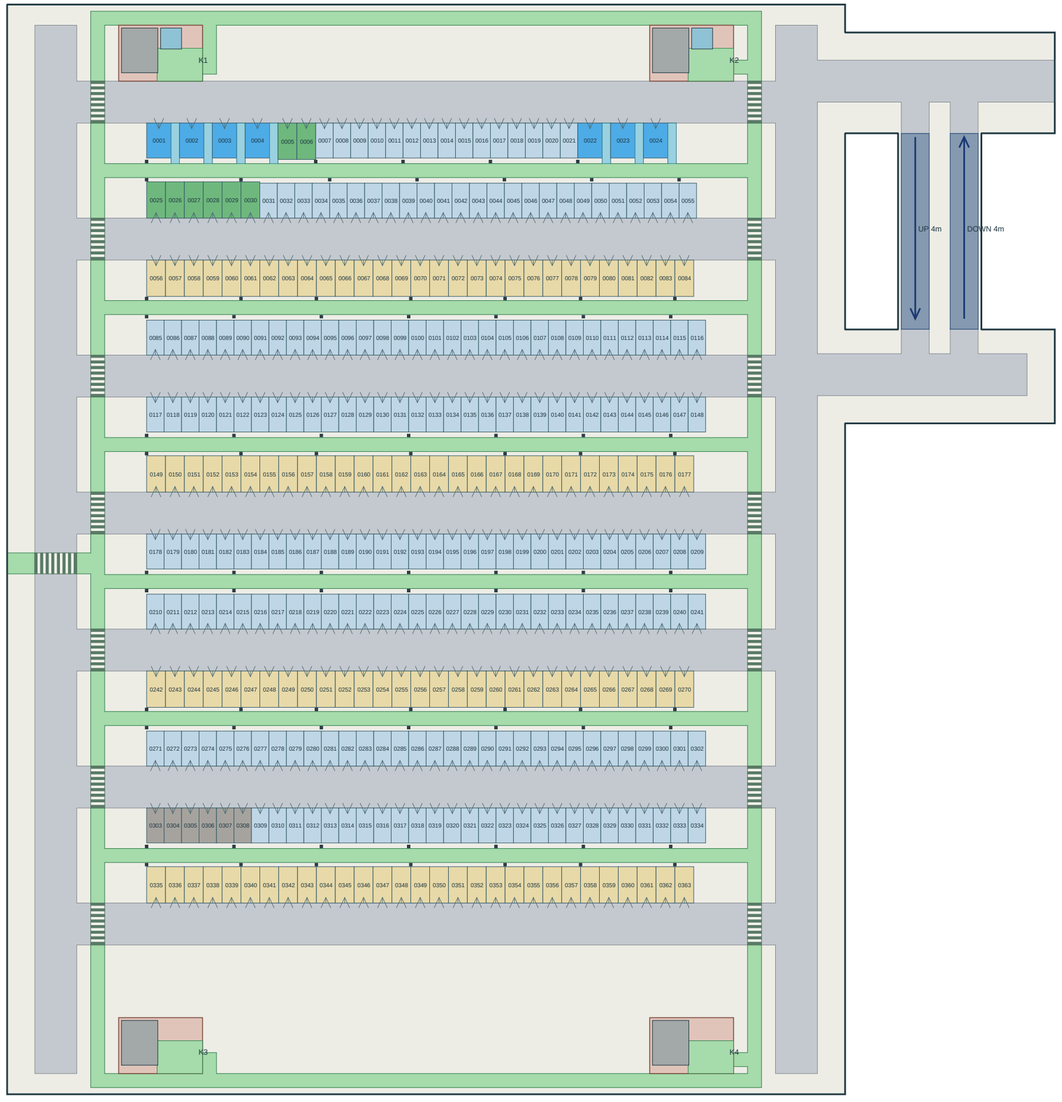

ID prefix: P-A-E-L01- / 4-digit bay labels + prefix = full stall ID

台数：一般226 / ゆとり116 / 身障者用7 / 充電EV8 / 職員6。赤は地上/橋受け口、緑は保護歩道、縞は指定横断歩道。

外周防護/転落防止1.2m。P1高端/P7低端の斜路口は赤茶の防護壁で閉鎖。上階の未接続口は仮設柵を維持し、橋が実際につながるまで開放しない。

4.8×2.0m車両のR6m旋回図形を車路・斜路平場内で検査。個々の駐車の切返しや実車制御を実測した結果ではありません。

A東立体駐車場｜P3 +5.525m / 363台

モール2F高 / ID接頭辞 P-A-E-L02- / 青=一般・黄=ゆとり・水色=身障者・緑=EV・灰=職員

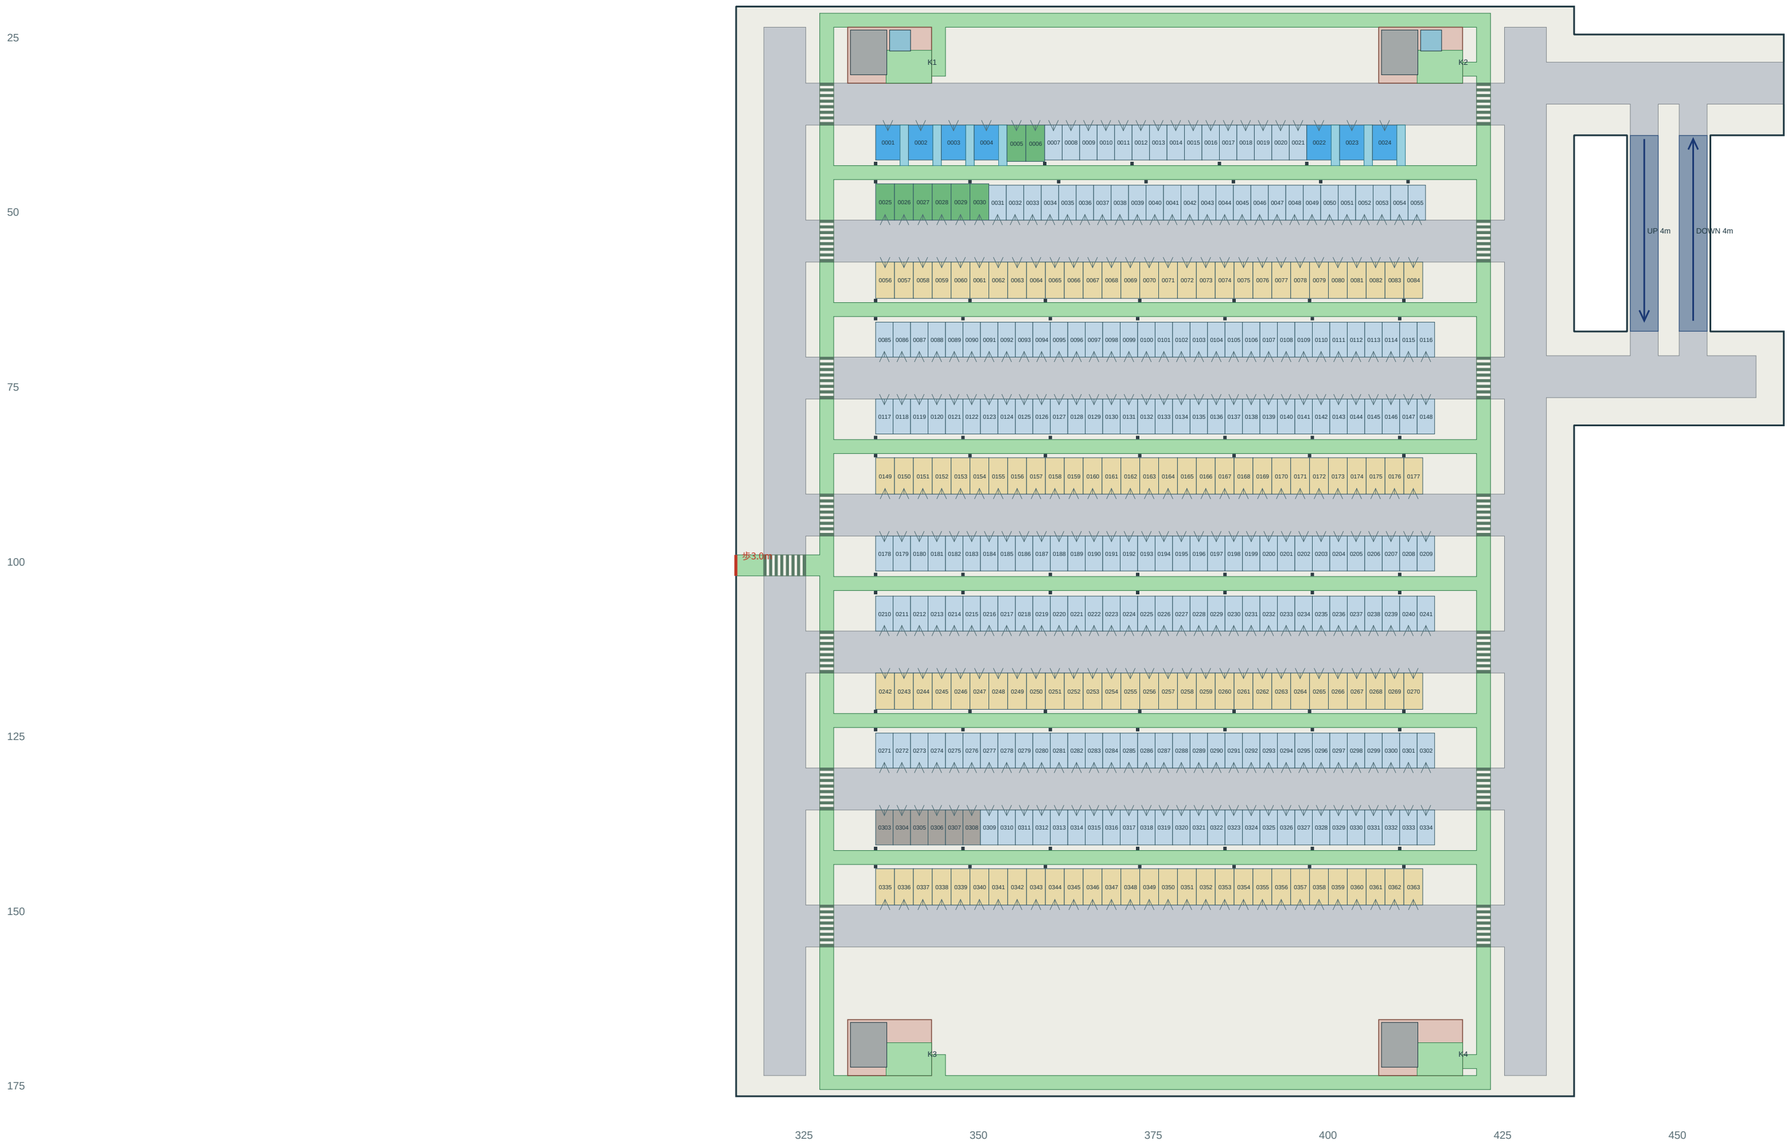

ID prefix: P-A-E-L02- / 4-digit bay labels + prefix = full stall ID

台数：一般226 / ゆとり116 / 身障者用7 / 充電EV8 / 職員6。赤は地上/橋受け口、緑は保護歩道、縞は指定横断歩道。

外周防護/転落防止1.2m。P1高端/P7低端の斜路口は赤茶の防護壁で閉鎖。上階の未接続口は仮設柵を維持し、橋が実際につながるまで開放しない。

4.8×2.0m車両のR6m旋回図形を車路・斜路平場内で検査。個々の駐車の切返しや実車制御を実測した結果ではありません。

A東立体駐車場｜P4 +8.200m / 363台

中間駐車段（モール直結なし） / ID接頭辞 P-A-E-L03- / 青=一般・黄=ゆとり・水色=身障者・緑=EV・灰=職員

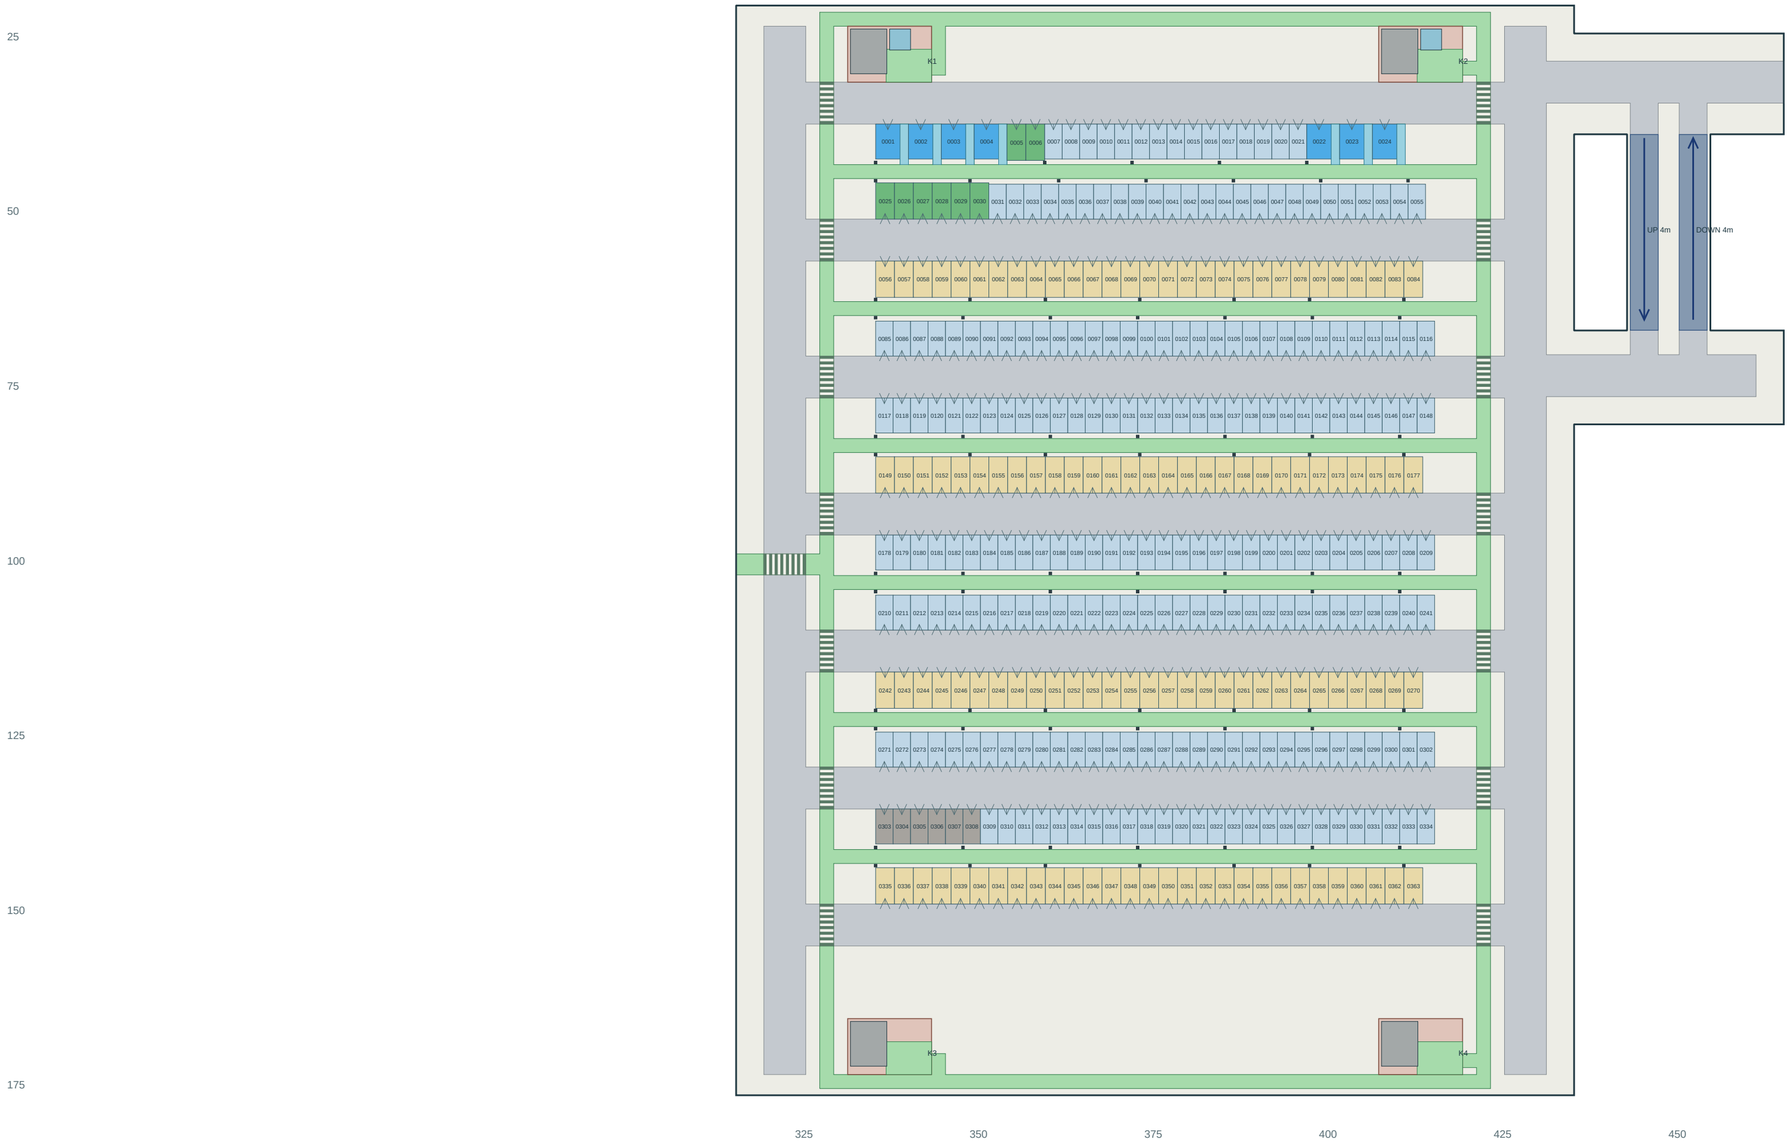

ID prefix: P-A-E-L03- / 4-digit bay labels + prefix = full stall ID

台数：一般226 / ゆとり116 / 身障者用7 / 充電EV8 / 職員6。赤は地上/橋受け口、緑は保護歩道、縞は指定横断歩道。

外周防護/転落防止1.2m。P1高端/P7低端の斜路口は赤茶の防護壁で閉鎖。上階の未接続口は仮設柵を維持し、橋が実際につながるまで開放しない。

4.8×2.0m車両のR6m旋回図形を車路・斜路平場内で検査。個々の駐車の切返しや実車制御を実測した結果ではありません。

A東立体駐車場｜P5 +10.875m / 363台

モール3F高 / ID接頭辞 P-A-E-L04- / 青=一般・黄=ゆとり・水色=身障者・緑=EV・灰=職員

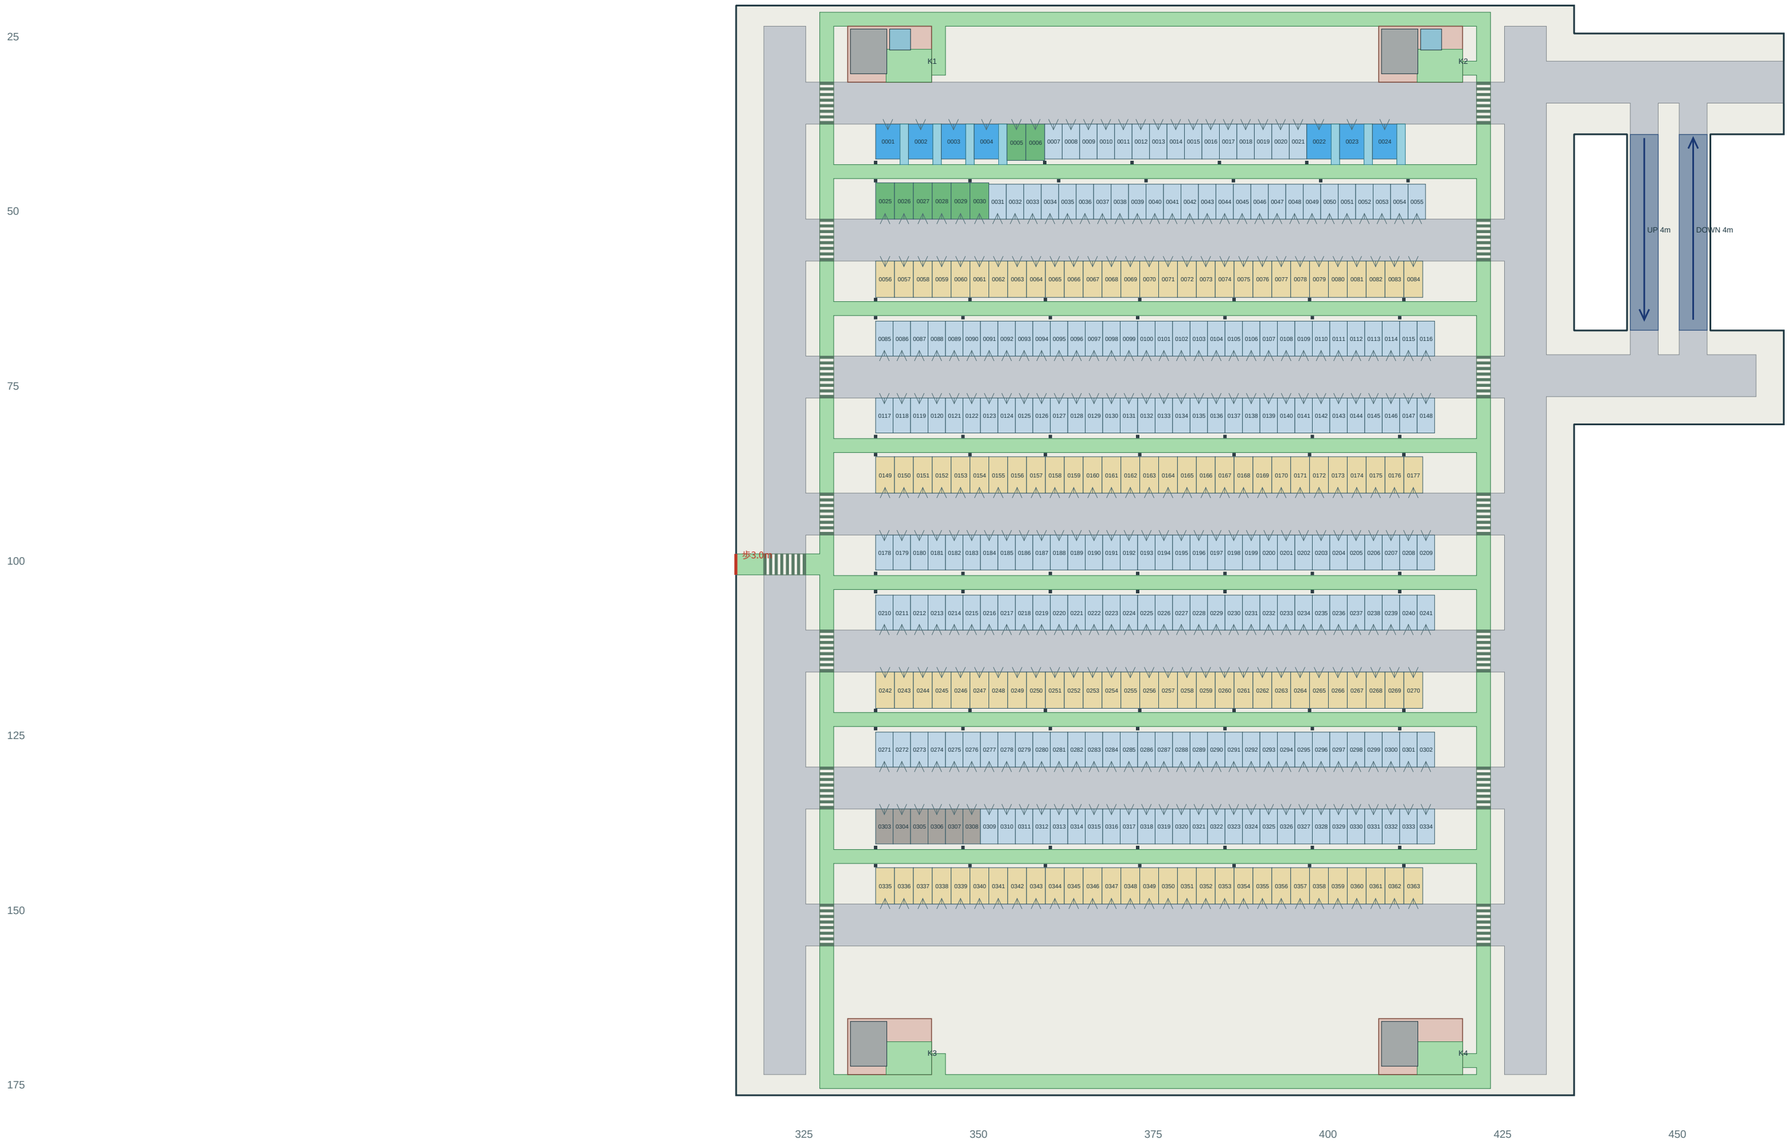

ID prefix: P-A-E-L04- / 4-digit bay labels + prefix = full stall ID

台数：一般226 / ゆとり116 / 身障者用7 / 充電EV8 / 職員6。赤は地上/橋受け口、緑は保護歩道、縞は指定横断歩道。

外周防護/転落防止1.2m。P1高端/P7低端の斜路口は赤茶の防護壁で閉鎖。上階の未接続口は仮設柵を維持し、橋が実際につながるまで開放しない。

4.8×2.0m車両のR6m旋回図形を車路・斜路平場内で検査。個々の駐車の切返しや実車制御を実測した結果ではありません。

A東立体駐車場｜P6 +13.625m / 363台

中間駐車段（モール直結なし） / ID接頭辞 P-A-E-L05- / 青=一般・黄=ゆとり・水色=身障者・緑=EV・灰=職員

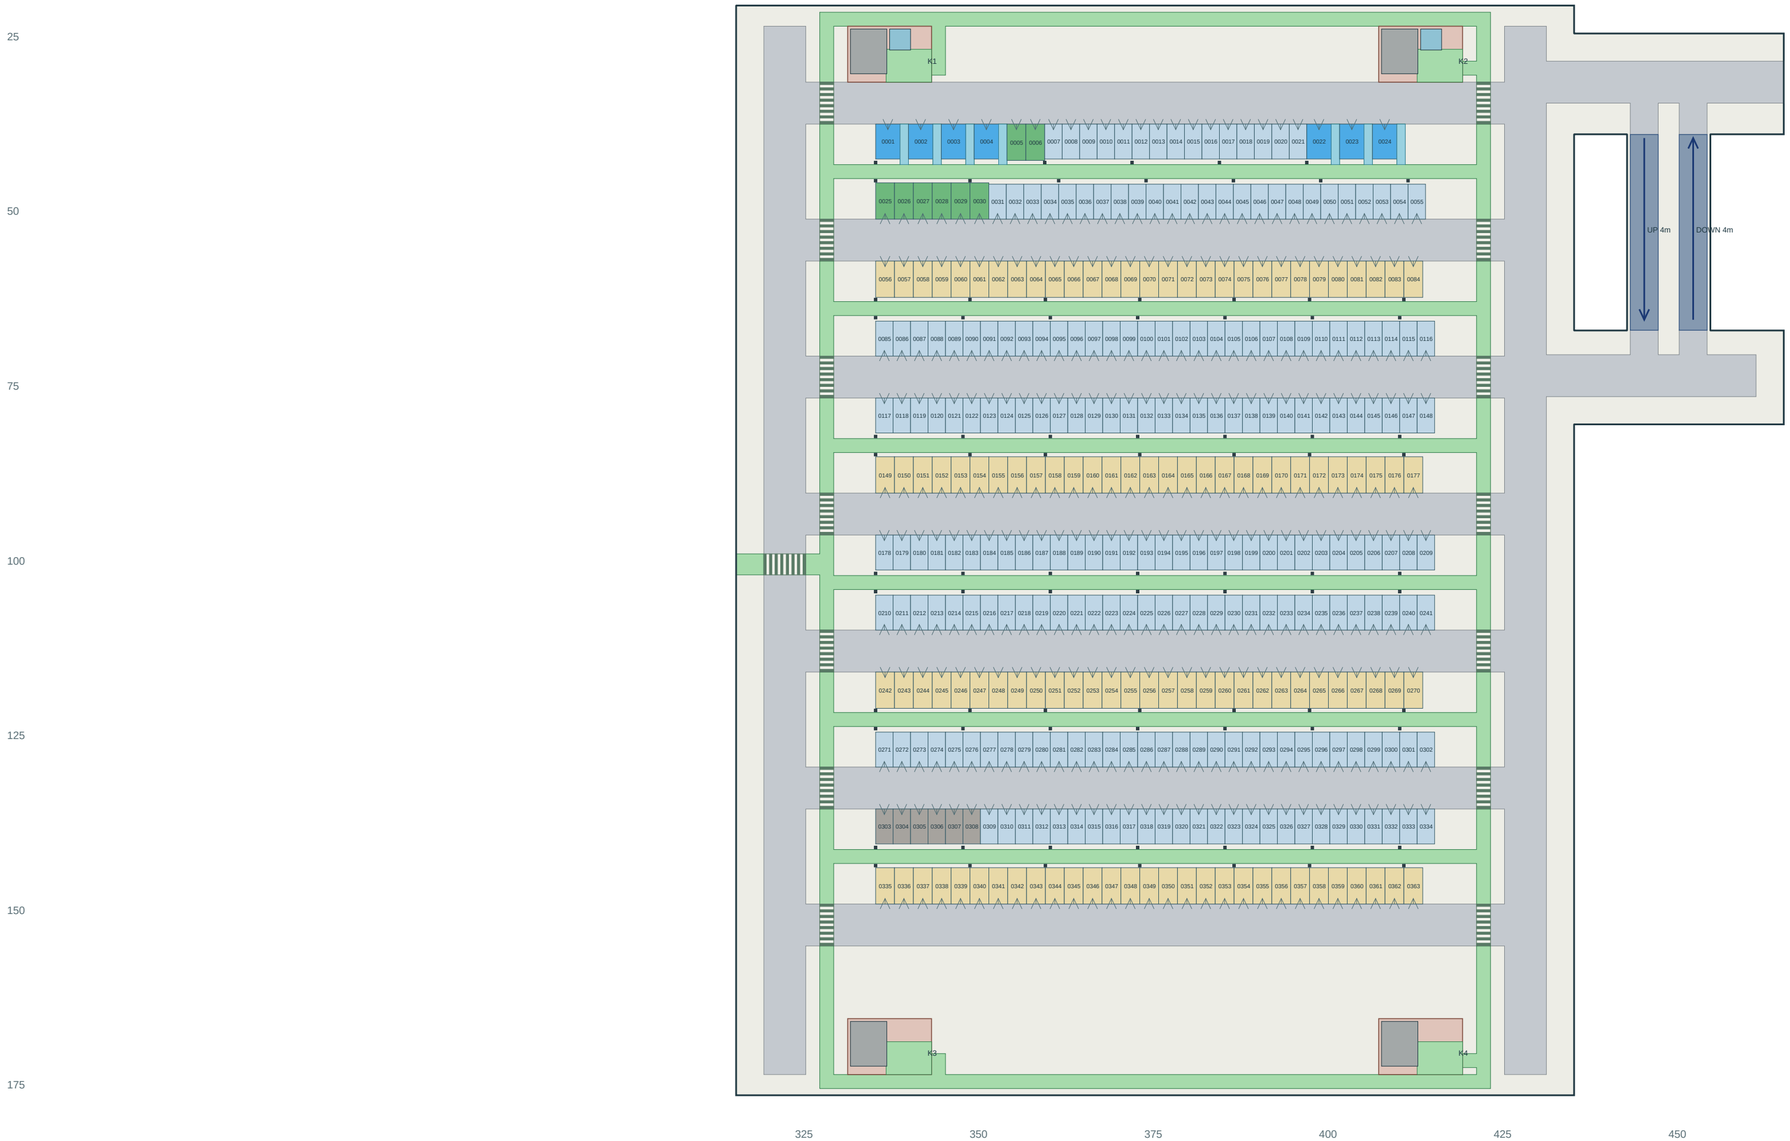

ID prefix: P-A-E-L05- / 4-digit bay labels + prefix = full stall ID

台数：一般226 / ゆとり116 / 身障者用7 / 充電EV8 / 職員6。赤は地上/橋受け口、緑は保護歩道、縞は指定横断歩道。

外周防護/転落防止1.2m。P1高端/P7低端の斜路口は赤茶の防護壁で閉鎖。上階の未接続口は仮設柵を維持し、橋が実際につながるまで開放しない。

4.8×2.0m車両のR6m旋回図形を車路・斜路平場内で検査。個々の駐車の切返しや実車制御を実測した結果ではありません。

A東立体駐車場｜P7 +16.400m / 363台

モールRF高 / ID接頭辞 P-A-E-L06- / 青=一般・黄=ゆとり・水色=身障者・緑=EV・灰=職員

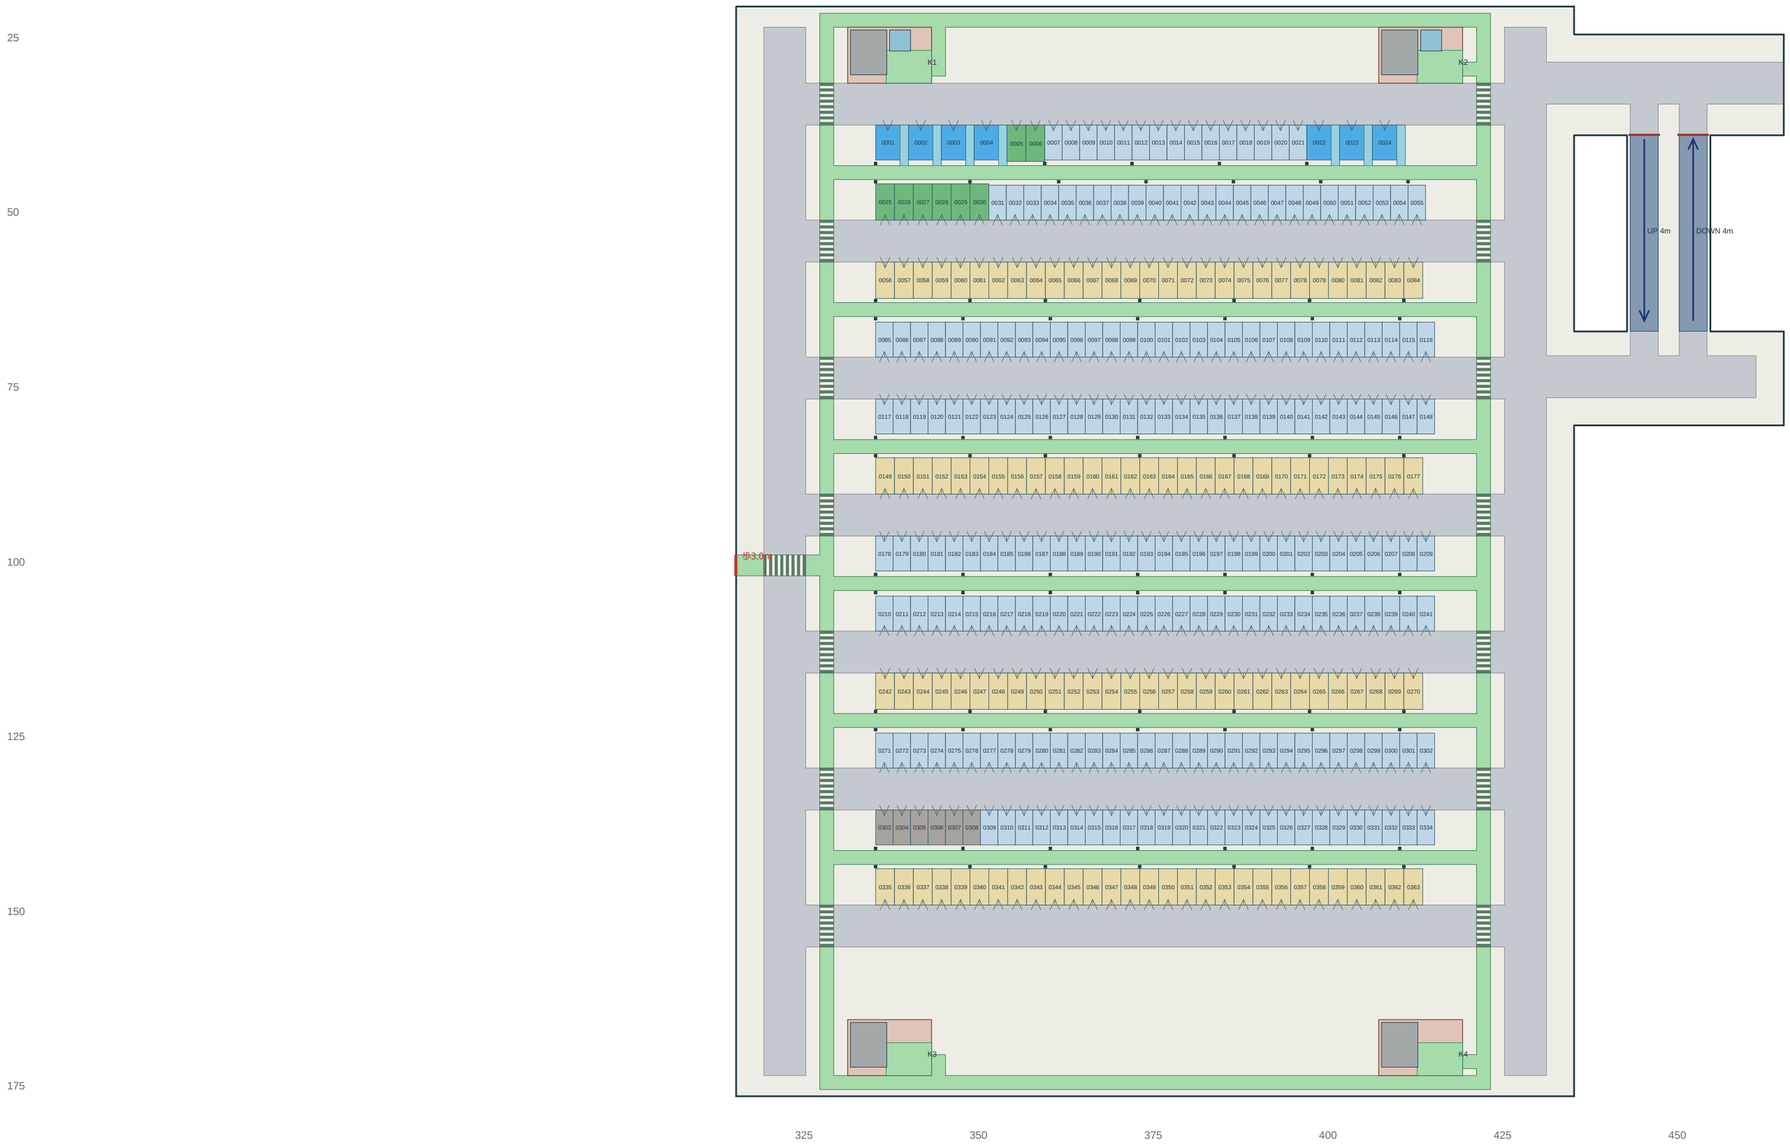

ID prefix: P-A-E-L06- / 4-digit bay labels + prefix = full stall ID

台数：一般226 / ゆとり116 / 身障者用7 / 充電EV8 / 職員6。赤は地上/橋受け口、緑は保護歩道、縞は指定横断歩道。

外周防護/転落防止1.2m。P1高端/P7低端の斜路口は赤茶の防護壁で閉鎖。上階の未接続口は仮設柵を維持し、橋が実際につながるまで開放しない。

4.8×2.0m車両のR6m旋回図形を車路・斜路平場内で検査。個々の駐車の切返しや実車制御を実測した結果ではありません。

A東立体駐車場｜駐車モジュール拡大

標準/ゆとり/身障者側方通路・後方保護歩道・柱・車路・横断歩道とEV/階段前室を拡大。

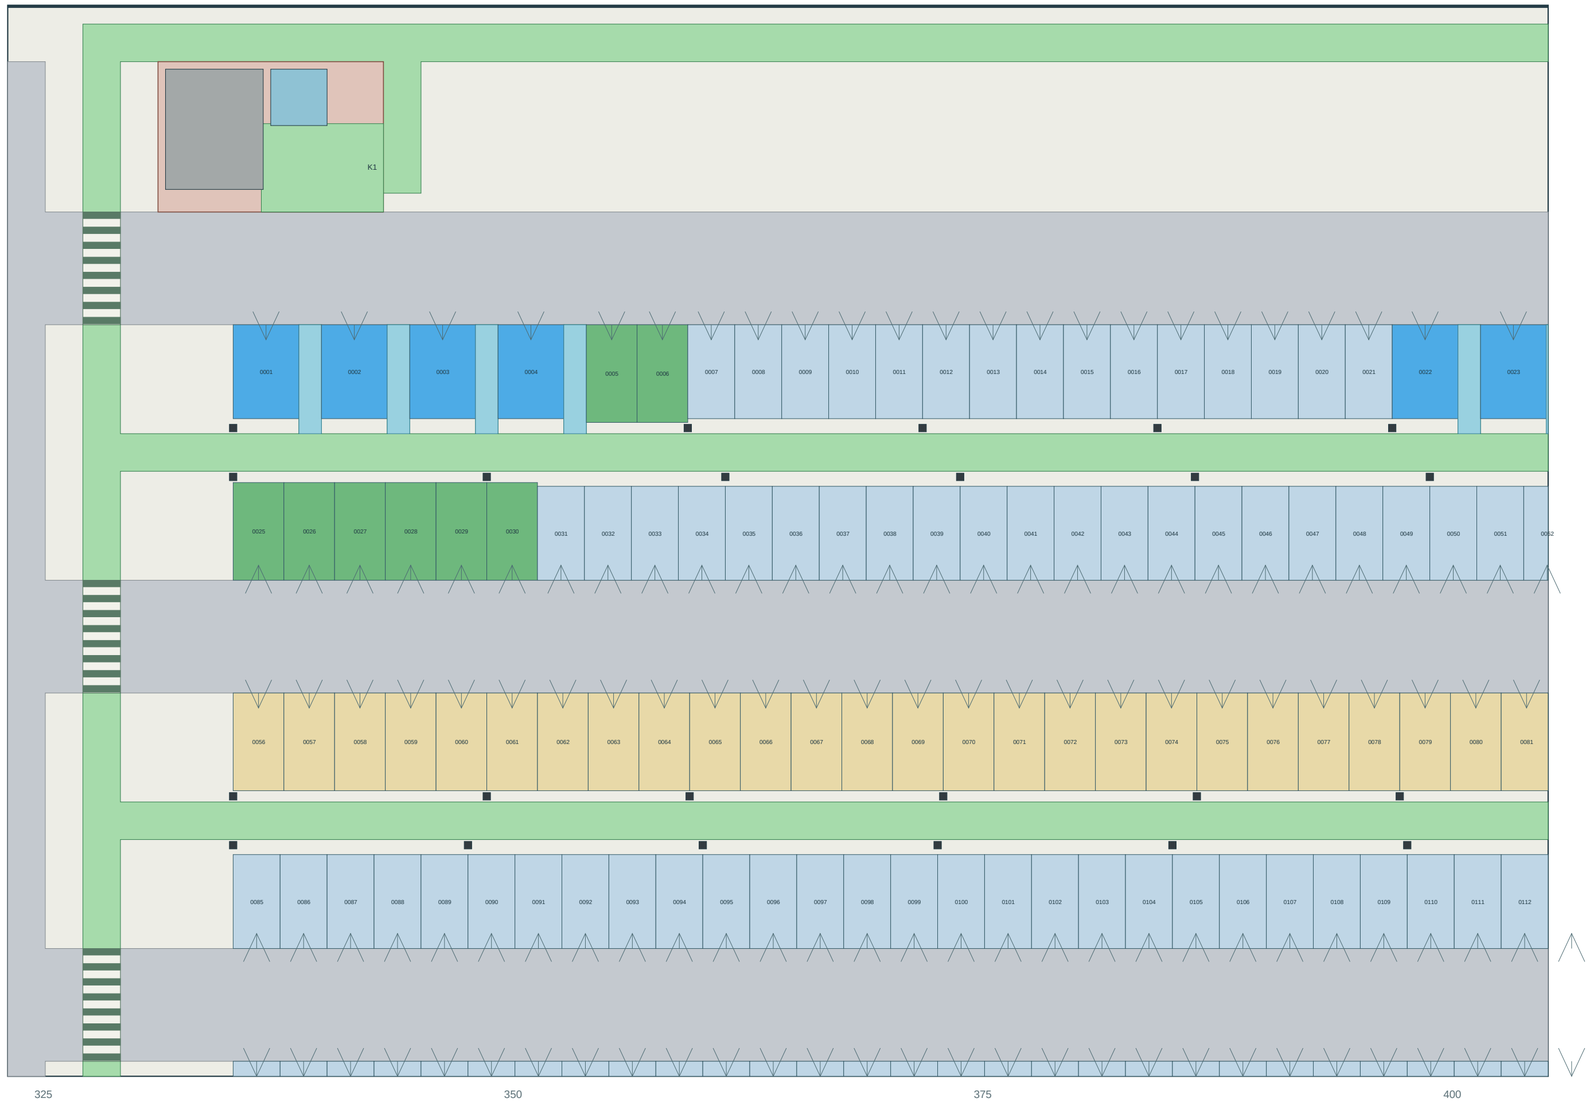

車路6m、後方保護歩道2m。背面サービス帯に0.4m角柱を配置し、駐車ポリゴン・歩道・各マスの後方アクセス線へ食い込まないことを検査。

身障者マス3.5m＋側方1.2m、ゆとりマス2.7m×5.2m。幾何上の位置を具体化した設計値で、構造/バリアフリー適合の認証ではない。

B南立体駐車場｜P1 +0.000m / 315台

モール1F / ID接頭辞 P-B-S-L00- / 青=一般・黄=ゆとり・水色=身障者・緑=EV・灰=職員

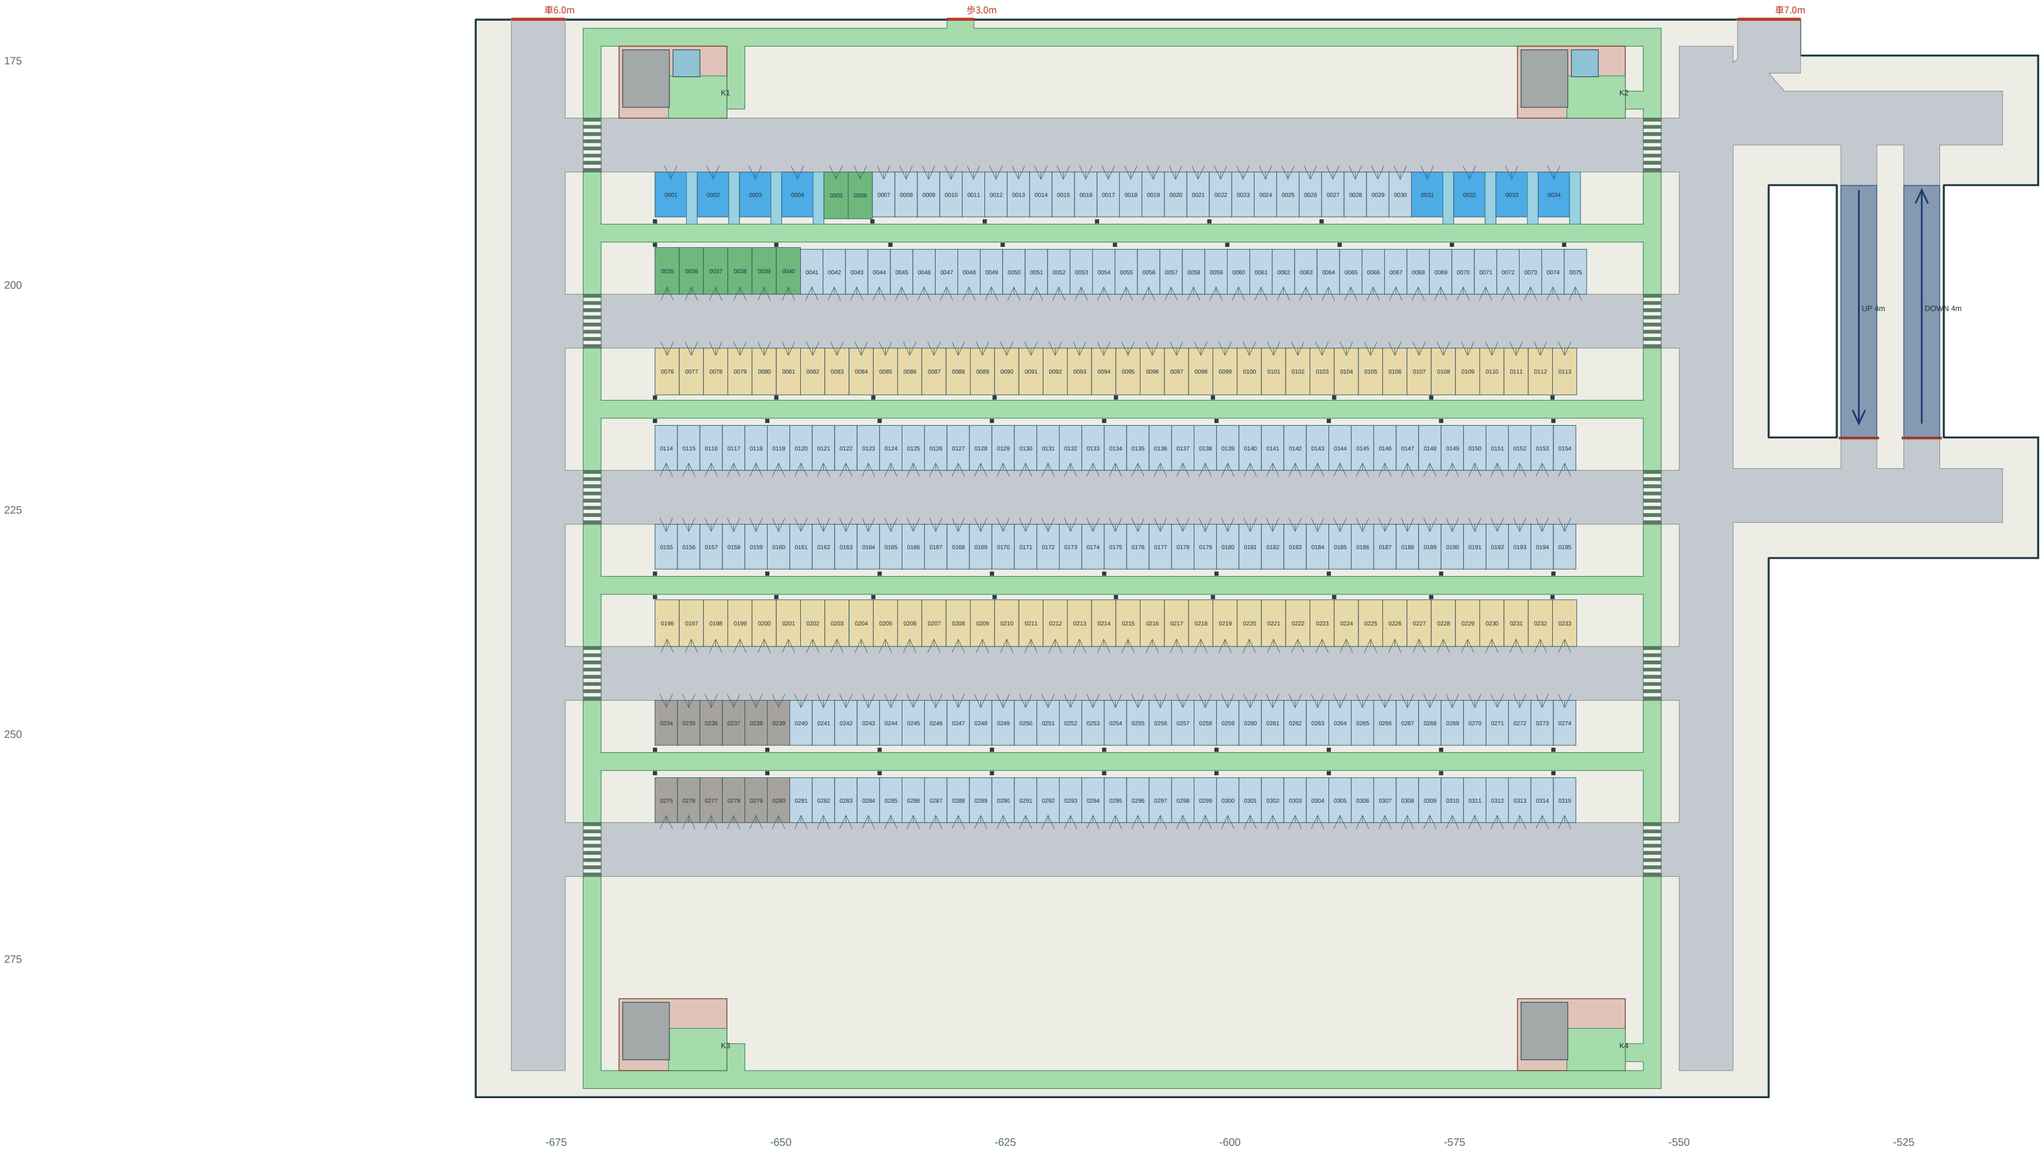

ID prefix: P-B-S-L00- / 4-digit bay labels + prefix = full stall ID

台数：一般211 / ゆとり76 / 身障者用8 / 充電EV8 / 職員12。赤は地上/橋受け口、緑は保護歩道、縞は指定横断歩道。

外周防護/転落防止1.2m。P1高端/P7低端の斜路口は赤茶の防護壁で閉鎖。上階の未接続口は仮設柵を維持し、橋が実際につながるまで開放しない。

4.8×2.0m車両のR6m旋回図形を車路・斜路平場内で検査。個々の駐車の切返しや実車制御を実測した結果ではありません。

B南立体駐車場｜P2 +2.750m / 315台

中間駐車段（モール直結なし） / ID接頭辞 P-B-S-L01- / 青=一般・黄=ゆとり・水色=身障者・緑=EV・灰=職員

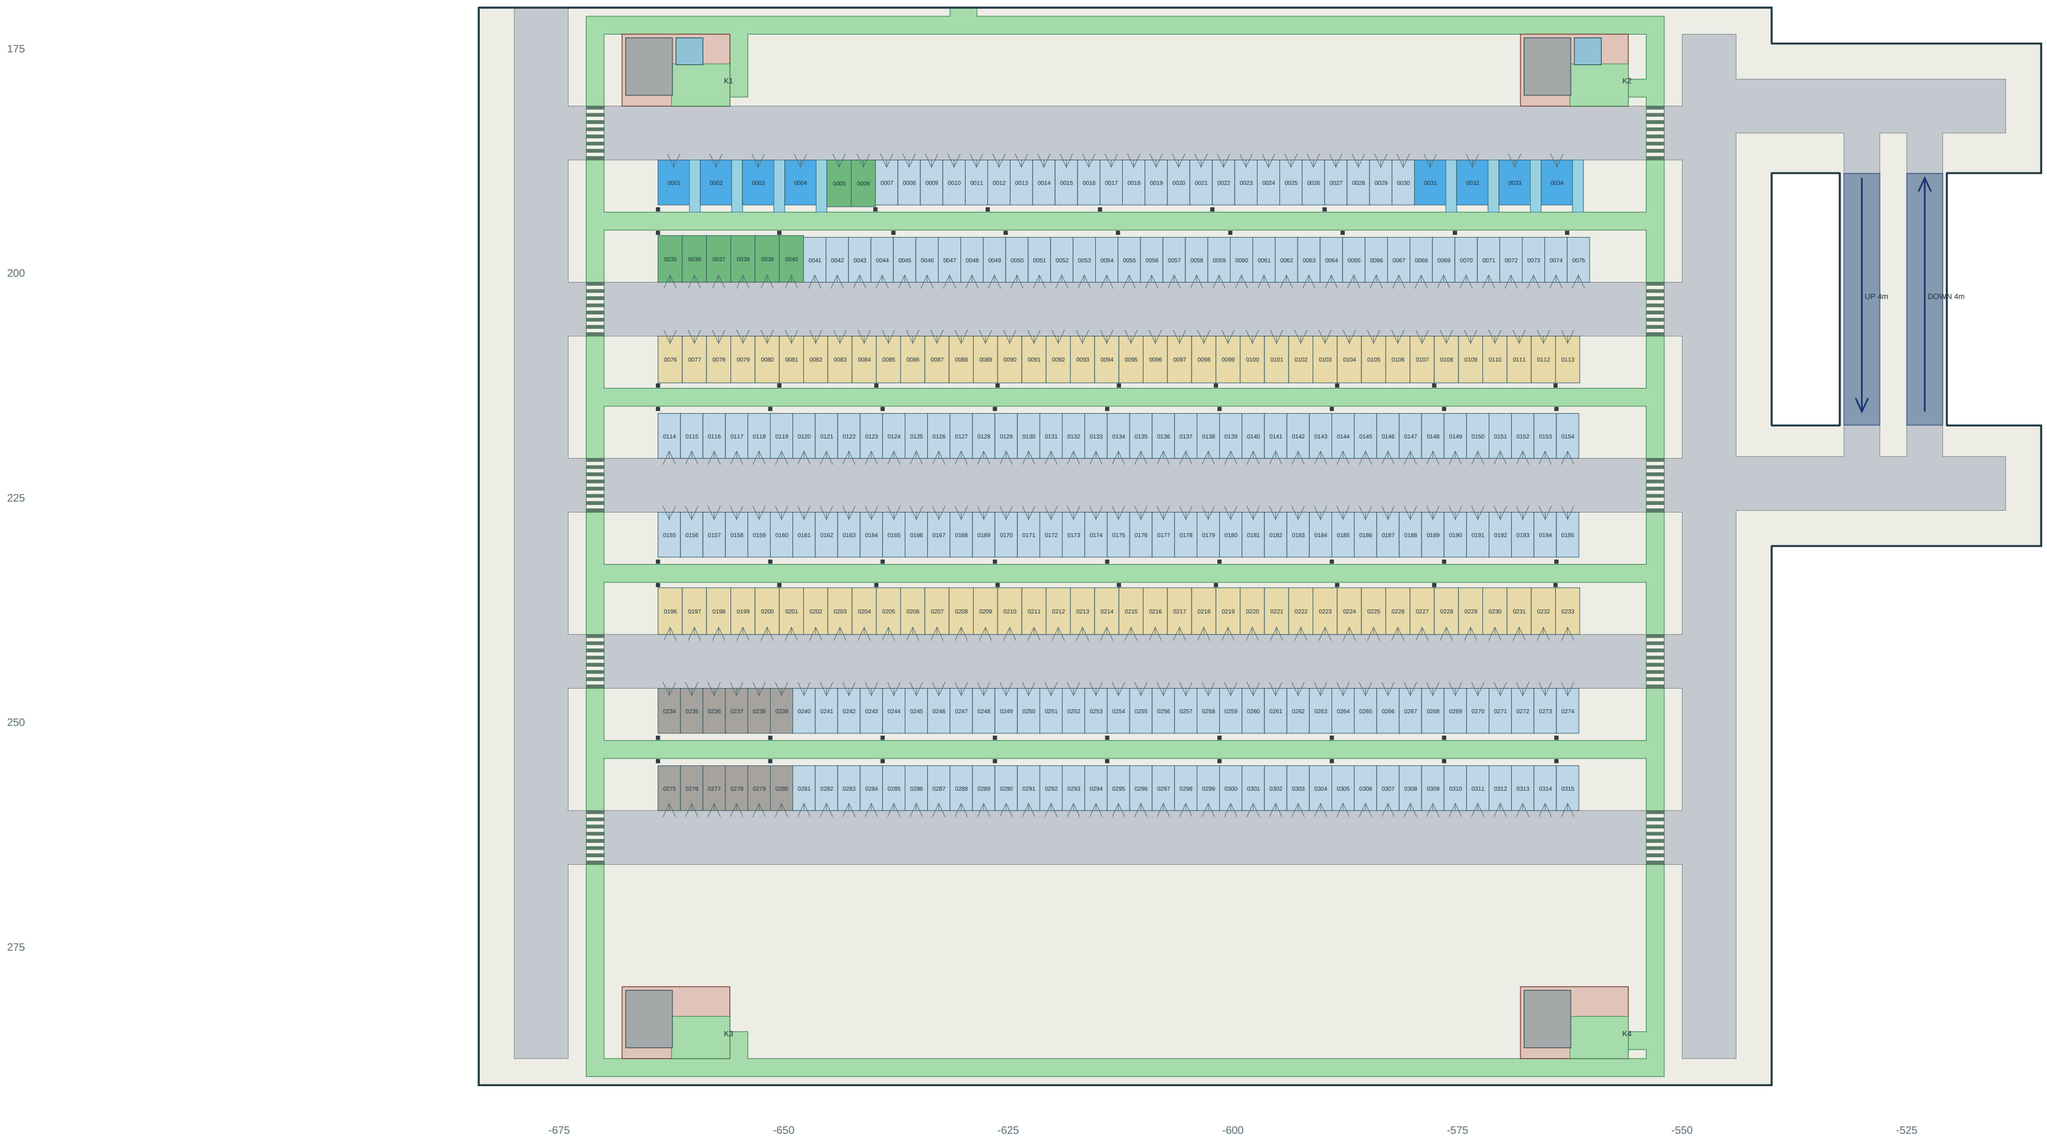

ID prefix: P-B-S-L01- / 4-digit bay labels + prefix = full stall ID

台数：一般211 / ゆとり76 / 身障者用8 / 充電EV8 / 職員12。赤は地上/橋受け口、緑は保護歩道、縞は指定横断歩道。

外周防護/転落防止1.2m。P1高端/P7低端の斜路口は赤茶の防護壁で閉鎖。上階の未接続口は仮設柵を維持し、橋が実際につながるまで開放しない。

4.8×2.0m車両のR6m旋回図形を車路・斜路平場内で検査。個々の駐車の切返しや実車制御を実測した結果ではありません。

B南立体駐車場｜P3 +5.525m / 315台

モール2F高 / ID接頭辞 P-B-S-L02- / 青=一般・黄=ゆとり・水色=身障者・緑=EV・灰=職員

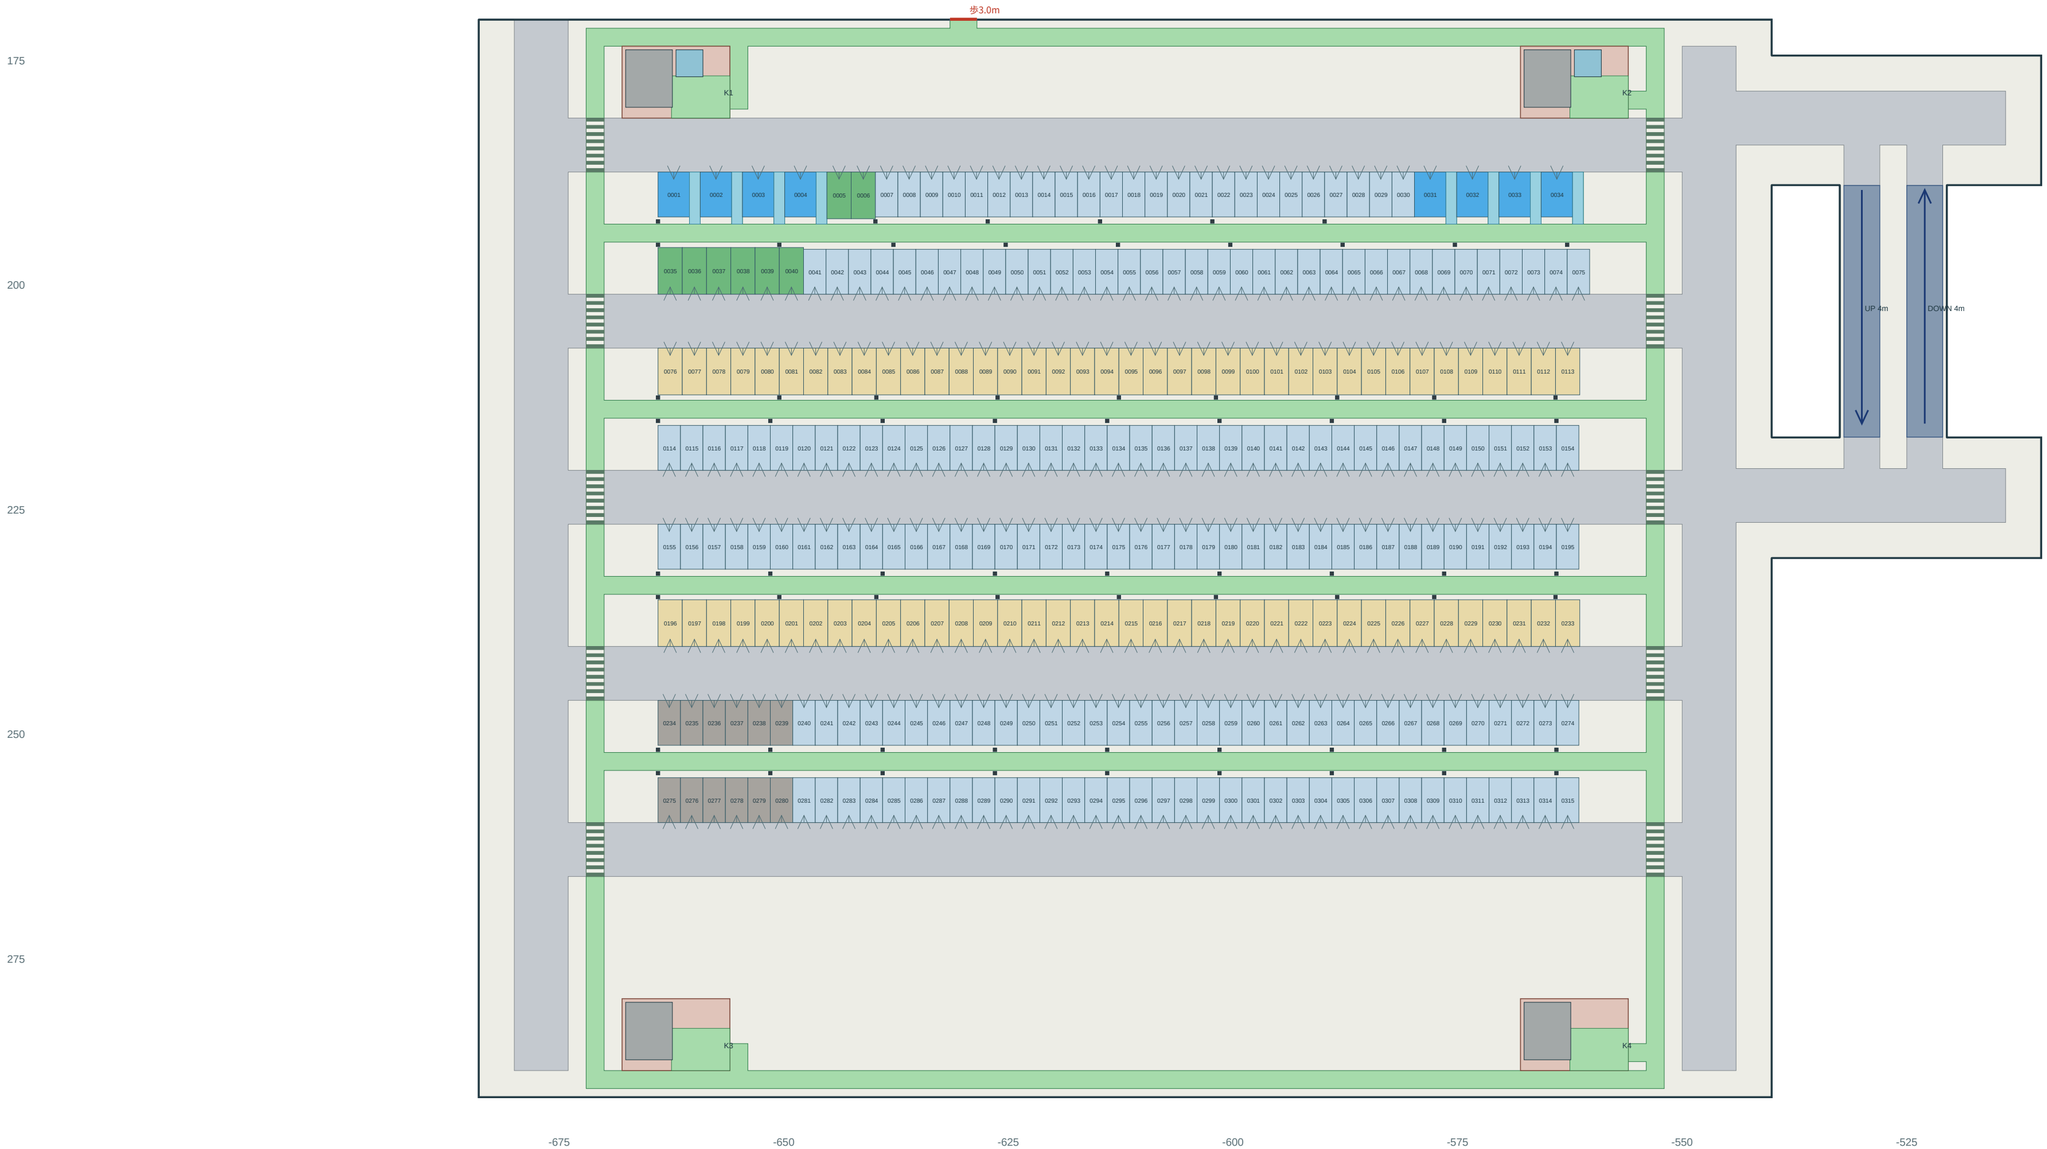

ID prefix: P-B-S-L02- / 4-digit bay labels + prefix = full stall ID

台数：一般211 / ゆとり76 / 身障者用8 / 充電EV8 / 職員12。赤は地上/橋受け口、緑は保護歩道、縞は指定横断歩道。

外周防護/転落防止1.2m。P1高端/P7低端の斜路口は赤茶の防護壁で閉鎖。上階の未接続口は仮設柵を維持し、橋が実際につながるまで開放しない。

4.8×2.0m車両のR6m旋回図形を車路・斜路平場内で検査。個々の駐車の切返しや実車制御を実測した結果ではありません。

B南立体駐車場｜P4 +8.200m / 315台

中間駐車段（モール直結なし） / ID接頭辞 P-B-S-L03- / 青=一般・黄=ゆとり・水色=身障者・緑=EV・灰=職員

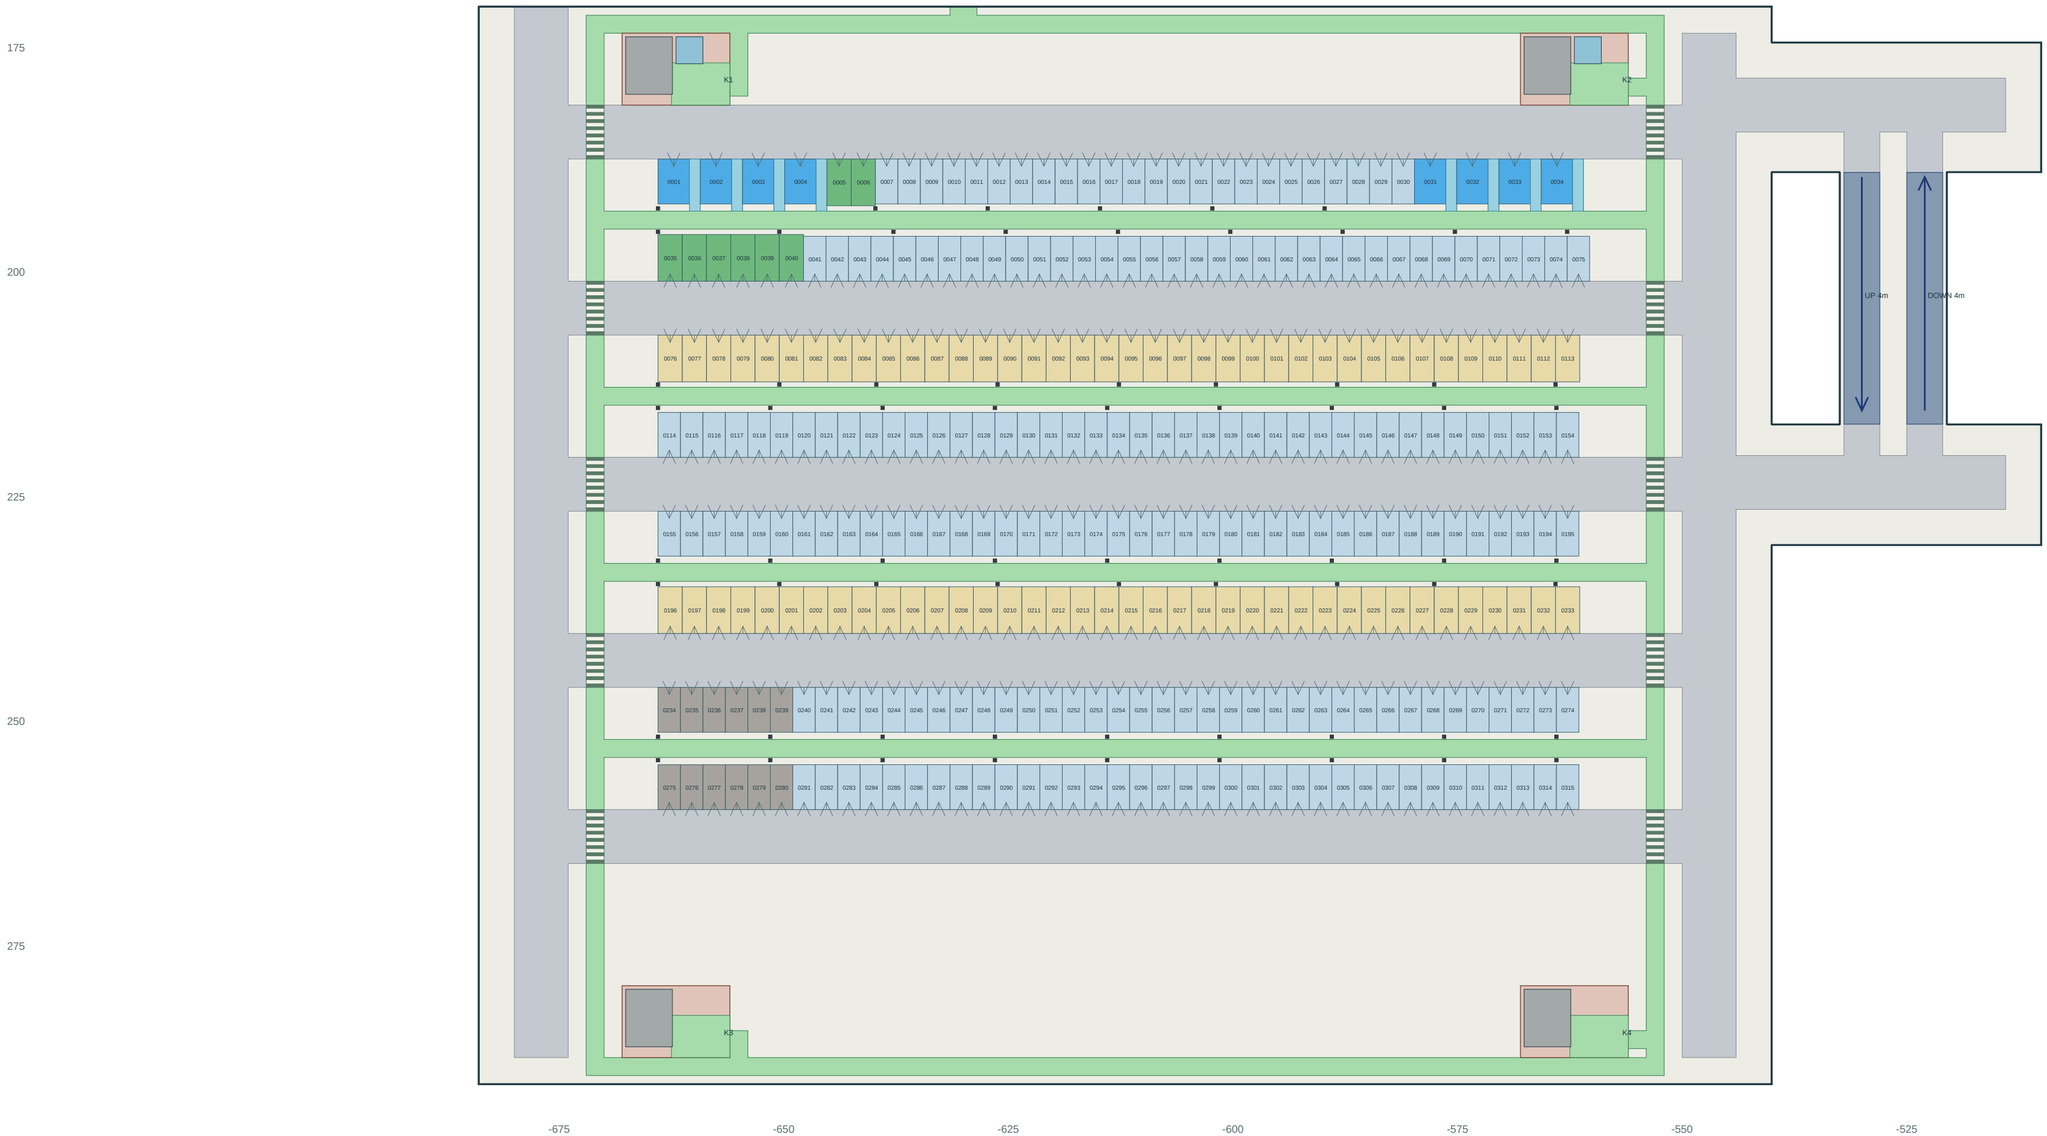

ID prefix: P-B-S-L03- / 4-digit bay labels + prefix = full stall ID

台数：一般211 / ゆとり76 / 身障者用8 / 充電EV8 / 職員12。赤は地上/橋受け口、緑は保護歩道、縞は指定横断歩道。

外周防護/転落防止1.2m。P1高端/P7低端の斜路口は赤茶の防護壁で閉鎖。上階の未接続口は仮設柵を維持し、橋が実際につながるまで開放しない。

4.8×2.0m車両のR6m旋回図形を車路・斜路平場内で検査。個々の駐車の切返しや実車制御を実測した結果ではありません。

B南立体駐車場｜P5 +10.875m / 315台

モール3F高 / ID接頭辞 P-B-S-L04- / 青=一般・黄=ゆとり・水色=身障者・緑=EV・灰=職員

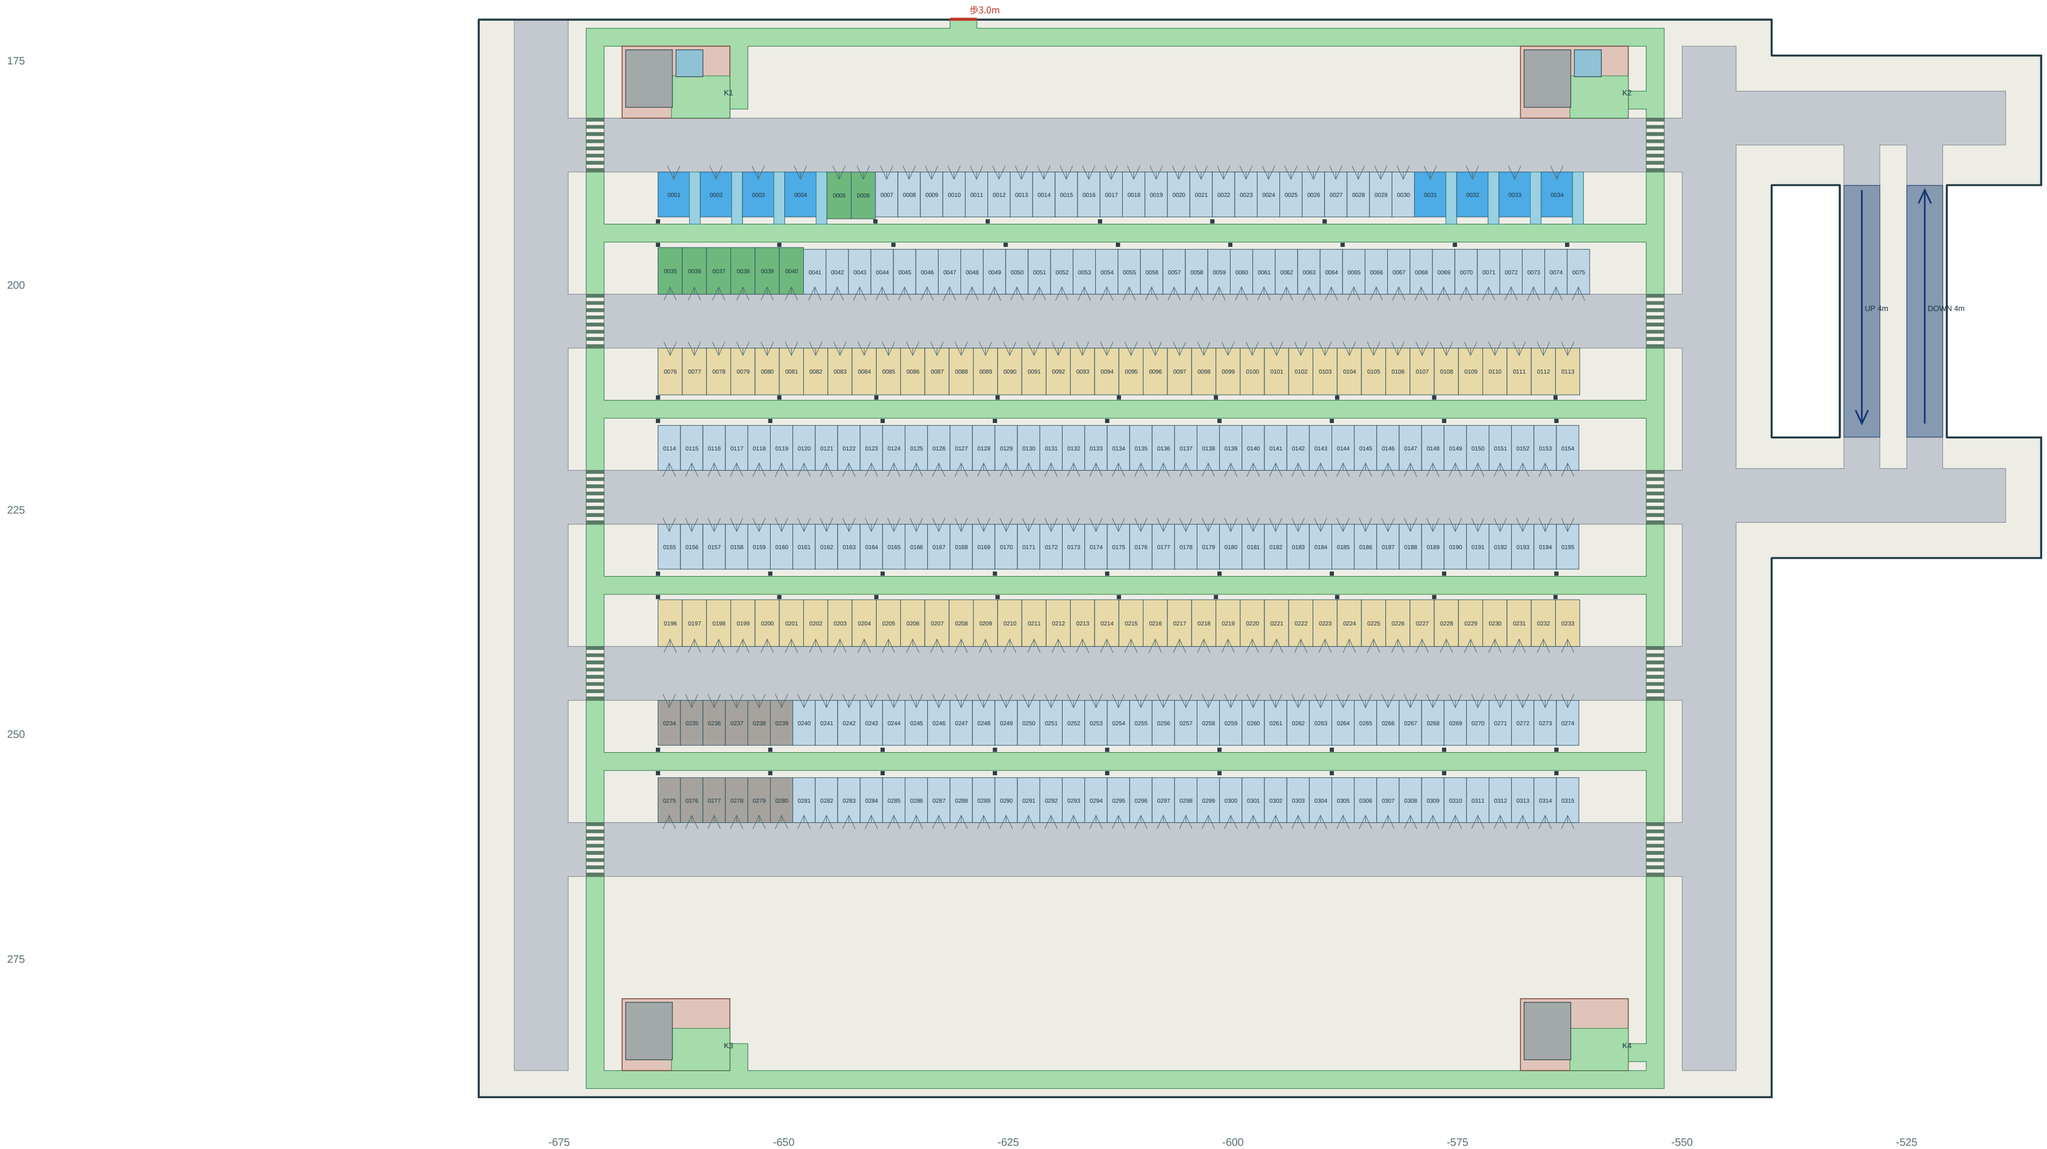

ID prefix: P-B-S-L04- / 4-digit bay labels + prefix = full stall ID

台数：一般211 / ゆとり76 / 身障者用8 / 充電EV8 / 職員12。赤は地上/橋受け口、緑は保護歩道、縞は指定横断歩道。

外周防護/転落防止1.2m。P1高端/P7低端の斜路口は赤茶の防護壁で閉鎖。上階の未接続口は仮設柵を維持し、橋が実際につながるまで開放しない。

4.8×2.0m車両のR6m旋回図形を車路・斜路平場内で検査。個々の駐車の切返しや実車制御を実測した結果ではありません。

B南立体駐車場｜P6 +13.625m / 315台

中間駐車段（モール直結なし） / ID接頭辞 P-B-S-L05- / 青=一般・黄=ゆとり・水色=身障者・緑=EV・灰=職員

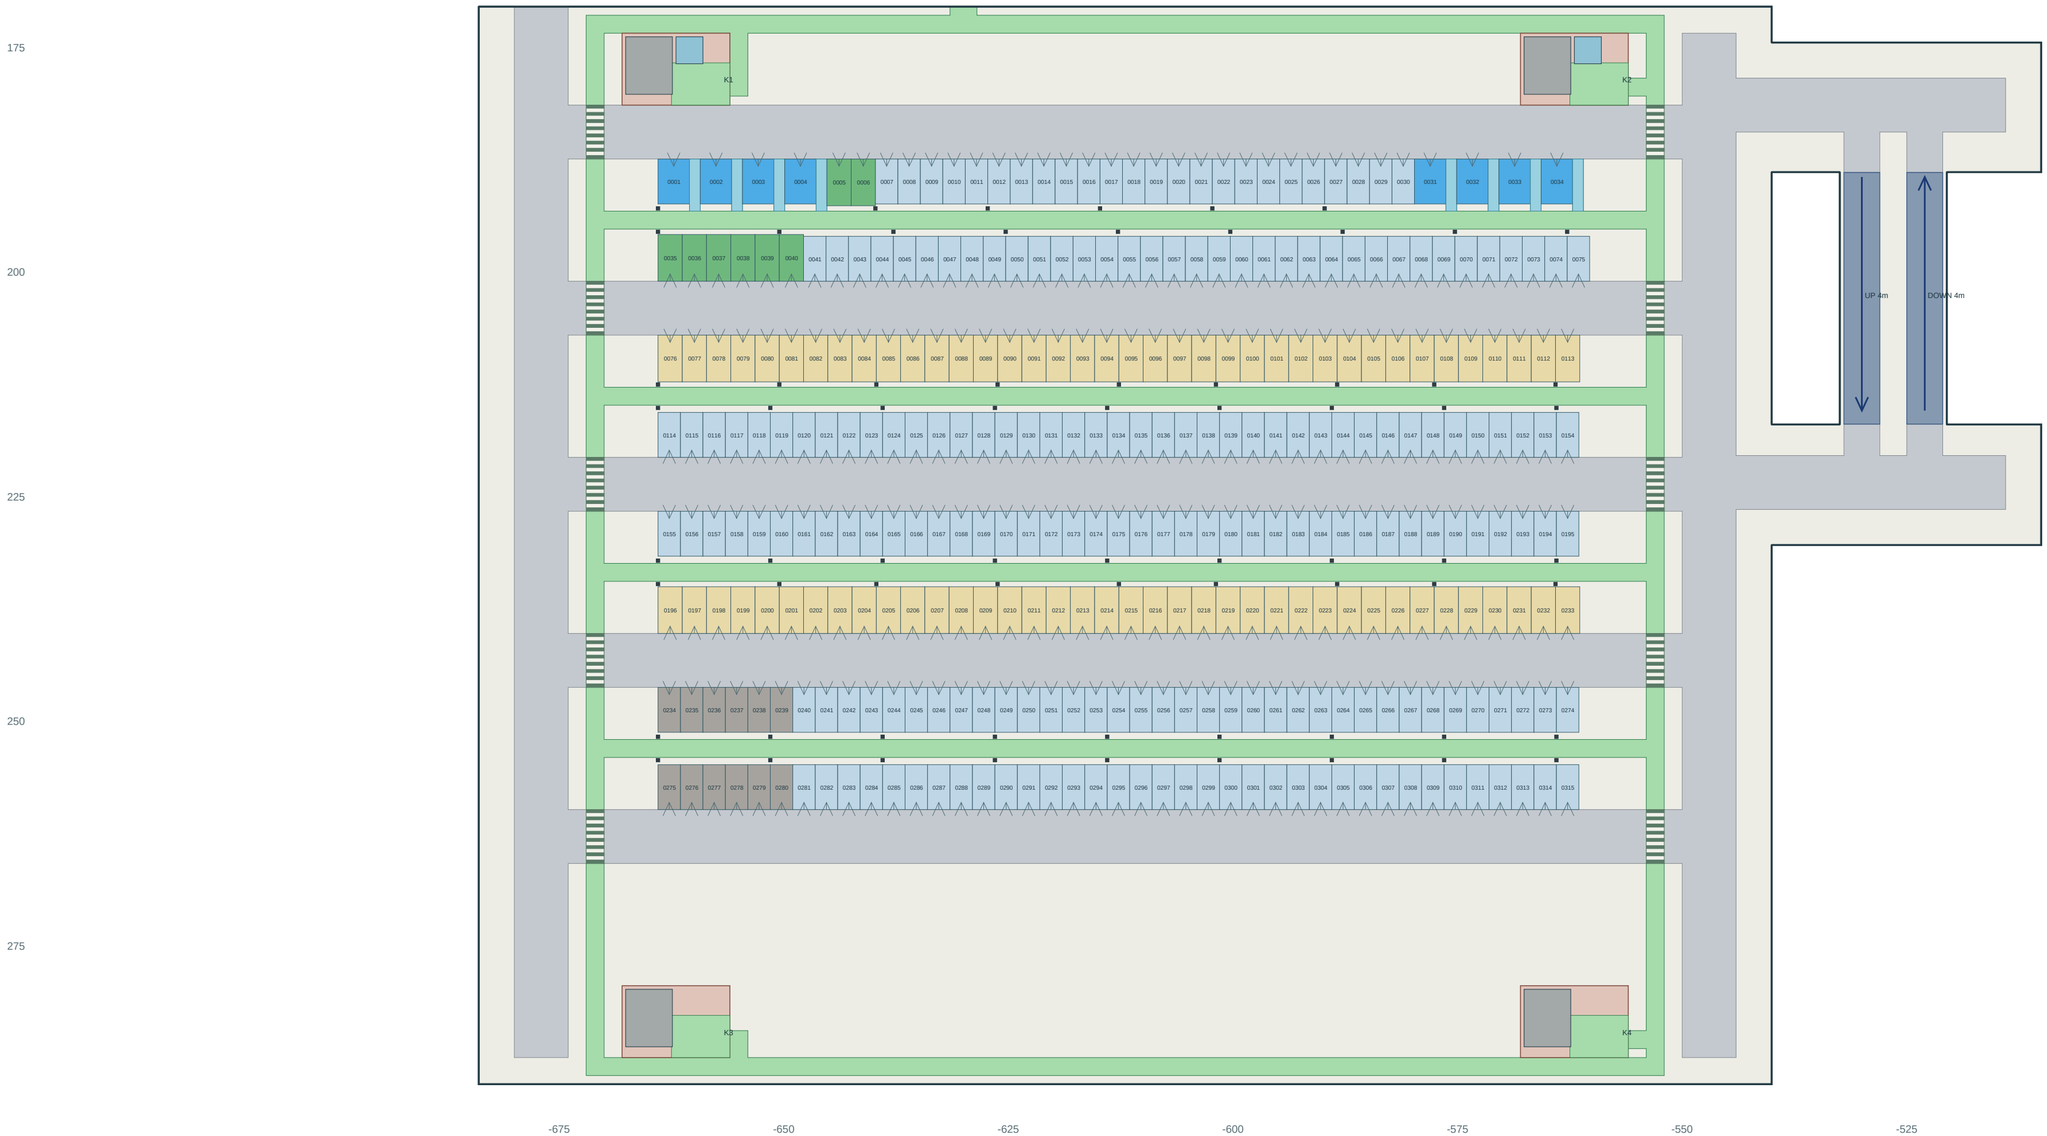

ID prefix: P-B-S-L05- / 4-digit bay labels + prefix = full stall ID

台数：一般211 / ゆとり76 / 身障者用8 / 充電EV8 / 職員12。赤は地上/橋受け口、緑は保護歩道、縞は指定横断歩道。

外周防護/転落防止1.2m。P1高端/P7低端の斜路口は赤茶の防護壁で閉鎖。上階の未接続口は仮設柵を維持し、橋が実際につながるまで開放しない。

4.8×2.0m車両のR6m旋回図形を車路・斜路平場内で検査。個々の駐車の切返しや実車制御を実測した結果ではありません。

B南立体駐車場｜P7 +16.400m / 315台

モールRF高 / ID接頭辞 P-B-S-L06- / 青=一般・黄=ゆとり・水色=身障者・緑=EV・灰=職員

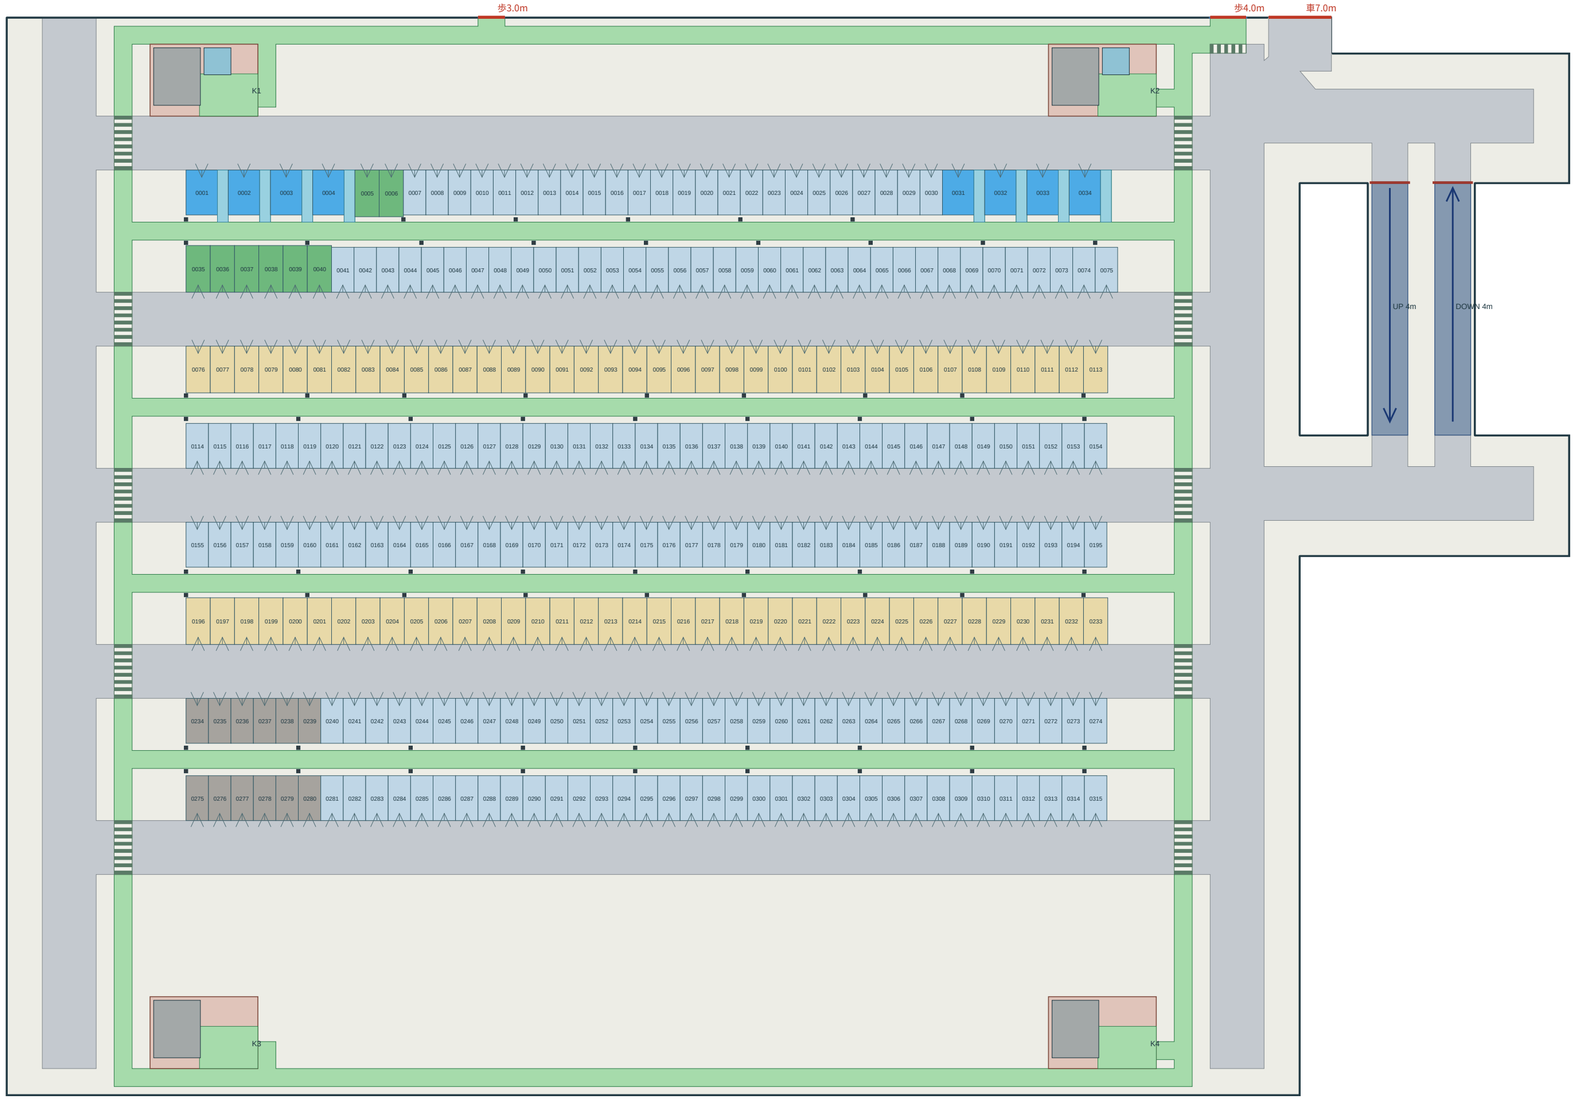

ID prefix: P-B-S-L06- / 4-digit bay labels + prefix = full stall ID

台数：一般211 / ゆとり76 / 身障者用8 / 充電EV8 / 職員12。赤は地上/橋受け口、緑は保護歩道、縞は指定横断歩道。

外周防護/転落防止1.2m。P1高端/P7低端の斜路口は赤茶の防護壁で閉鎖。上階の未接続口は仮設柵を維持し、橋が実際につながるまで開放しない。

4.8×2.0m車両のR6m旋回図形を車路・斜路平場内で検査。個々の駐車の切返しや実車制御を実測した結果ではありません。

B南立体駐車場｜駐車モジュール拡大

標準/ゆとり/身障者側方通路・後方保護歩道・柱・車路・横断歩道とEV/階段前室を拡大。

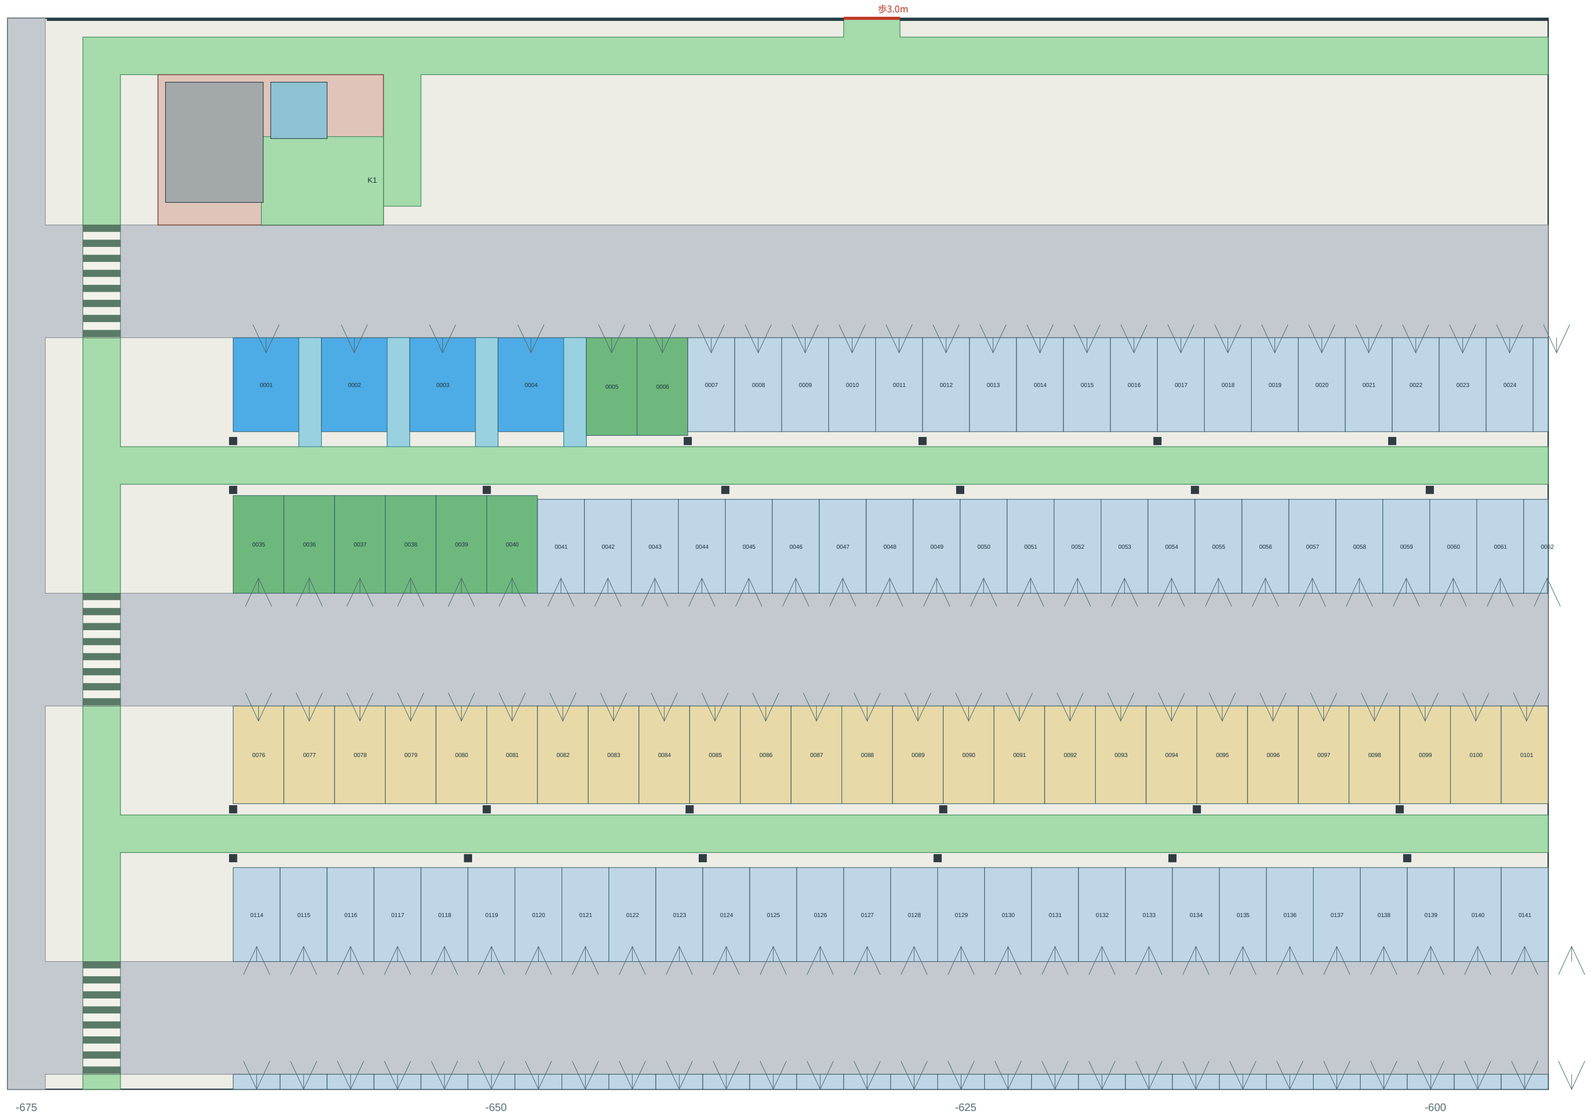

車路6m、後方保護歩道2m。背面サービス帯に0.4m角柱を配置し、駐車ポリゴン・歩道・各マスの後方アクセス線へ食い込まないことを検査。

身障者マス3.5m＋側方1.2m、ゆとりマス2.7m×5.2m。幾何上の位置を具体化した設計値で、構造/バリアフリー適合の認証ではない。

C北平面駐車場｜GROUND +0.000m / 465台

地上平面 / ID接頭辞 P-C-N-L00- / 青=一般・黄=ゆとり・水色=身障者・緑=EV・灰=職員

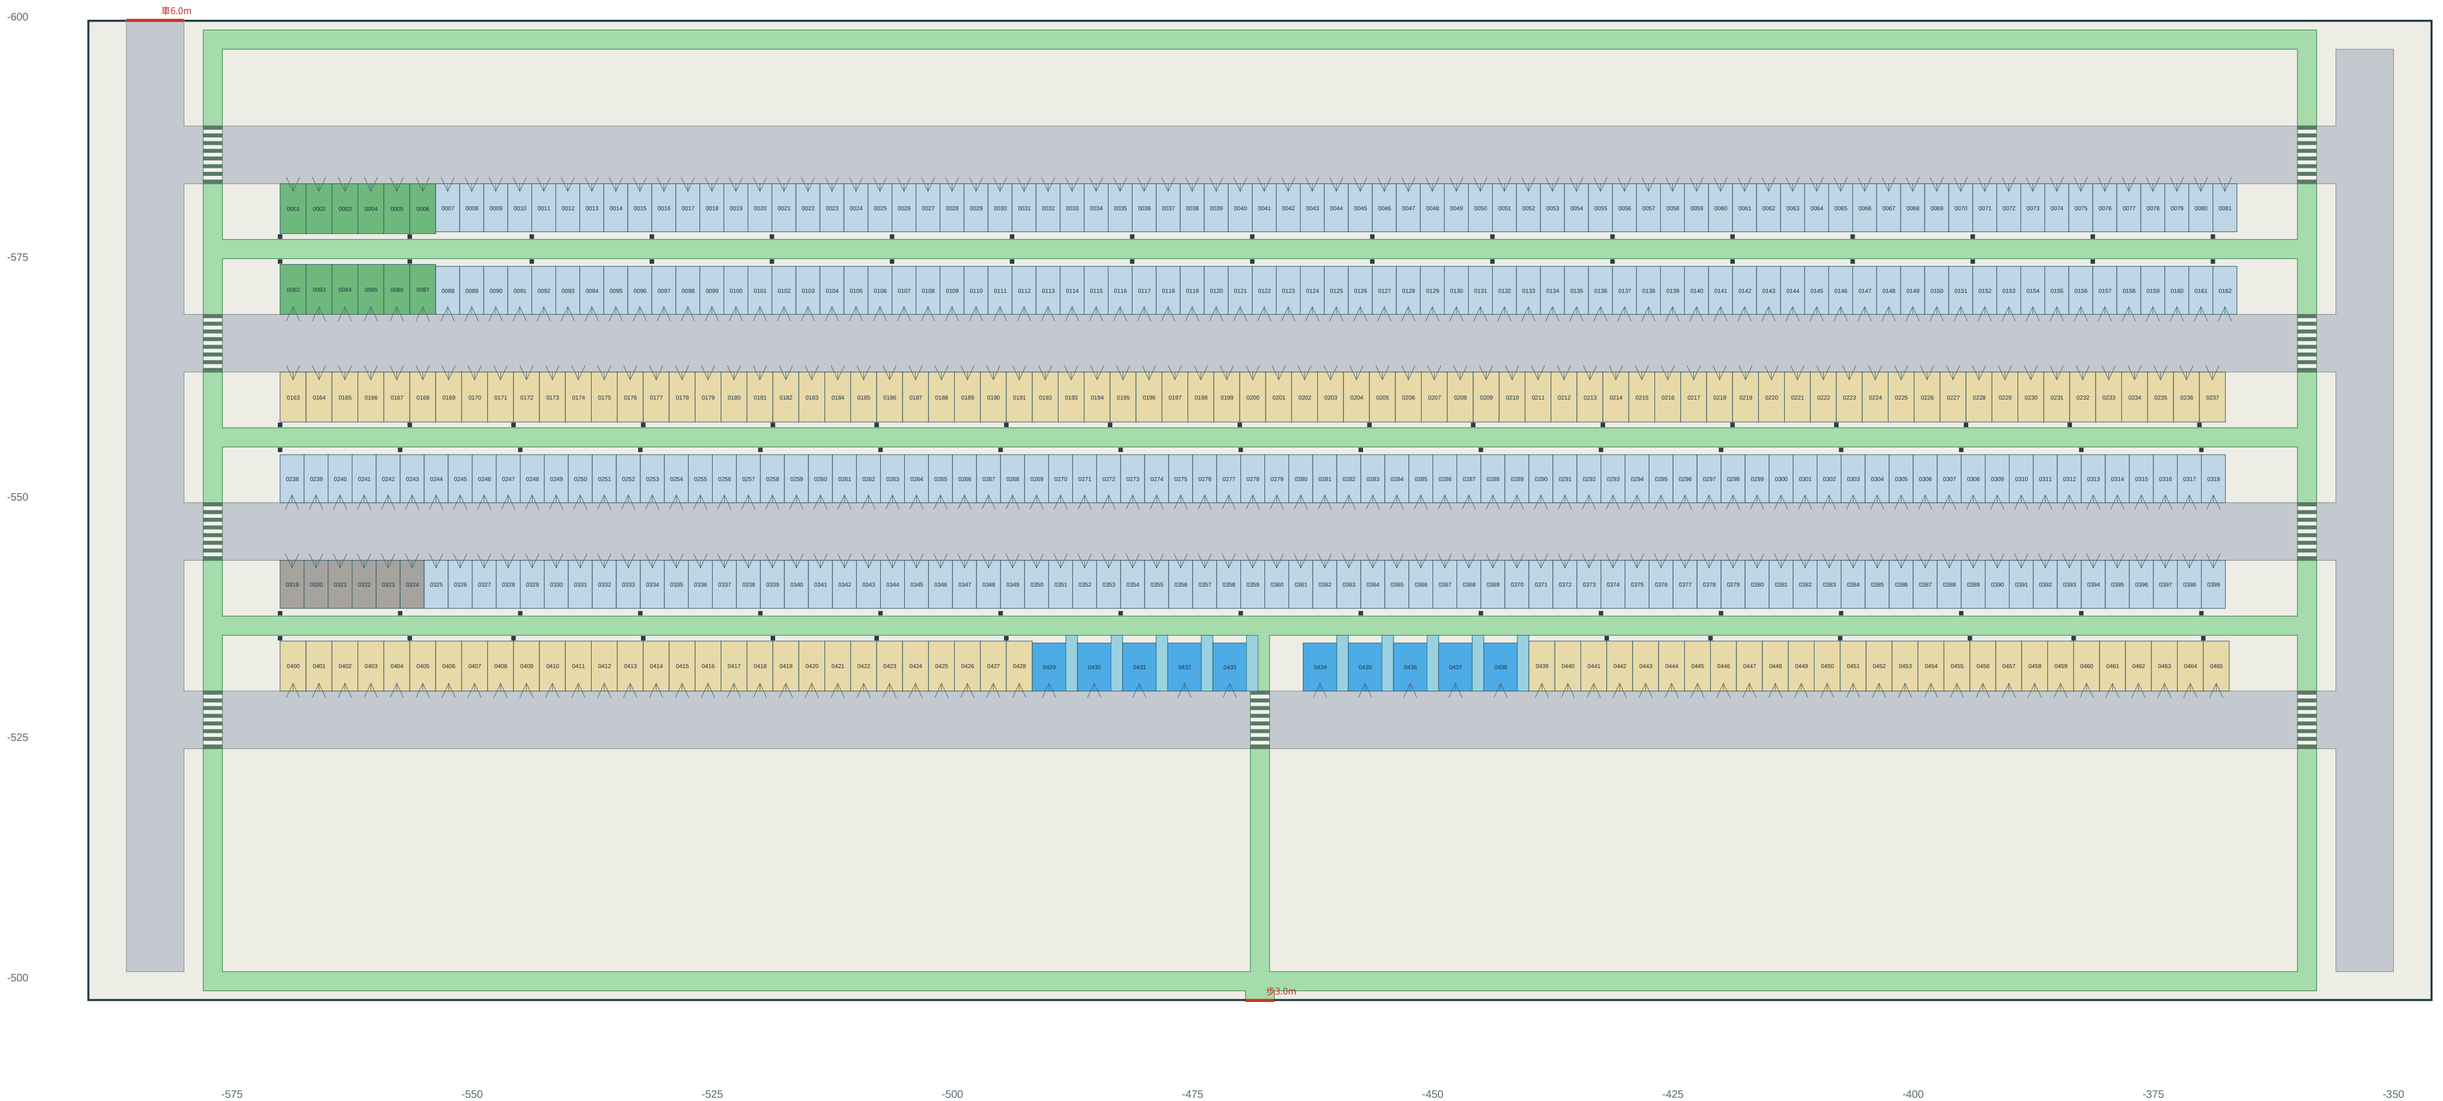

ID prefix: P-C-N-L00- / 4-digit bay labels + prefix = full stall ID

台数：一般306 / ゆとり131 / 身障者用10 / 充電EV12 / 職員6。赤は地上/橋受け口、緑は保護歩道、縞は指定横断歩道。

平面場に不要な階段/EVを置かず、保護歩道で地上出口へ。身障者側方通路と主保護歩道はフラットに接続。

4.8×2.0m車両のR6m旋回図形を車路・斜路平場内で検査。個々の駐車の切返しや実車制御を実測した結果ではありません。

C北平面駐車場｜駐車モジュール拡大

標準/ゆとり/身障者側方通路・後方保護歩道・柱・車路・横断歩道とEV/階段前室を拡大。

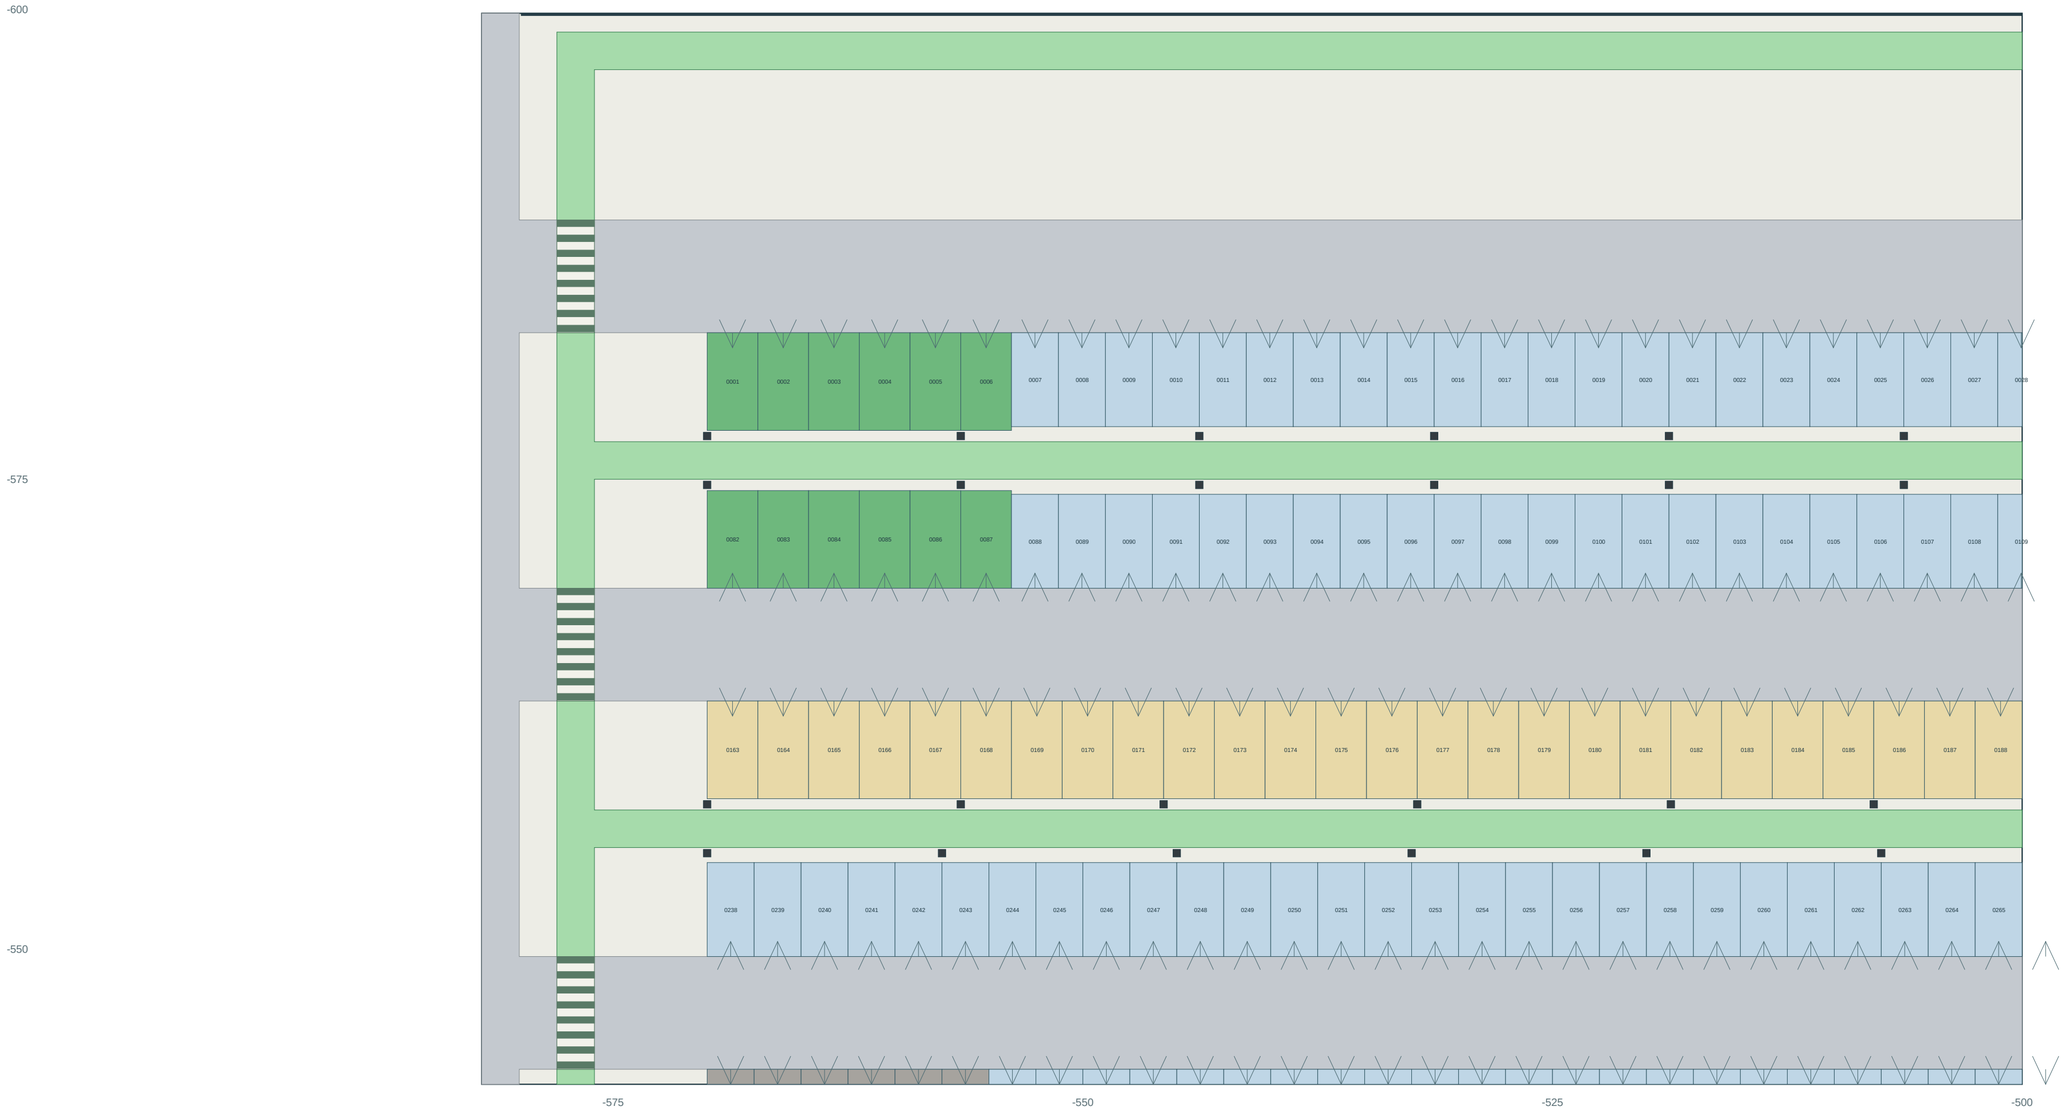

車路6m、後方保護歩道2m。背面サービス帯に0.4m角柱を配置し、駐車ポリゴン・歩道・各マスの後方アクセス線へ食い込まないことを検査。

身障者マス3.5m＋側方1.2m、ゆとりマス2.7m×5.2m。幾何上の位置を具体化した設計値で、構造/バリアフリー適合の認証ではない。

B西平面駐車場｜GROUND +0.000m / 485台

地上平面 / ID接頭辞 P-B-W-L00- / 青=一般・黄=ゆとり・水色=身障者・緑=EV・灰=職員

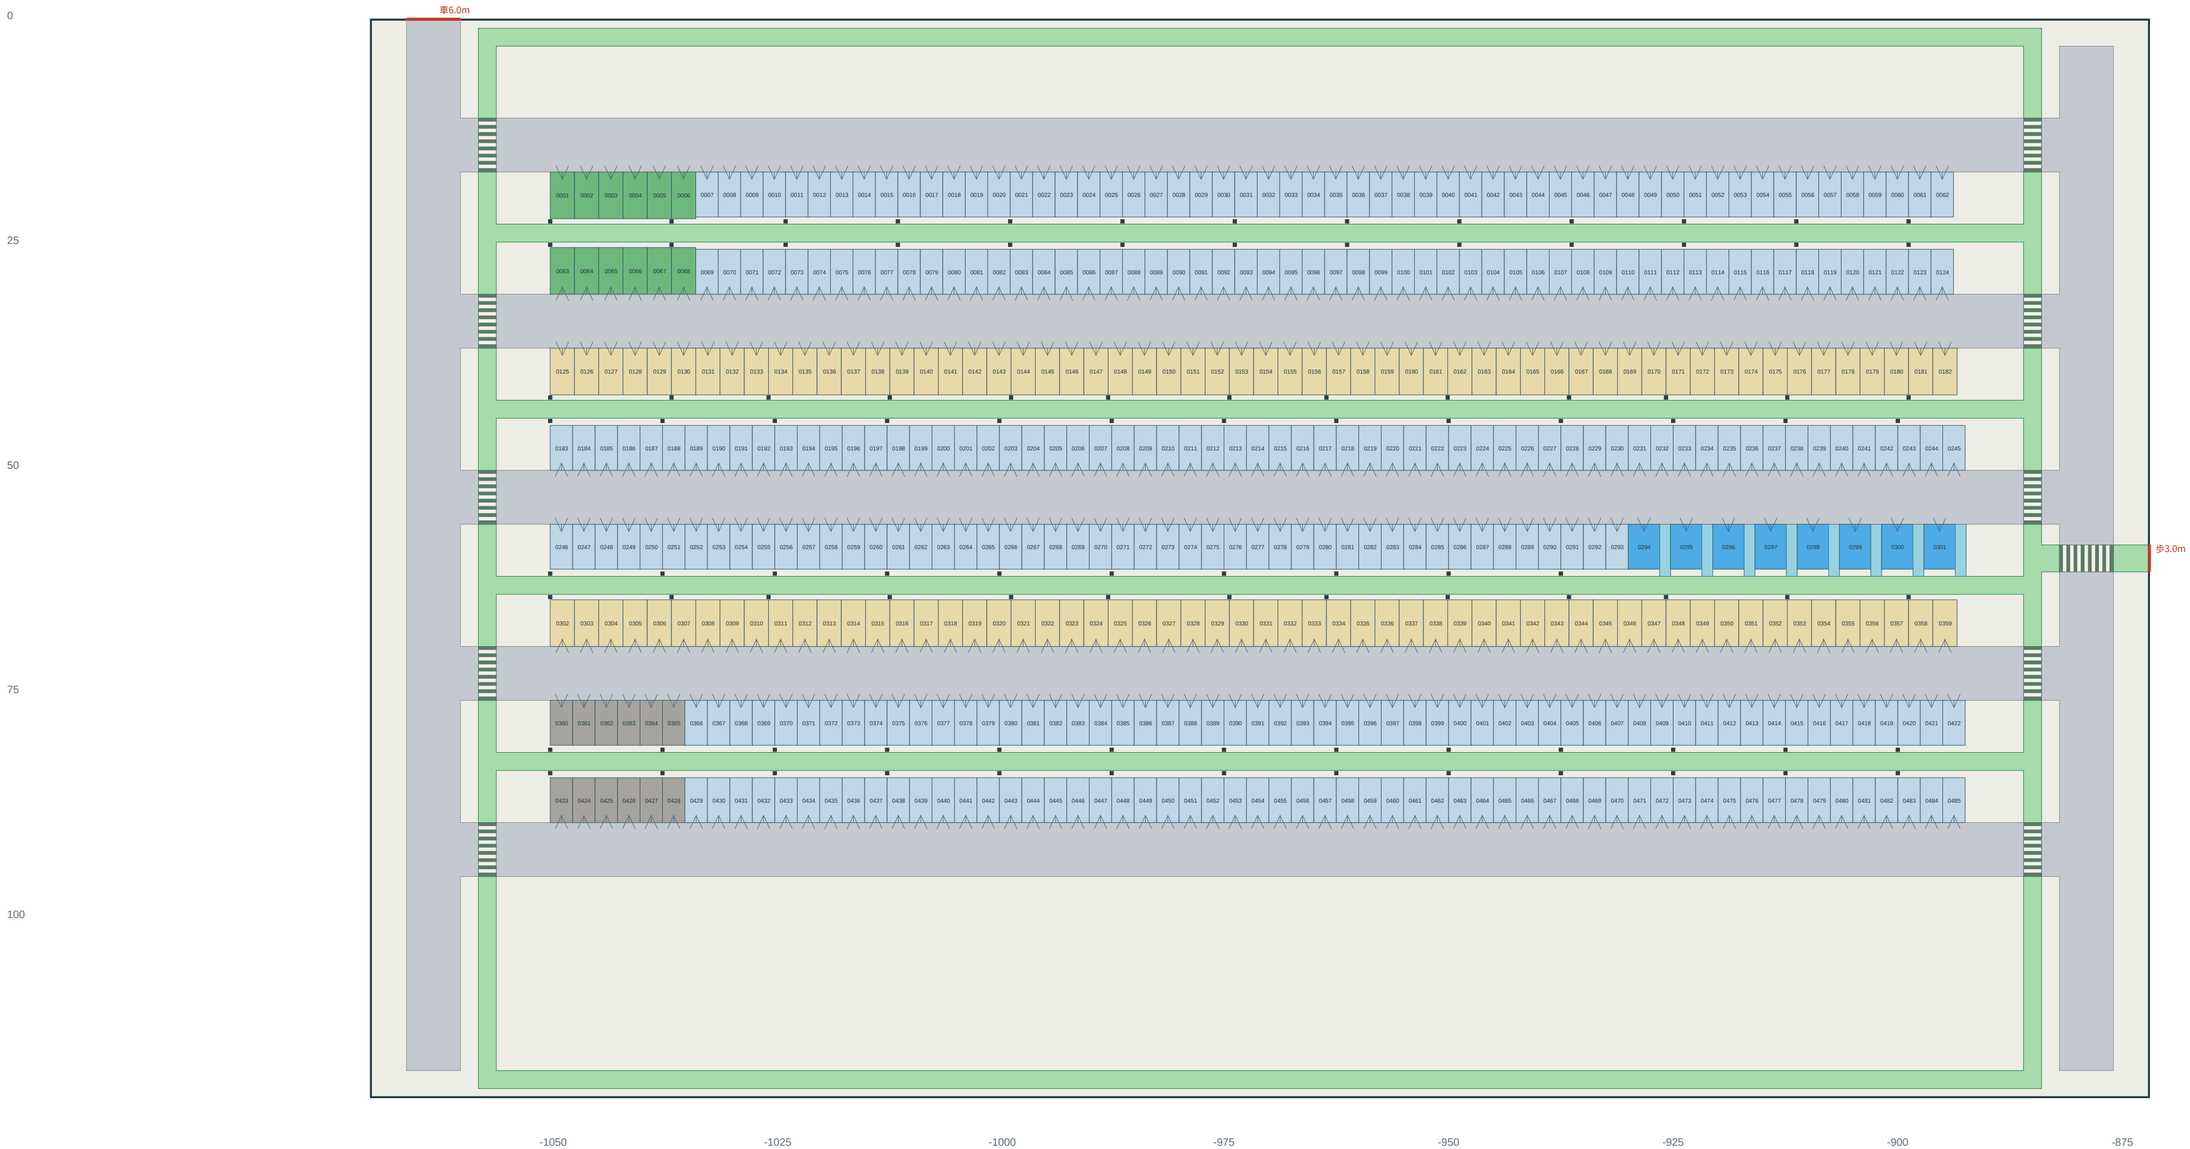

ID prefix: P-B-W-L00- / 4-digit bay labels + prefix = full stall ID

台数：一般337 / ゆとり116 / 身障者用8 / 充電EV12 / 職員12。赤は地上/橋受け口、緑は保護歩道、縞は指定横断歩道。

平面場に不要な階段/EVを置かず、保護歩道で地上出口へ。身障者側方通路と主保護歩道はフラットに接続。

4.8×2.0m車両のR6m旋回図形を車路・斜路平場内で検査。個々の駐車の切返しや実車制御を実測した結果ではありません。

B西平面駐車場｜駐車モジュール拡大

標準/ゆとり/身障者側方通路・後方保護歩道・柱・車路・横断歩道とEV/階段前室を拡大。

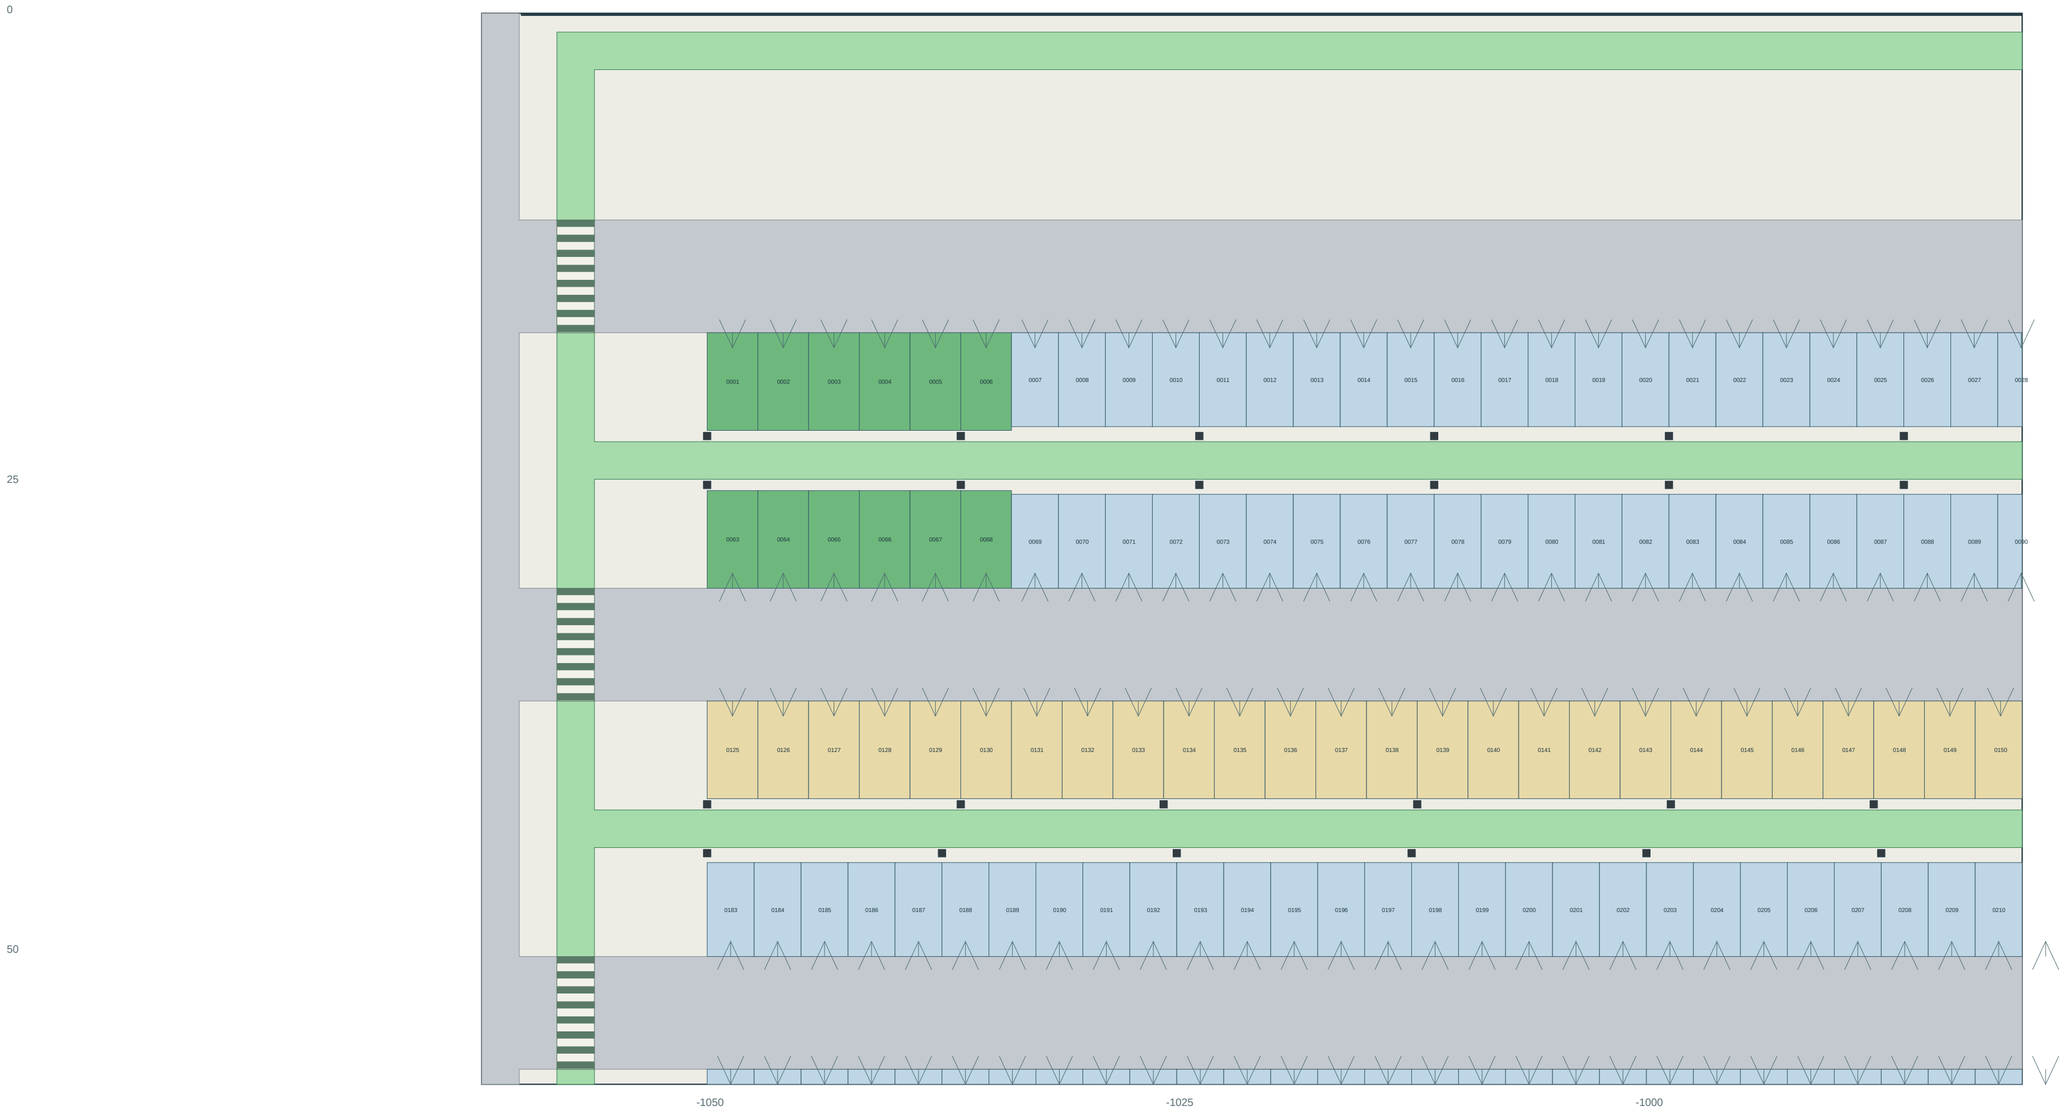

車路6m、後方保護歩道2m。背面サービス帯に0.4m角柱を配置し、駐車ポリゴン・歩道・各マスの後方アクセス線へ食い込まないことを検査。

身障者マス3.5m＋側方1.2m、ゆとりマス2.7m×5.2m。幾何上の位置を具体化した設計値で、構造/バリアフリー適合の認証ではない。

A南平面駐車場｜GROUND +0.000m / 673台

地上平面 / ID接頭辞 P-A-S-L00- / 青=一般・黄=ゆとり・水色=身障者・緑=EV・灰=職員

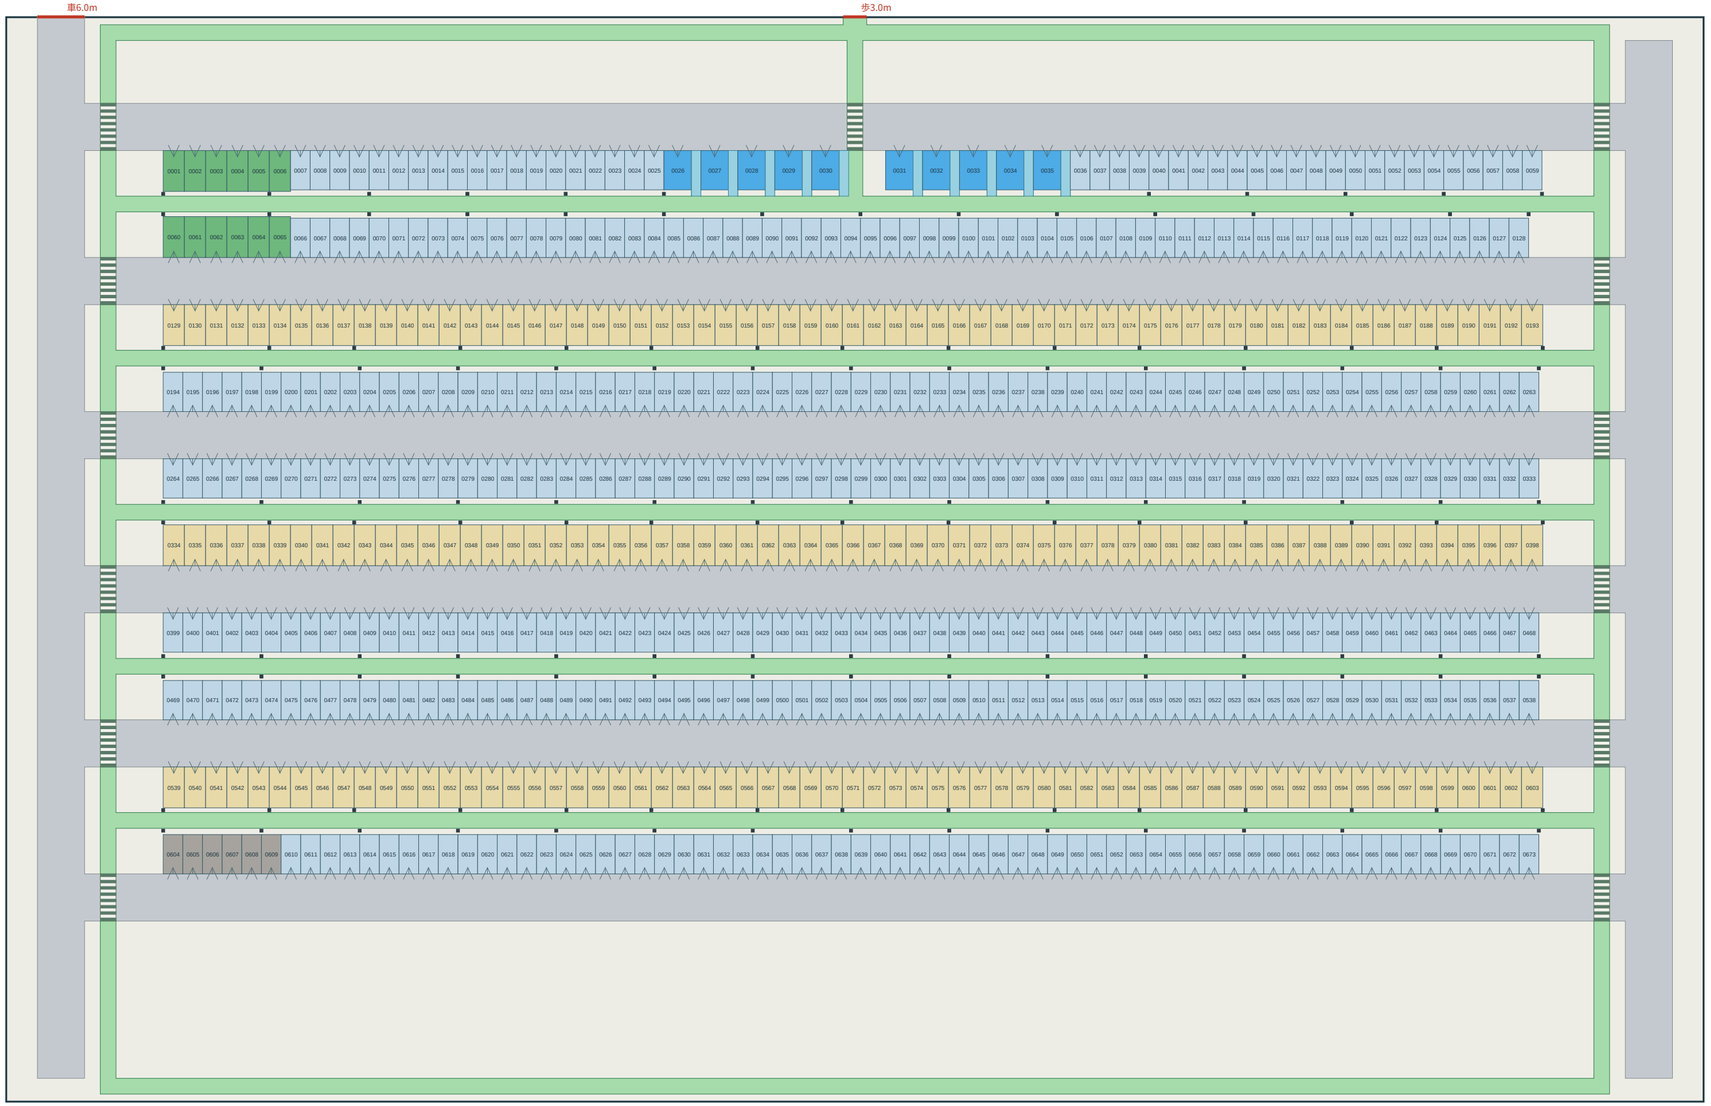

ID prefix: P-A-S-L00- / 4-digit bay labels + prefix = full stall ID

台数：一般450 / ゆとり195 / 身障者用10 / 充電EV12 / 職員6。赤は地上/橋受け口、緑は保護歩道、縞は指定横断歩道。

平面場に不要な階段/EVを置かず、保護歩道で地上出口へ。身障者側方通路と主保護歩道はフラットに接続。

4.8×2.0m車両のR6m旋回図形を車路・斜路平場内で検査。個々の駐車の切返しや実車制御を実測した結果ではありません。

A南平面駐車場｜駐車モジュール拡大

標準/ゆとり/身障者側方通路・後方保護歩道・柱・車路・横断歩道とEV/階段前室を拡大。

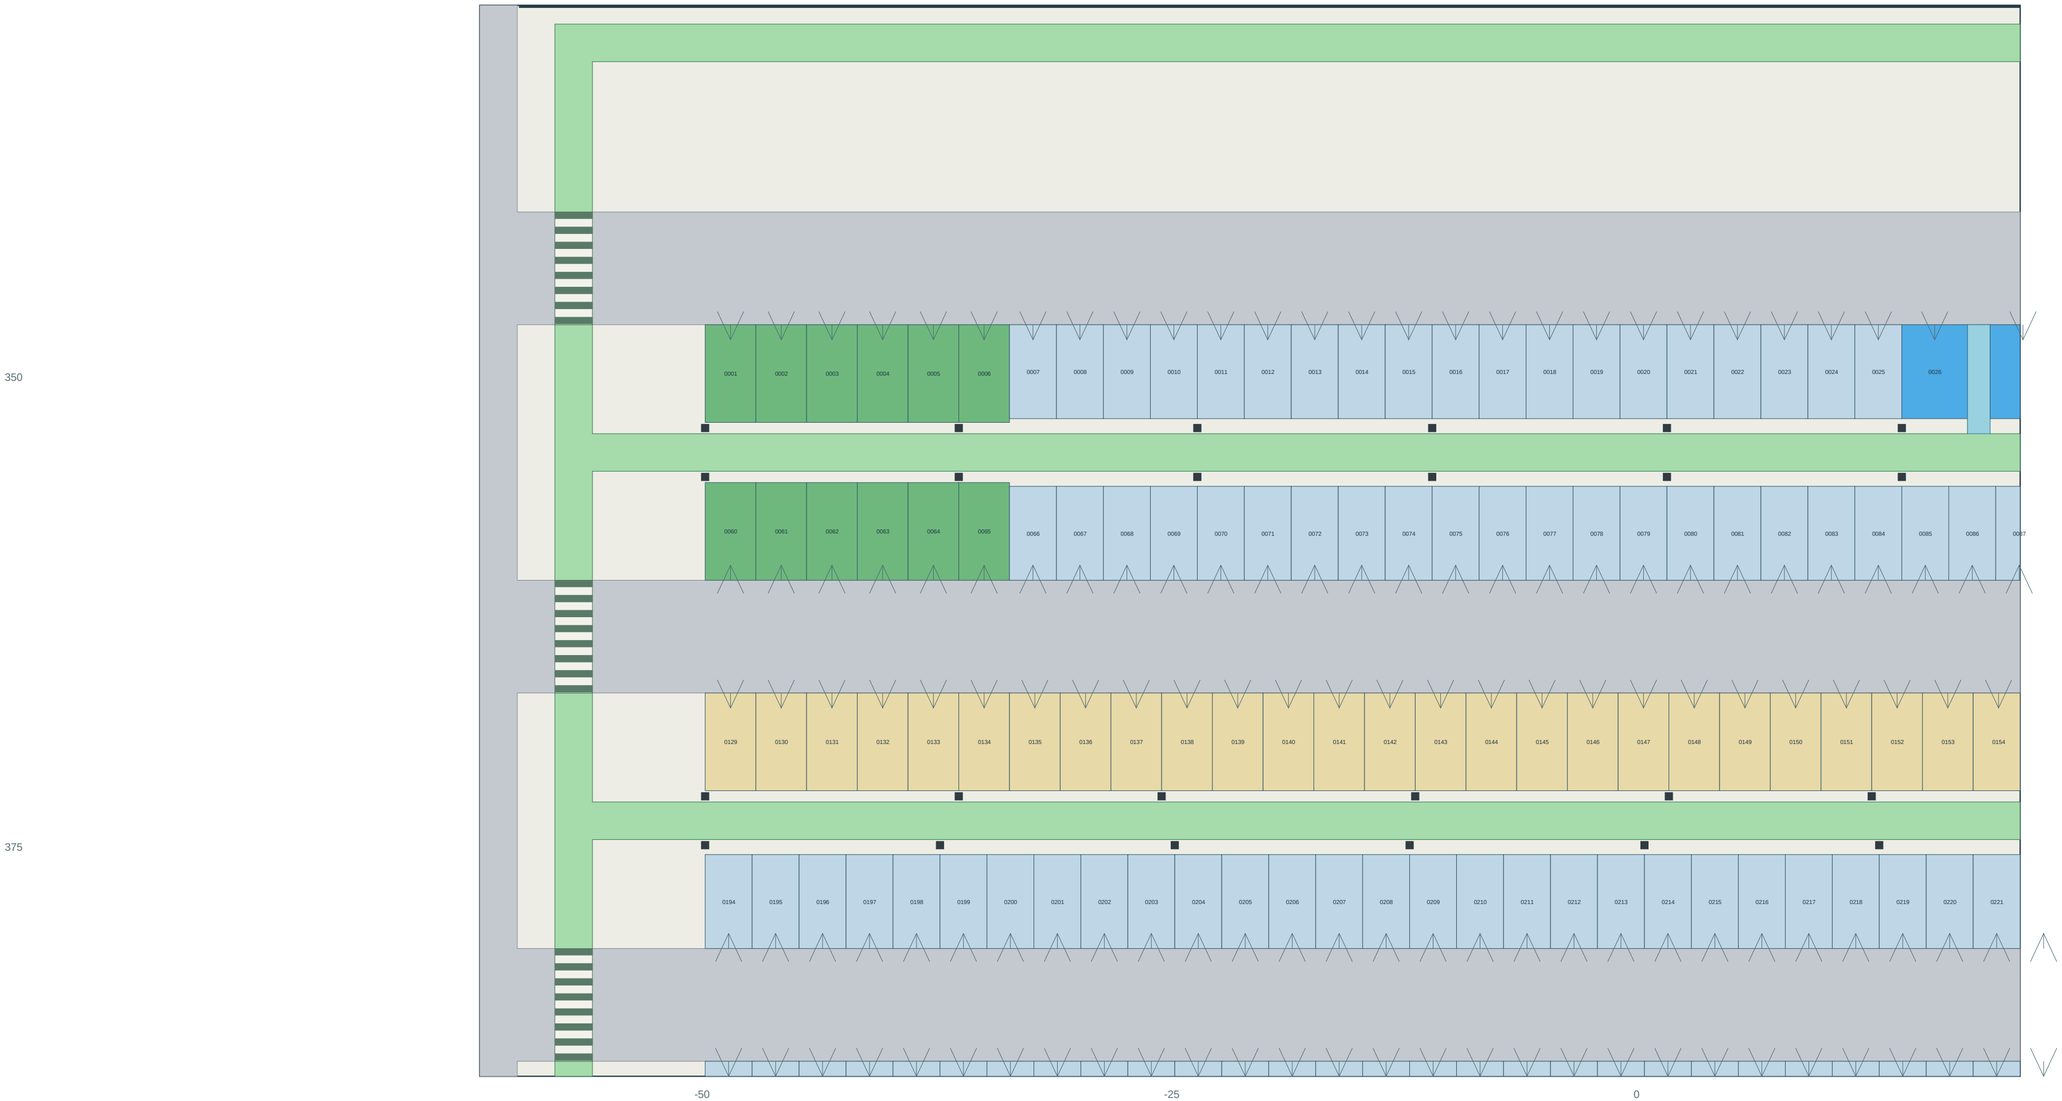

車路6m、後方保護歩道2m。背面サービス帯に0.4m角柱を配置し、駐車ポリゴン・歩道・各マスの後方アクセス線へ食い込まないことを検査。

身障者マス3.5m＋側方1.2m、ゆとりマス2.7m×5.2m。幾何上の位置を具体化した設計値で、構造/バリアフリー適合の認証ではない。

共通寸法｜保護歩道を挟む両面モジュール

車路・駐車・保護歩道を意図的に分離。寸法単位m。

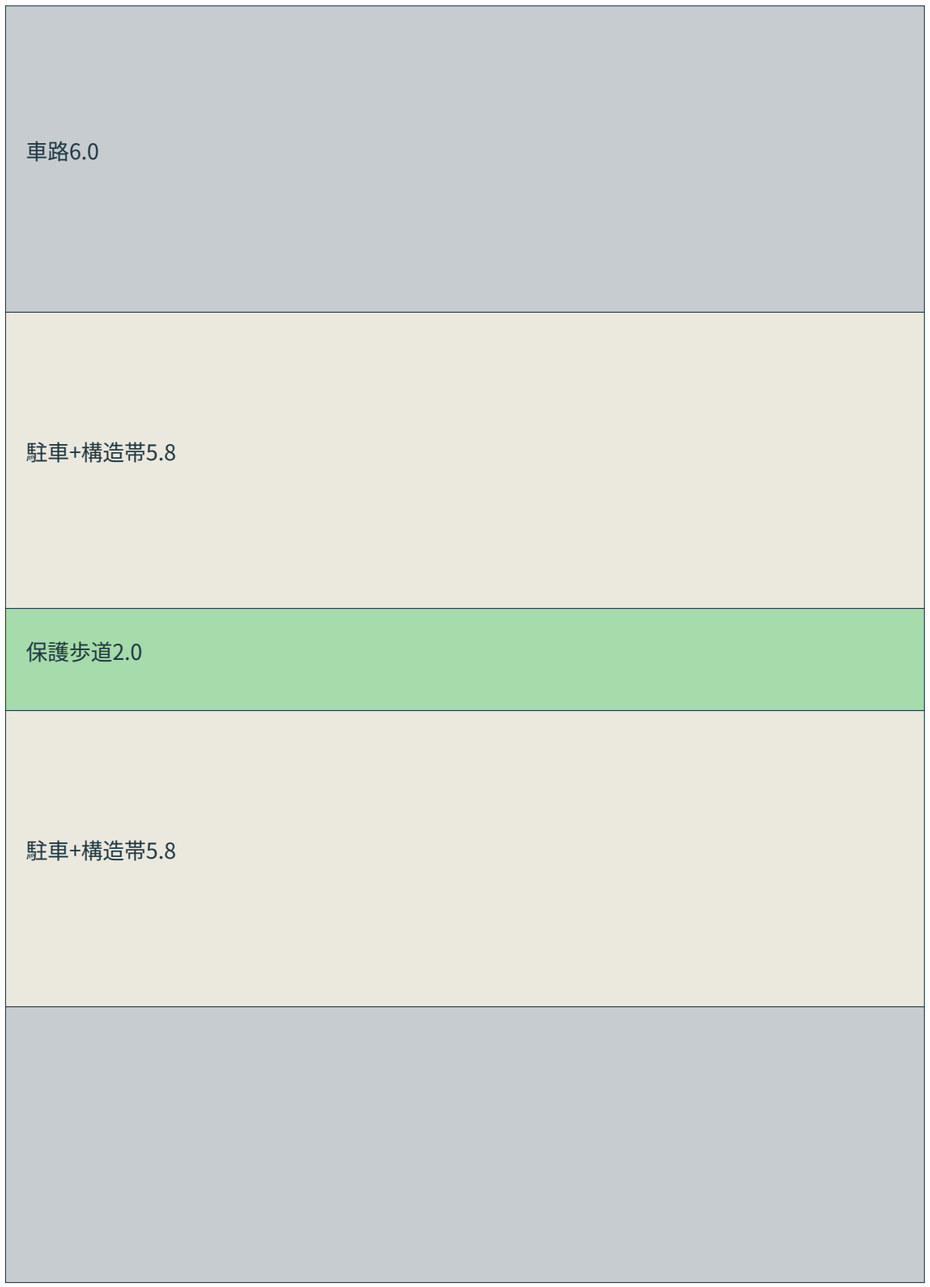

標準マス2.5×5.0m、ゆとり2.7×5.2m。モジュールの駐車側奥行5.8mには、車後方のアクセス/構造柱帯を含む。

柱は0.4m角、奥行方向のサービス帯に置き、マスと主歩道に干渉させない。柱割りと部材/床スパンは概念的な支持配置で構造計算ではない。

側方通路1.2mは身障者マスとは別ポリゴン。歩道2.0mへ連続し、段差は設けない。指定横断部は歩道優先の停止線/低速運用を計画。

各マスの後方接続は図面の線分/距離で検査。駐車中車両の扉や車椅子の実動作、運転者の切返しを再現した検査ではない。

A東立体駐車場｜斜路・平場・旋回の拡大

UP/DOWN各4m一方向。低速車路と斜路の合流は停止/譲り標示を設計。大型配送車は通さない。

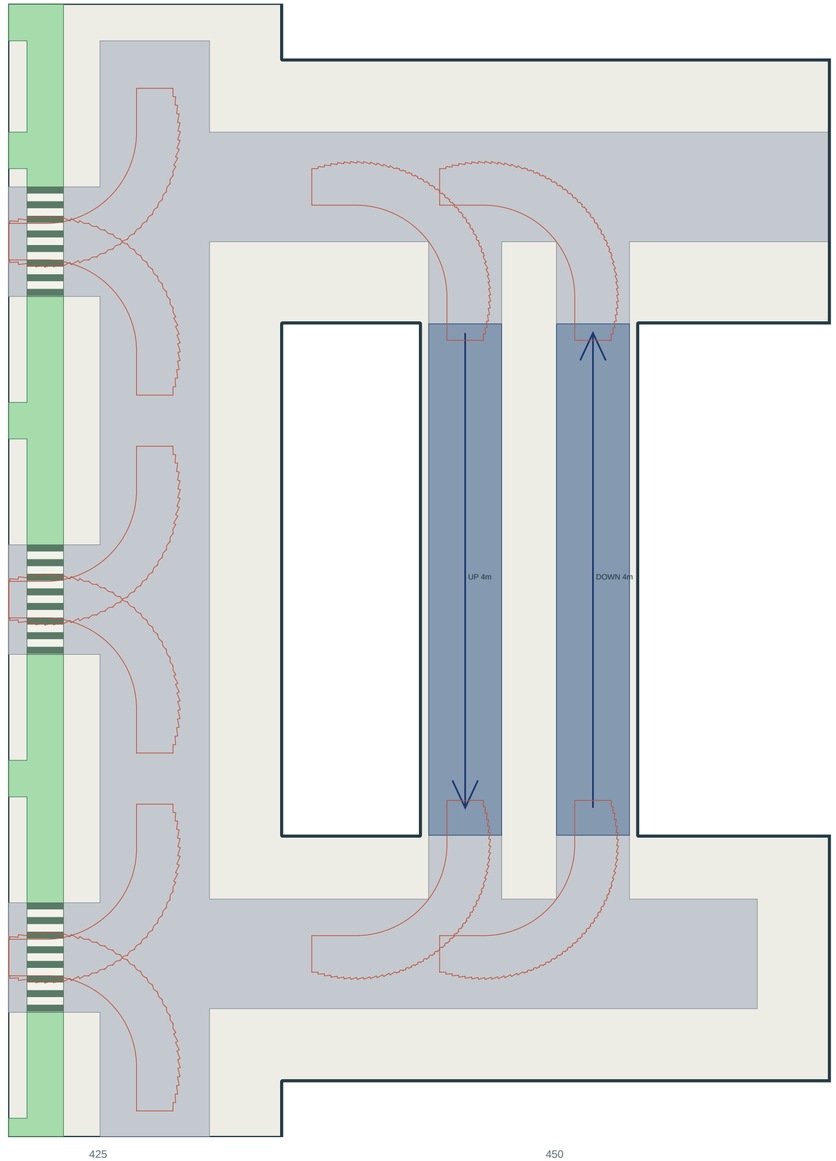

下端平場10.5m、上端9.5m。斜路の水平ラン28m（緩和3m＋直線22m＋緩和3m）、段の高差は2.675〜2.775m。

実際の断面は縦曲線をサンプリングし、平場で勾配0、直線区間で10.7〜11.1%。架空の段差ワープで上下接続していない。

赤線は4.8×2.0m設計車のR6m車体包絡のサンプル。マス列端の旋回と斜路平場の右左折が通る図形内に収まることを検査。

斜路両側は4m内法を侵さない位置に1.1m防護壁。平場・車路と共用歩道を交差させず、歩行者を斜路へ誘導しない。

UP到着側の上端から、次段のUP低端へは同じ階の車路を回って移動する。階を飛ばす接続ではなく、上下別レーンの連続系統。

A東立体駐車場｜全6階間の斜路断面

断面は横方向と鉛直方向を別倍率で示す。実寸・勾配は数値を参照。段差のない縦接続を確認する設計図。

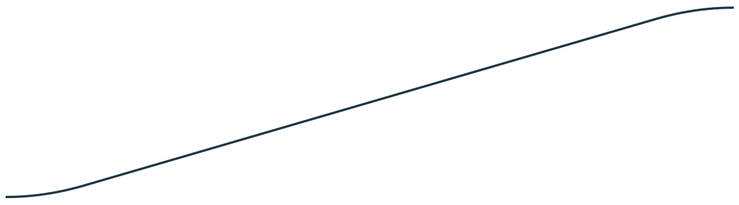

P1→P2 +2.750m / 11.0%

下端10.5m平場 / 緩和3+直線22+緩和3m / 上端9.5m平場

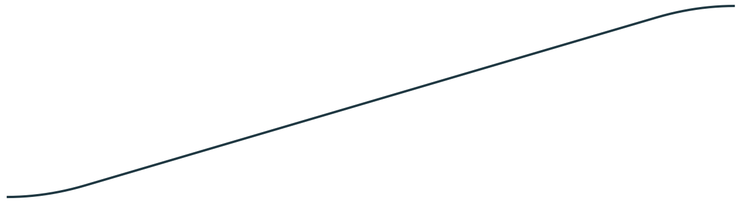

P2→P3 +2.775m / 11.1%

下端10.5m平場 / 緩和3+直線22+緩和3m / 上端9.5m平場

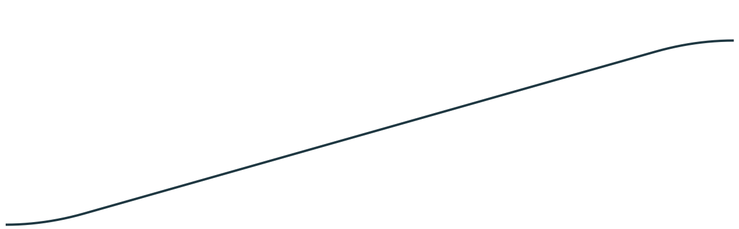

P3→P4 +2.675m / 10.7%

下端10.5m平場 / 緩和3+直線22+緩和3m / 上端9.5m平場

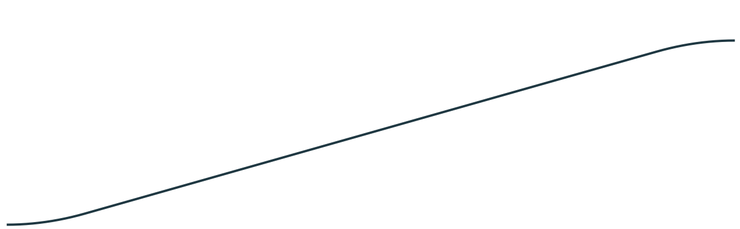

P4→P5 +2.675m / 10.7%

下端10.5m平場 / 緩和3+直線22+緩和3m / 上端9.5m平場

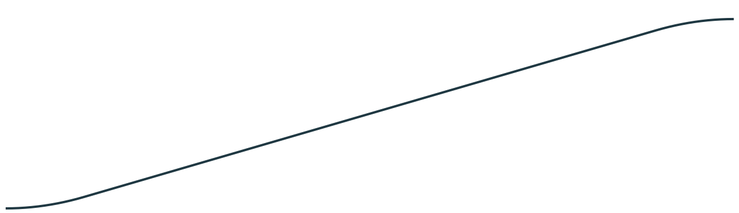

P5→P6 +2.750m / 11.0%

下端10.5m平場 / 緩和3+直線22+緩和3m / 上端9.5m平場

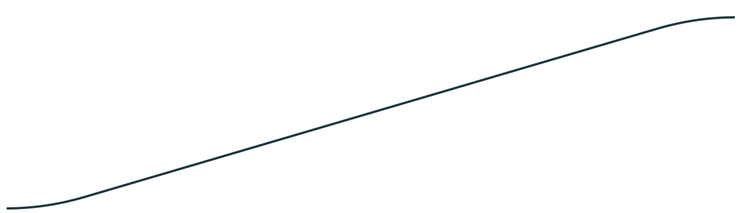

P6→P7 +2.775m / 11.1%

下端10.5m平場 / 緩和3+直線22+緩和3m / 上端9.5m平場

B南立体駐車場｜斜路・平場・旋回の拡大

UP/DOWN各4m一方向。低速車路と斜路の合流は停止/譲り標示を設計。大型配送車は通さない。

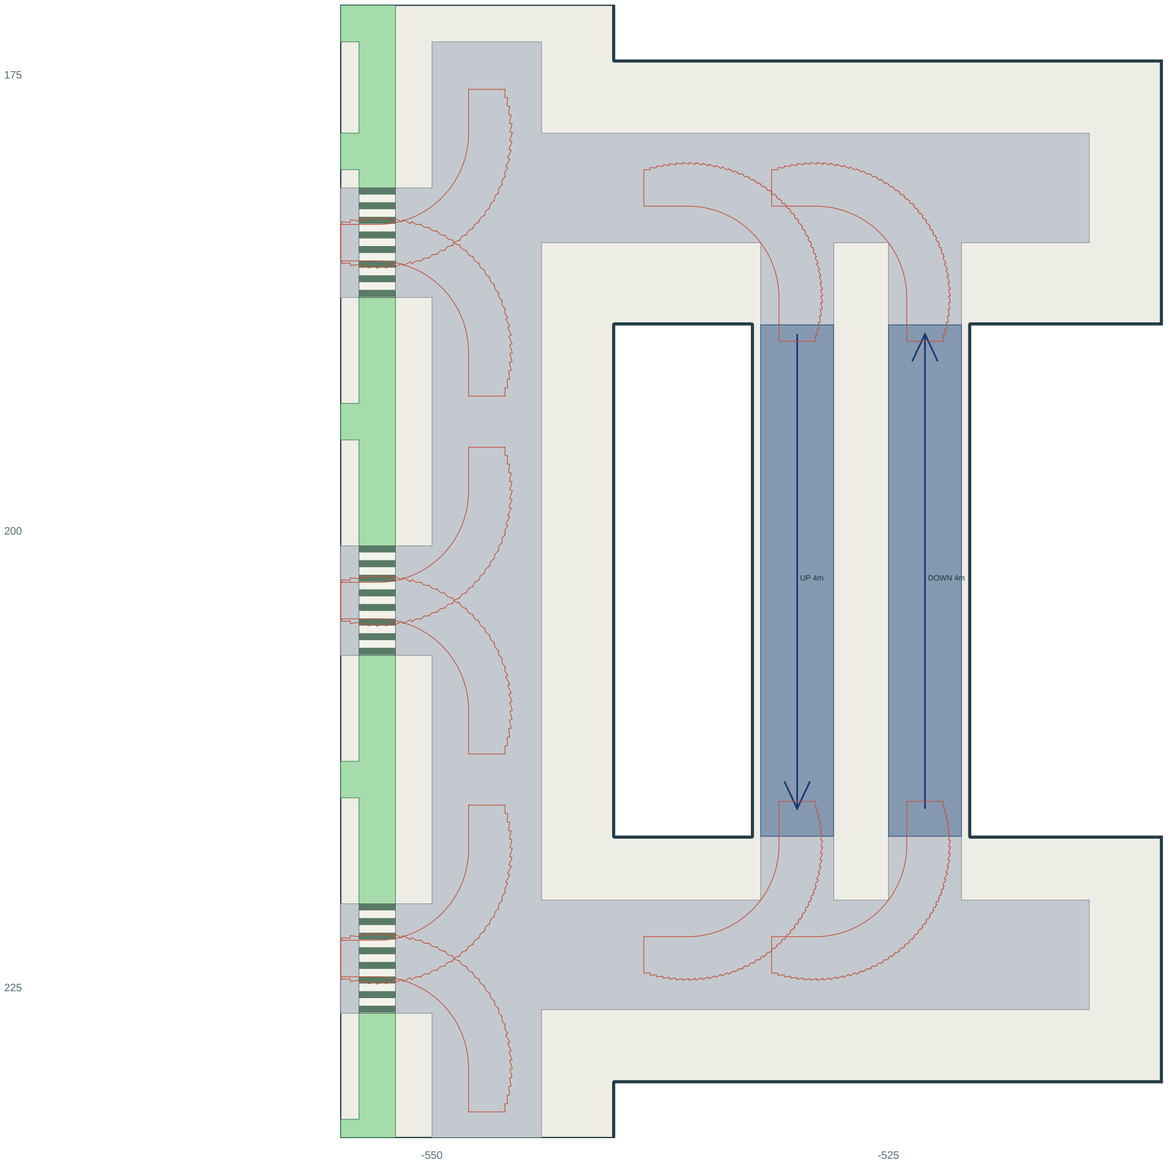

下端平場10.5m、上端9.5m。斜路の水平ラン28m（緩和3m＋直線22m＋緩和3m）、段の高差は2.675〜2.775m。

実際の断面は縦曲線をサンプリングし、平場で勾配0、直線区間で10.7〜11.1%。架空の段差ワープで上下接続していない。

赤線は4.8×2.0m設計車のR6m車体包絡のサンプル。マス列端の旋回と斜路平場の右左折が通る図形内に収まることを検査。

斜路両側は4m内法を侵さない位置に1.1m防護壁。平場・車路と共用歩道を交差させず、歩行者を斜路へ誘導しない。

UP到着側の上端から、次段のUP低端へは同じ階の車路を回って移動する。階を飛ばす接続ではなく、上下別レーンの連続系統。

B南立体駐車場｜全6階間の斜路断面

断面は横方向と鉛直方向を別倍率で示す。実寸・勾配は数値を参照。段差のない縦接続を確認する設計図。

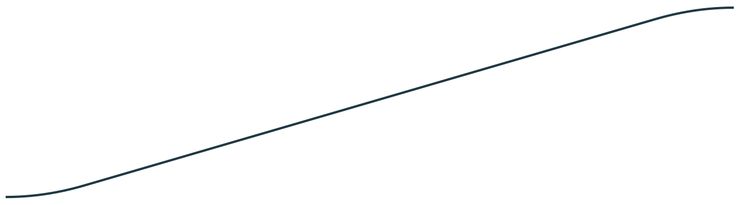

P1→P2 +2.750m / 11.0%

下端10.5m平場 / 緩和3+直線22+緩和3m / 上端9.5m平場

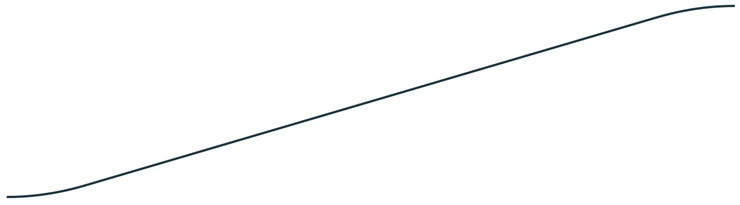

P2→P3 +2.775m / 11.1%

下端10.5m平場 / 緩和3+直線22+緩和3m / 上端9.5m平場

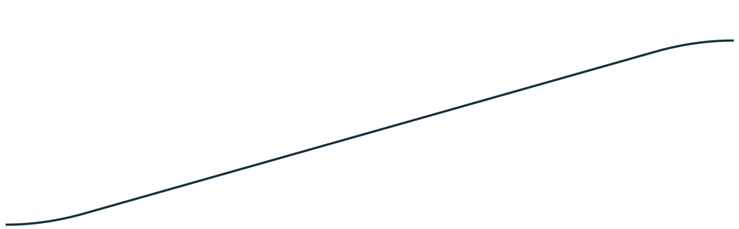

P3→P4 +2.675m / 10.7%

下端10.5m平場 / 緩和3+直線22+緩和3m / 上端9.5m平場

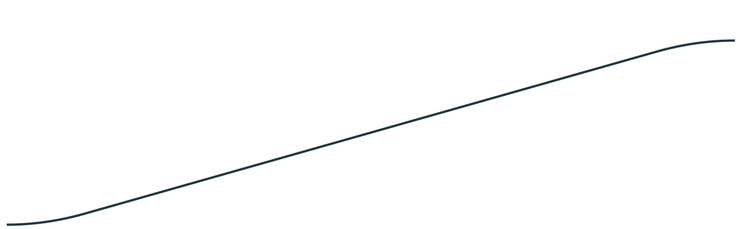

P4→P5 +2.675m / 10.7%

下端10.5m平場 / 緩和3+直線22+緩和3m / 上端9.5m平場

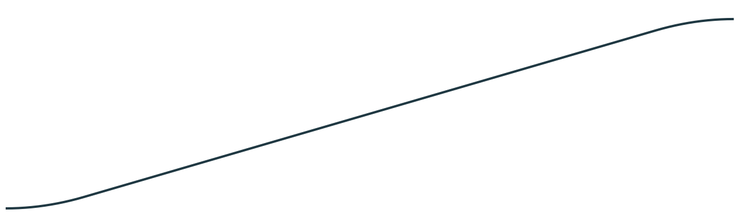

P5→P6 +2.750m / 11.0%

下端10.5m平場 / 緩和3+直線22+緩和3m / 上端9.5m平場

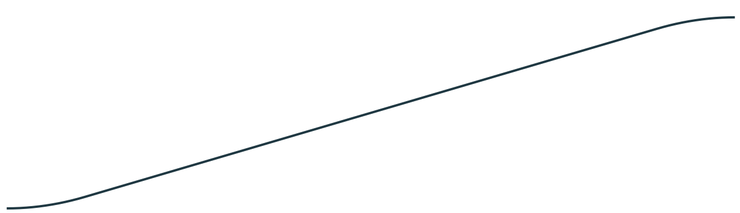

P6→P7 +2.775m / 11.1%

下端10.5m平場 / 緩和3+直線22+緩和3m / 上端9.5m平場

立体駐車場｜4階段核・2EV核・前室の詳細

前側2核はEV併設、後側2核は階段。平面駐車場に不要な昇降核は設けない。

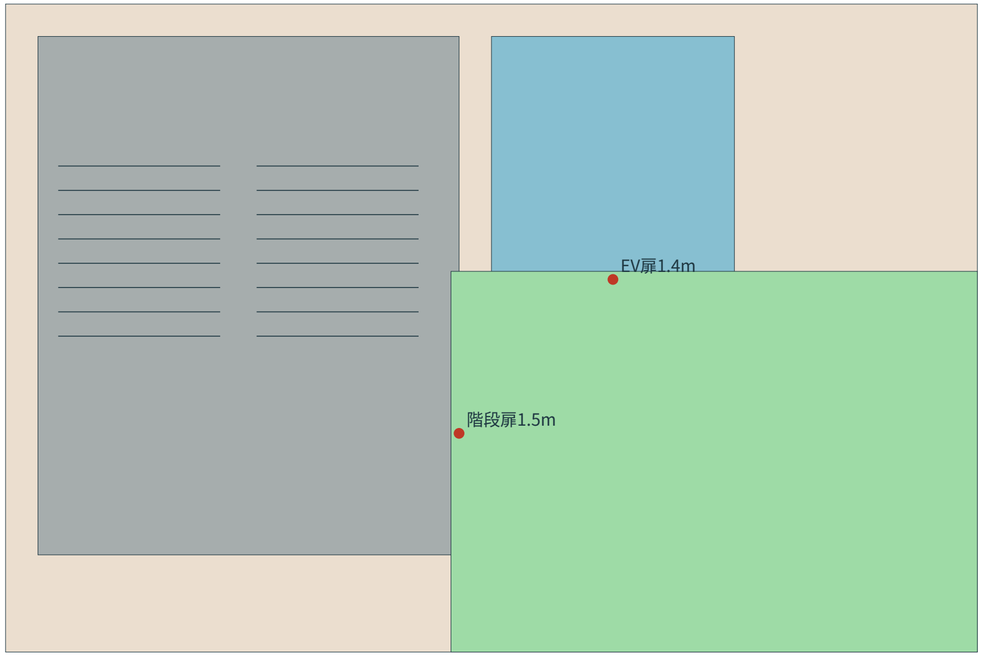

前側：階段＋EV＋前室

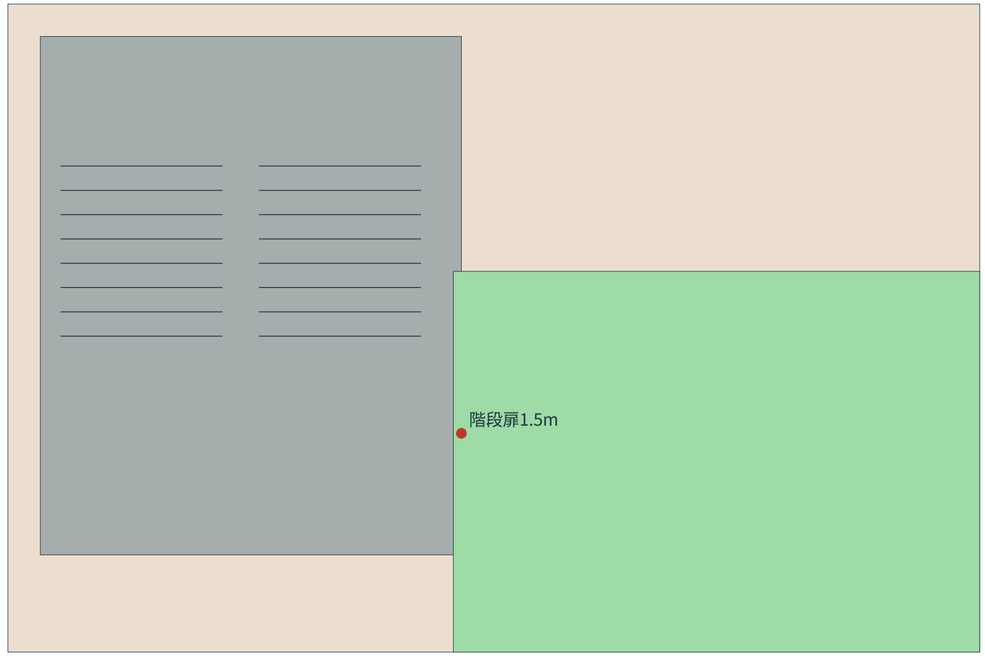

後側：階段＋前室

階段は2.0m内法×2フライト、各段16蹴上げ（8＋8）、踏面0.30m、踊場1.5m以上。最大蹴上0.17344m。各核で全7段を接続。

EVシャフト3×3m、扉1.4m、前室は保護歩道へ接続。車路の中へ直接降りず、階段を横切るロビー短絡も作らない。

EV実機・地震/火災/避難性能、階段の梁下、扉・敷居の実コリジョンは未検証。

各段の高さ・制限高・車歩の系統

段の高さはモールに合わせ、奇数の中間段に無理なモール連絡橋を追加しない。

高さ：0.000／2.750／5.525／8.200／10.875／13.625／16.400m。屋上も車マスを実際に配置し、未接続の外周開口は防護柵で閉じる。

構造床厚0.30m・設備帯0.15mを仮定した最小クリアランスは2.225m。車両制限高は2.0mとして入口・分岐に表示する設計。実際の梁/設備/構造計算で減少する場合は高さ/段構成の再検討が必要。

これは無梁床構成を仮定したゲーム用計画値。荷重・柱スパン・耐震・防火を検証済みとせず、構造/設備の詳細が確定する前に実建物やゲーム物理の完成扱いにしない。

車は専用UP/DOWNで全7段へ、歩行者は保護歩道→前室→階段/EV→地上出口へ接続。共用の車線上を歩行者通路として丸ごと兼用せず、指定横断部だけを例外にする。

モール橋はP3/P5/P7高の歩行受け口。B南P1には新B館地下へのスロープ受け口、P7にはB RF車橋受け口を別に設ける。橋/外部斜路の本体はrootの統合資料へ。

B南｜G0地下連絡口・RF車橋と歩行橋の分離

北東の受け口はG0/RFだけ。他の中間段へ外部車口を開けない。

P1 +0.000m

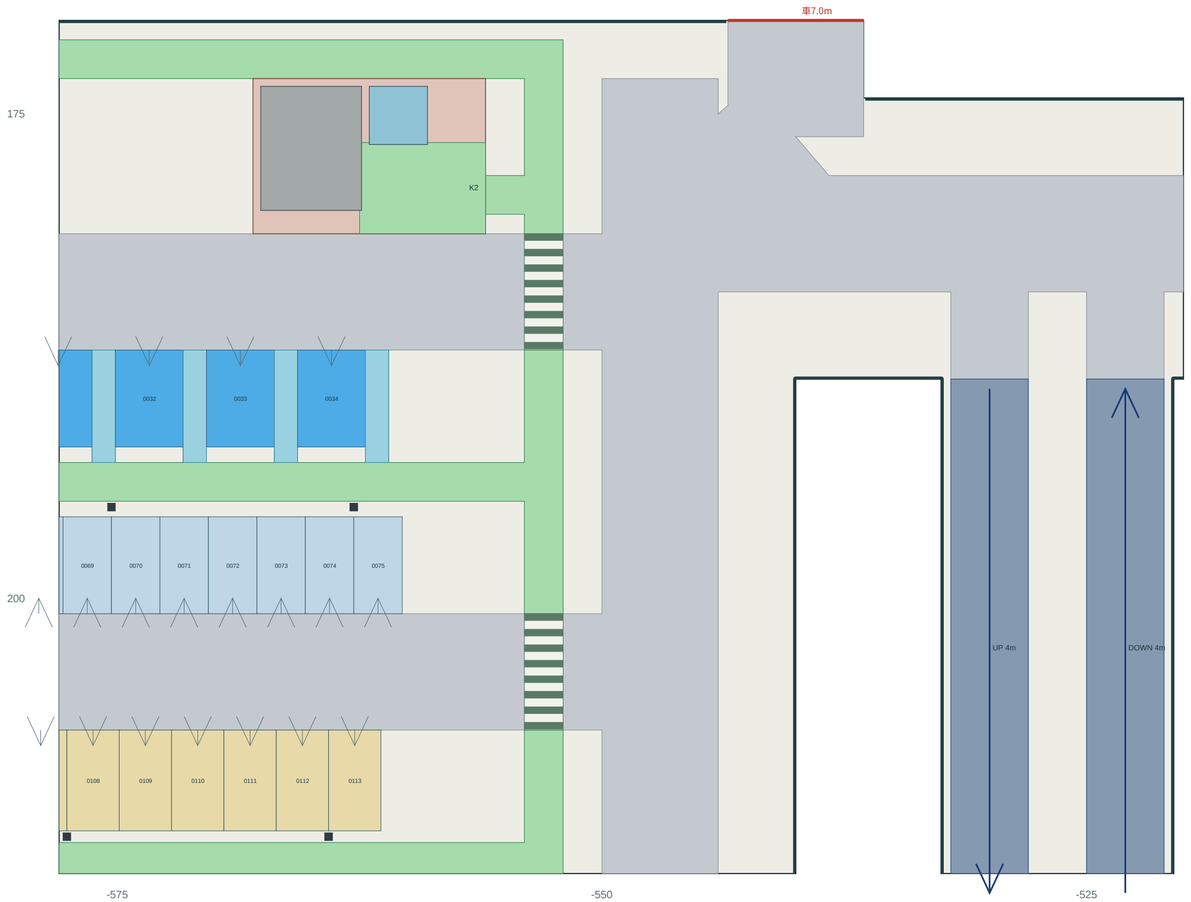

P7 +16.400m

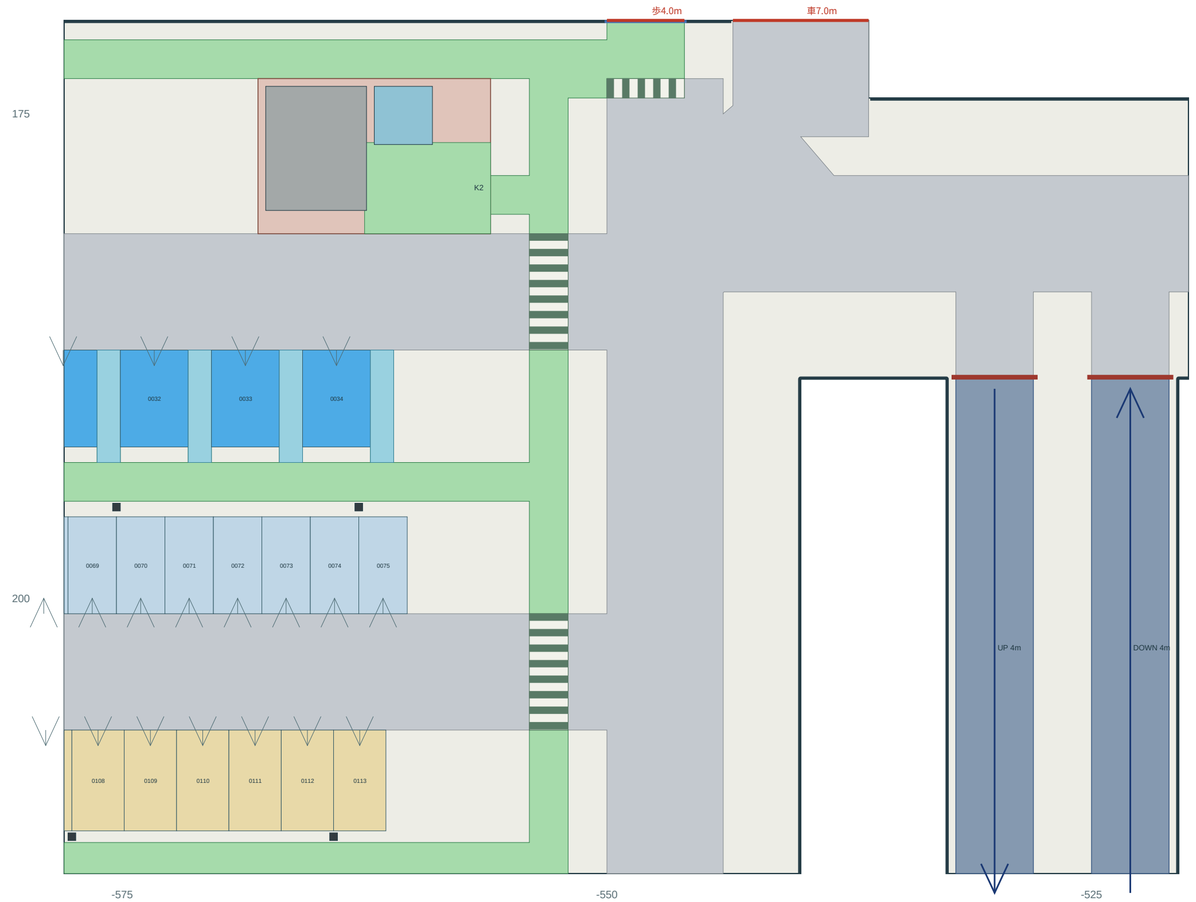

車口 World(-540,170)・幅7m北向き。RF歩行口(-548,170)・幅4m北向きは、車口と平面で離隔し保護歩道へ接続。

主体の東角からはみ出す部分に明示的な受入平場を追加し、幅全体を床で支持。車/歩のアプローチが重ならないことを検査。

G0の車口はrootの新B1スロープへ、RFはB新屋上車橋へ。G0主車口(-677,170)と地上歩行口(-630,170)は維持。外側の道路/橋/スロープはroot担当。

接続受け口一覧｜root敷地ネットワークとの境界

World X/Z m、向きは施設から外へ。モール内部やB館v4.1の既存座標は変更しない。

P-A-E-VEH-G	vehicle	L0 +0.000m	[465, 31]	6.0m / [1, 0]
P-A-E-PED-G	pedestrian	L0 +0.000m	[315, 100]	3.0m / [-1, 0]
P-A-E-PED-L2	pedestrian_bridge_receiver	L2 +5.525m	[315, 100]	3.0m / [-1, 0]
P-A-E-PED-L4	pedestrian_bridge_receiver	L4 +10.875m	[315, 100]	3.0m / [-1, 0]
P-A-E-PED-L6	pedestrian_bridge_receiver	L6 +16.400m	[315, 100]	3.0m / [-1, 0]
P-B-S-VEH-G	vehicle	L0 +0.000m	[-677, 170]	6.0m / [0, -1]
P-B-S-PED-G	pedestrian	L0 +0.000m	[-630, 170]	3.0m / [0, -1]
P-B-S-PED-L2	pedestrian_bridge_receiver	L2 +5.525m	[-630, 170]	3.0m / [0, -1]
P-B-S-PED-L4	pedestrian_bridge_receiver	L4 +10.875m	[-630, 170]	3.0m / [0, -1]
P-B-S-PED-L6	pedestrian_bridge_receiver	L6 +16.400m	[-630, 170]	3.0m / [0, -1]
P-B-S-VEH-B1-G0	vehicle_basement_ramp_receiver	L0 +0.000m	[-540, 170]	7.0m / [0, -1]
P-B-S-PED-RF-NEAR-B	pedestrian_bridge_receiver	L6 +16.400m	[-548, 170]	4.0m / [0, -1]
P-B-S-VEH-RF	vehicle_bridge_receiver	L6 +16.400m	[-540, 170]	7.0m / [0, -1]
P-C-N-VEH-G	vehicle	L0 +0.000m	[-583, -600]	6.0m / [0, -1]
P-C-N-PED-G	pedestrian	L0 +0.000m	[-468, -498]	3.0m / [0, 1]
P-B-W-VEH-G	vehicle	L0 +0.000m	[-1063, 0]	6.0m / [0, -1]
P-B-W-PED-G	pedestrian	L0 +0.000m	[-872, 60]	3.0m / [1, 0]
P-A-S-VEH-G	vehicle	L0 +0.000m	[-63, 330]	6.0m / [0, -1]
P-A-S-PED-G	pedestrian	L0 +0.000m	[38, 330]	3.0m / [0, -1]

全段台数表｜描画マスと一致する実数

全17面。用途内訳CSV/JSONとマス台帳を同梱。

施設 / 段	高さm	一般	ゆとり	身障者	EV	職員	合計
P-A-E L0	0.000	226	116	7	8	6	363
P-A-E L1	2.750	226	116	7	8	6	363
P-A-E L2	5.525	226	116	7	8	6	363
P-A-E L3	8.200	226	116	7	8	6	363
P-A-E L4	10.875	226	116	7	8	6	363
P-A-E L5	13.625	226	116	7	8	6	363
P-A-E L6	16.400	226	116	7	8	6	363
P-B-S L0	0.000	211	76	8	8	12	315
P-B-S L1	2.750	211	76	8	8	12	315
P-B-S L2	5.525	211	76	8	8	12	315
P-B-S L3	8.200	211	76	8	8	12	315
P-B-S L4	10.875	211	76	8	8	12	315
P-B-S L5	13.625	211	76	8	8	12	315
P-B-S L6	16.400	211	76	8	8	12	315
P-C-N L0	0.000	306	131	10	12	6	465
P-B-W L0	0.000	337	116	8	12	12	485
P-A-S L0	0.000	450	195	10	12	6	673

図面検査と未検証事項

図面上の静的幾何と接続を確認。実車試験・ゲーム内走行/実歩行ではない。

生成時の図面検査44,815件、不合格0。全6,369台の車路前面接続・後方歩道接続、柱/開口/車路との非交差、重複マス、保護歩道と車路の横断例外、各段車路/歩道の連結、階段/EV入口、斜路平場、RF/G0受入の全幅支持を確認。

旋回検査は4.8×2.0mの設計車体をR6mの軌跡でサンプルした2D図形。列末端と斜路平場を対象とし、隣接車両がいる各駐車の切返し、車両軸距/操舵/勾配変化の実動作、背の高い配送車を検証済みとはしない。

歩行接続は保護路・前室・階段/EVポータルの幾何連結。駐車中車両のドア開閉、車椅子の操作や交通誘導を含む実測ではない。出口までの移動距離・運用容量・混雑は今後の評価対象。

未検証：構造荷重・柱スパン/接合・地盤/排水、法定設備・消防/避難、受電/充電容量、ガードの実物衝突、梁下/設備、外部道路の信号/見通しと実車走行。

ゲーム本体、NPC、スキャン、セーブ、既存館は変更していない。root全体図との接続確認後に図面を提出し、承認前に実装を始めない。