
V30 | B / 1F | NORMAL LAYOUT


Design review / not structural certification. World X = map X + 429; world Z = map Z - 46.

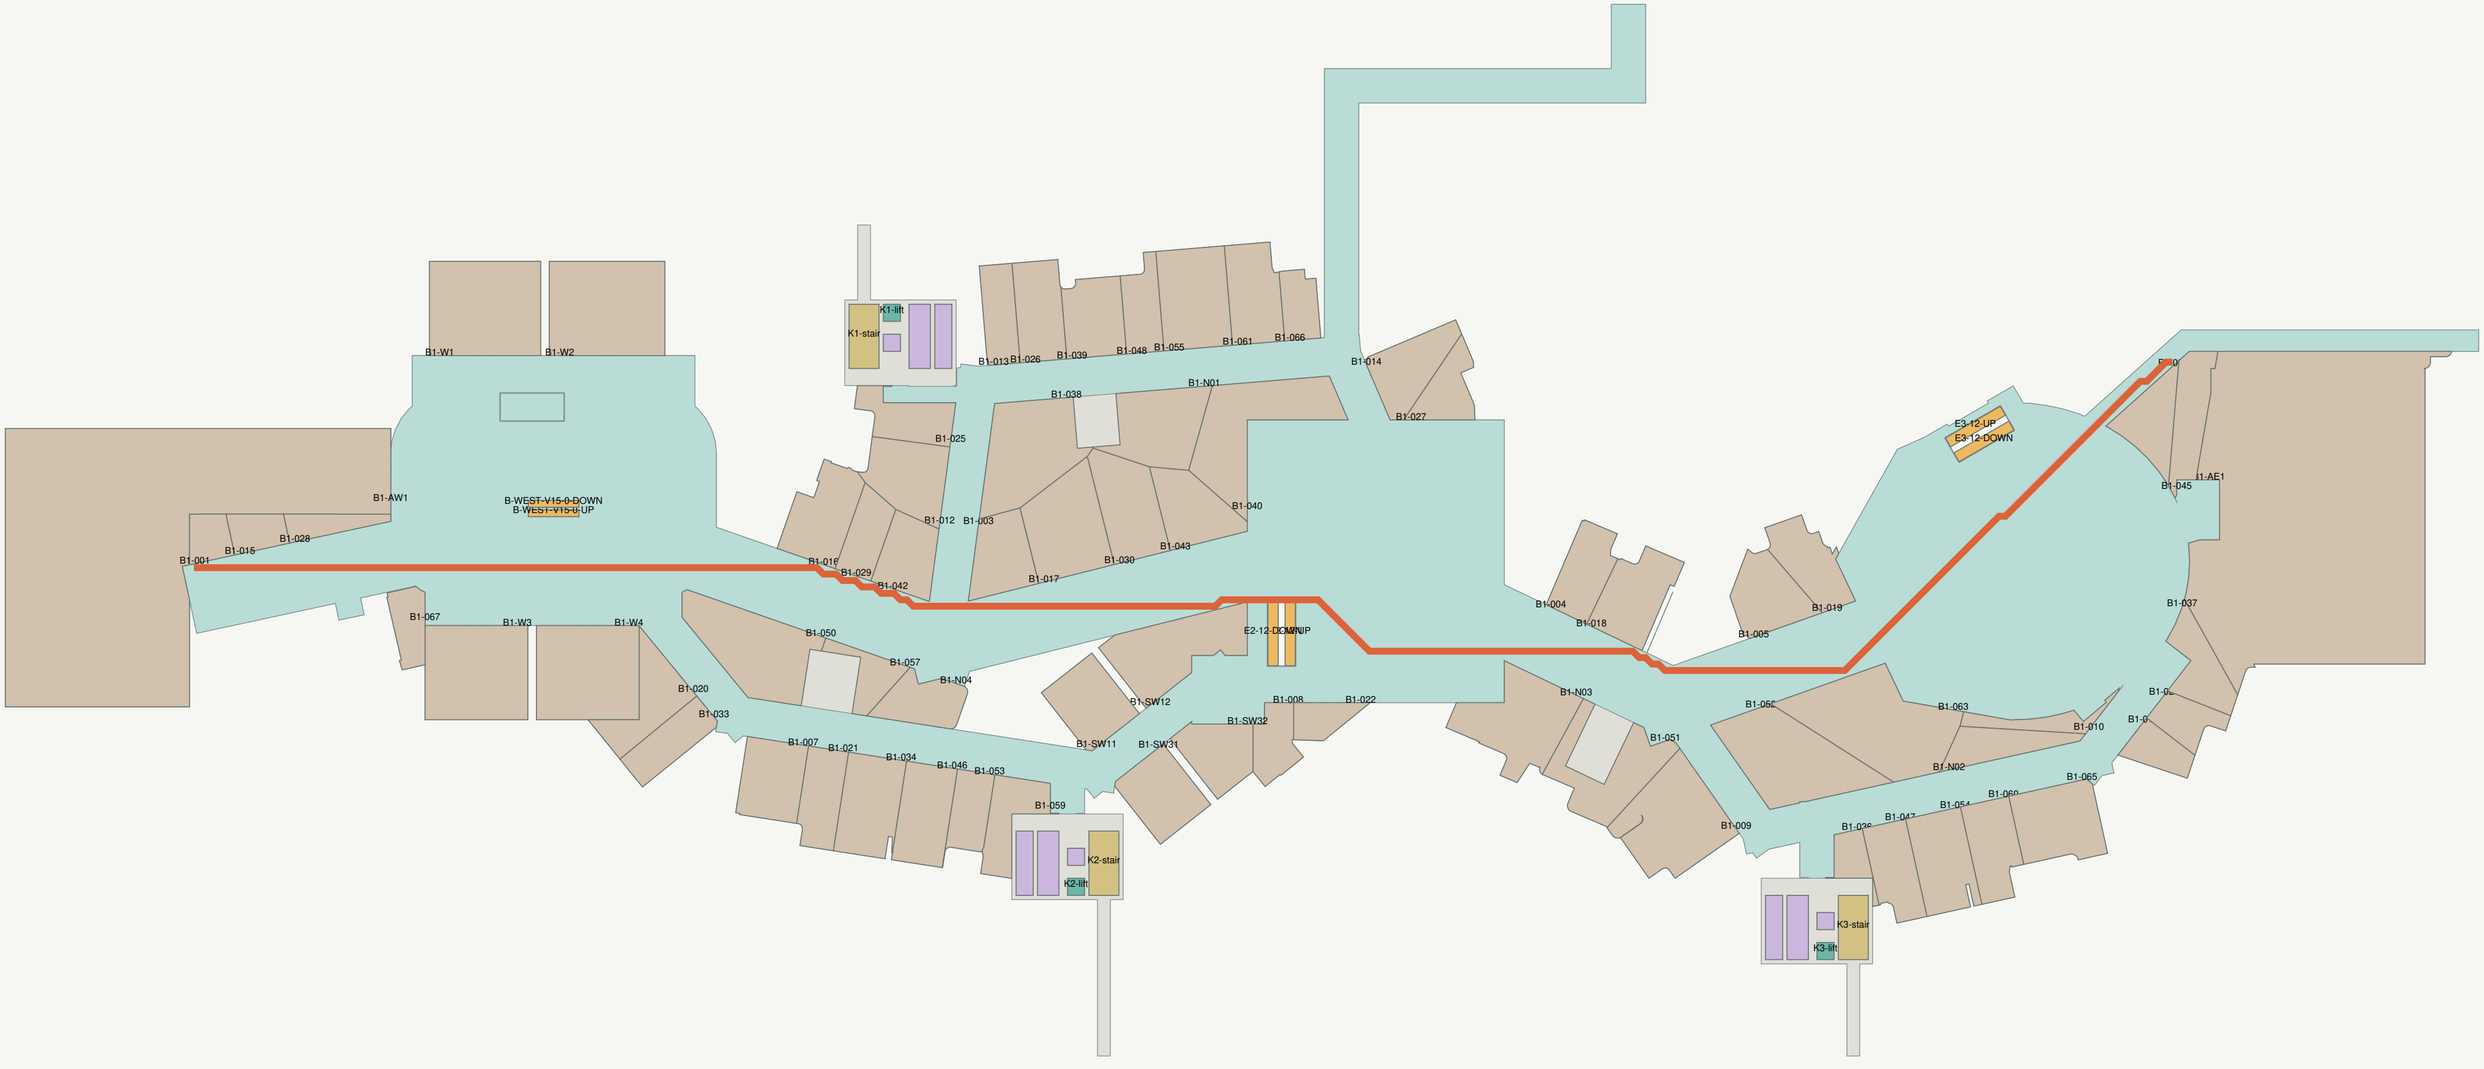

Orange: controller-walked main route 503.0 m. Visual approval is separate from walkability.

V30 | B / 2F | NORMAL LAYOUT

Design review / not structural certification. World X = map X + 429; world Z = map Z - 46.

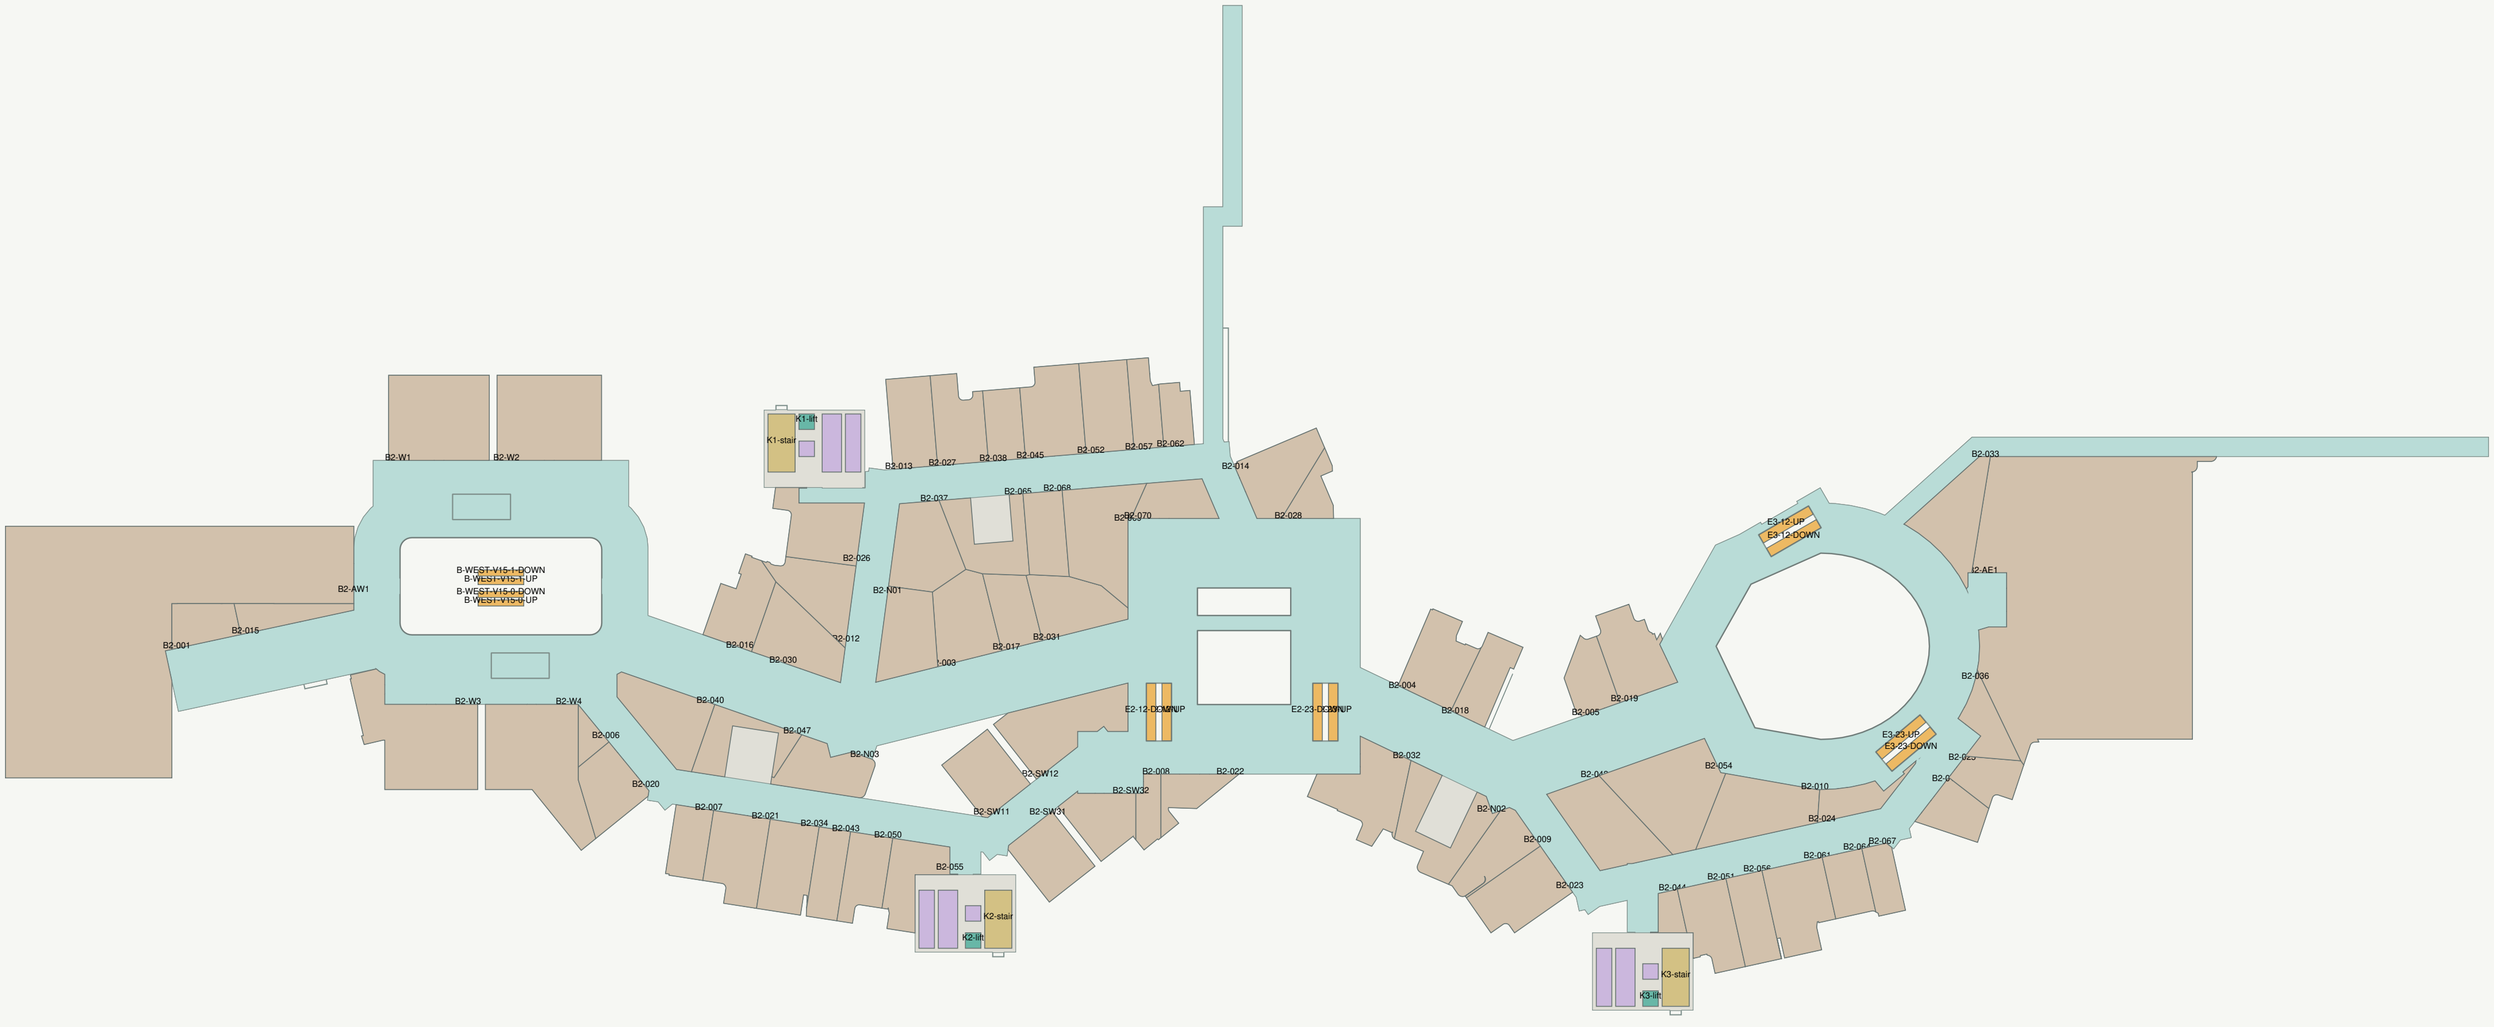


V30 | B / 3F | NORMAL LAYOUT

Design review / not structural certification. World X = map X + 429; world Z = map Z - 46.




V30 | B / B1 | NORMAL LAYOUT

Design review / not structural certification. World X = map X + 429; world Z = map Z - 46.

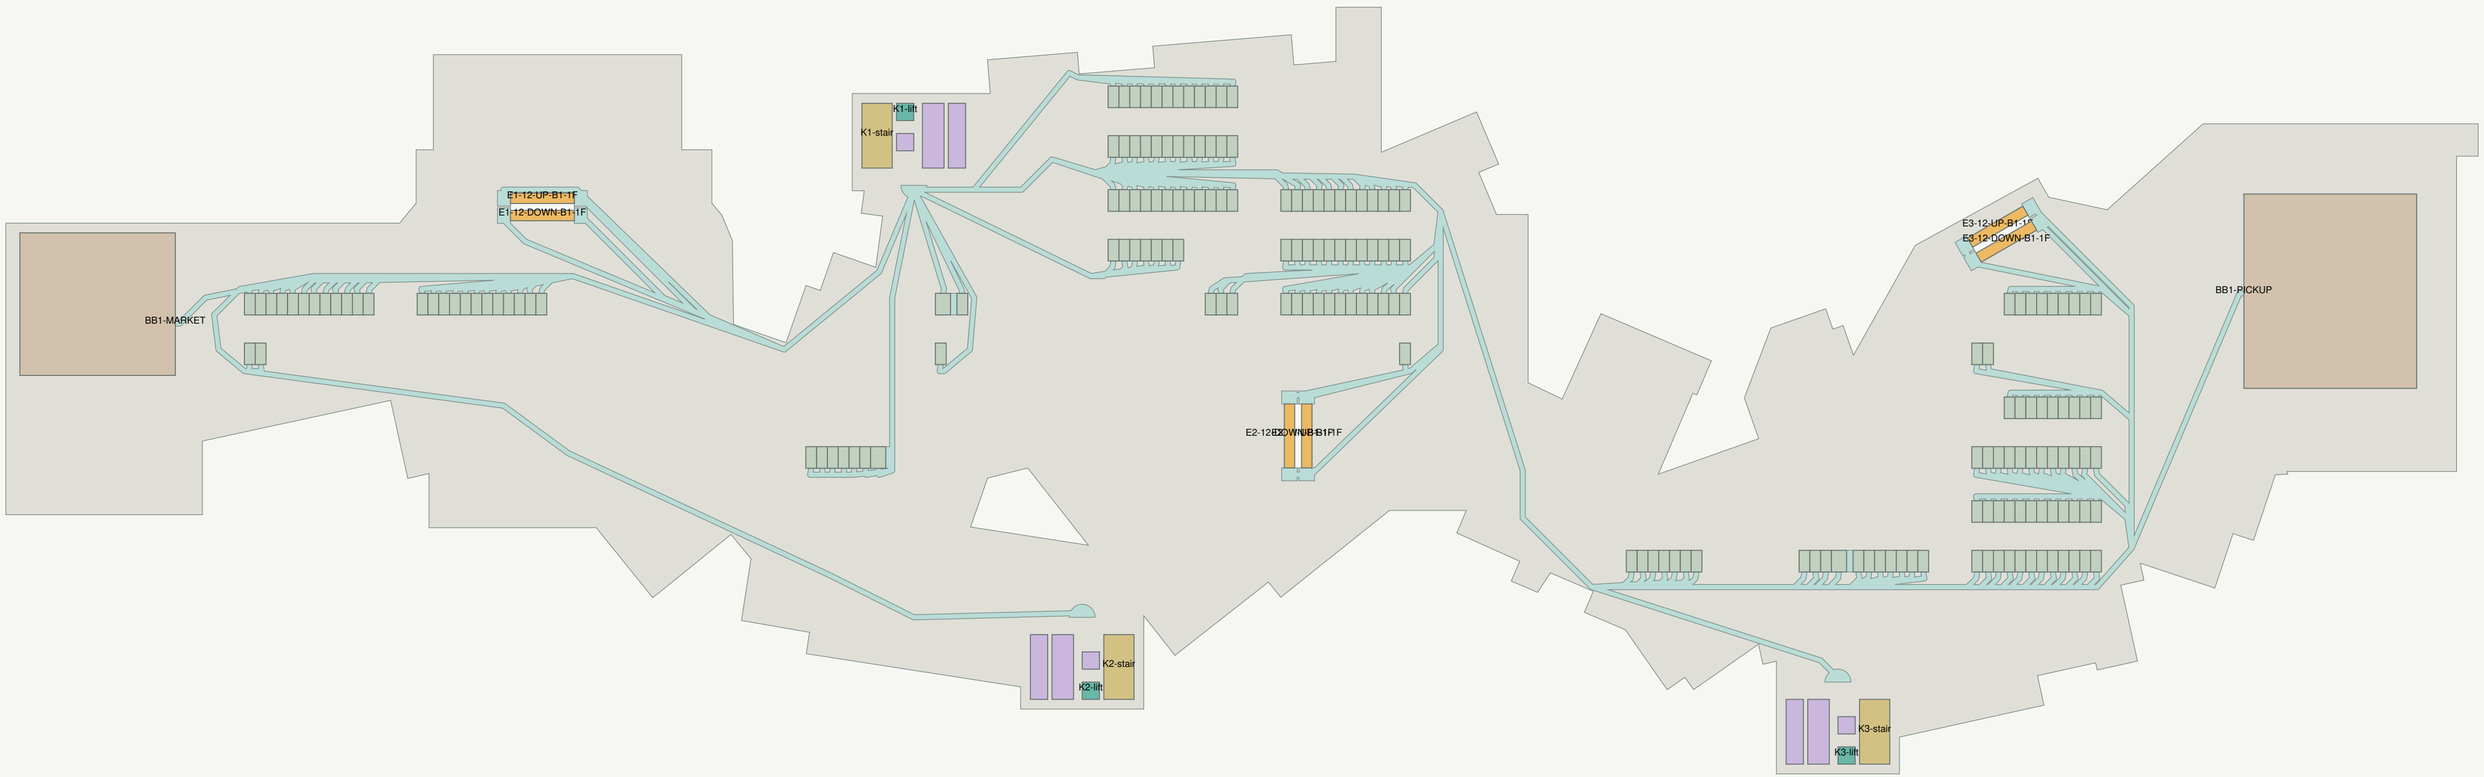


V30 | B / RF | NORMAL LAYOUT

Design review / not structural certification. World X = map X + 429; world Z = map Z - 46.

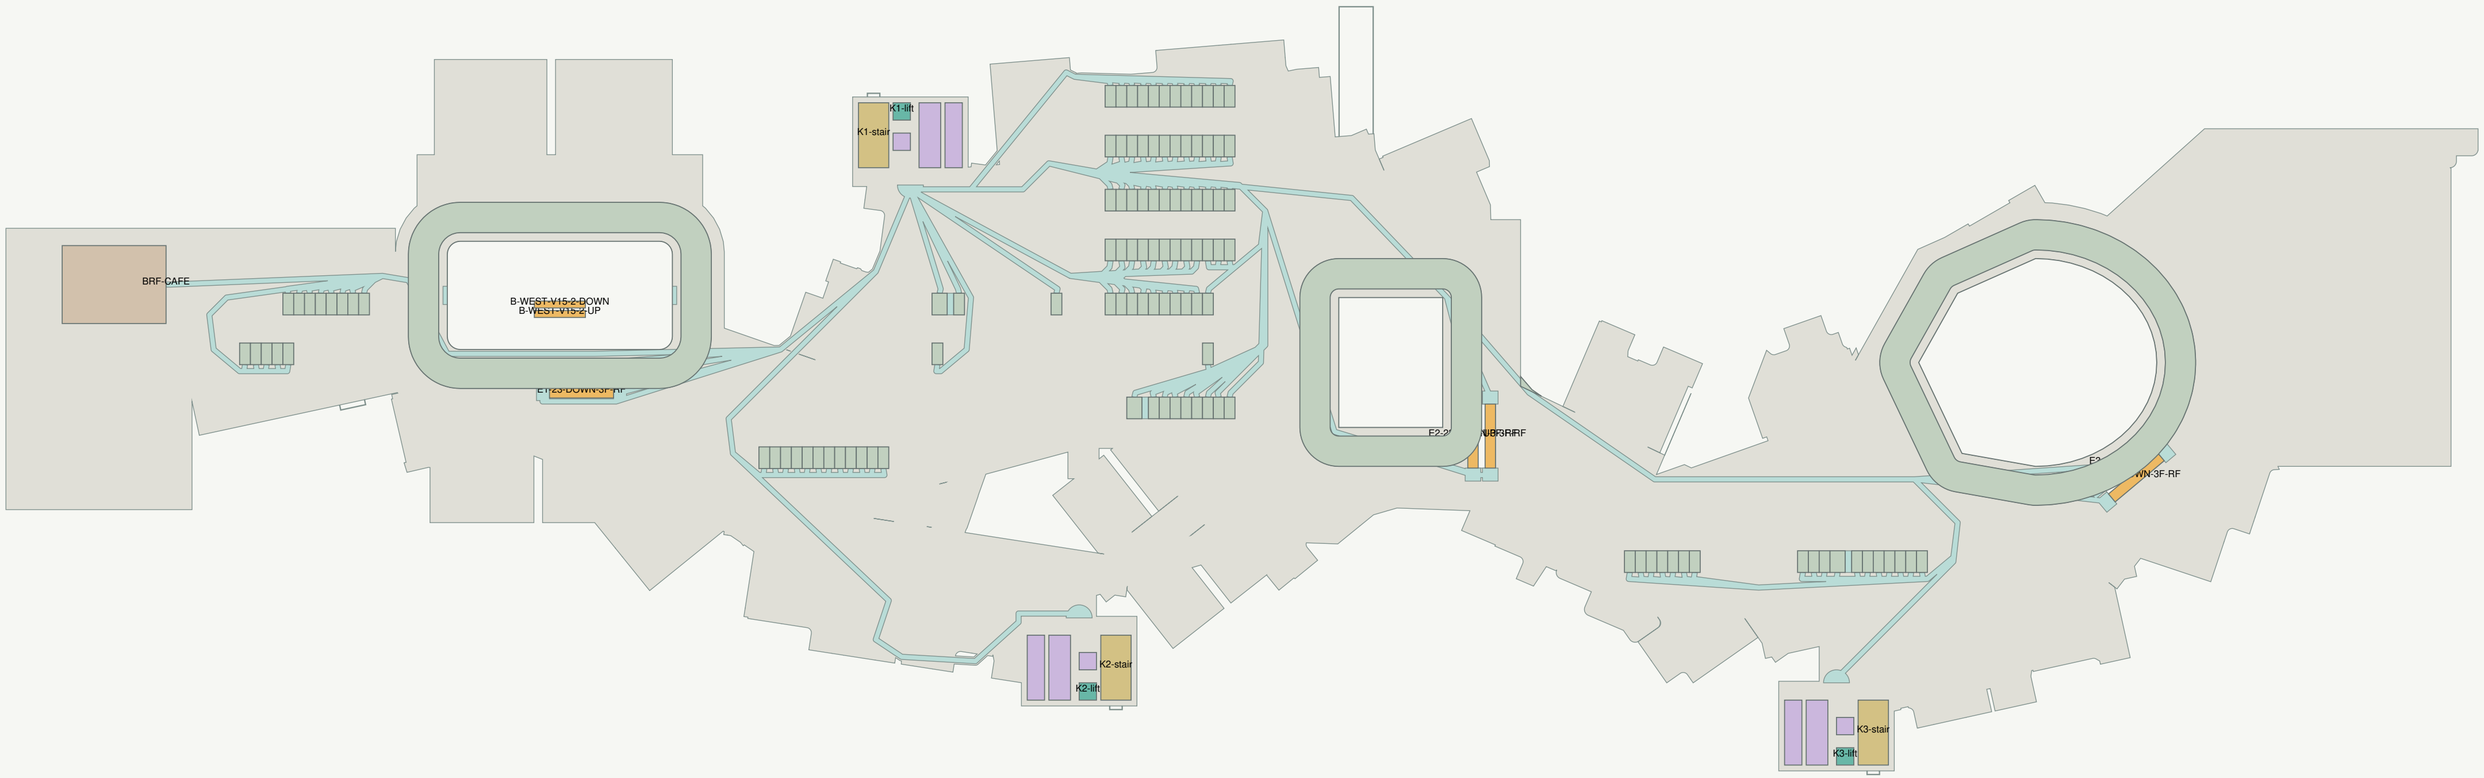


B WEST | level 1 | coordinates: world metres

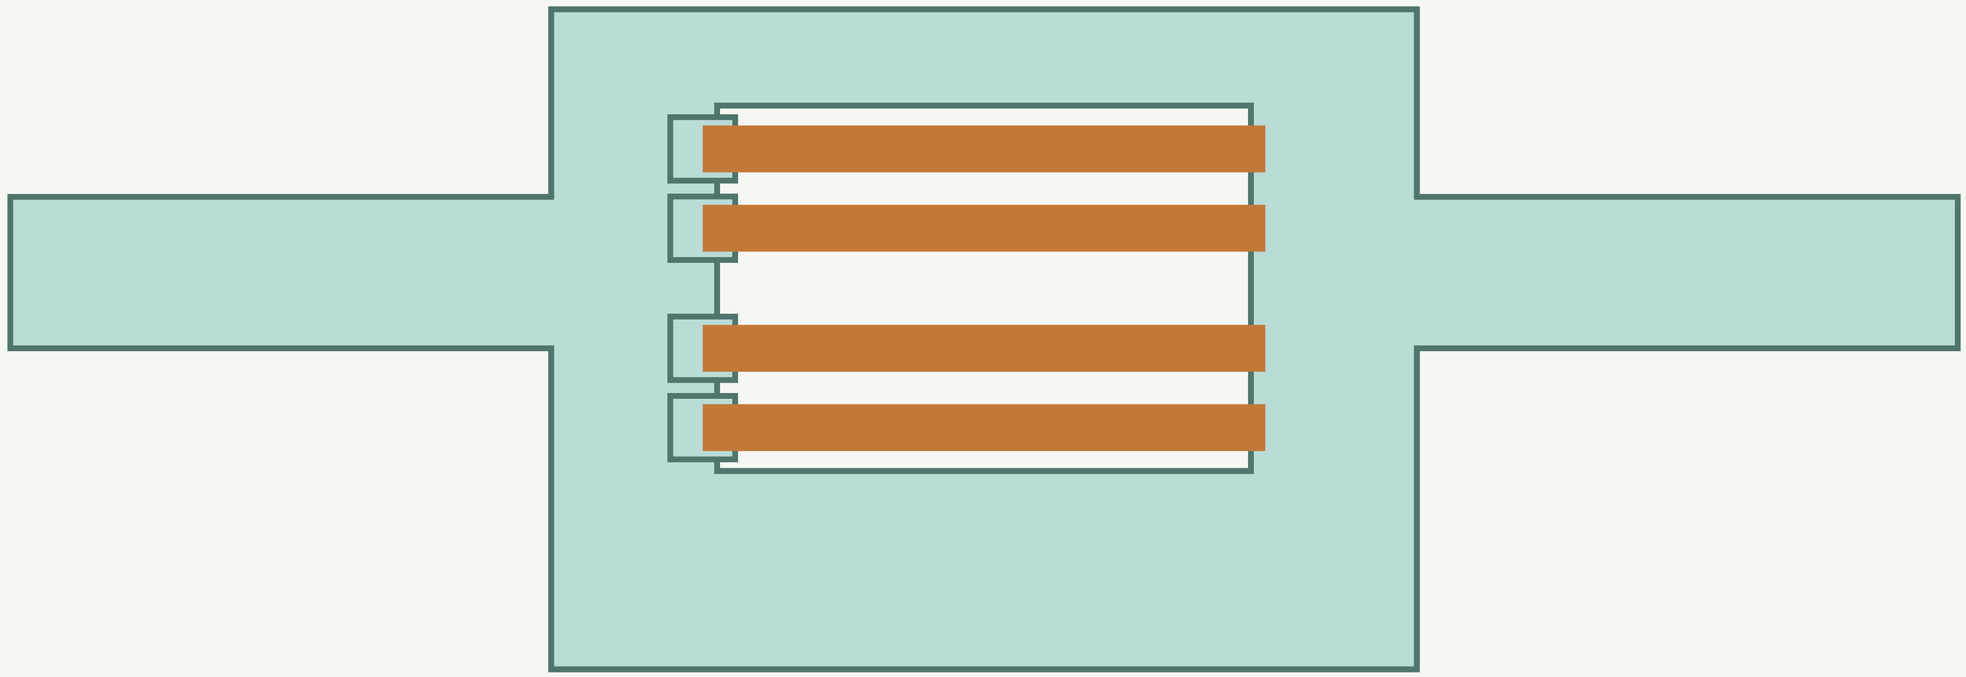


4.2 m public connectors. Upper transfer 7.53 m / 7.53 m; paired ES retained.

B WEST | level 2 | coordinates: world metres

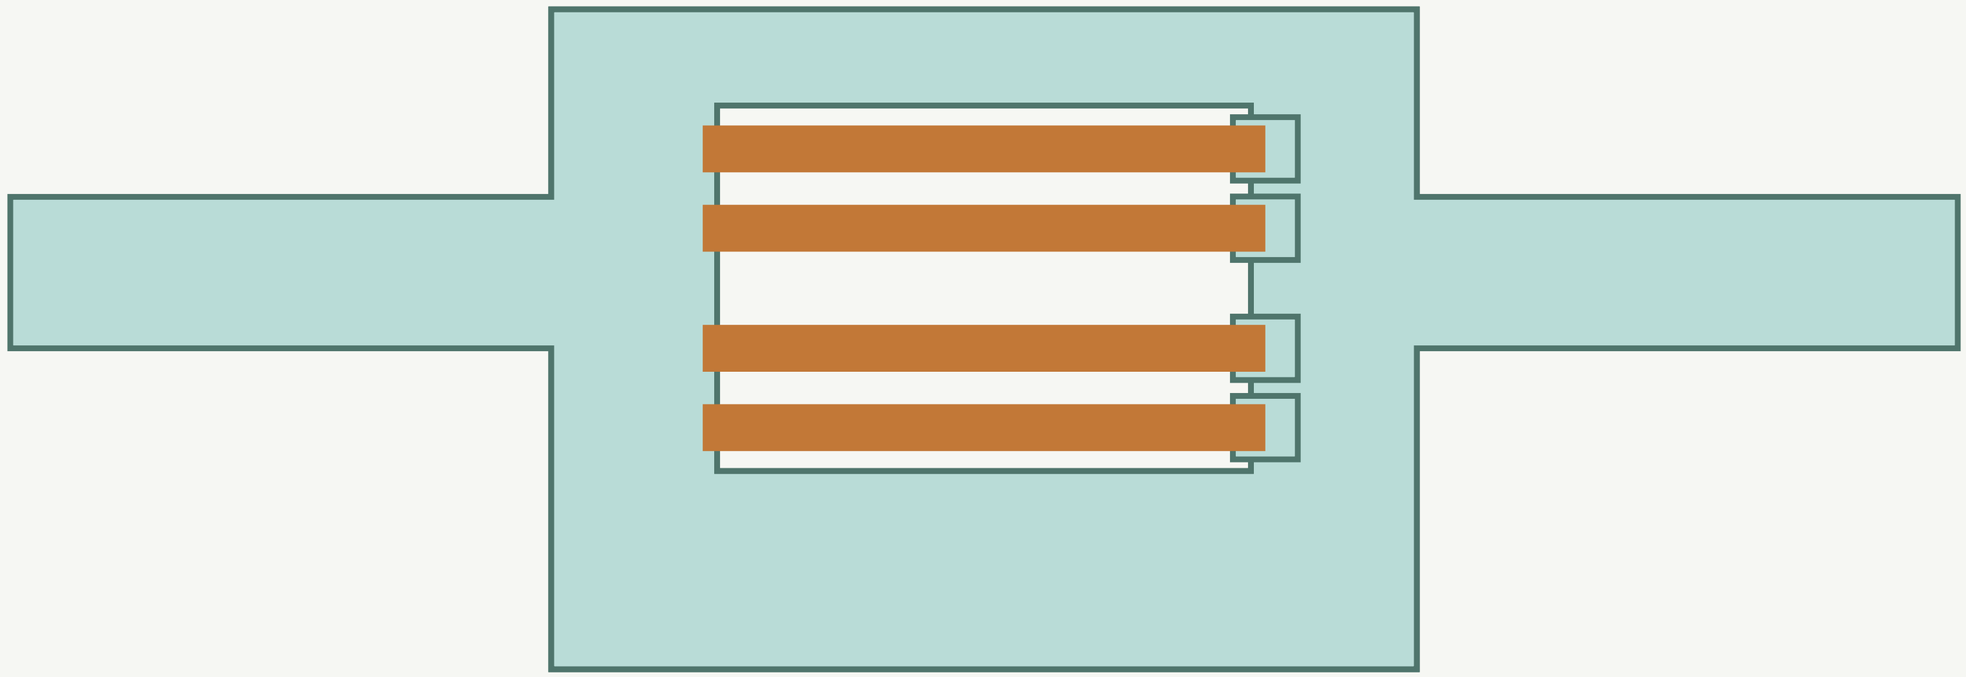

4.2 m public connectors. Upper transfer 7.53 m / 7.53 m; paired ES retained.

B WEST | level 3 | coordinates: world metres

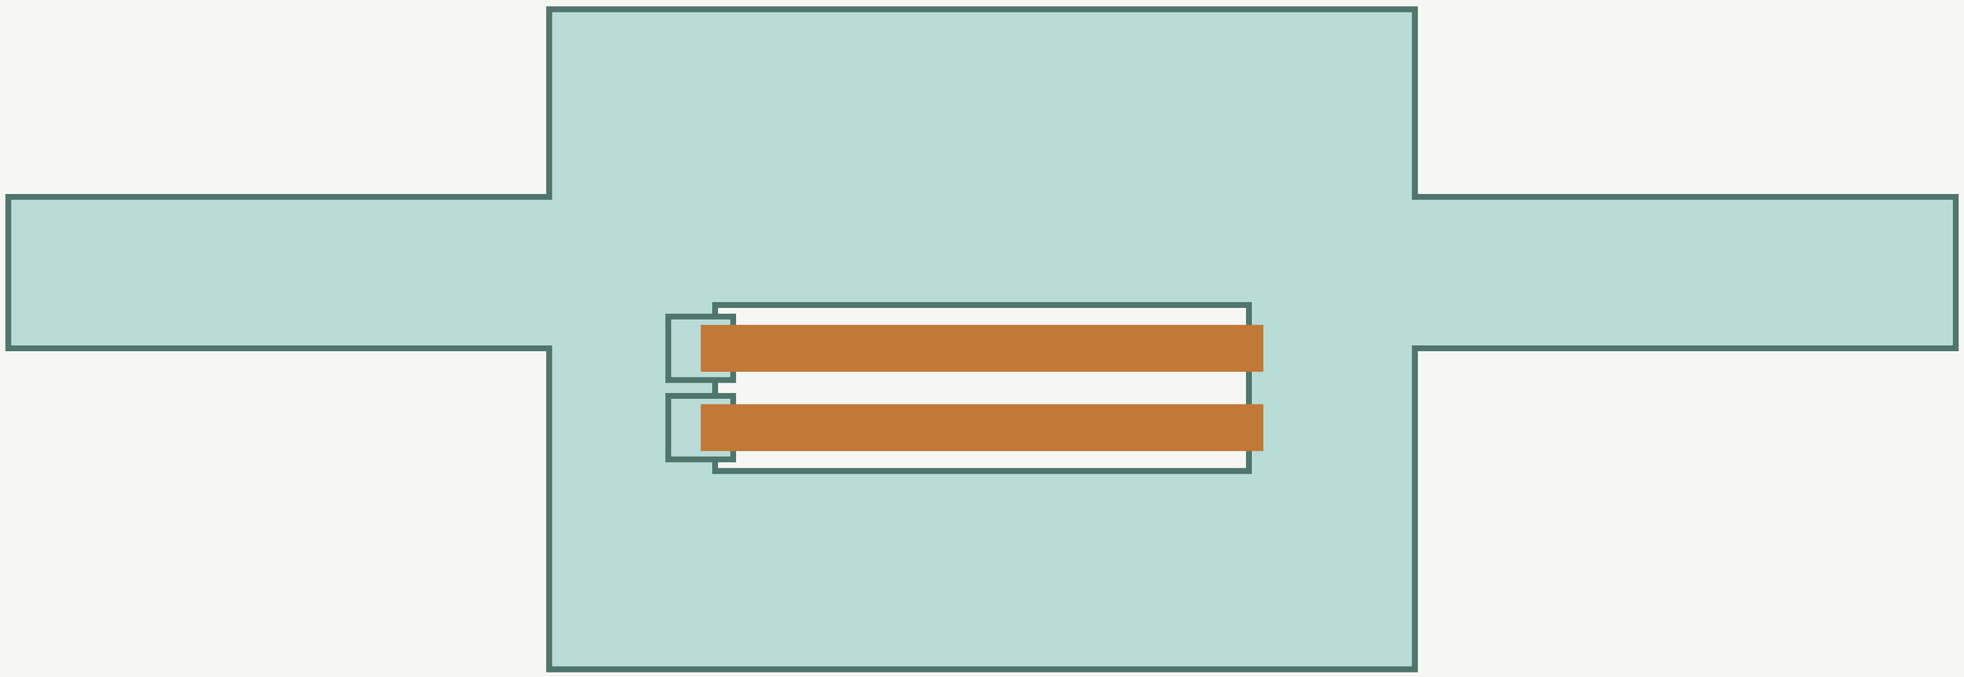

4.2 m public connectors. Upper transfer 7.53 m / 7.53 m; paired ES retained.