
FIND YOURSELF / B館 1F 建築平面・一次協議案

未施工 / ゲーム用仮寸法。旧楕円リングを廃止し、屈曲する主軸と局所的な近道へ。

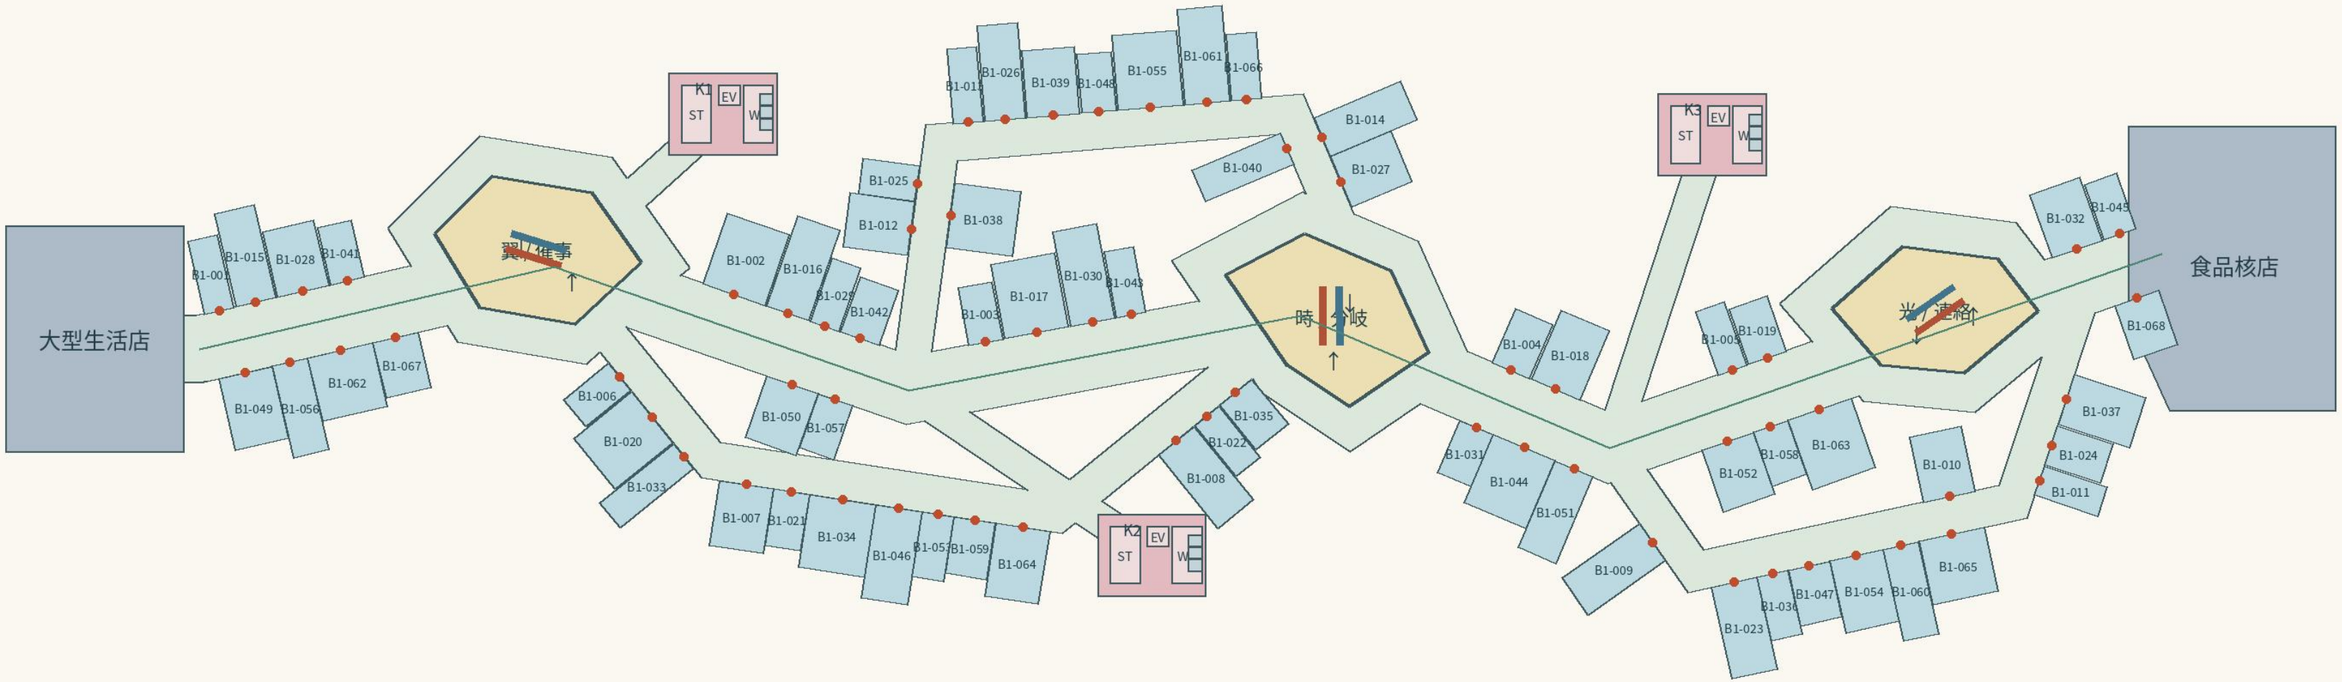

図示：通常区画 68 ＋ 核区画2。すべて計画上の区画数であり、完成店舗数ではありません。


主軸16m / 枝道9m / 設備連絡8m / 開口は2F・3Fで整合。赤点＝店舗入口。

局所座標を表示。既存館への接続・エスカレーター干渉・室内動線は設計審査待ち。実歩行テスト未実施。

100m（ゲーム用仮設計）

FIND YOURSELF / B館 2F 建築平面・一次協議案

未施工 / ゲーム用仮寸法。旧楕円リングを廃止し、屈曲する主軸と局所的な近道へ。

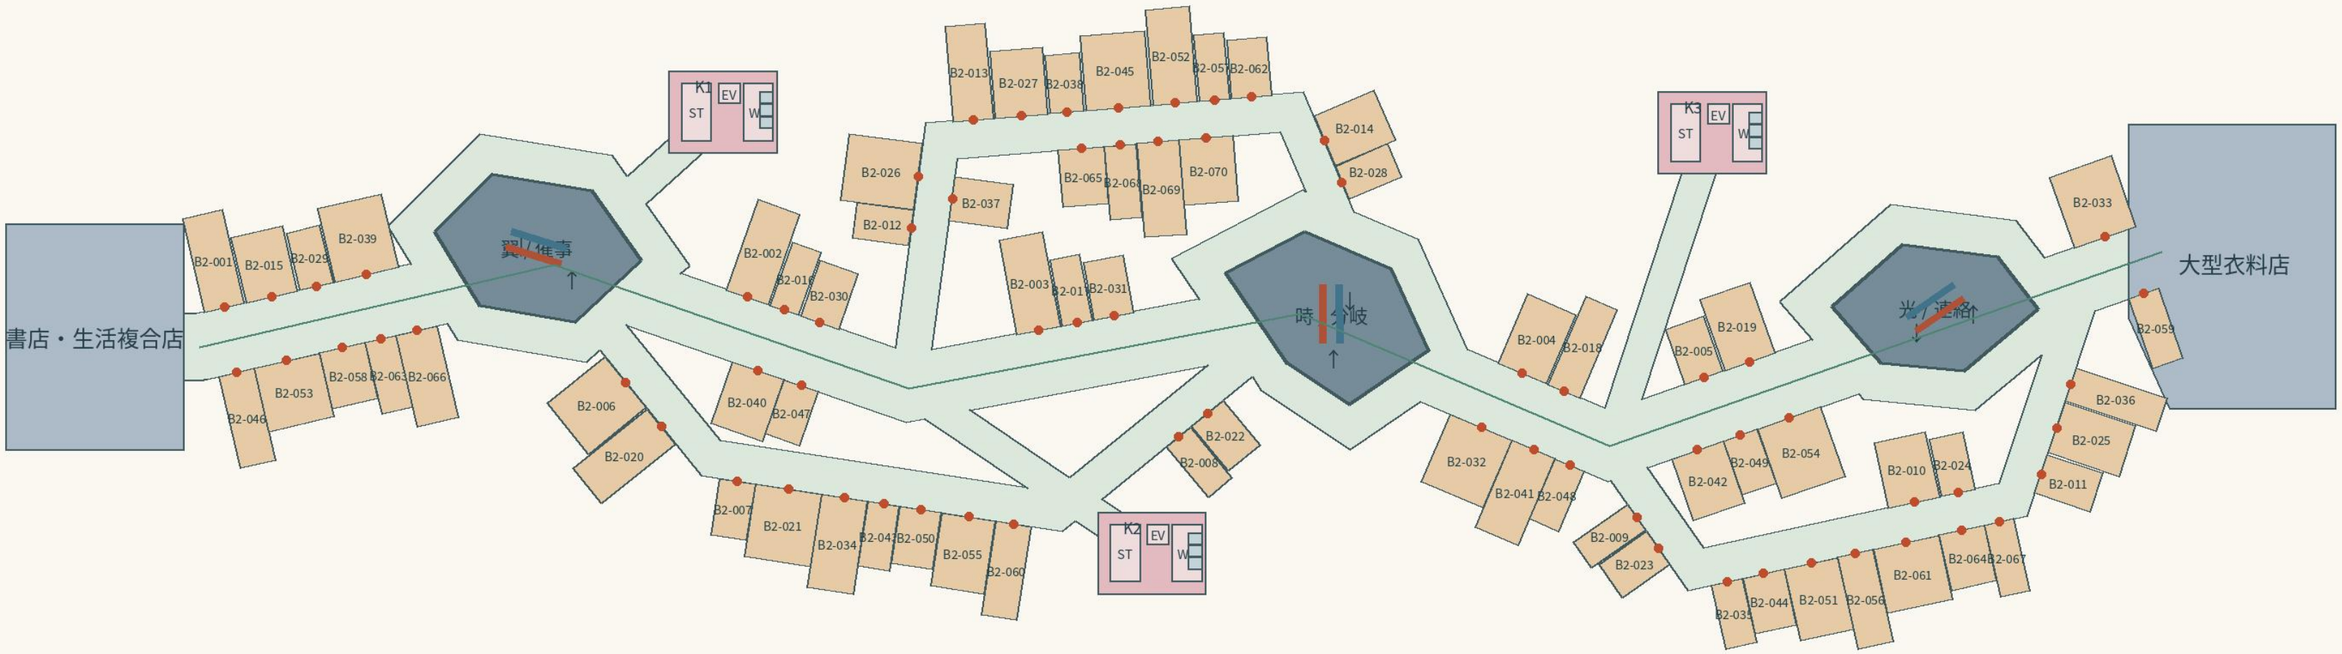

図示：通常区画 70 ＋ 核区画2。すべて計画上の区画数であり、完成店舗数ではありません。


主軸16m / 枝道9m / 設備連絡8m / 開口は2F・3Fで整合。赤点＝店舗入口。

局所座標を表示。既存館への接続・エスカレーター干渉・室内動線は設計審査待ち。実歩行テスト未実施。

100m（ゲーム用仮設計）

FIND YOURSELF / B館 3F 建築平面・一次協議案

未施工 / ゲーム用仮寸法。旧楕円リングを廃止し、屈曲する主軸と局所的な近道へ。

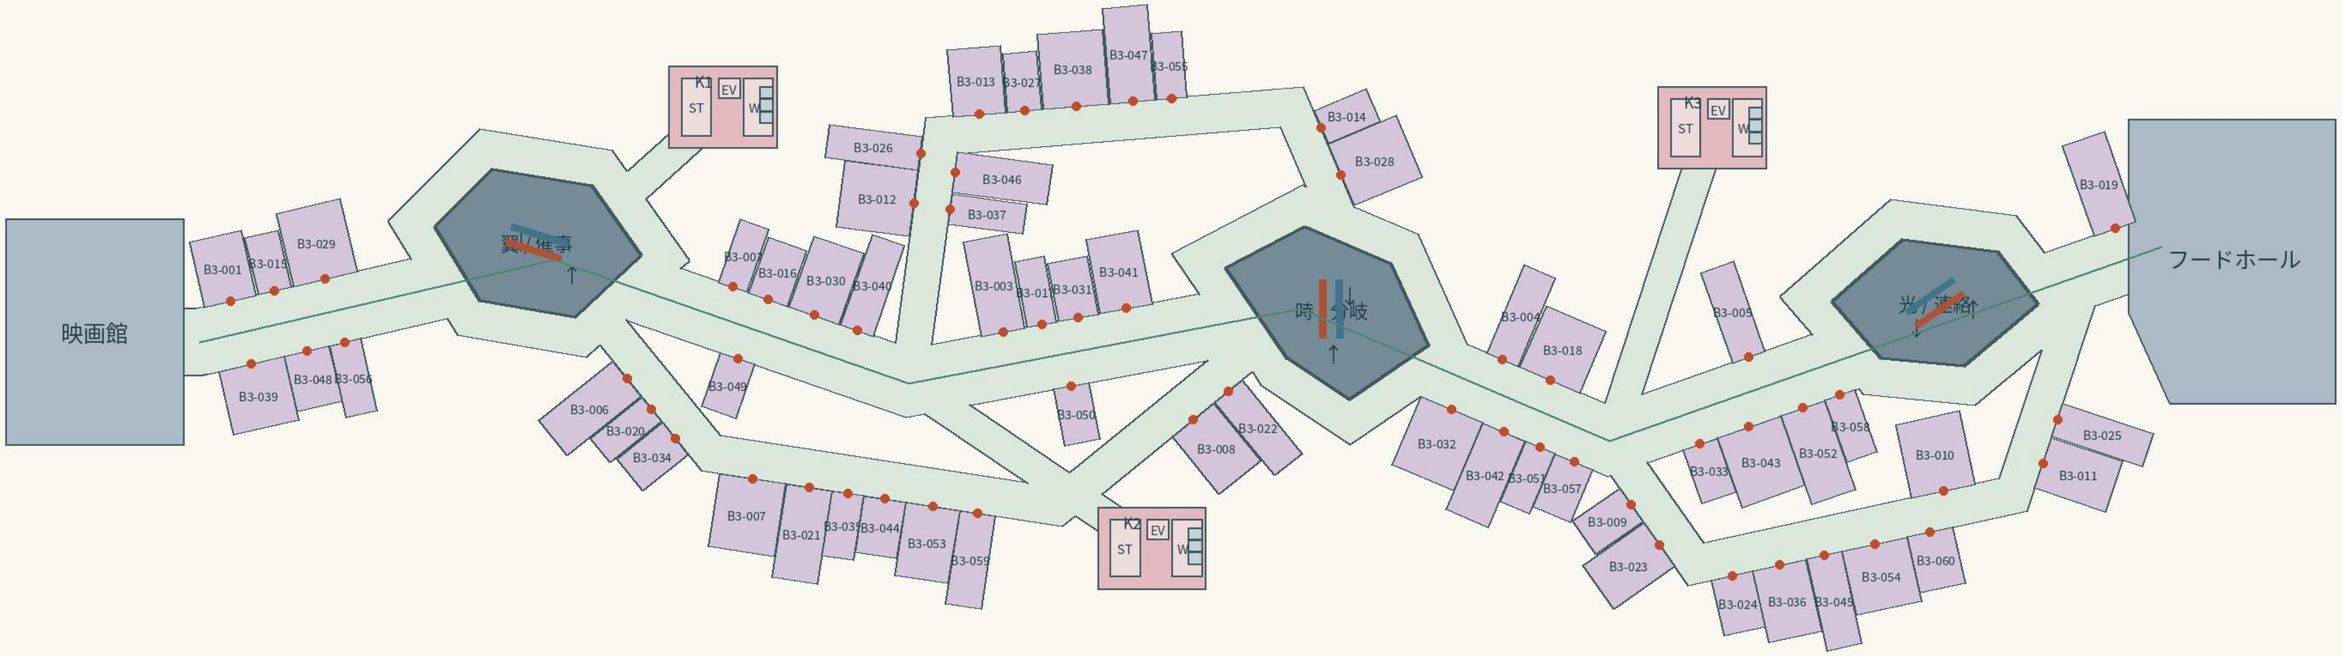

図示：通常区画 60 ＋ 核区画2。すべて計画上の区画数であり、完成店舗数ではありません。

主軸16m / 枝道9m / 設備連絡8m / 開口は2F・3Fで整合。赤点＝店舗入口。

局所座標を表示。既存館への接続・エスカレーター干渉・室内動線は設計審査待ち。実歩行テスト未実施。

100m（ゲーム用仮設計）